


28

28

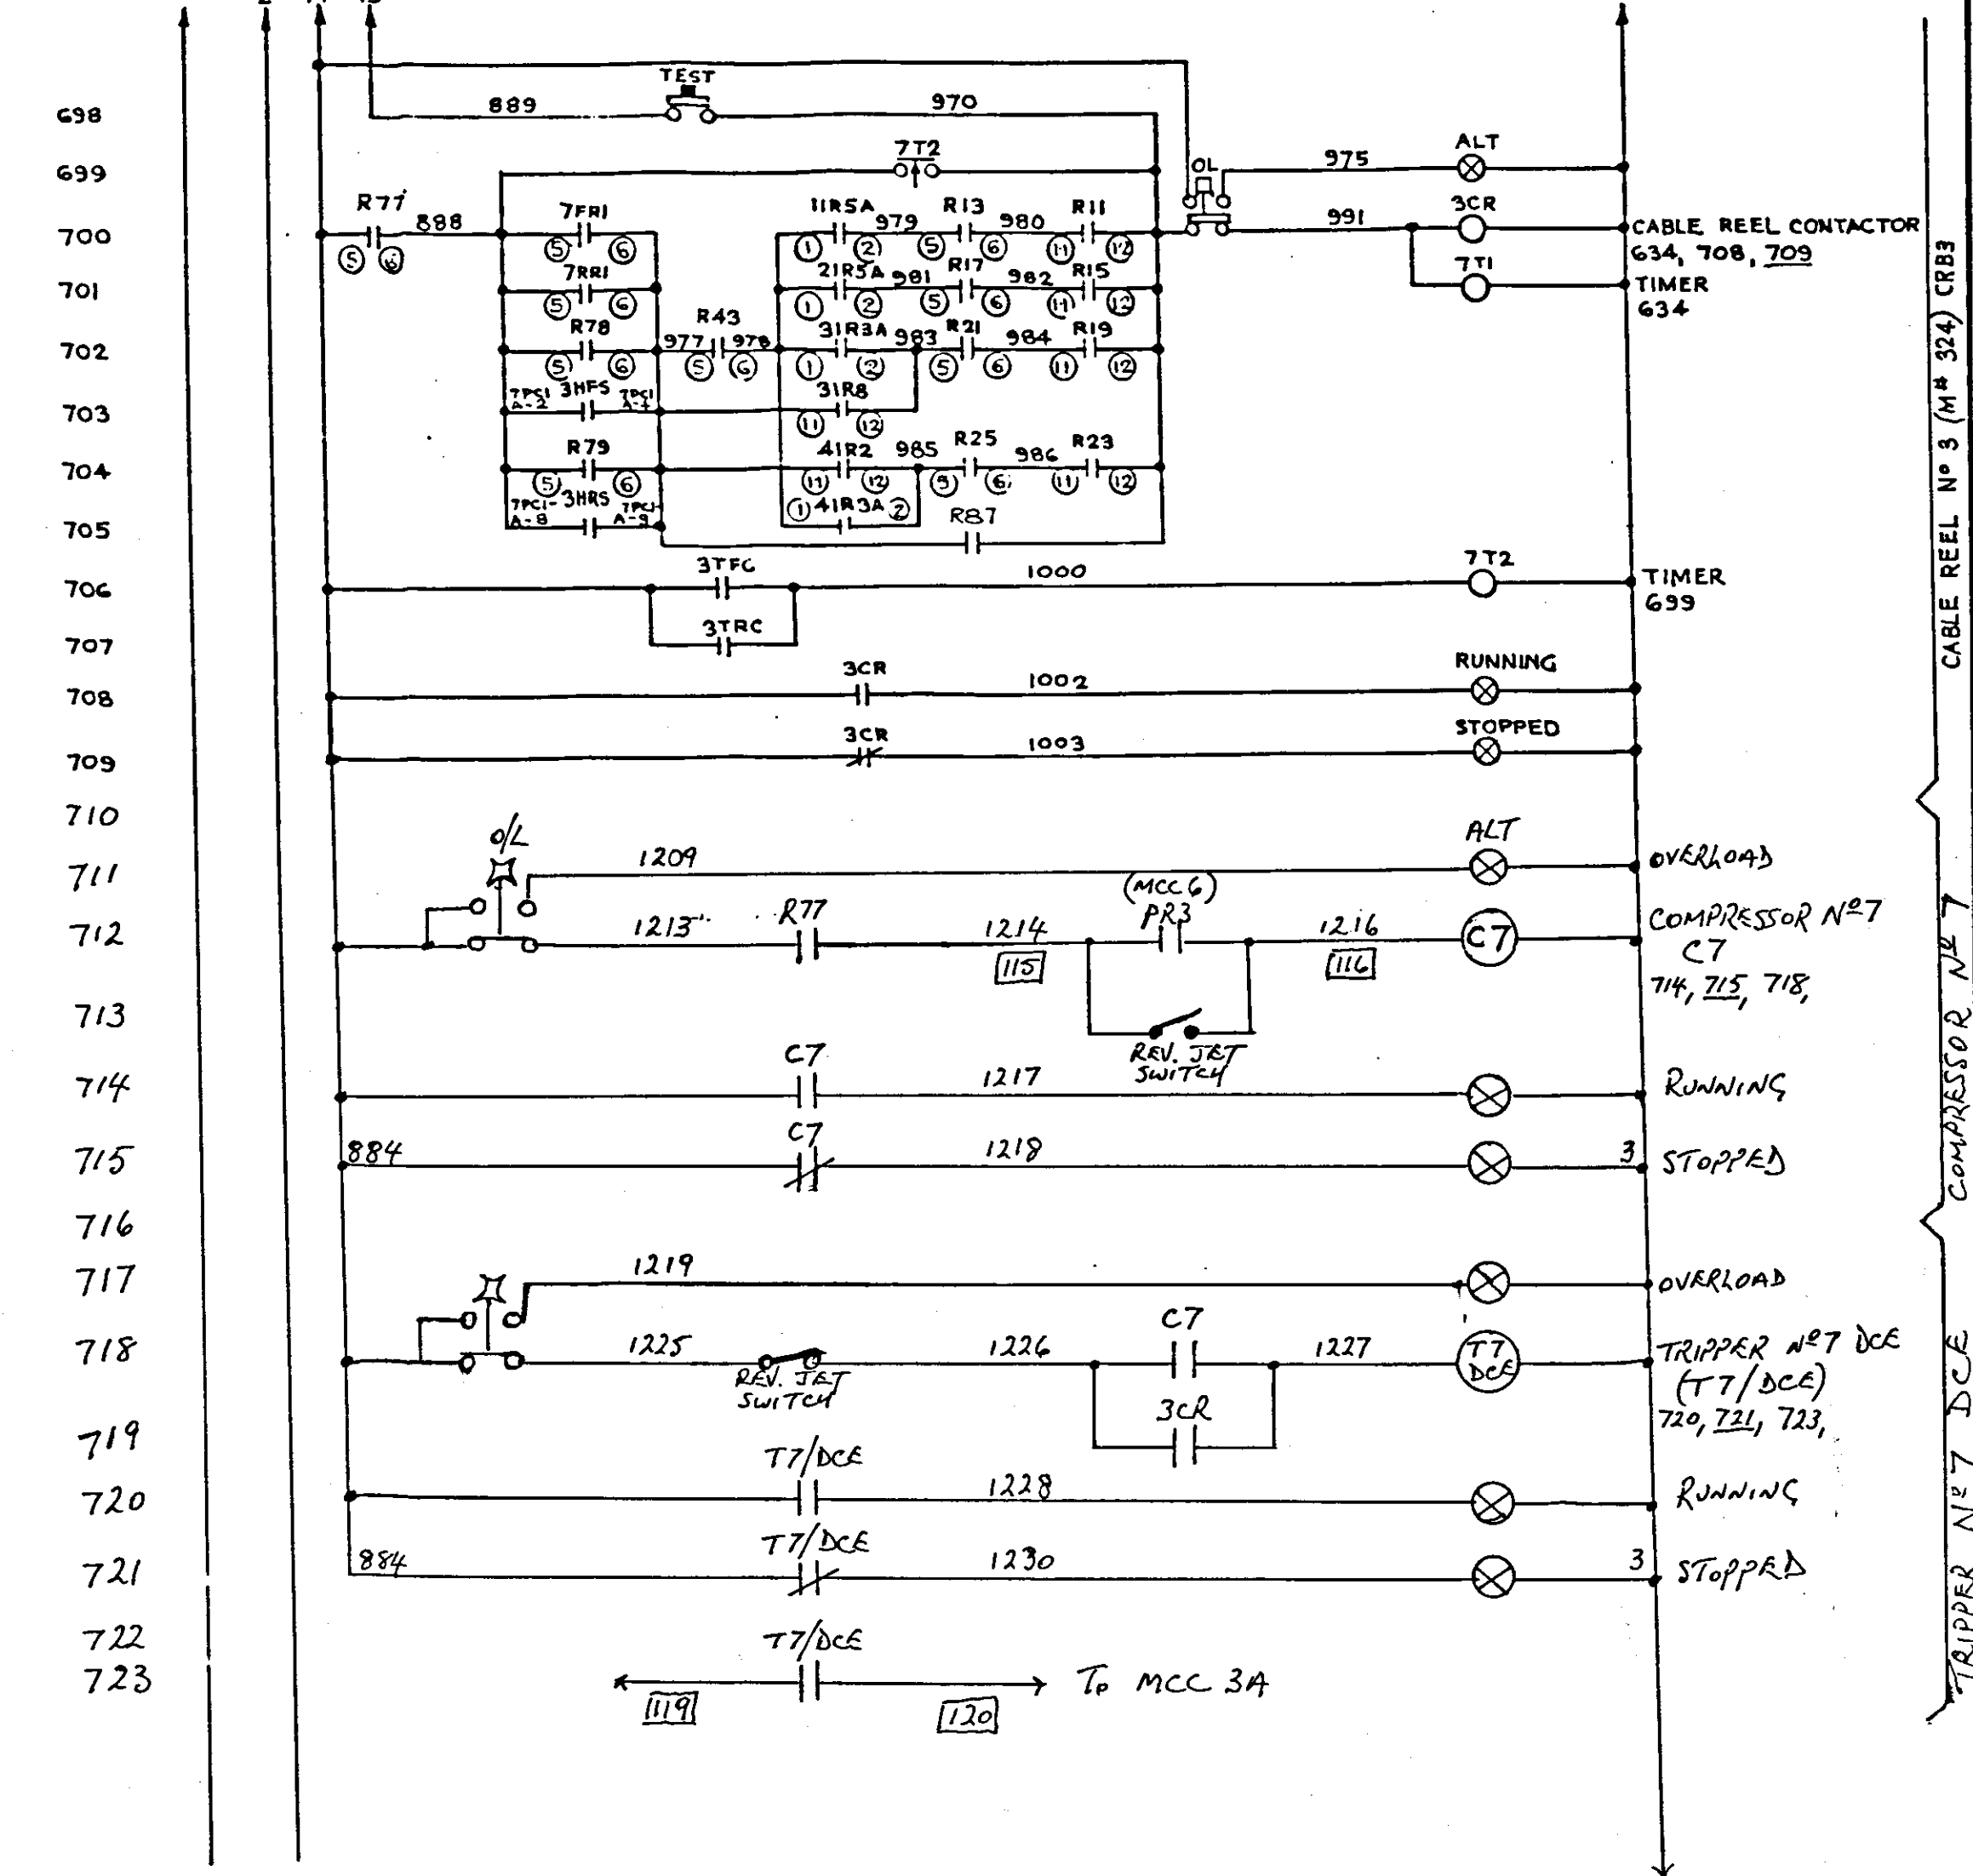

SCHEME FOR MCC 3B - SEAFORTH GRAIN TERMINAL.

DEWHURST & PARTNER LTD.
MELBOURNE WORKS. HOUNSLOW.

TITLE:
SCHEME FOR MCC 3B SEAFORTH GRAIN TERMINAL

REVISION: 9 OVERSPEED TIMER ADDED	REVISION: 8 TRIPPER OVERLOADS REPLACED BY LRI-4 & HOL & LOL.	REVISION: 7 INTERLOCKS FROM TR66 MODIFIED ON LINES 552 & 553 0532 NOW N/O SO RELAY R 85 CONTACTS NOW N/C BRAKE CTT MOD: ORIGIN: SITE	REVISION: 6 TURNHEAD INTERLOCK CTT ADDED TO OPEN CONTACT LINE. STOP RELAY CONTACT ADDED TO CABLE REEL
ORIGIN: ICD 16/1/77 15	ORIGIN ICD 9/1/77 15	ORIGIN: SITE 15	ORIGIN: ICD 18/3/72 15

REVISION: 5 DESK TERMINALS ADDED.	REVISION: 4 CHUTE BLOCK INDICATION WAS TO TERM 7G	REVISION: 3 GF3, 3AR, 3AF, & CBR3 CONTACTS MODIFIED
ORIGIN: ICD. 1/2/72 SCD. JS.	ORIGIN: EISP. 10/3/71 SCD. J.T.	ORIGIN: EISP. 2/2/71 SCD. J.T.

REVISION: 2
3 AR & 3 AF
CONTACTS MODIFIED

ORIGIN: EISP.
26/2/71 SGD J.T.

REVISION: 1
R87 CONTACT MOVED FROM
LINE 643 TO 644. H/C
CONTACT ADDED TO LINE 649
VALVE INDICATORS WERE EAST
WEST, 1126, 1251, 1276 MODIFIED
ORIGIN: EISP.
19/2/71 SGD.

DRAWN BY A.M.	
DATE	18.1.71
CHECKED BY	
APPROVED BY	
DATE	

KEY DIAG. N°
EXT. DIAG. N° STX 361U
REL. DIAG N°
PANEL LAYOUT N° HTX 361U

ISSUE	1	2	3	4	5	6	7	8	9	10	11
DTX 361U/4											
DTX 361U/4											