
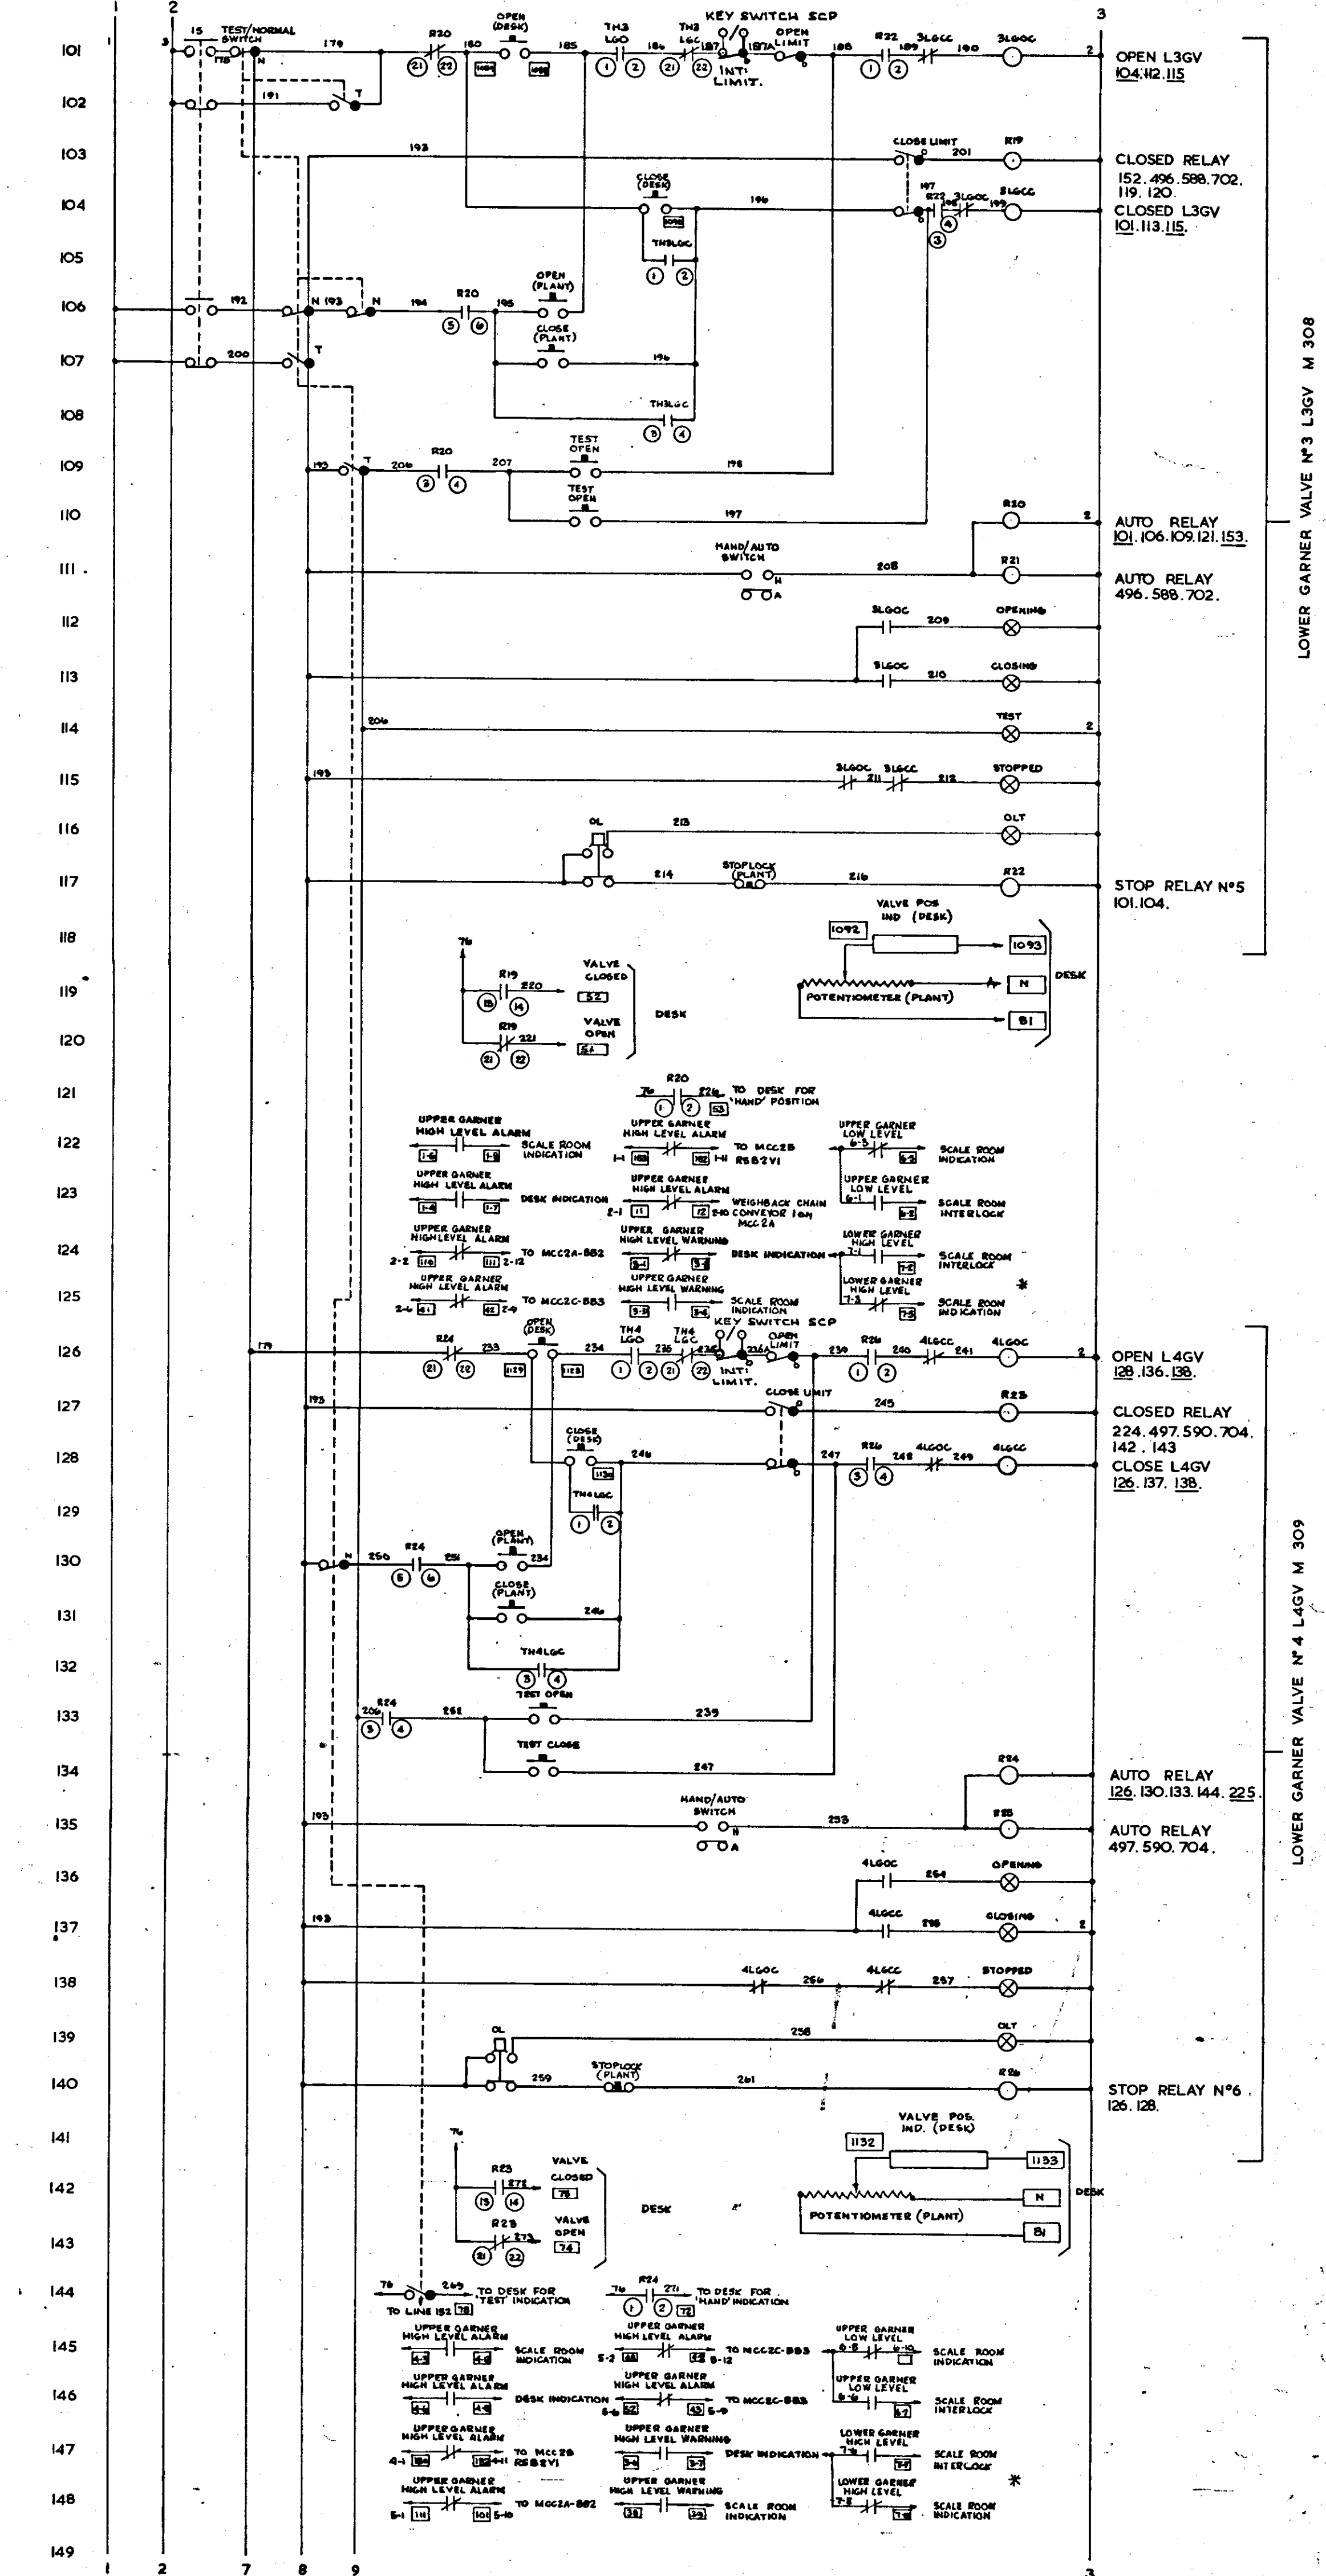
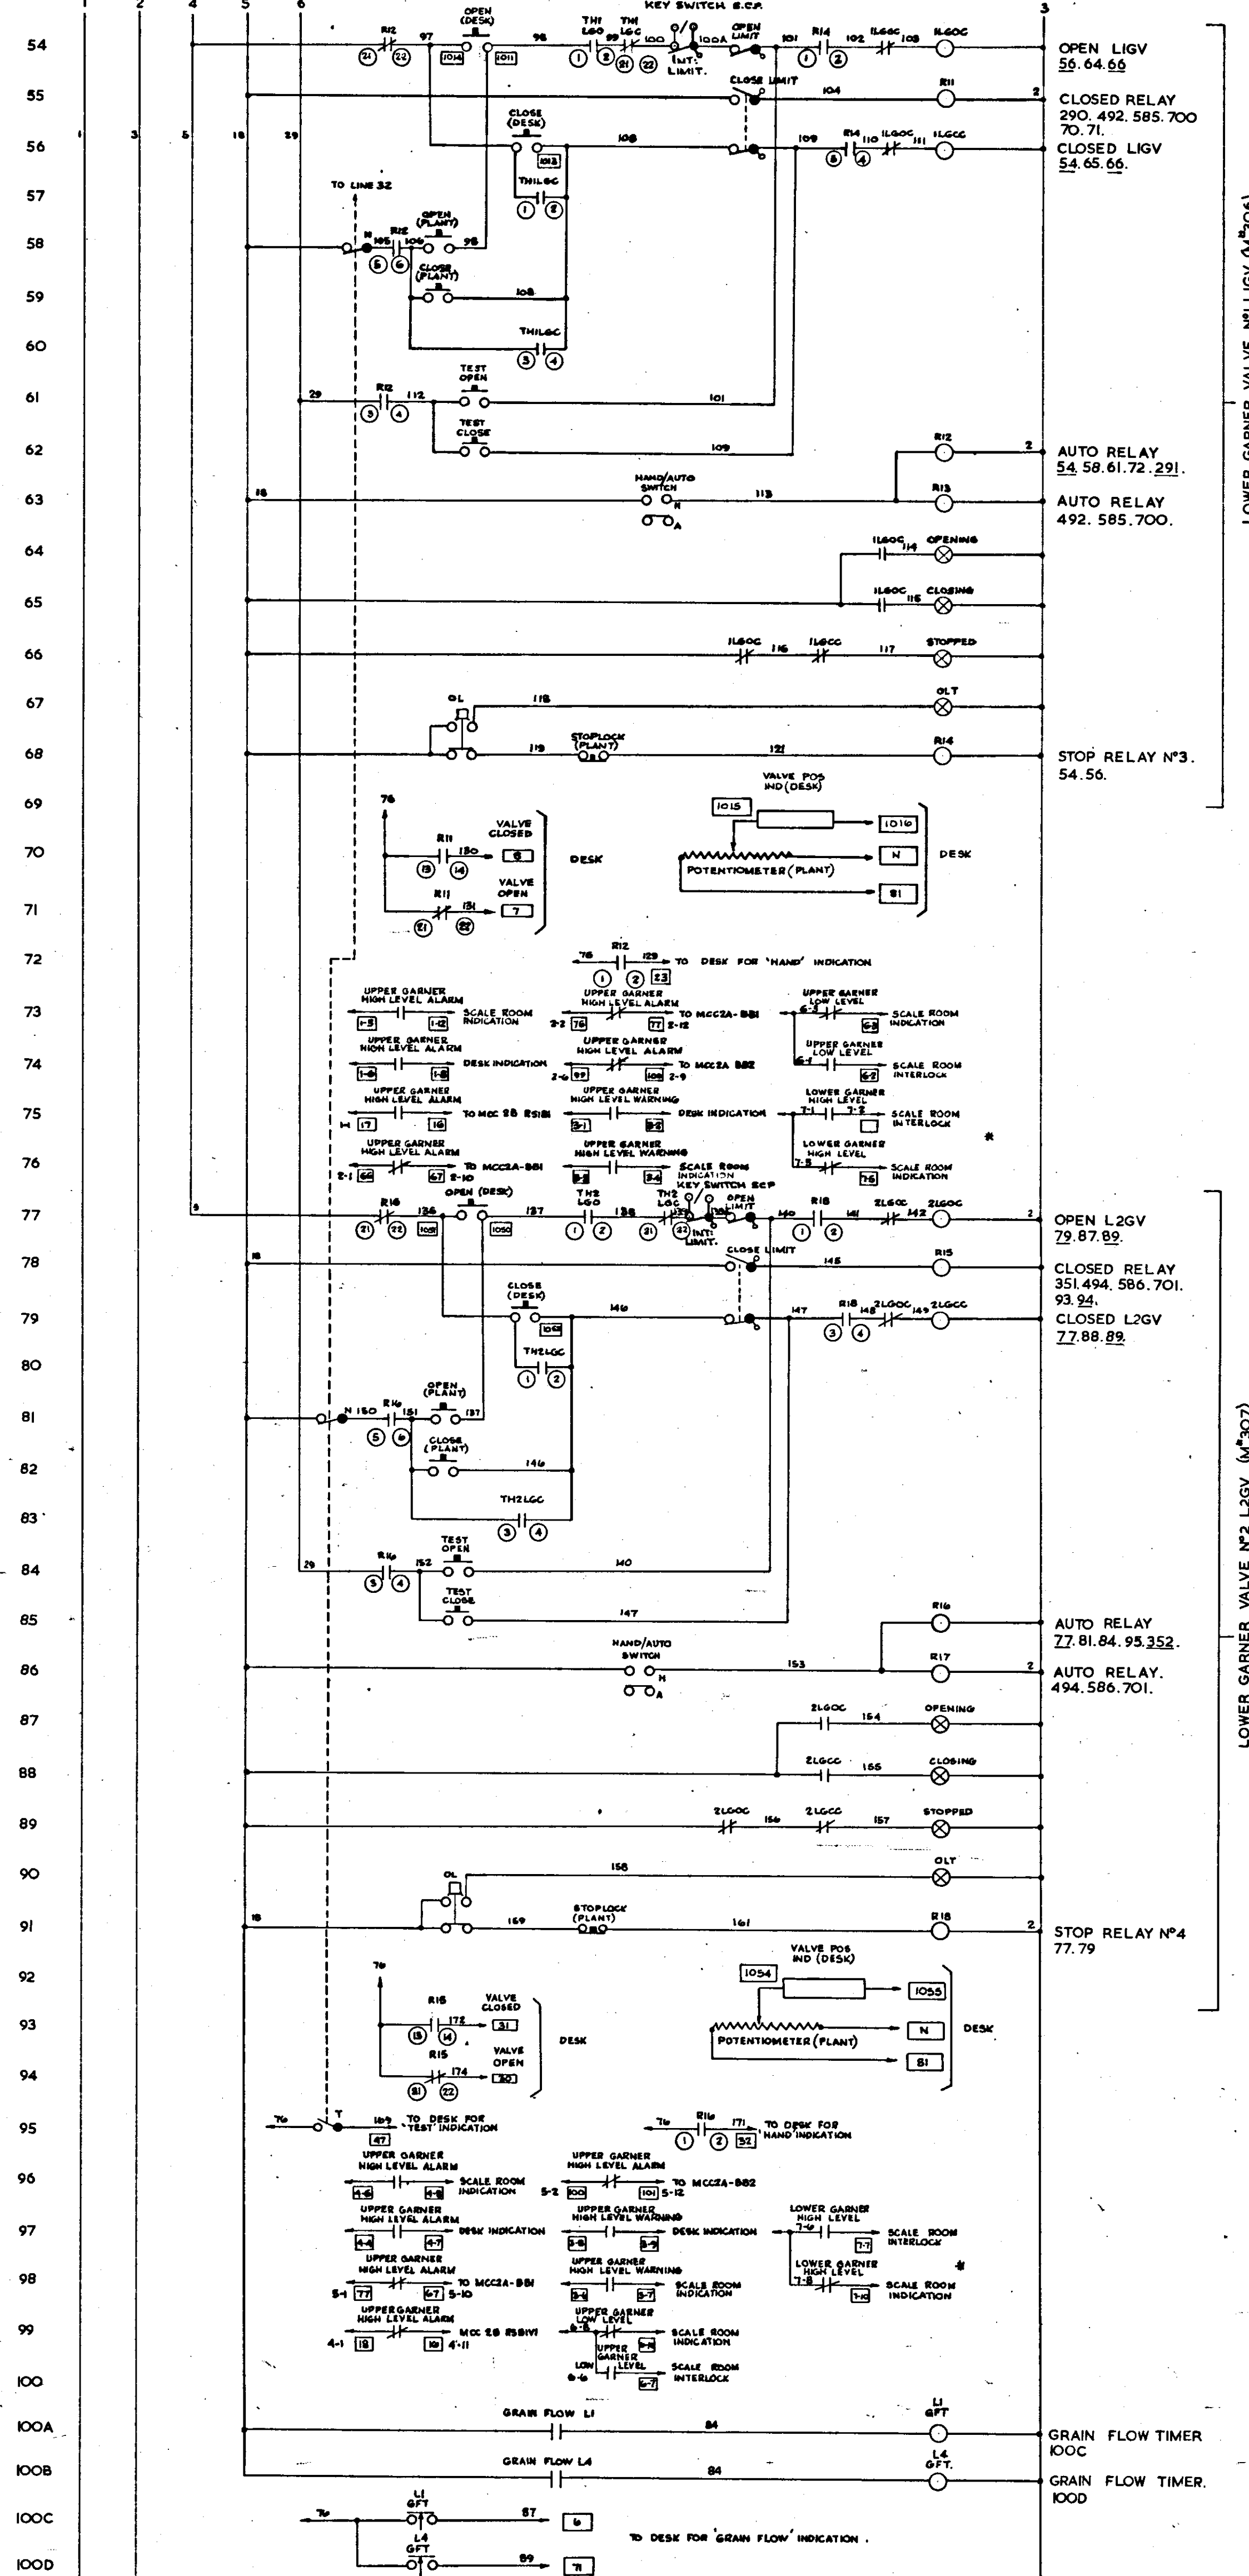


10733.

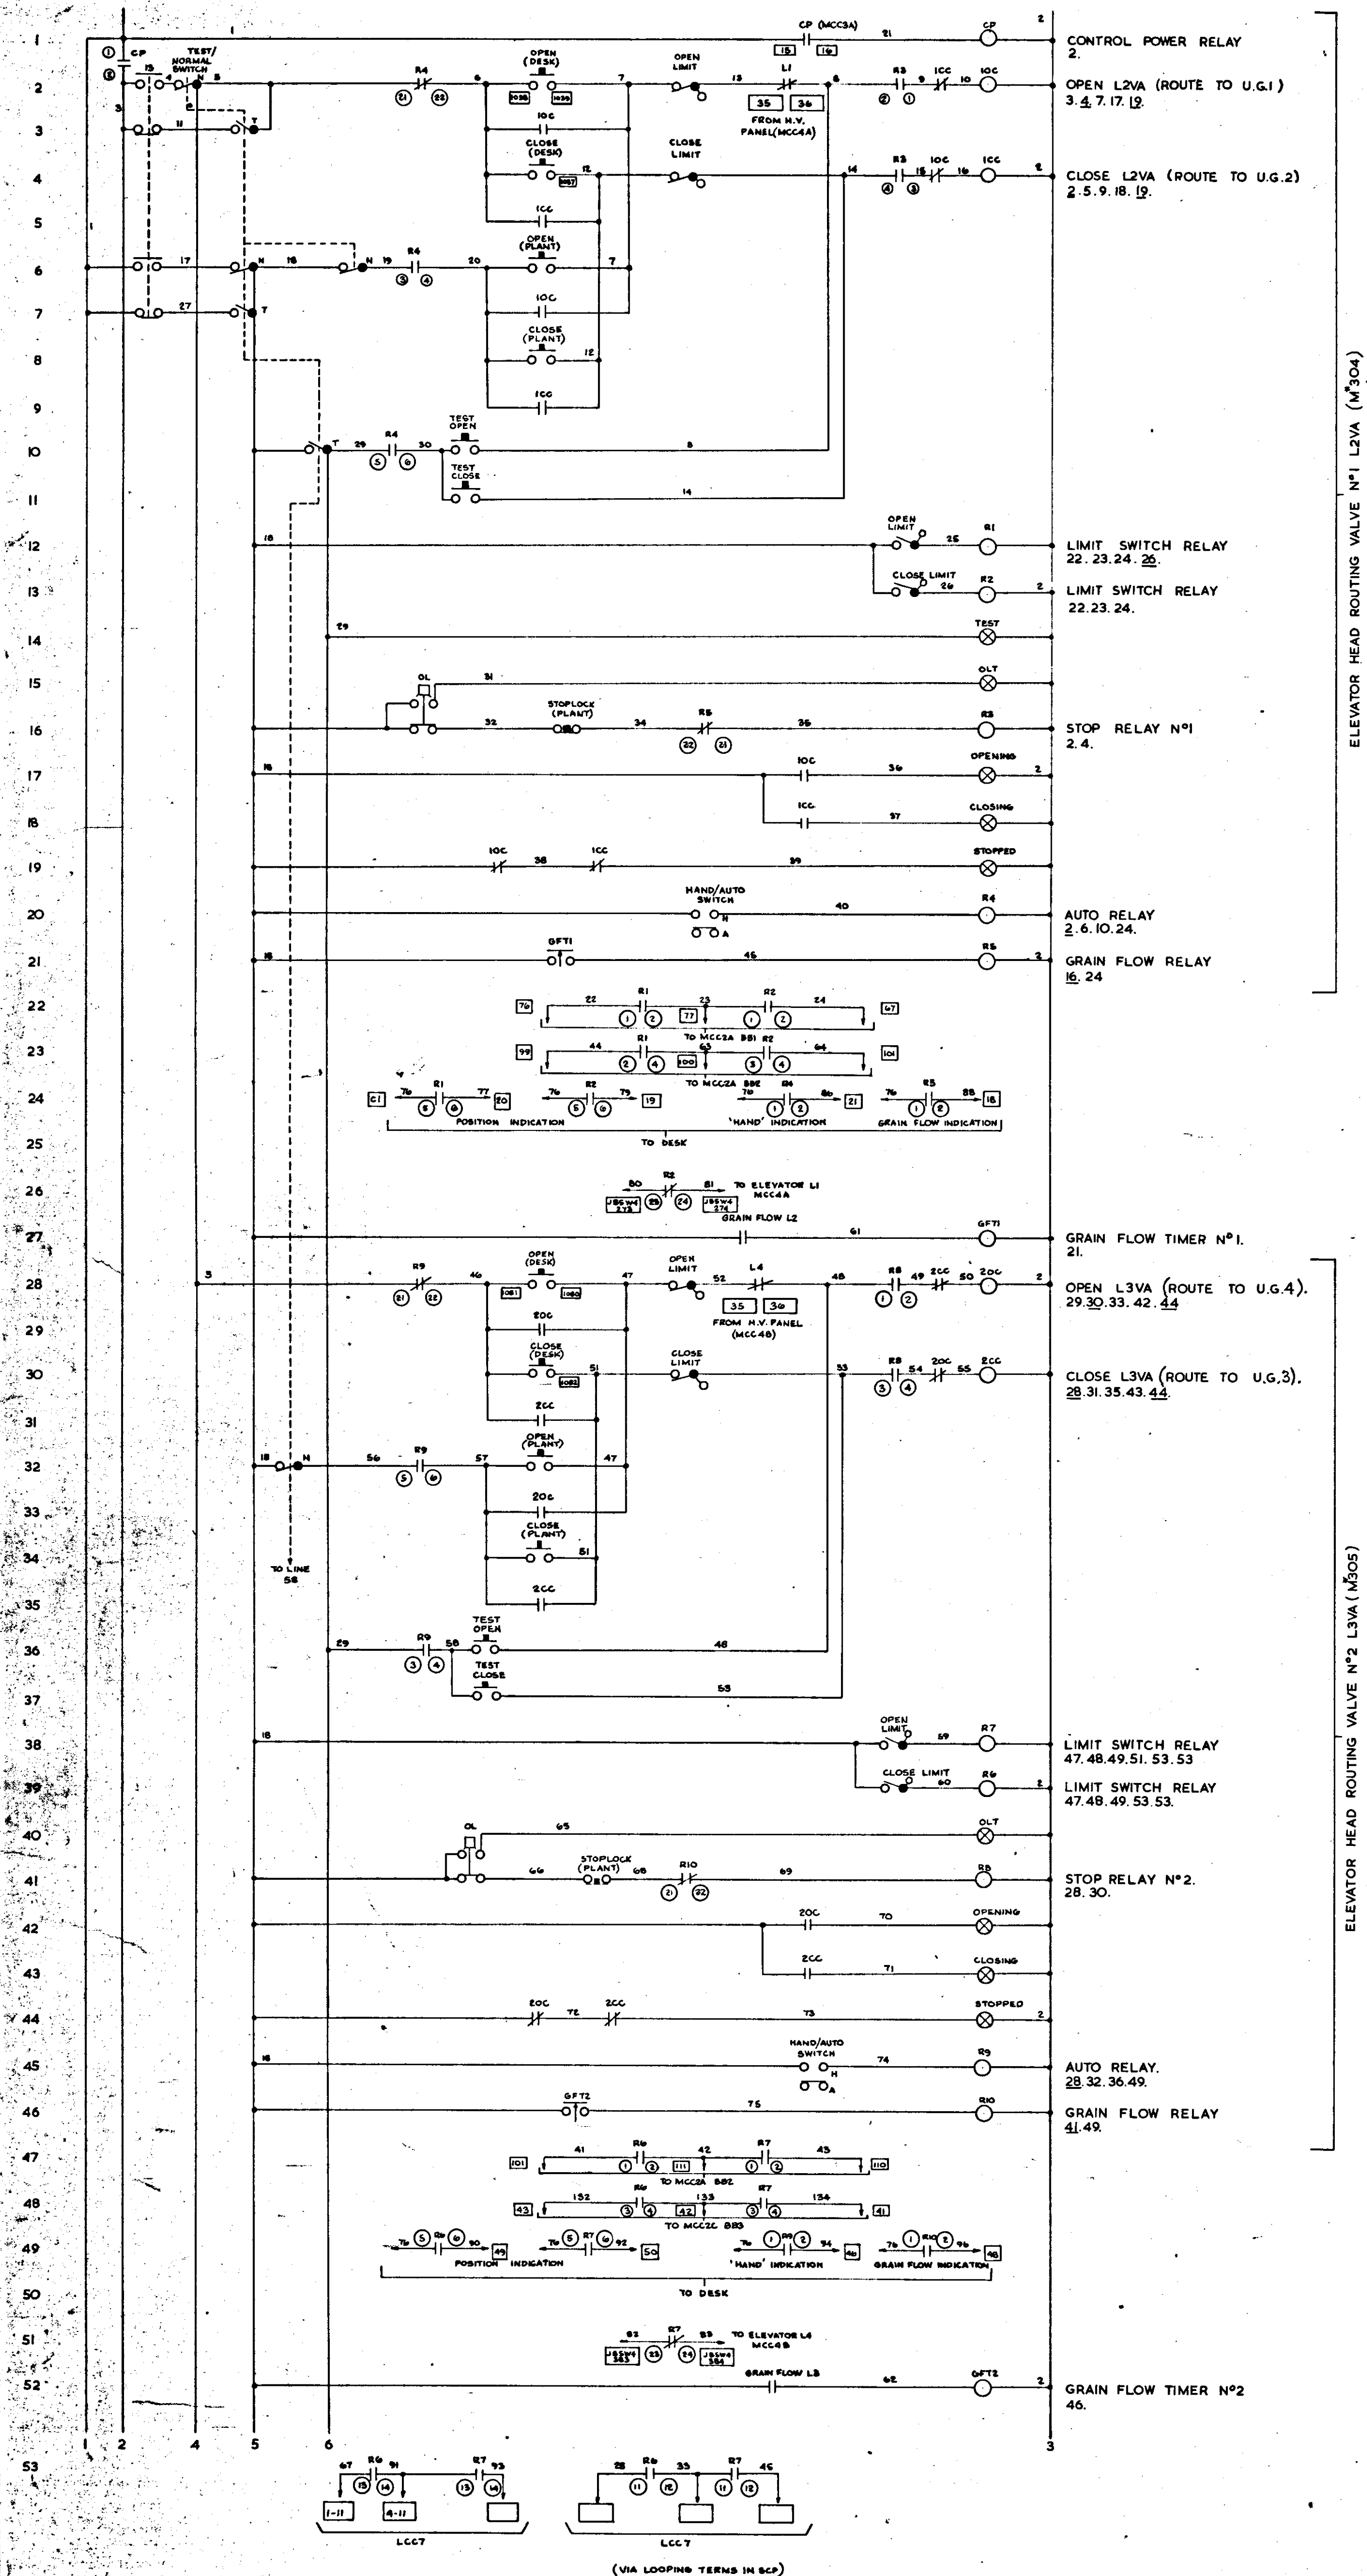

CONTINUED ON DTX 36IU/2

10733.

SCHEME FOR MCC3B-SEAFORTH GRAIN TERMINAL

THE DESIGN AND MANUFACTURING INFORMATION CONTAINED IN THIS DRAWING IS THE EXCLUSIVE RIGHT OF DEWHURST & PARTNER LTD. AND MUST NOT BE COPIED OR USED FOR MANUFACTURING PURPOSES.

ISSUE	112			
DTX36IU/1.				

DTX36IU/I.

DEWHURST & PARTNER LTD.
MELBOURNE WORKS HOUNSLOW

LE: SCHEME FOR MCC3B- SEAFORTH GRAIN TERMINAL.

REVISION: 10. ADDITIONAL CONTACTS TO RELAYS R6+R7	REVISION: 9. ROUTING VALVES REVERSED.	REVISION: 8 ADDITIONAL CONTACTS TO RELAYS R6+R7	REVISION: 7 DESK TERMINALS ADDED	REVISION: 6. LEVEL CONTROL TERMINALS ADDED	REVISION: 5 LIGHT+LAMP ADDED
ORIGIN: ICD. 5/1/73 ICD.	ORIGIN: SITE 27/12/72 J.S.	ORIGIN: ICD 20/1/72 J.S.	ORIGIN: 31/1/72 J.S.	ORIGIN: EISP 2/9/71 J.T.	ORIGIN: EISP 2/9/71 S.G. B.J.C.

REVISION: 4 LZGV VALVE OPEN INDICATION TERMINAL WAS ITC	REVISION: 3 - MINOR DESIGNATION MOD, SCALE ROOM INDICATION MOD.	REVISION: 2 CONTACTS ON LINE 254 R6 ON LINE 2400 WERE R6 VALVE INDICATION ADDED TO #11, R16, R19, R23.	REVISION: 1 UPPER OWNER CONNECTIONS TO MISC ADDED
ORIGIN: E15P 80/3/71 SGD J.T.	ORIGIN: E15P 12/3/71 SGD J.T.	ORIGIN: E15P 2/2/71 SGD J.T.	ORIGIN: E15P 4/2/71 SGD J.T.

	DRAWN BY J.F.
	DATE. 7.12.'70
	CHECKED BY
	APPROVED BY.
	DATE

KEY DIAG. N°.
EXT. DIAG. N°.
REL. DIAG. N°.
PANEL LAYOUT N°.