
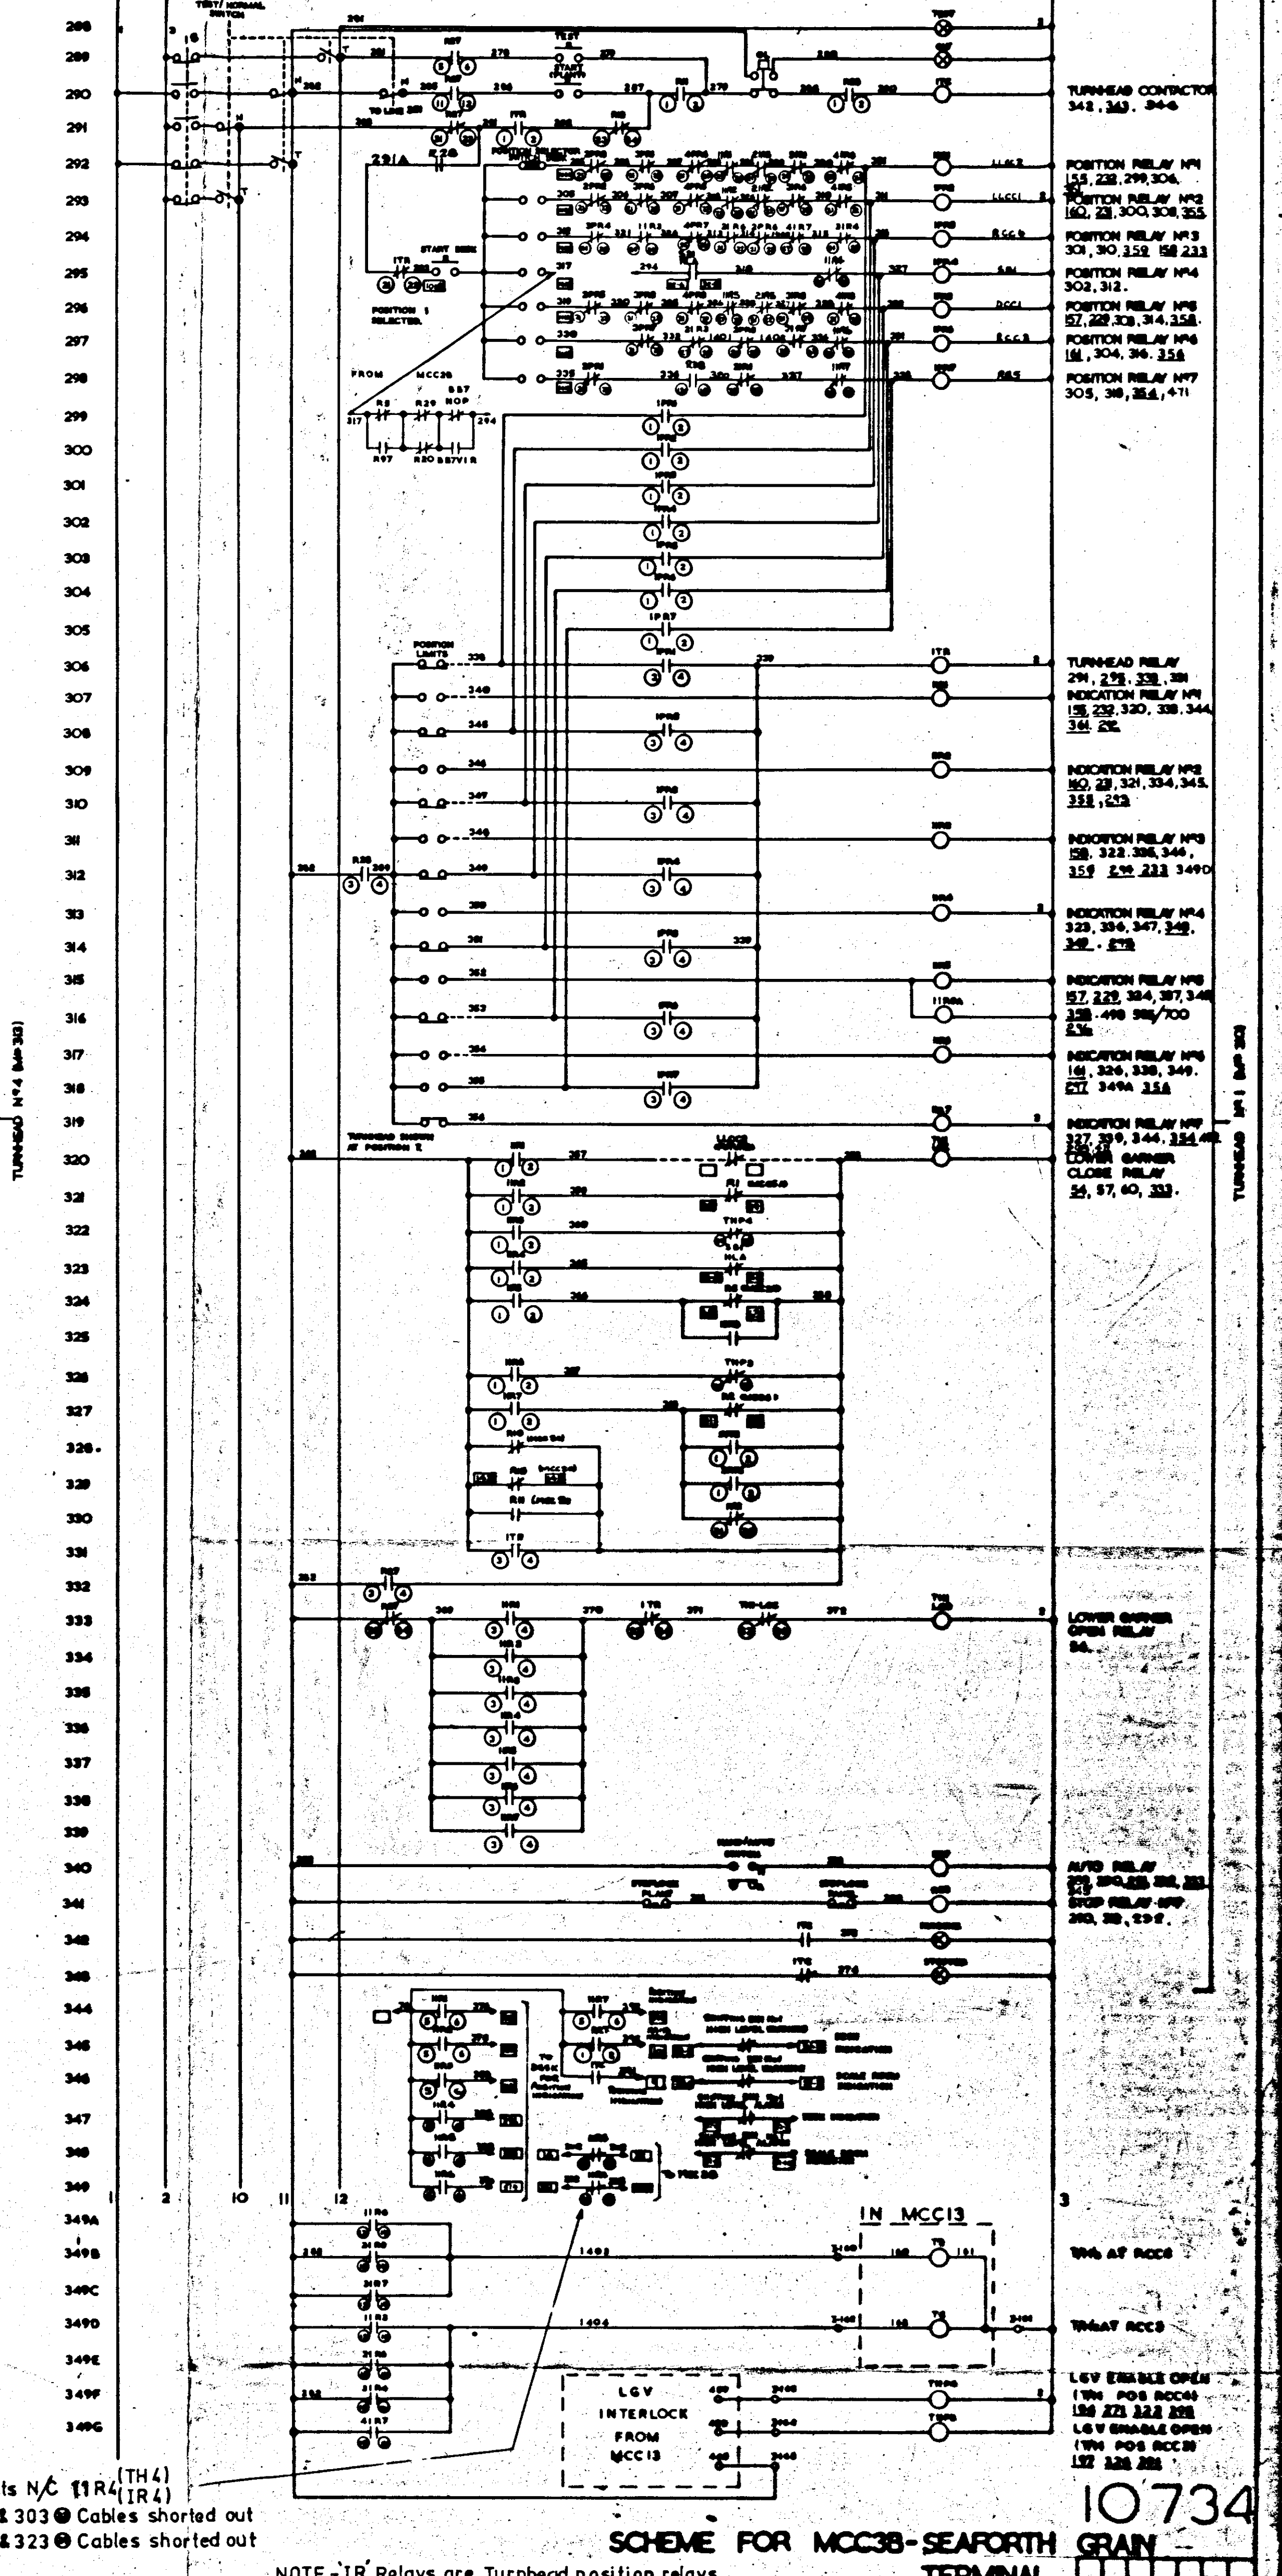
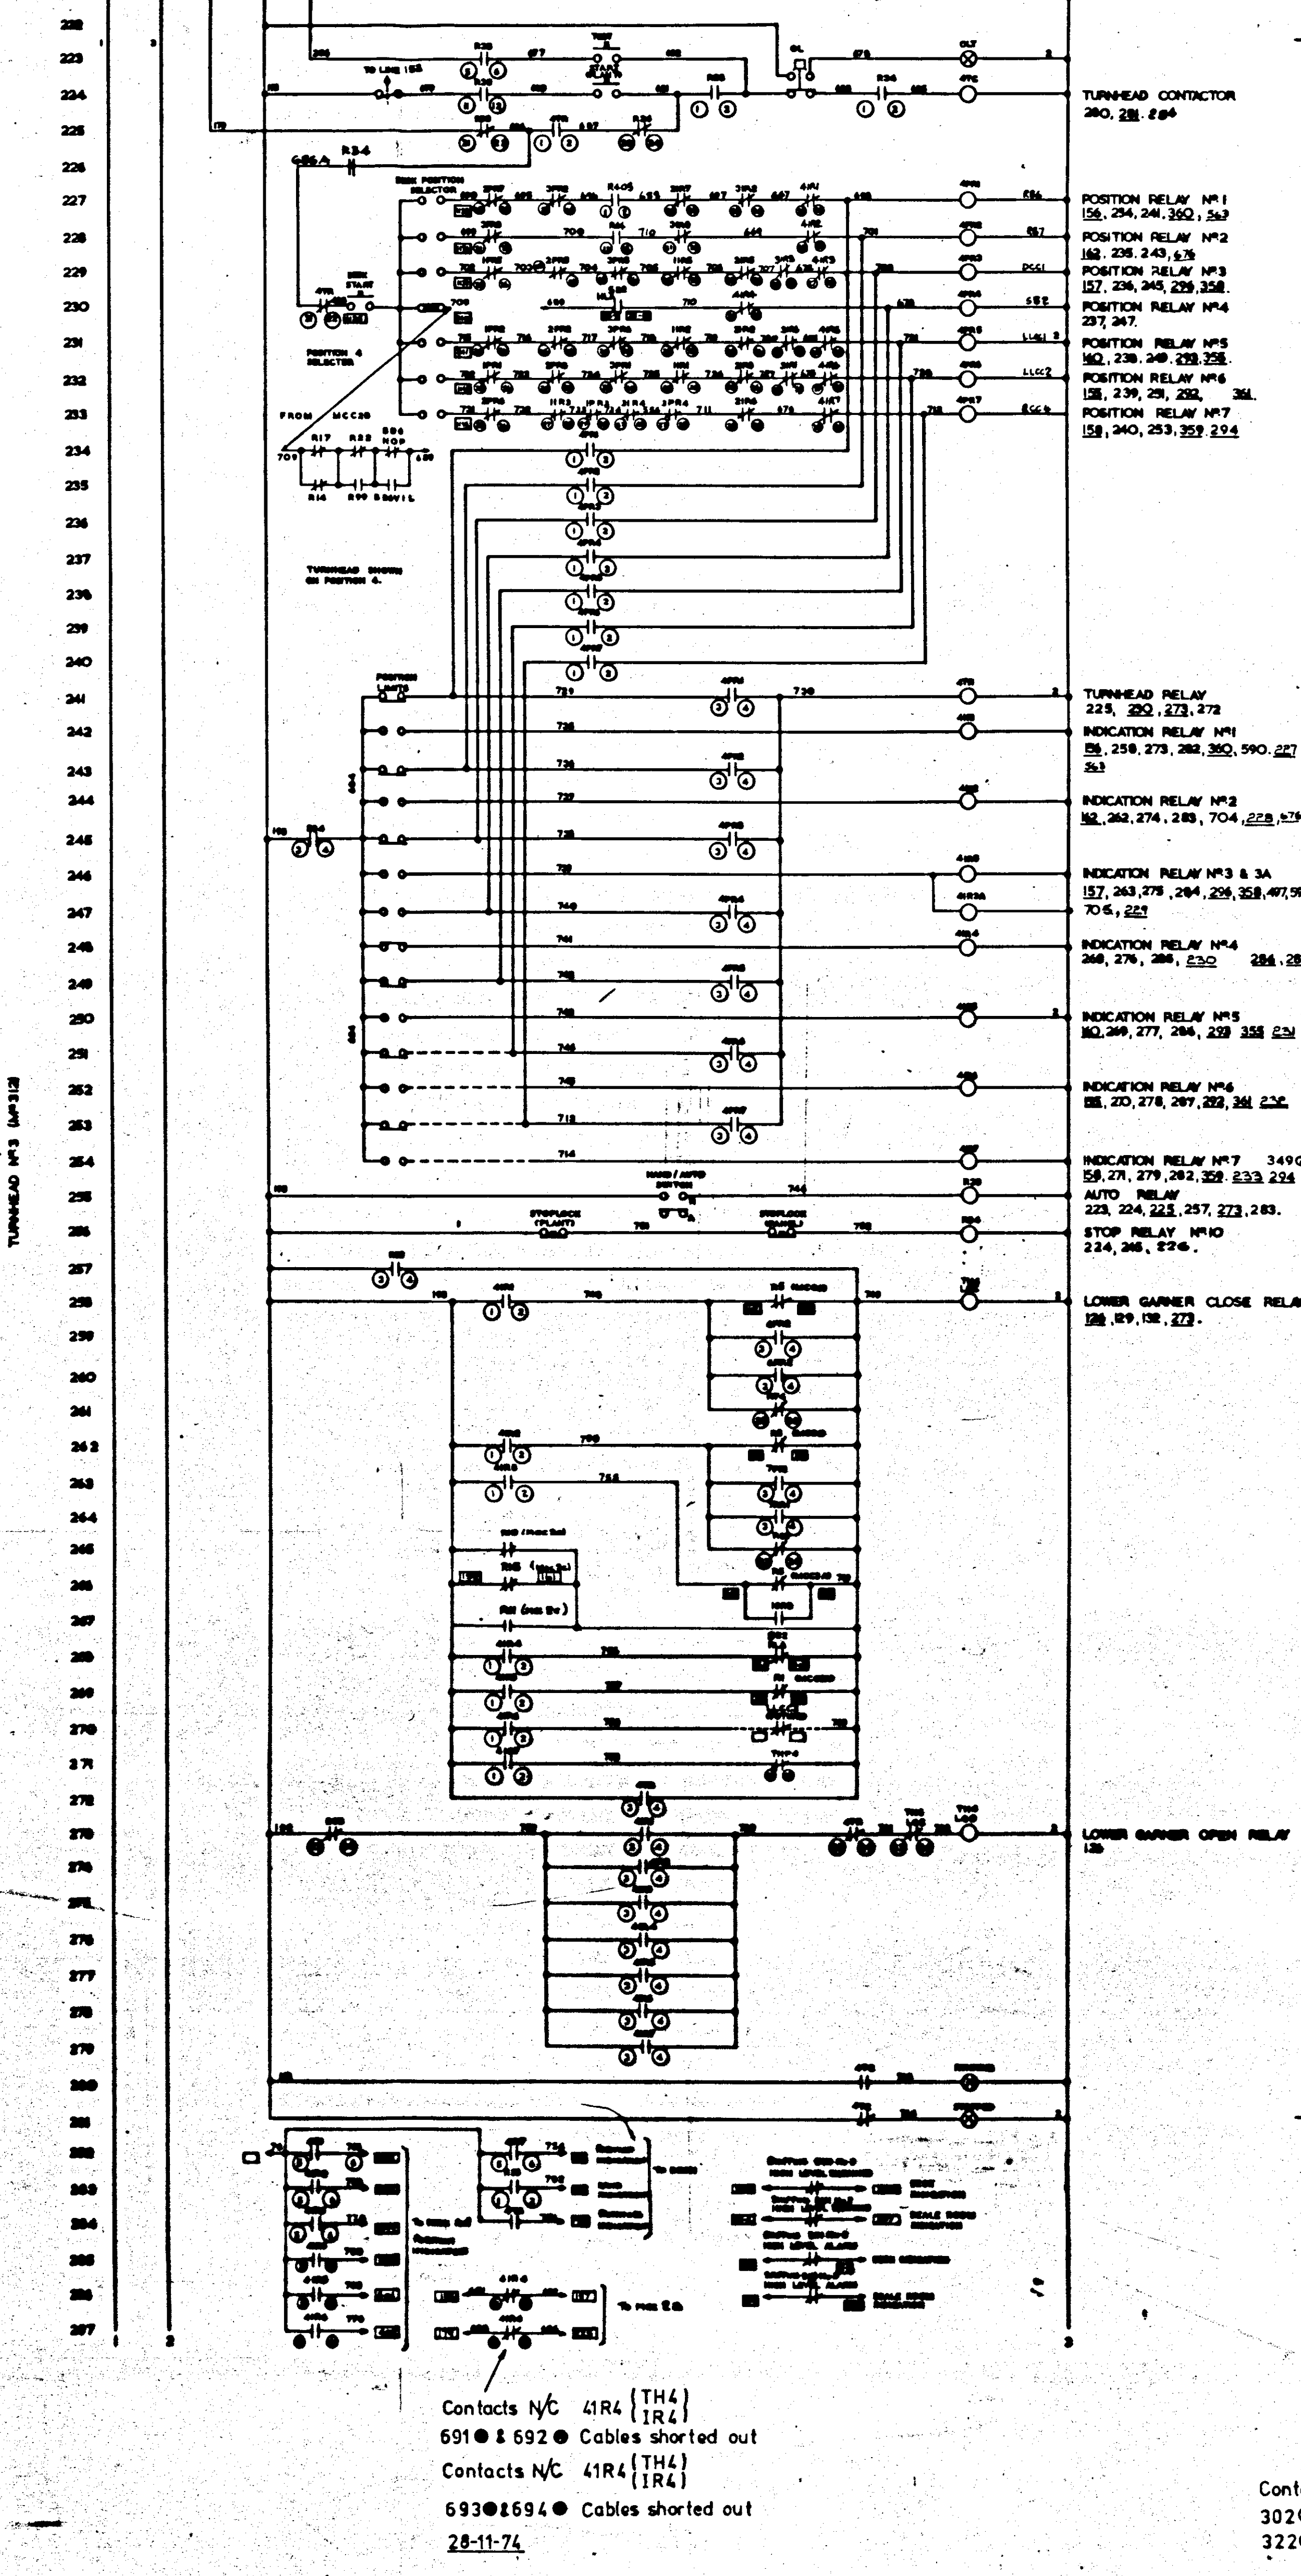


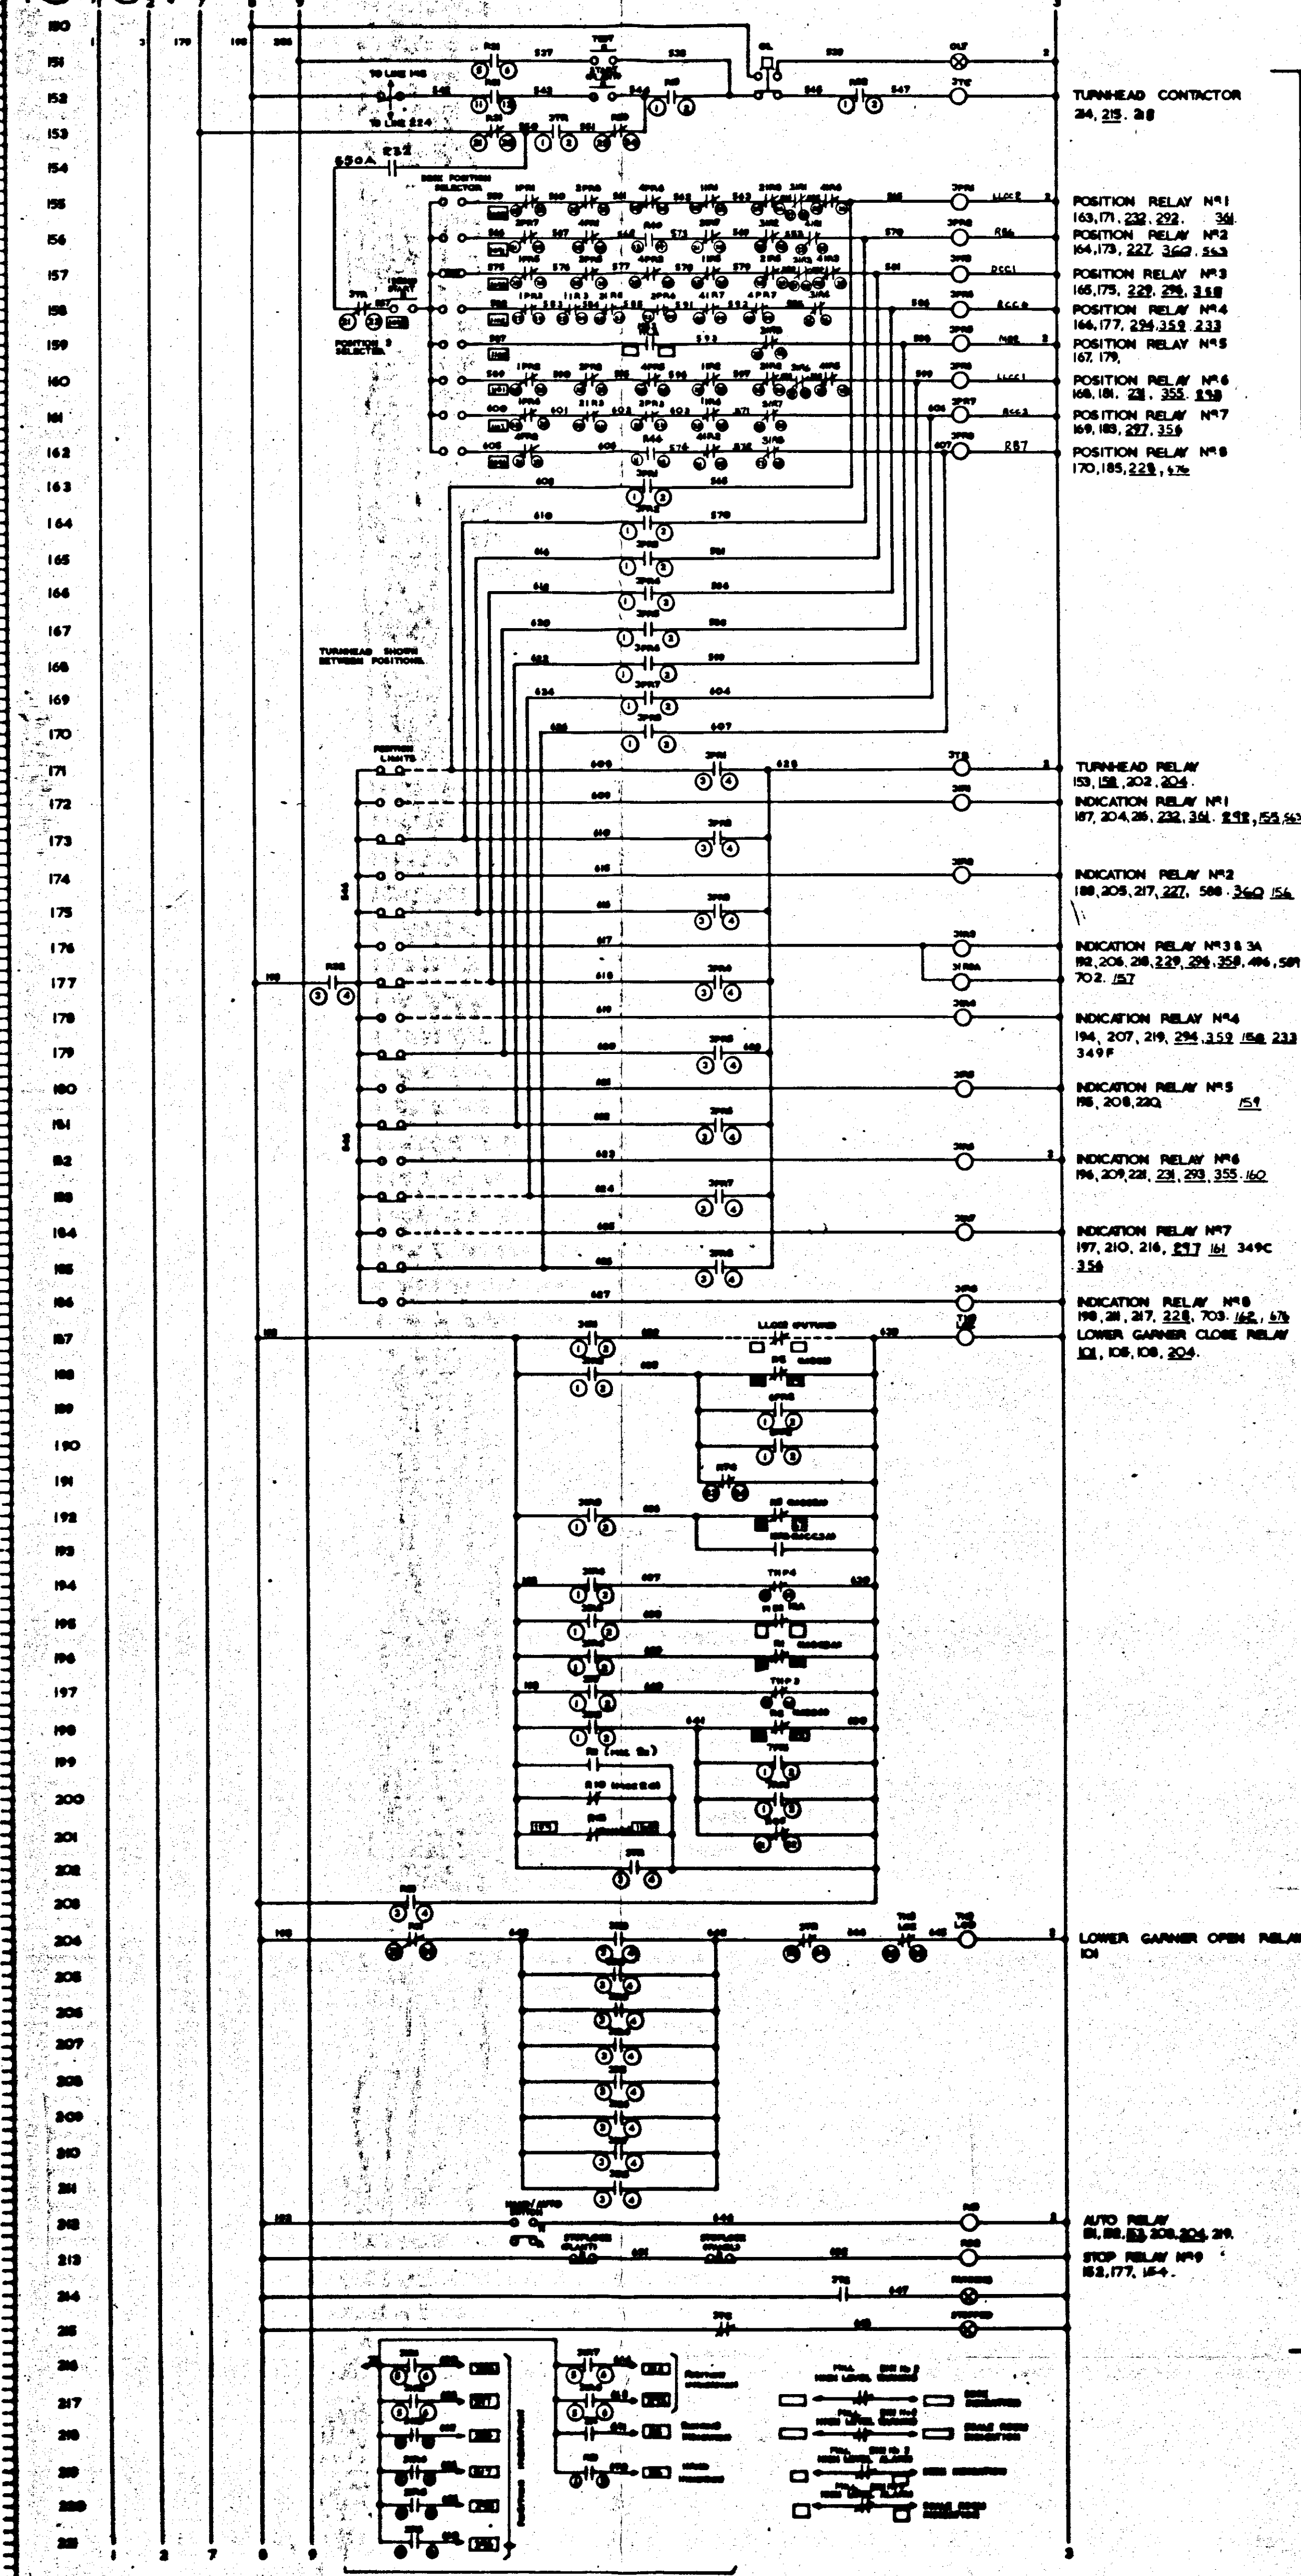

Contacts N/C 41R4 (TH4)
691 & 692 Cables shorted out
Contacts N/C 41R4 (TH4)
693 & 694 Cables shorted out
28-11-74

Contacts N/C 11R4 (TH4)
302 & 303 Cables shorted out
322 & 323 Cables shorted out

NOTE - IR Relays are Turnhead position relays

SCHEME FOR MCC3B-SEAFORTH GRAIN

TERMINAL