
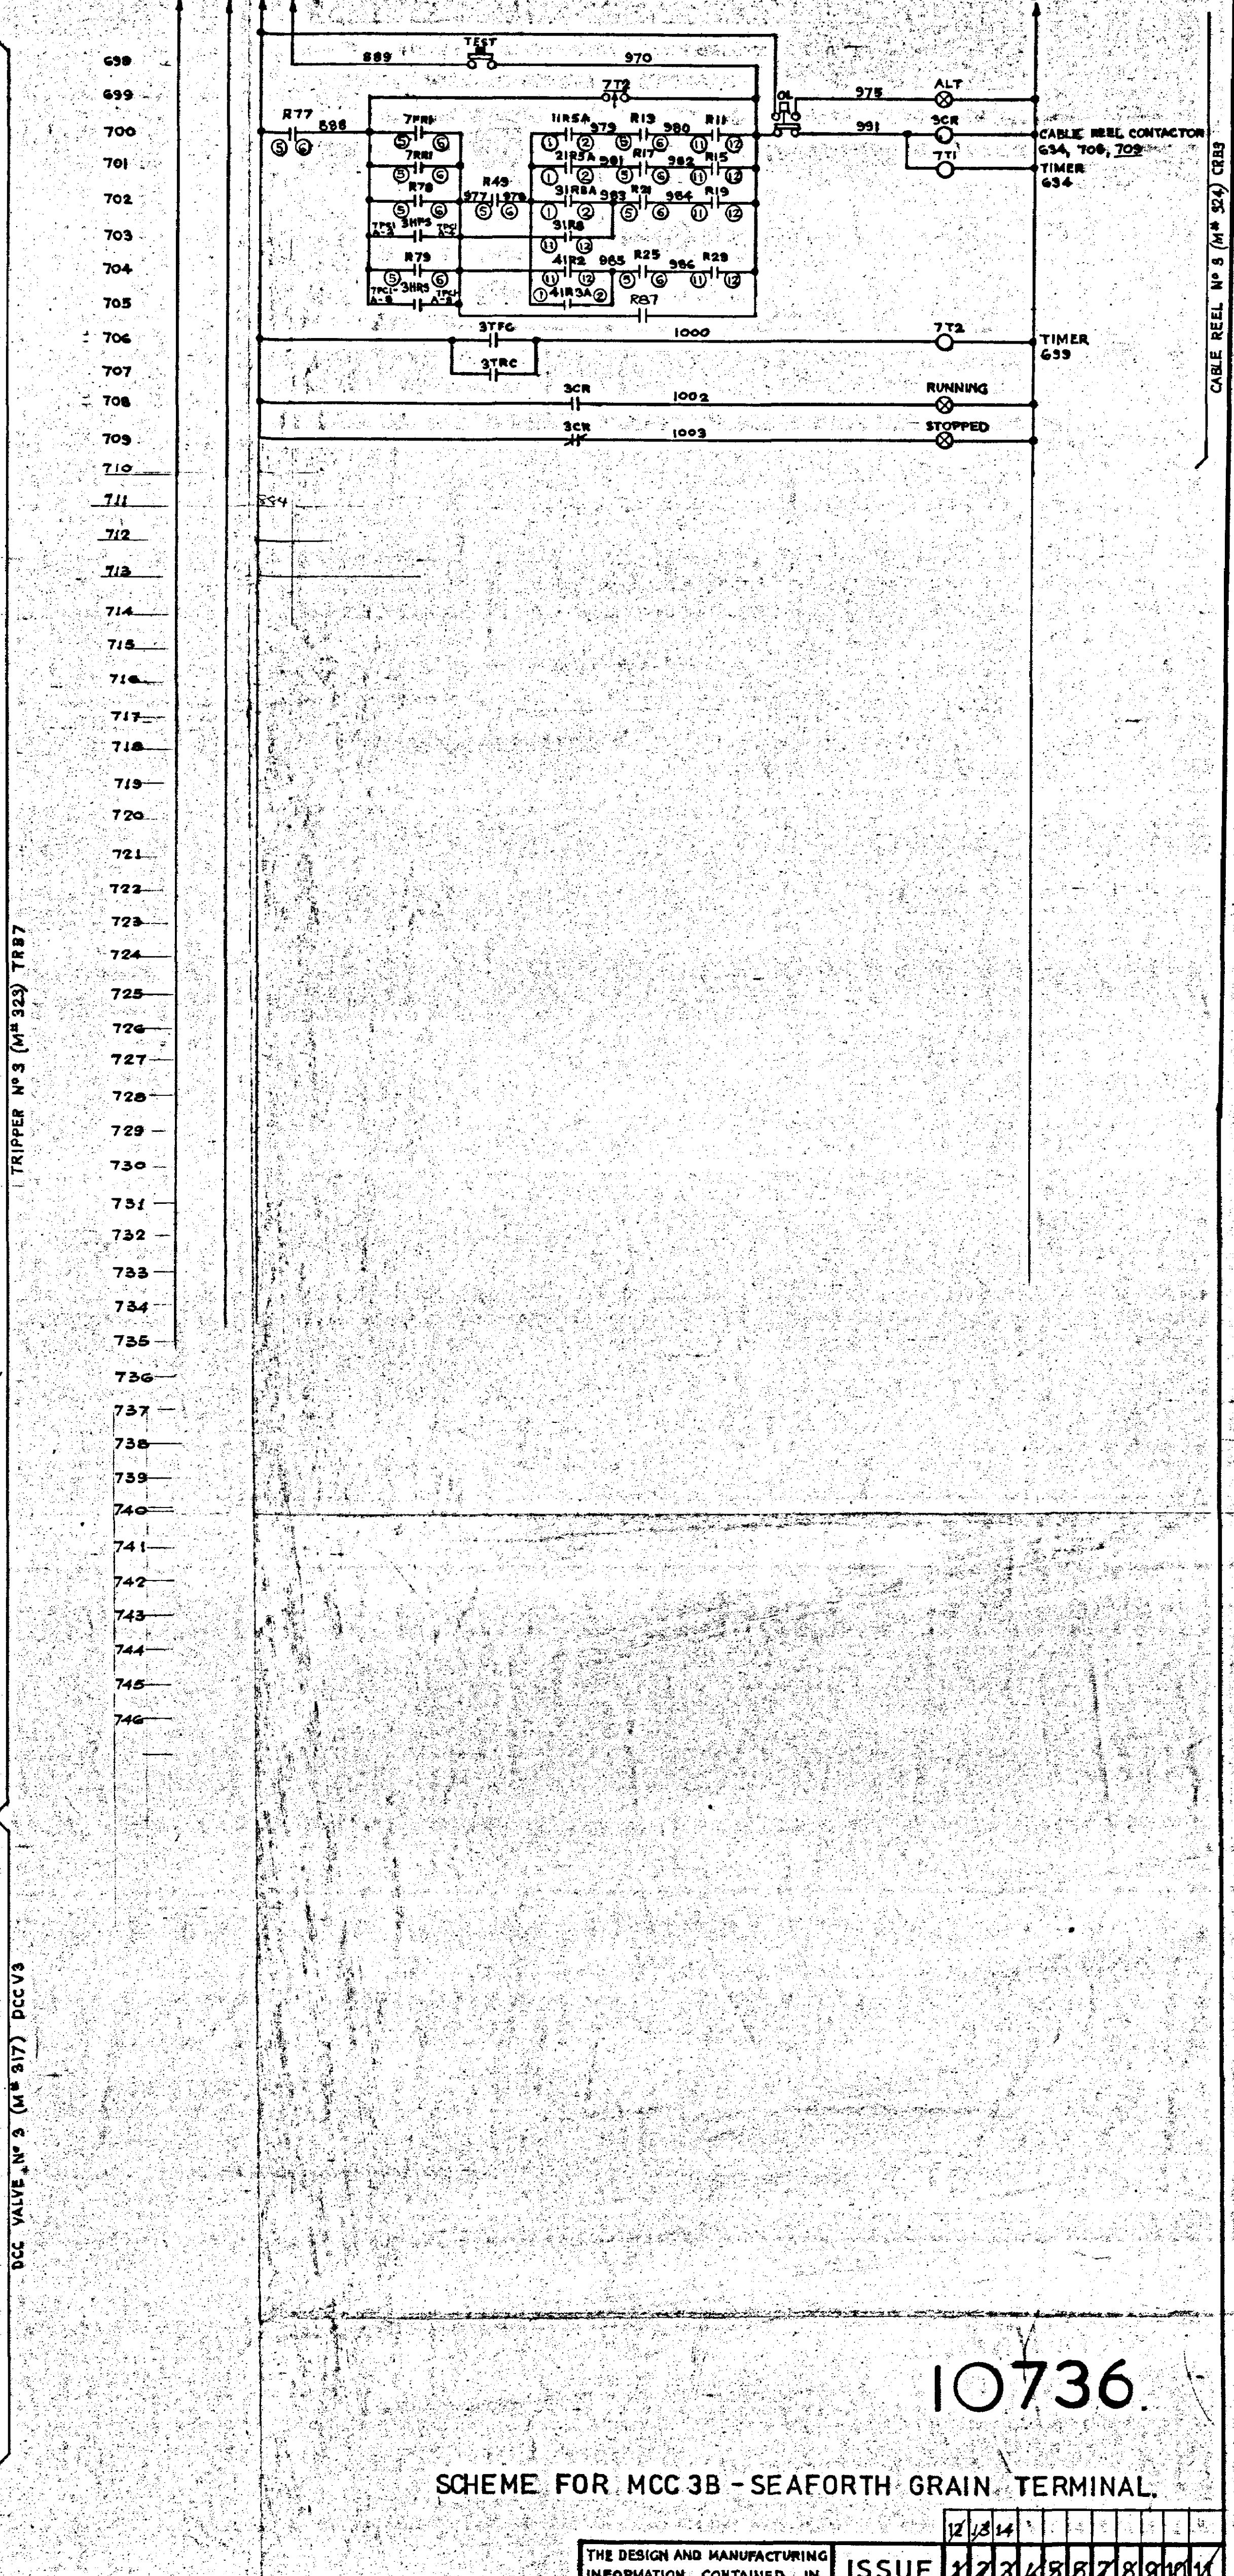
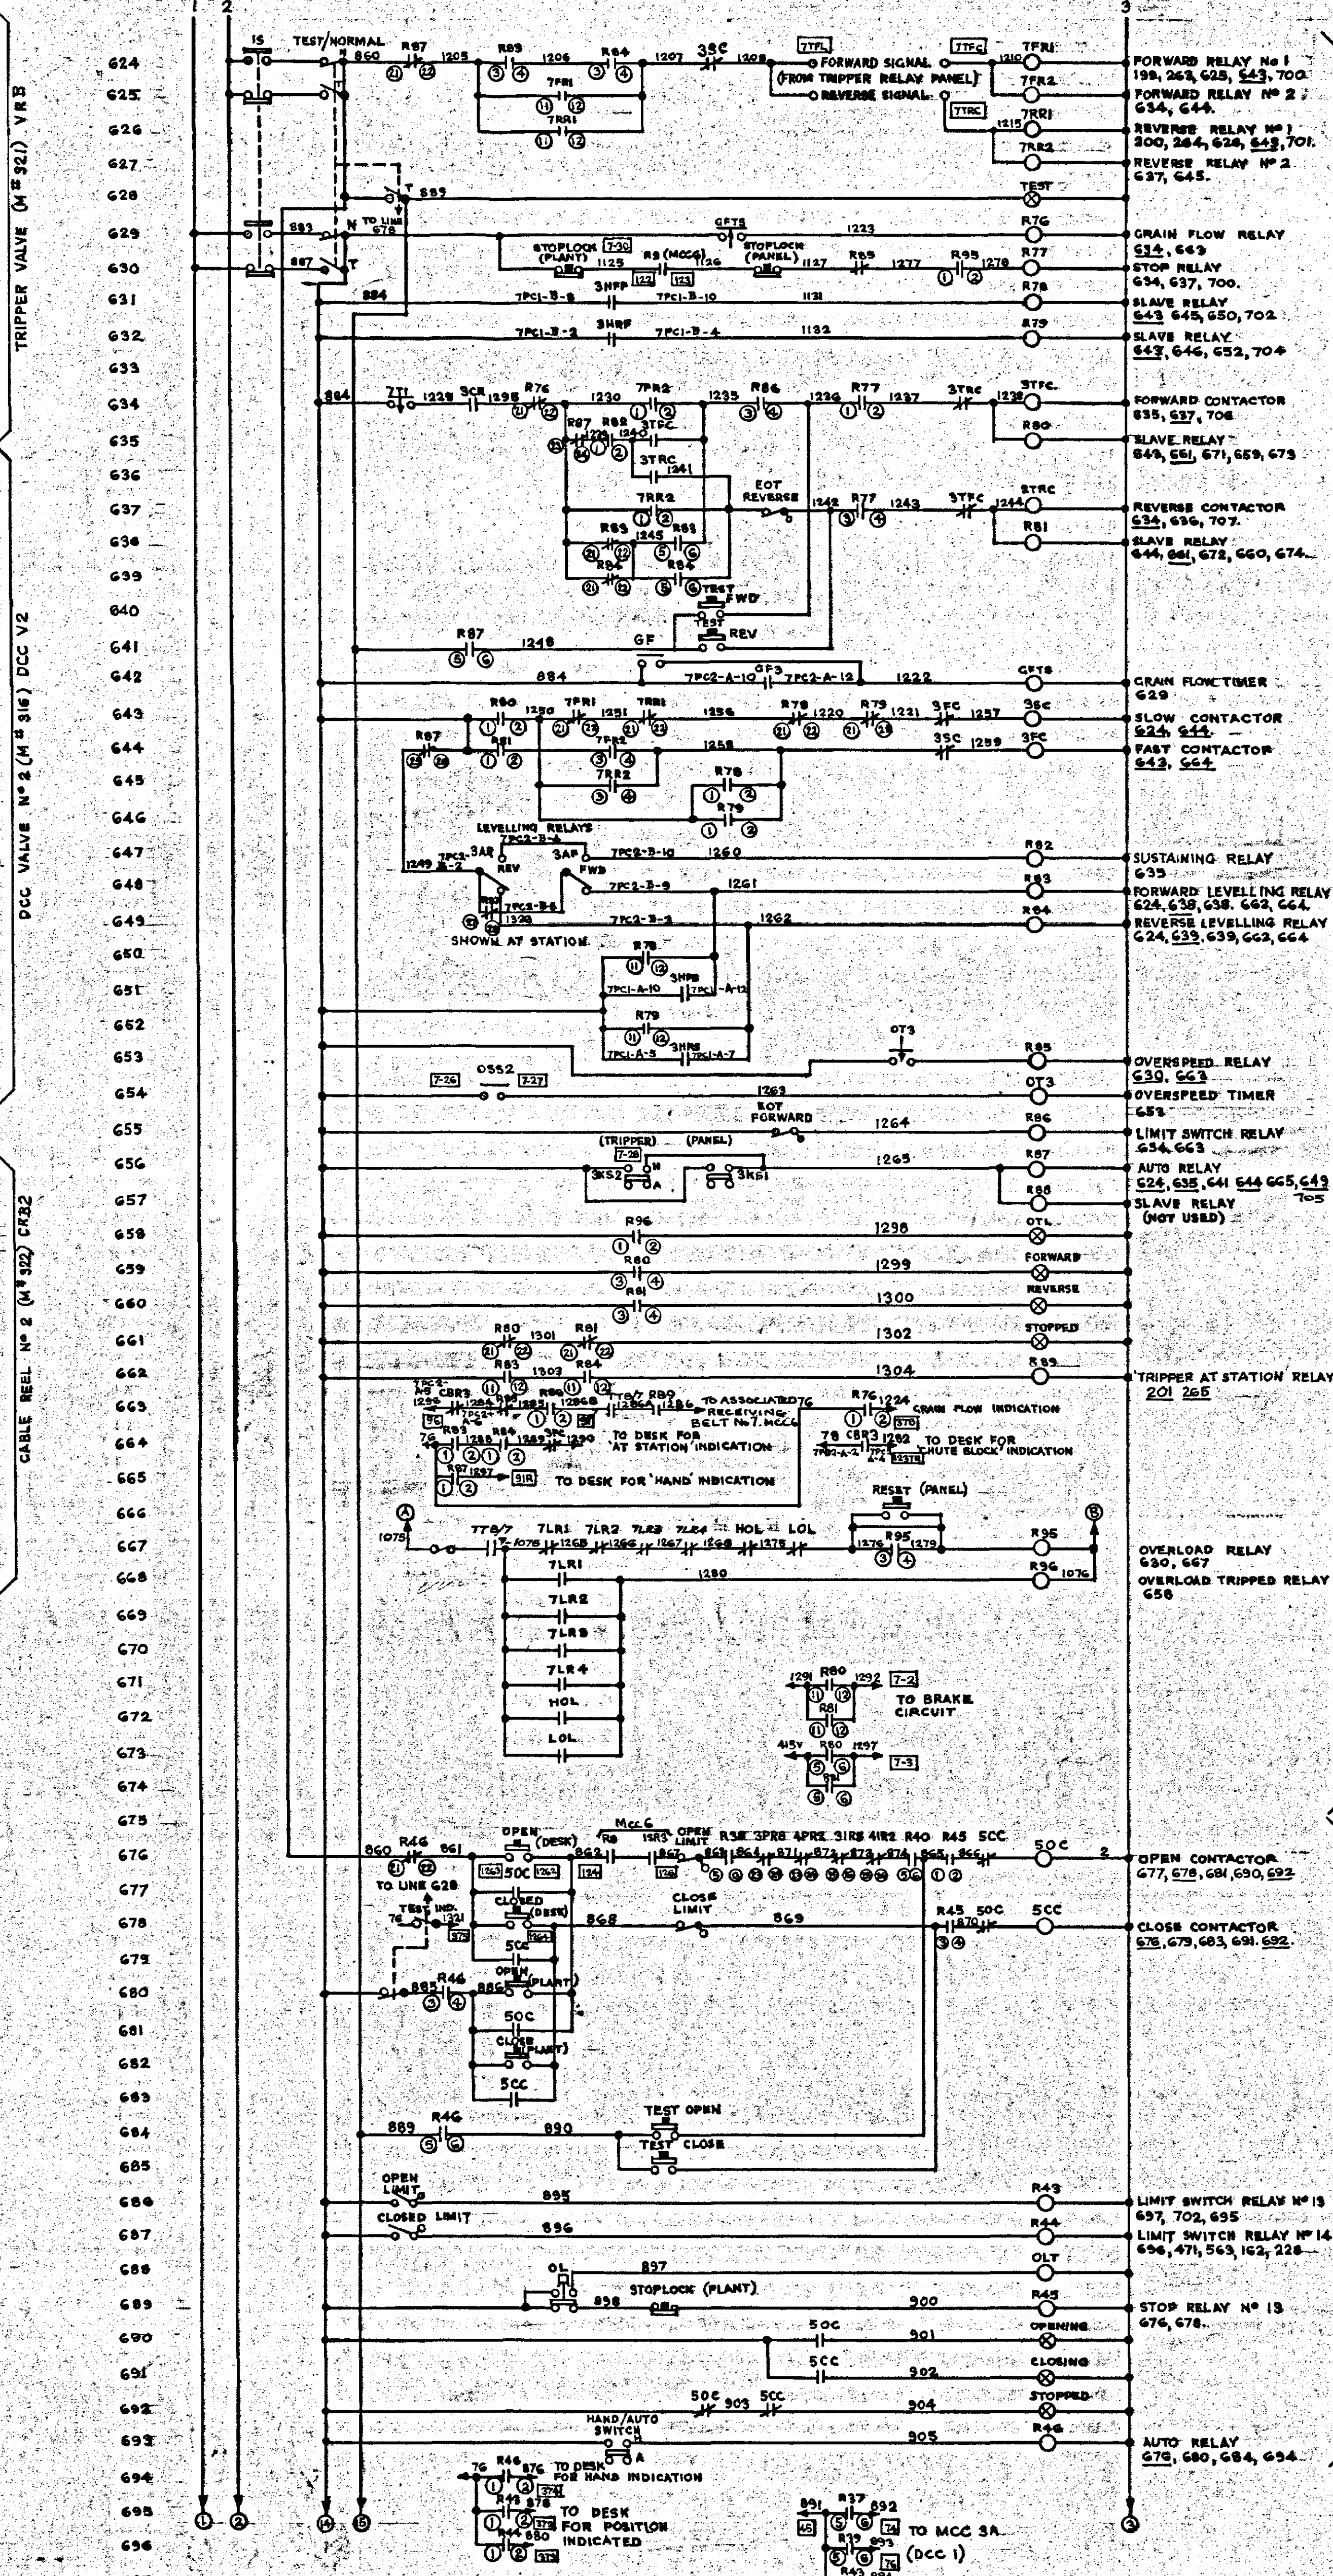


10736

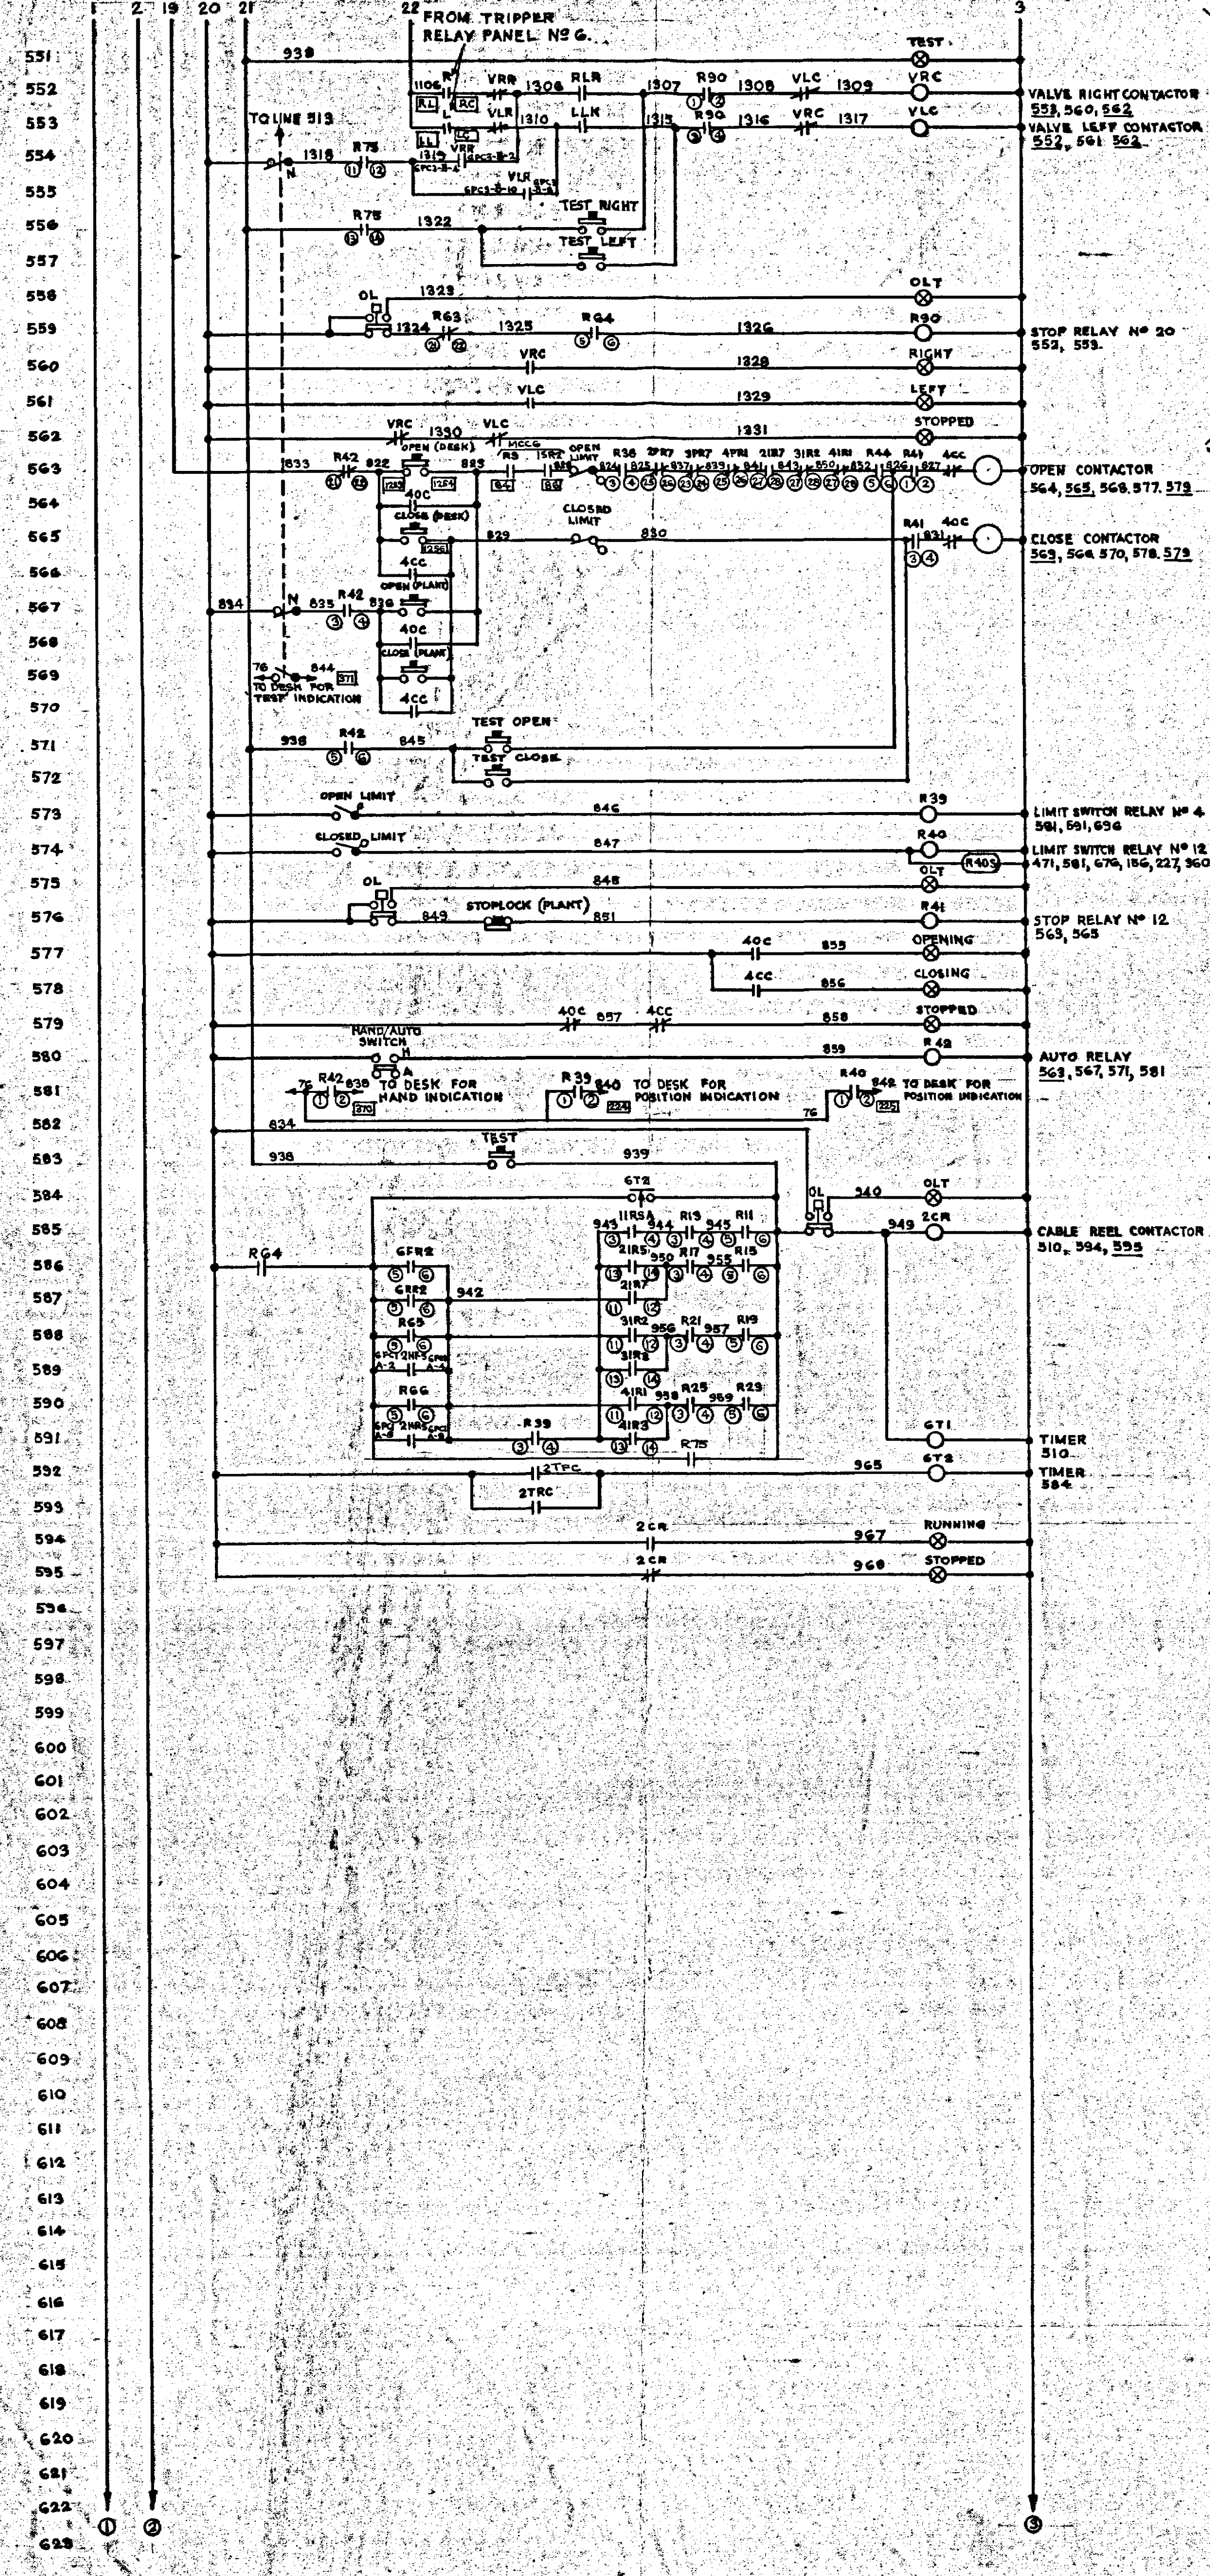

10736

SCHEME FOR MCC 3B - SEAFORTH GRAIN TERMINAL

DEWHURST & PARTNER LTD.
MELBOURNE WORKS. HOUNSLOW.

TITLE: SCHEME FOR MCC 3B SEAFORTH GRAIN TERMINAL

REVISION: 9
OVERSPEED
TIMER ADDED
ORIGIN: ICD
16/1/79 JS

REVISION: 8
TRIPPER OVERLOADS
REPLACED BY RELAY
& HOL & LOL
ORIGIN: ICD
9/1/79 JS

REVISION: 7
INTERLOCKING FROM TRIPPER
ADDED TO OPEN CONTACTOR
552 & 553/559. NOW
N/O SO RELAY R 85
CONTACTS. NOW N/O
BRAKE CIRCUIT.
ORIGIN: ICD
18/3/79 JS

REVISION: 6
TURNHEAD INTERLOCKING
ADDED TO OPEN CONTACTOR
LINE STOP RELAY CONTACT
ADDED TO CABLE REEL
ORIGIN: ICD
18/3/79 JS

REVISION: 5
DESK TERMINALS
ADDED.
ORIGIN: ICD
1/2/78 GED. JS

REVISION: 4
CHUTE BLOCK
INDICATOR ADDED
TO TERM 7C
ORIGIN: E18
10/5/71 GED. JT

REVISION: 3
25.3.3AR, 5AR & 6AR
CONTACTS MODIFIED
ORIGIN: E18
2/2/71 GED. JT

REVISION: 2
3AR & 5AR
CONTACTS MODIFIED
ORIGIN: E18
26/2/71 GED. JT

REVISION: 1
RED CONTACT MOVES FROM
LINE 5AR TO 6AR, N/O
CONTACT ADDED TO LINE 6AR
WHICH WAS PREVIOUSLY
N/O. (SEE NOTE 1000)
ORIGIN: E18
19/2/71 GED. JT

DRAWN BY: A.M.
DATE: 19.1.71
CHECKED BY:
APPROVED BY:
DATE:

THE DESIGN AND MANUFACTURING
INFORMATION CONTAINED IN
THIS DRAWING IS THE EXCLUSIVE
RIGHT OF DEWHURST & PARTNER
LTD. AND MUST NOT BE COPIED
OR USED FOR MANUFACTURING
PURPOSES.

ISSUE 1 2 3 4 5 6 7 8 9 10 11

DTX 361U/4

DTX 361U/4

KEY DIAG NO
EXT. DIAG NO DTX 361U
REL. DIAG NO
PANEL LAYOUT NO HTX 361U