

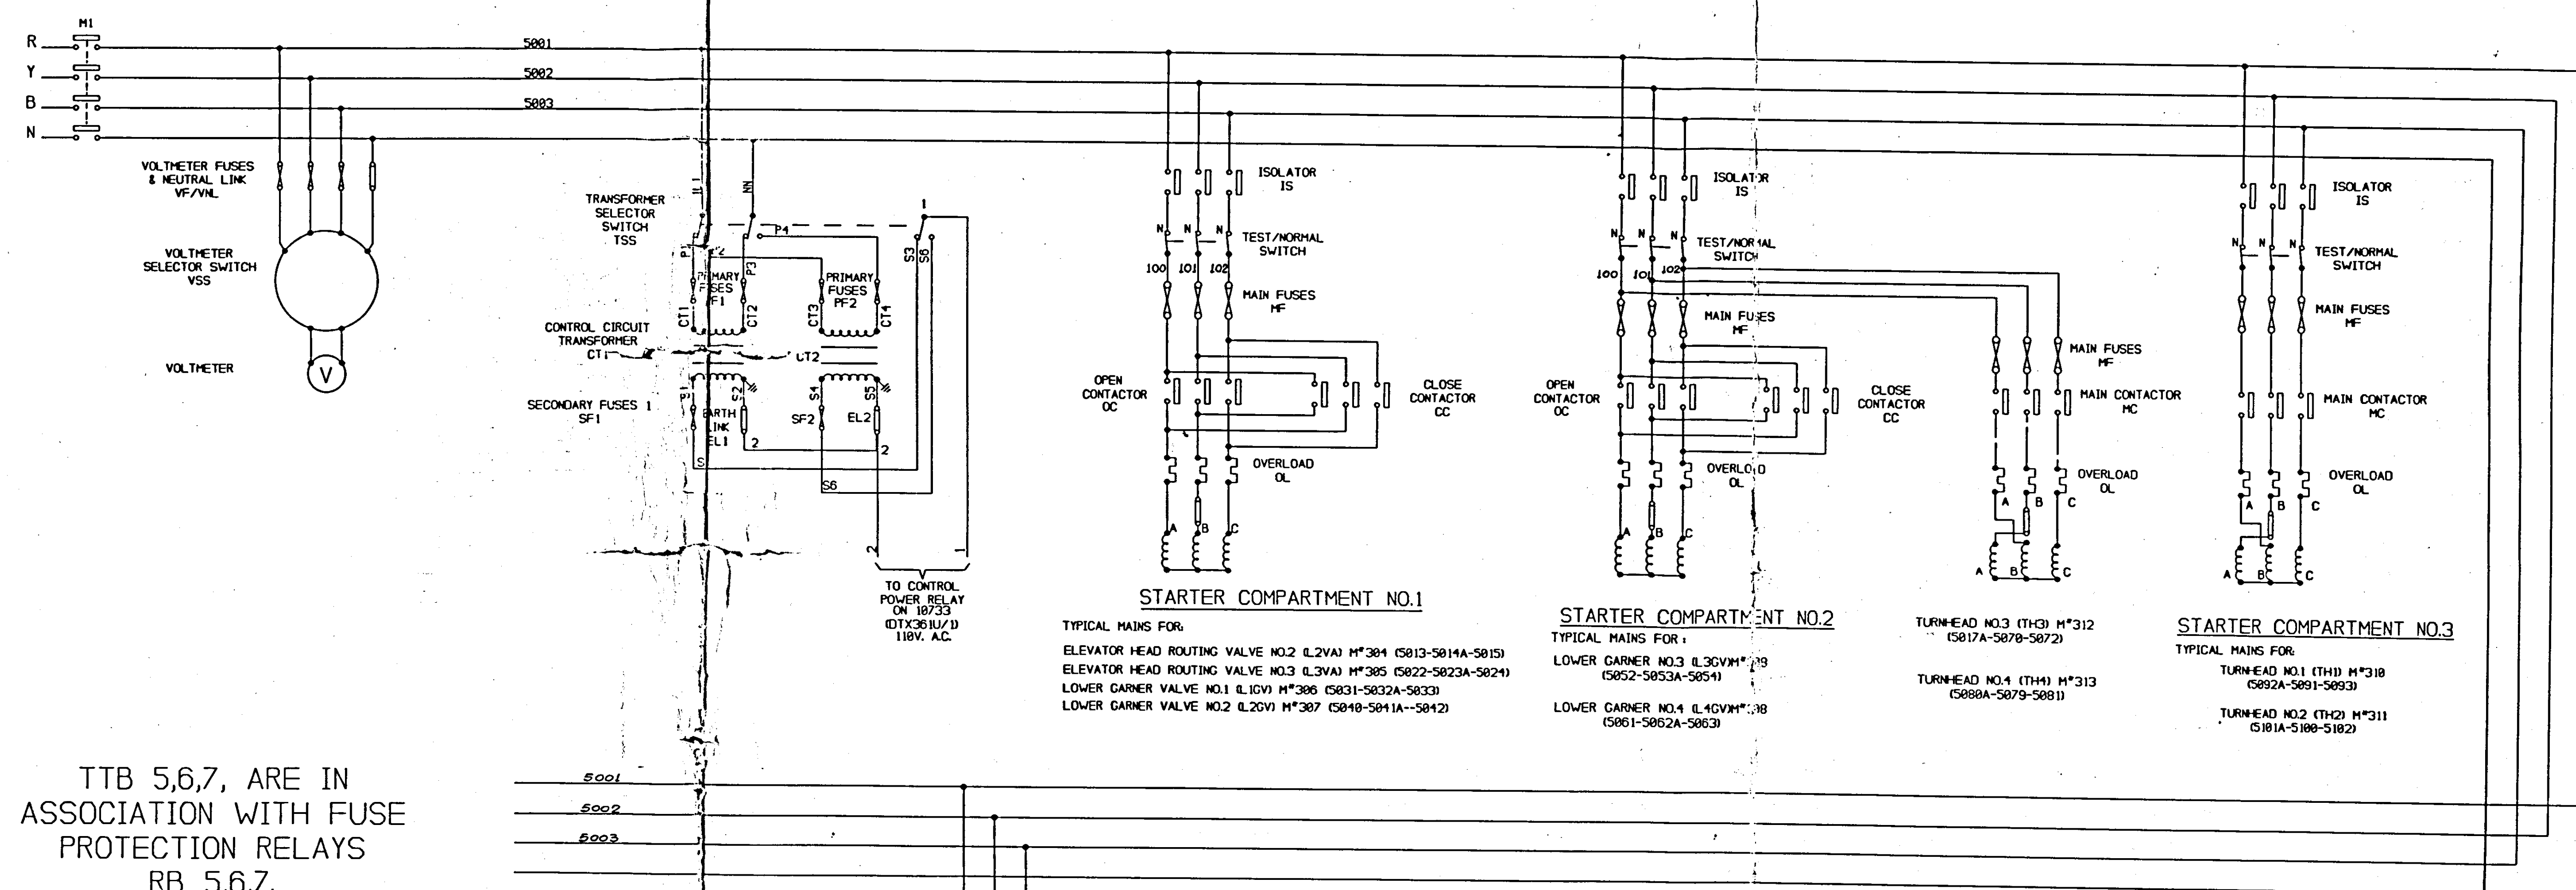


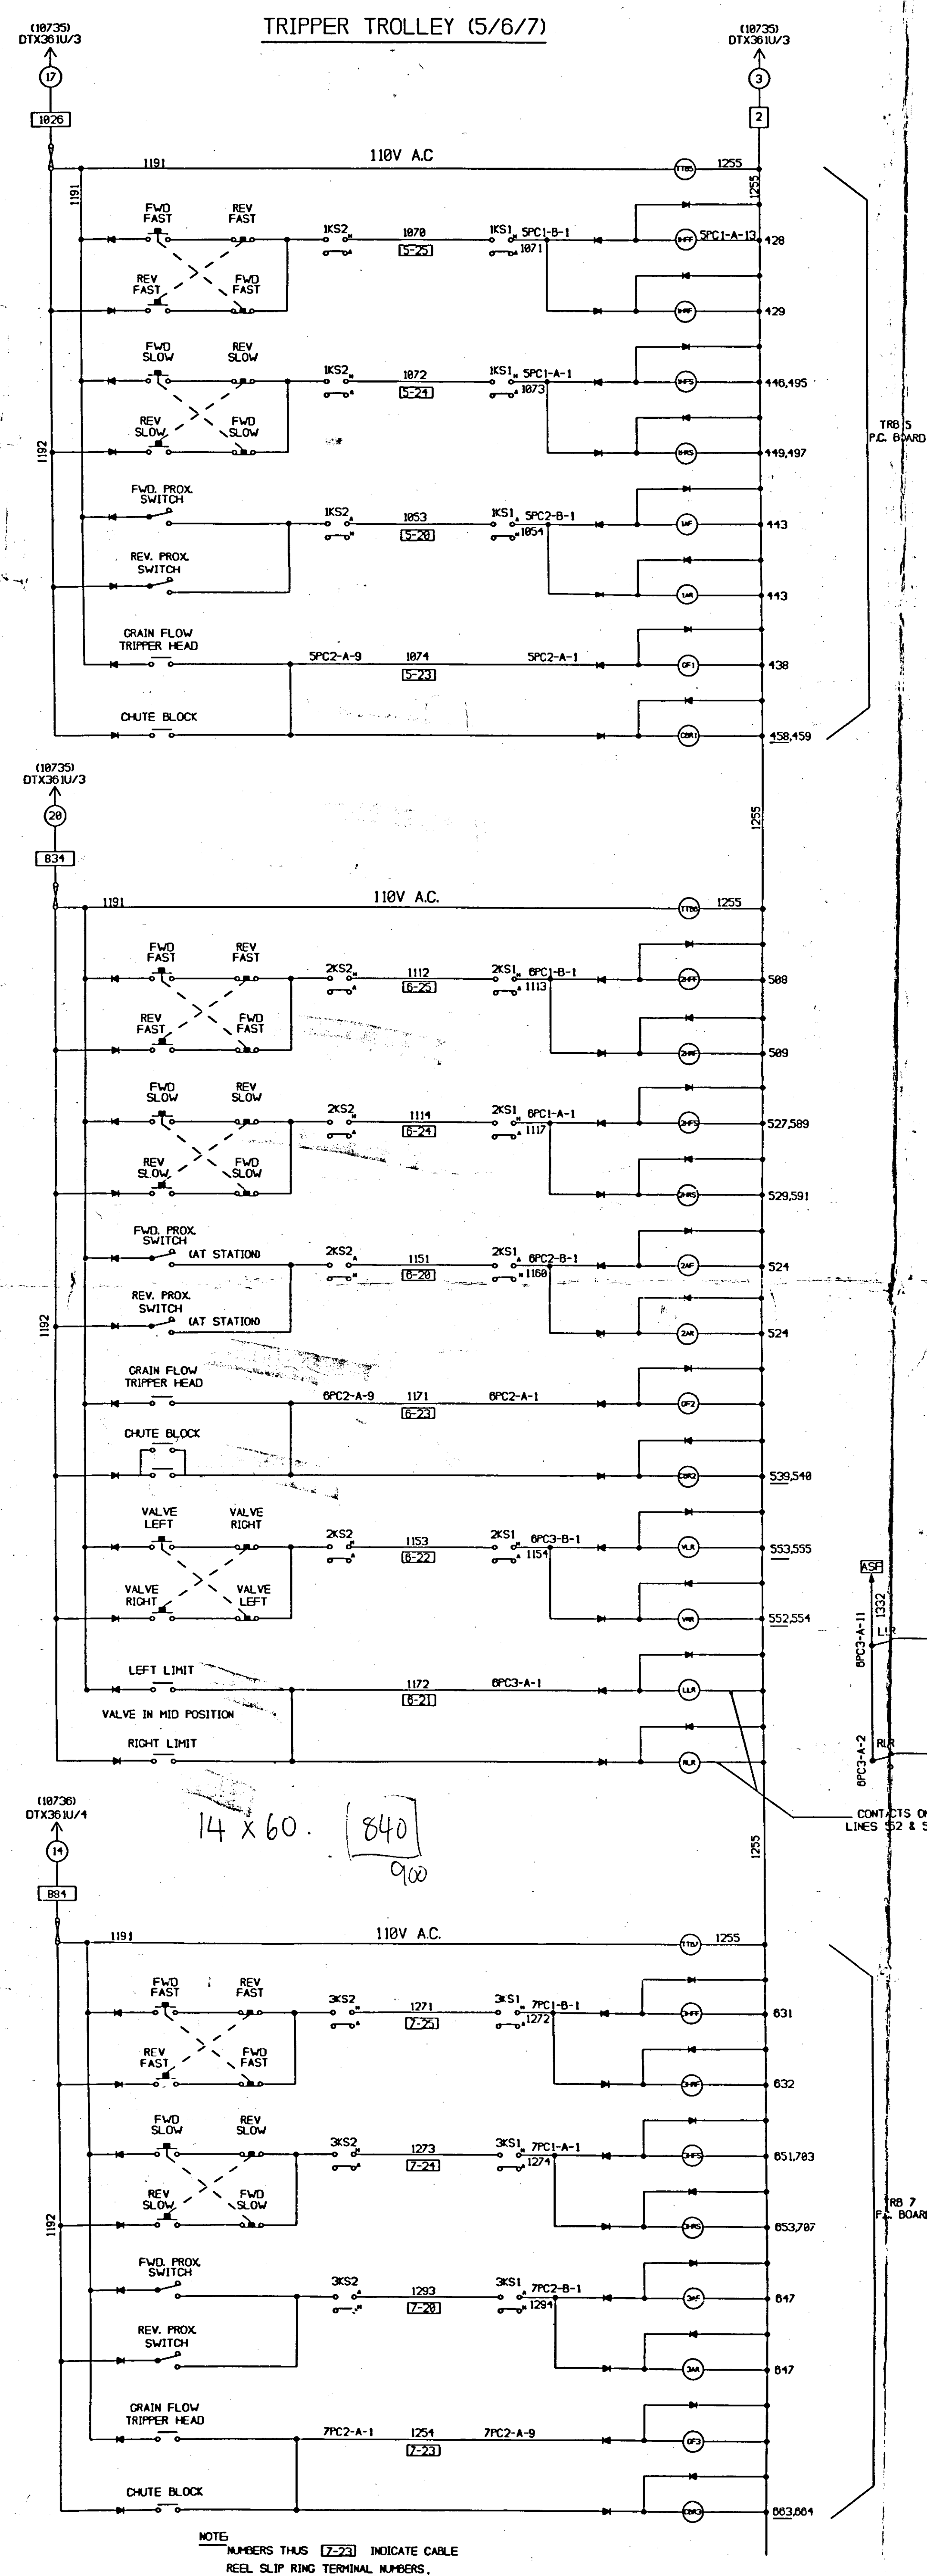

TTB 5,6,7, ARE IN
ASSOCIATION WITH FUSE
PROTECTION RELAYS
RB 5,6,7.

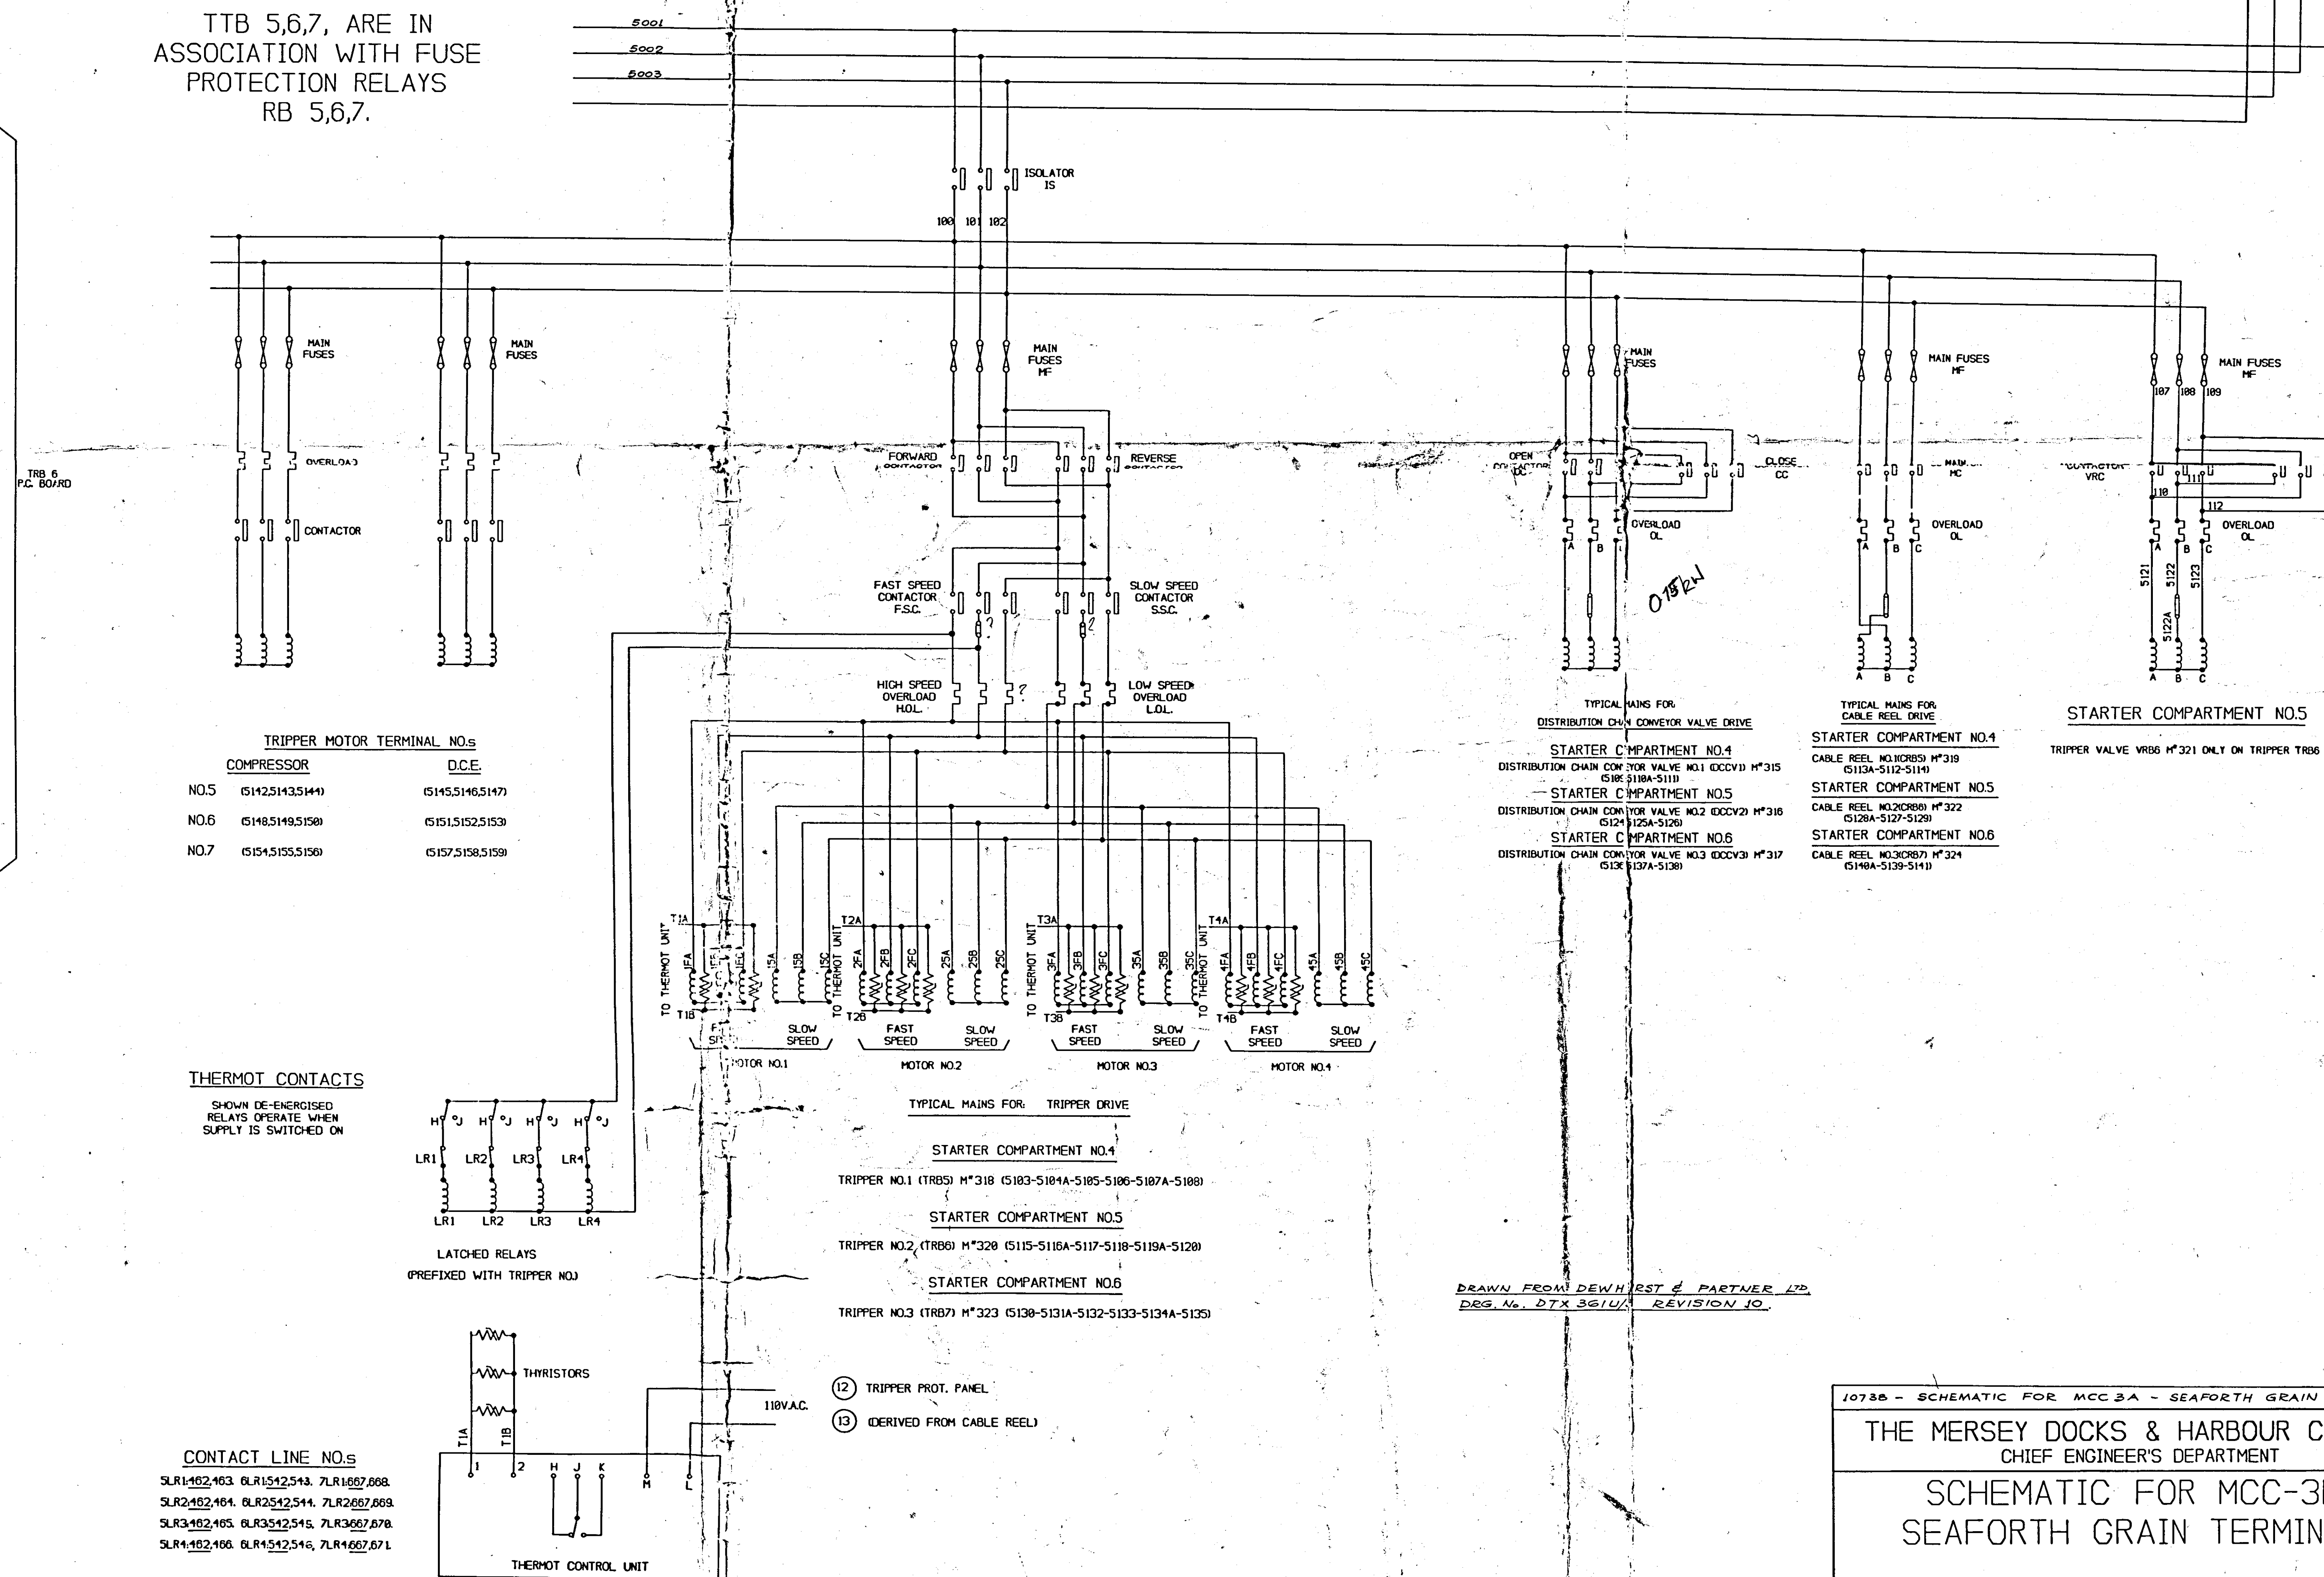

DRAWN FROM DEWHIRST & PARTNER LTD.
DRG. No. DTX 361U/1 REVISION 10

10738 - SCHEMATIC FOR MCC 3A - SEAFORTH GRAIN TERMINAL

THE MERSEY DOCKS & HARBOUR COMPANY
CHIEF ENGINEER'S DEPARTMENT

SCHEMATIC FOR MCC-3B
SEAFORTH GRAIN TERMINAL

DRAWN	S.G.L.	DATE	13 - 9 - 95	DRAWING NUMBER (10737)
CHECKED	E.E.P.			
SCALES 			DTX 36111/	