

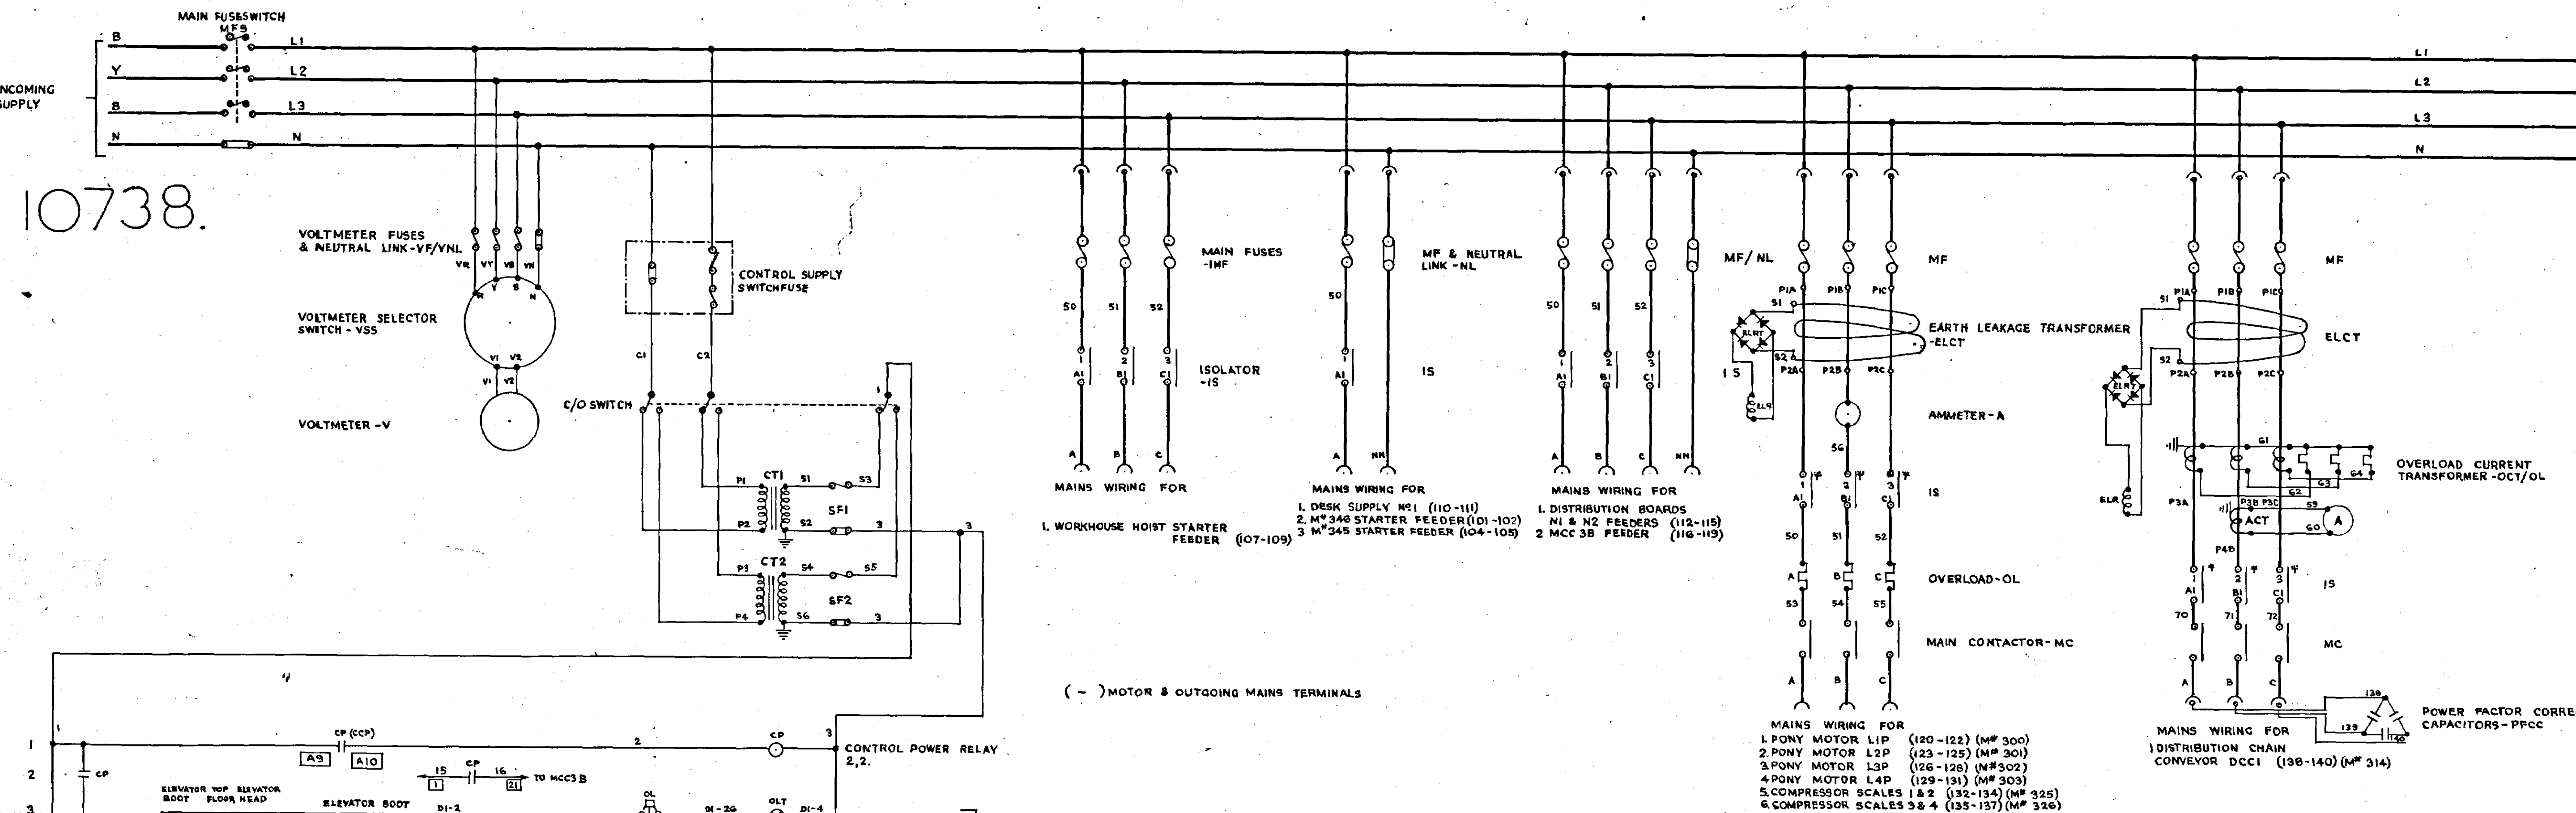


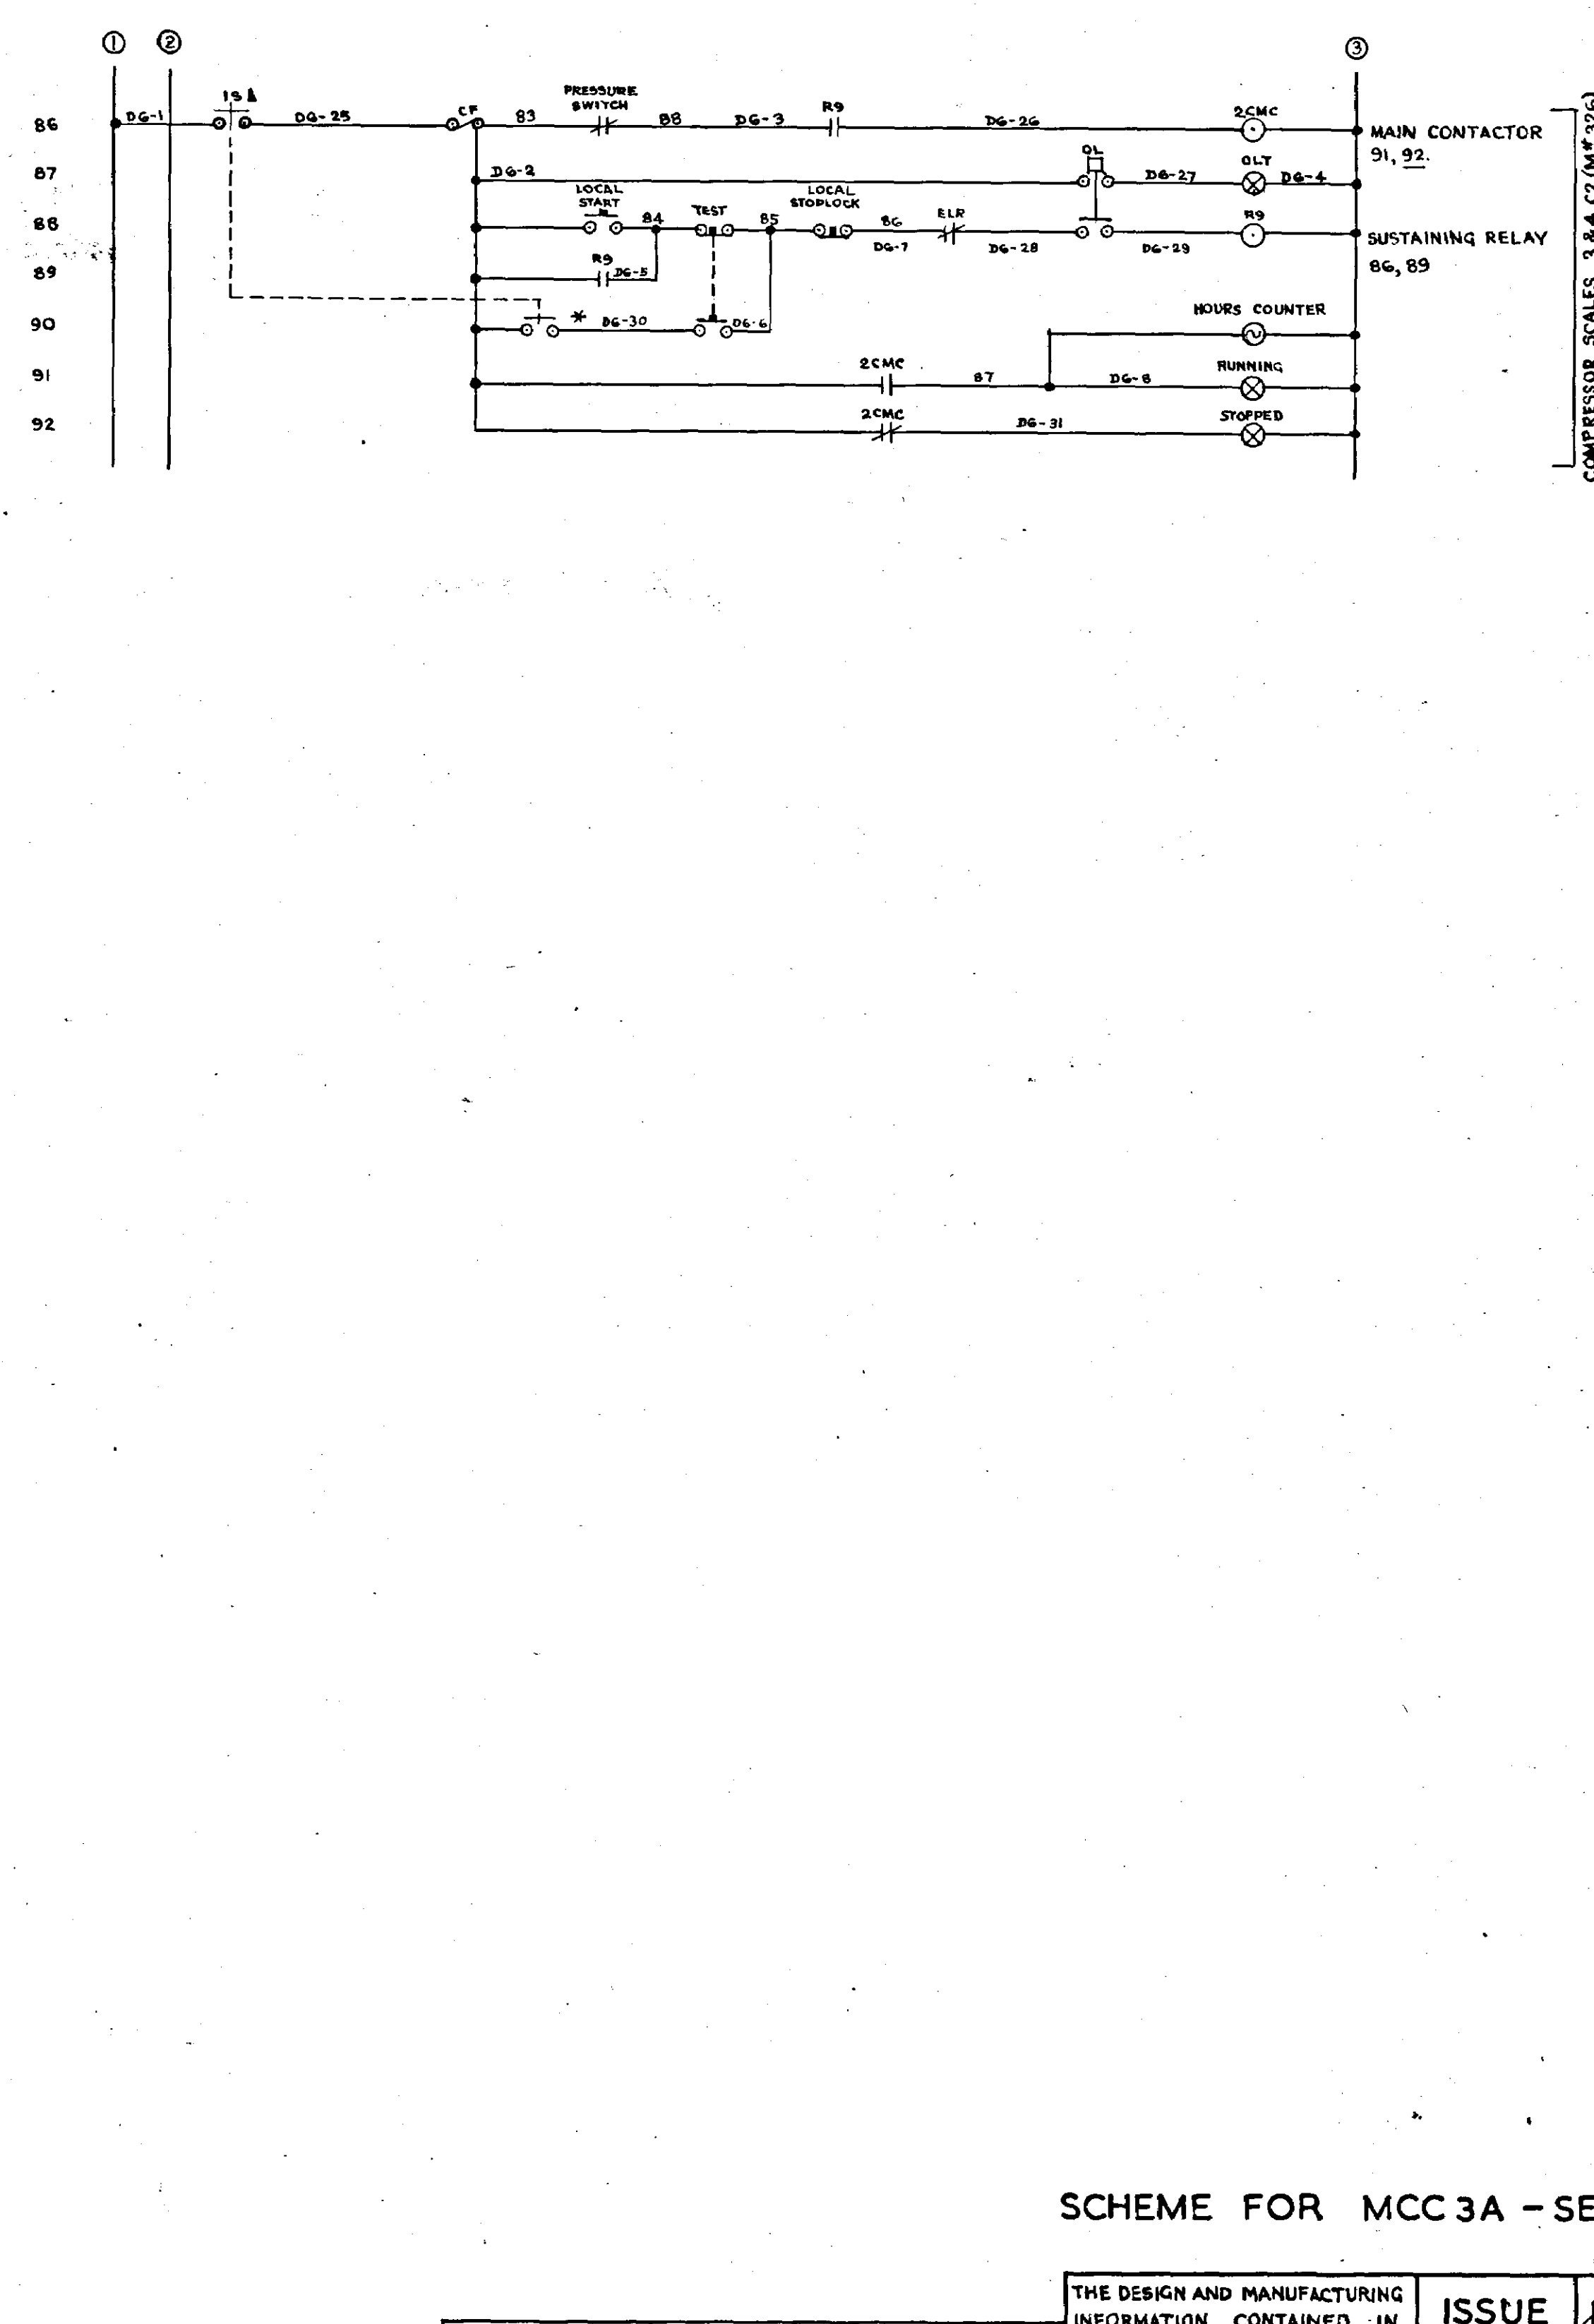

(-) MOTOR & OUTGOING MAINS TERMINALS

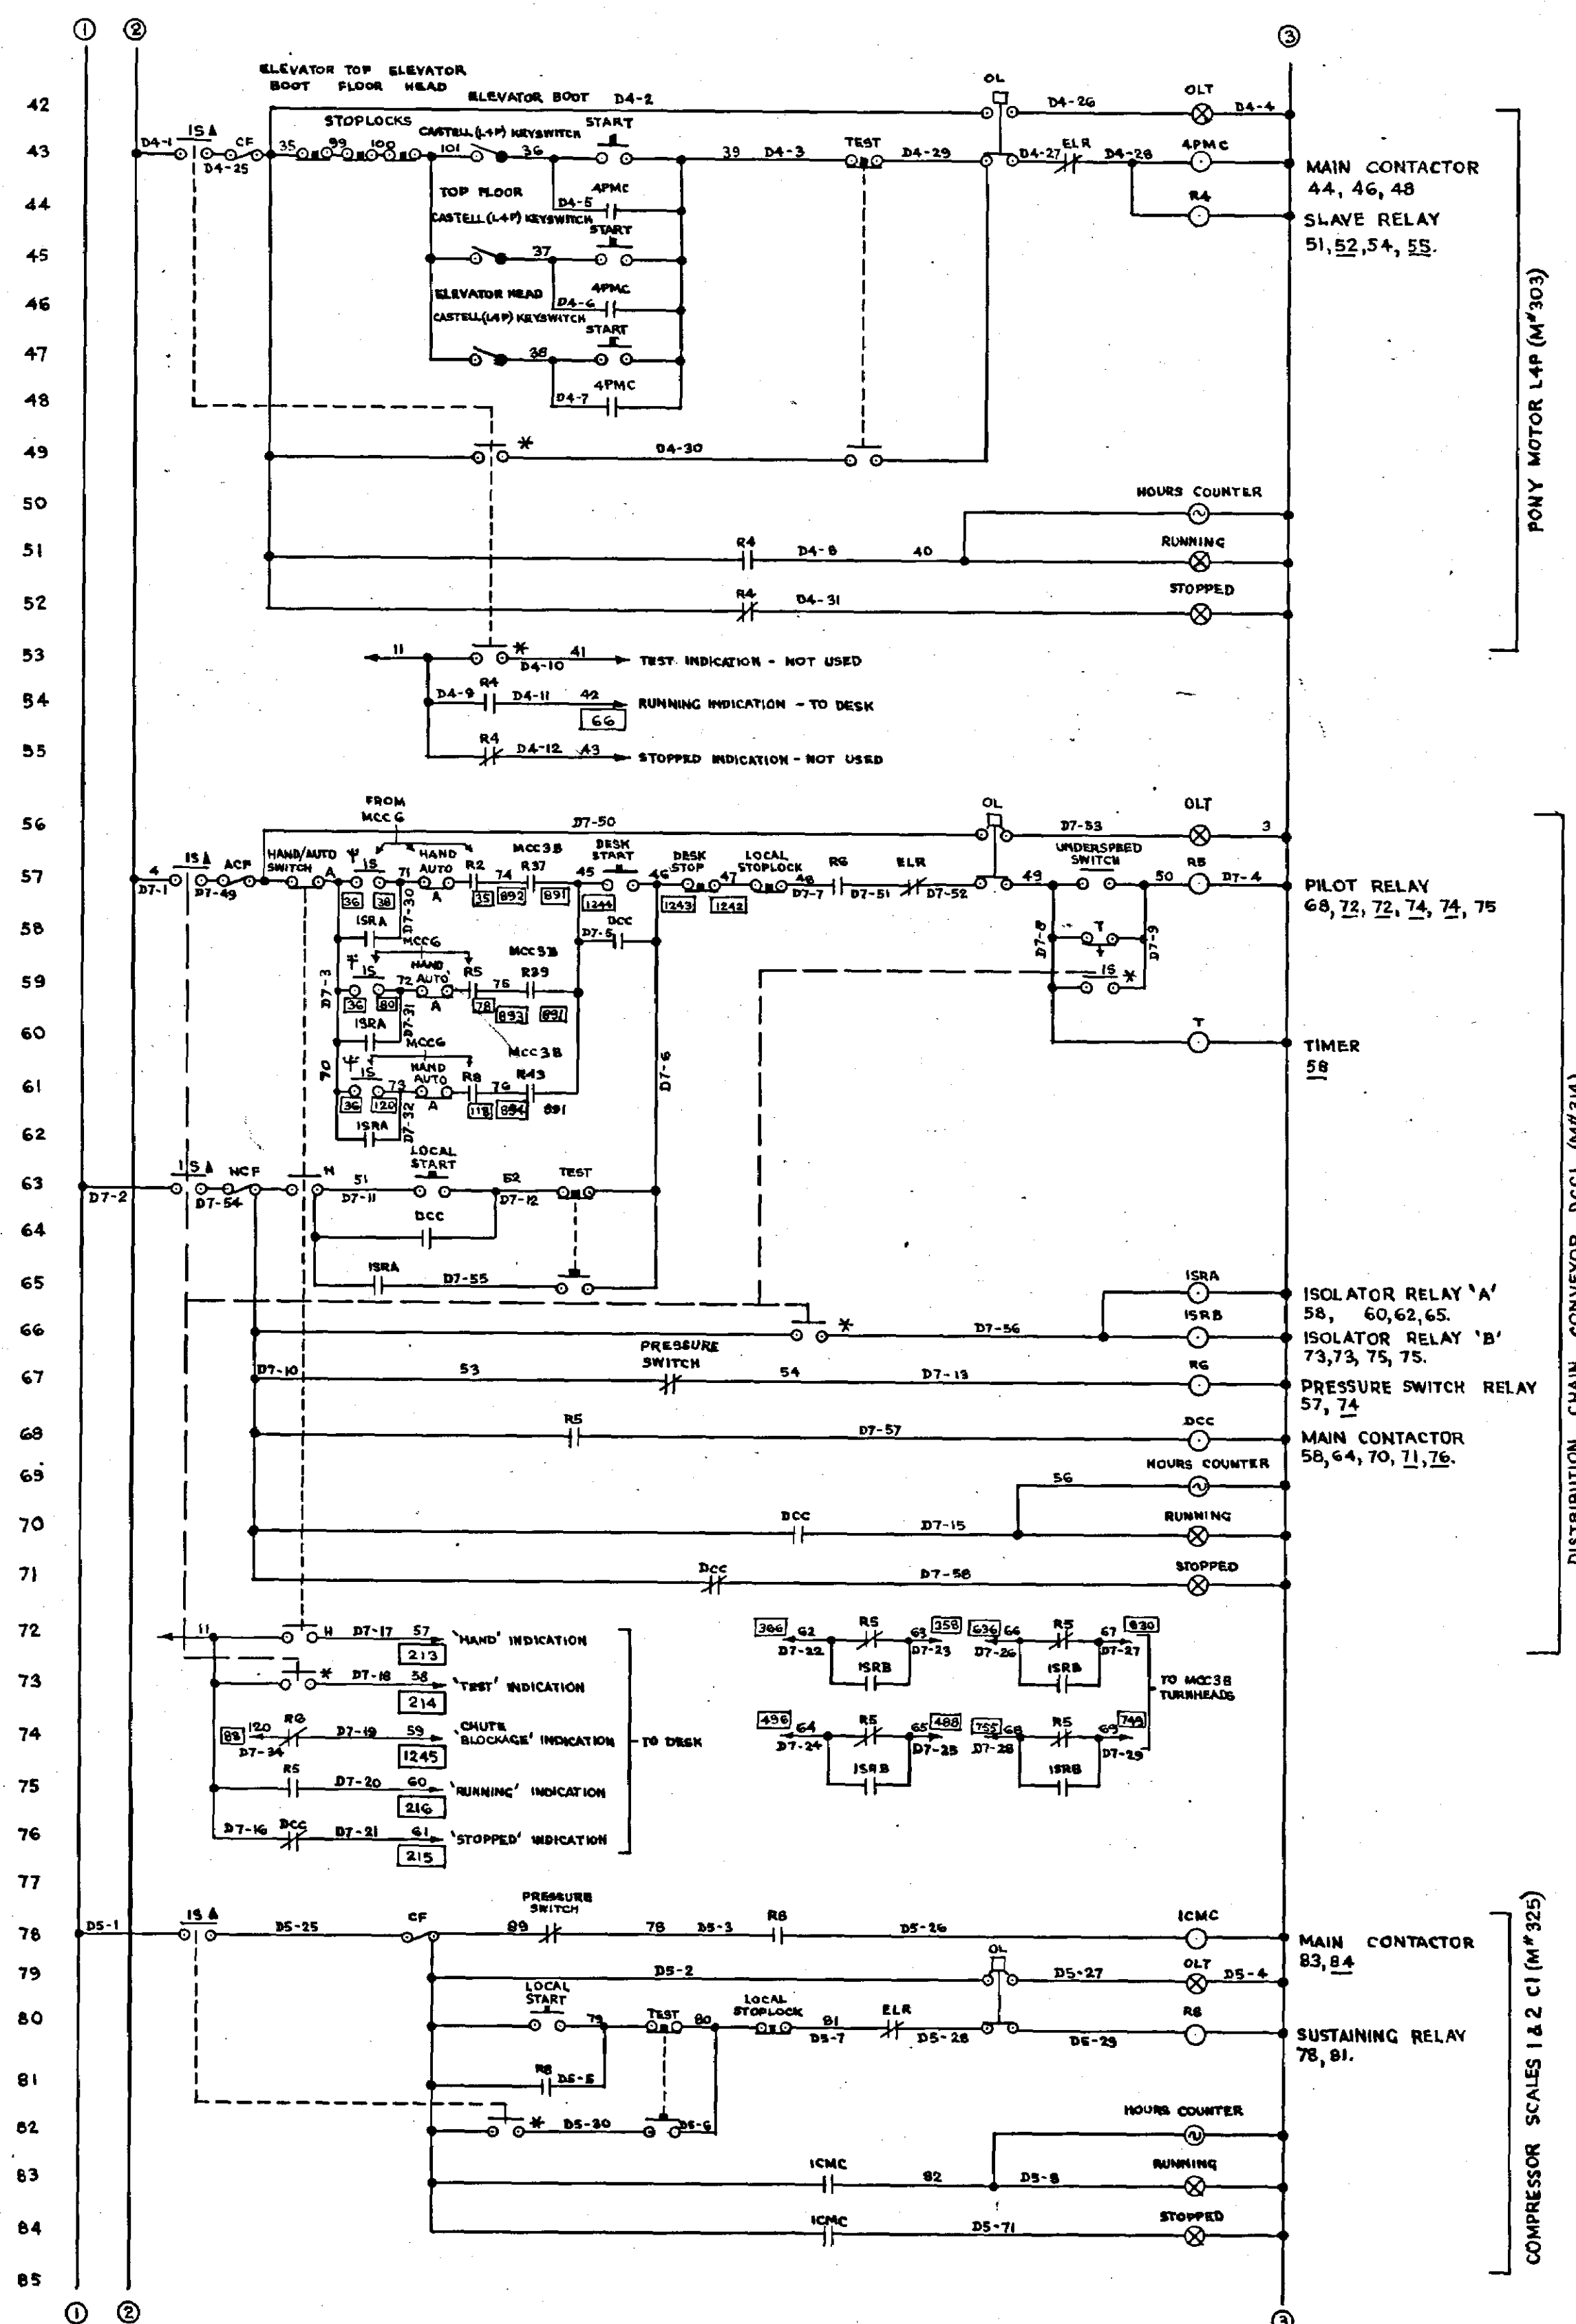

10738

SCHEME FOR MCC 3A - SEAFORTH GRAIN
TERMINAL

ISSUE	1	2	3	4	5	6	7	8	9	10
-------	---	---	---	---	---	---	---	---	---	----

DTX 361V

DTX 361V

DEWHURST & PARTNER LTD.
MELBOURNE WORKS. HOUNSLOW,

SCHEME FOR MCC3A - SEAFORTH GRAIN TERMINAL

REVISION: 6
TERMINALS ON
MCC 3 B MODIFIED.
ORIGIN: EISP

REVISION: 5
PONY MOTOR, STO
MODIFIED.
ORIGIN: CUST.

LOCKS	REVISION: 4 M345 STARTER FE WAS M347 START FEEDER, MODS, T DCCI. ORIGIN: CUST.
-------	---

DER	REVISION: 3
R	MCCG INTERLOCK
-	REVISED AND
	DESIGNATIONS AD
	MCC2C DESIGNATIONS A
	ORIGIN: EISR

REVISION: 2
ISOLATOR NOTES
ADDED.

REVISION: 1
MOTOR NRS ADDED
TO MAINS
ORIGIN: CUST

DRAWN BY J.F.
DATE 20.11.1970
CHECKED BY
APPROVED BY

THE DESIGN AND MANUFACTURING INFORMATION CONTAINED IN THIS DRAWING IS THE EXCLUSIVE RIGHT OF DEWHURST & PARTNER LTD. AND MUST NOT BE COPIED OR USED FOR MANUFACTURING PURPOSES

KEY DIAG. No.	— — — —
EXT. DIAG. No.	
REL. DIAG. No.	
PANEL LAYOUT No.	GTX 361V