
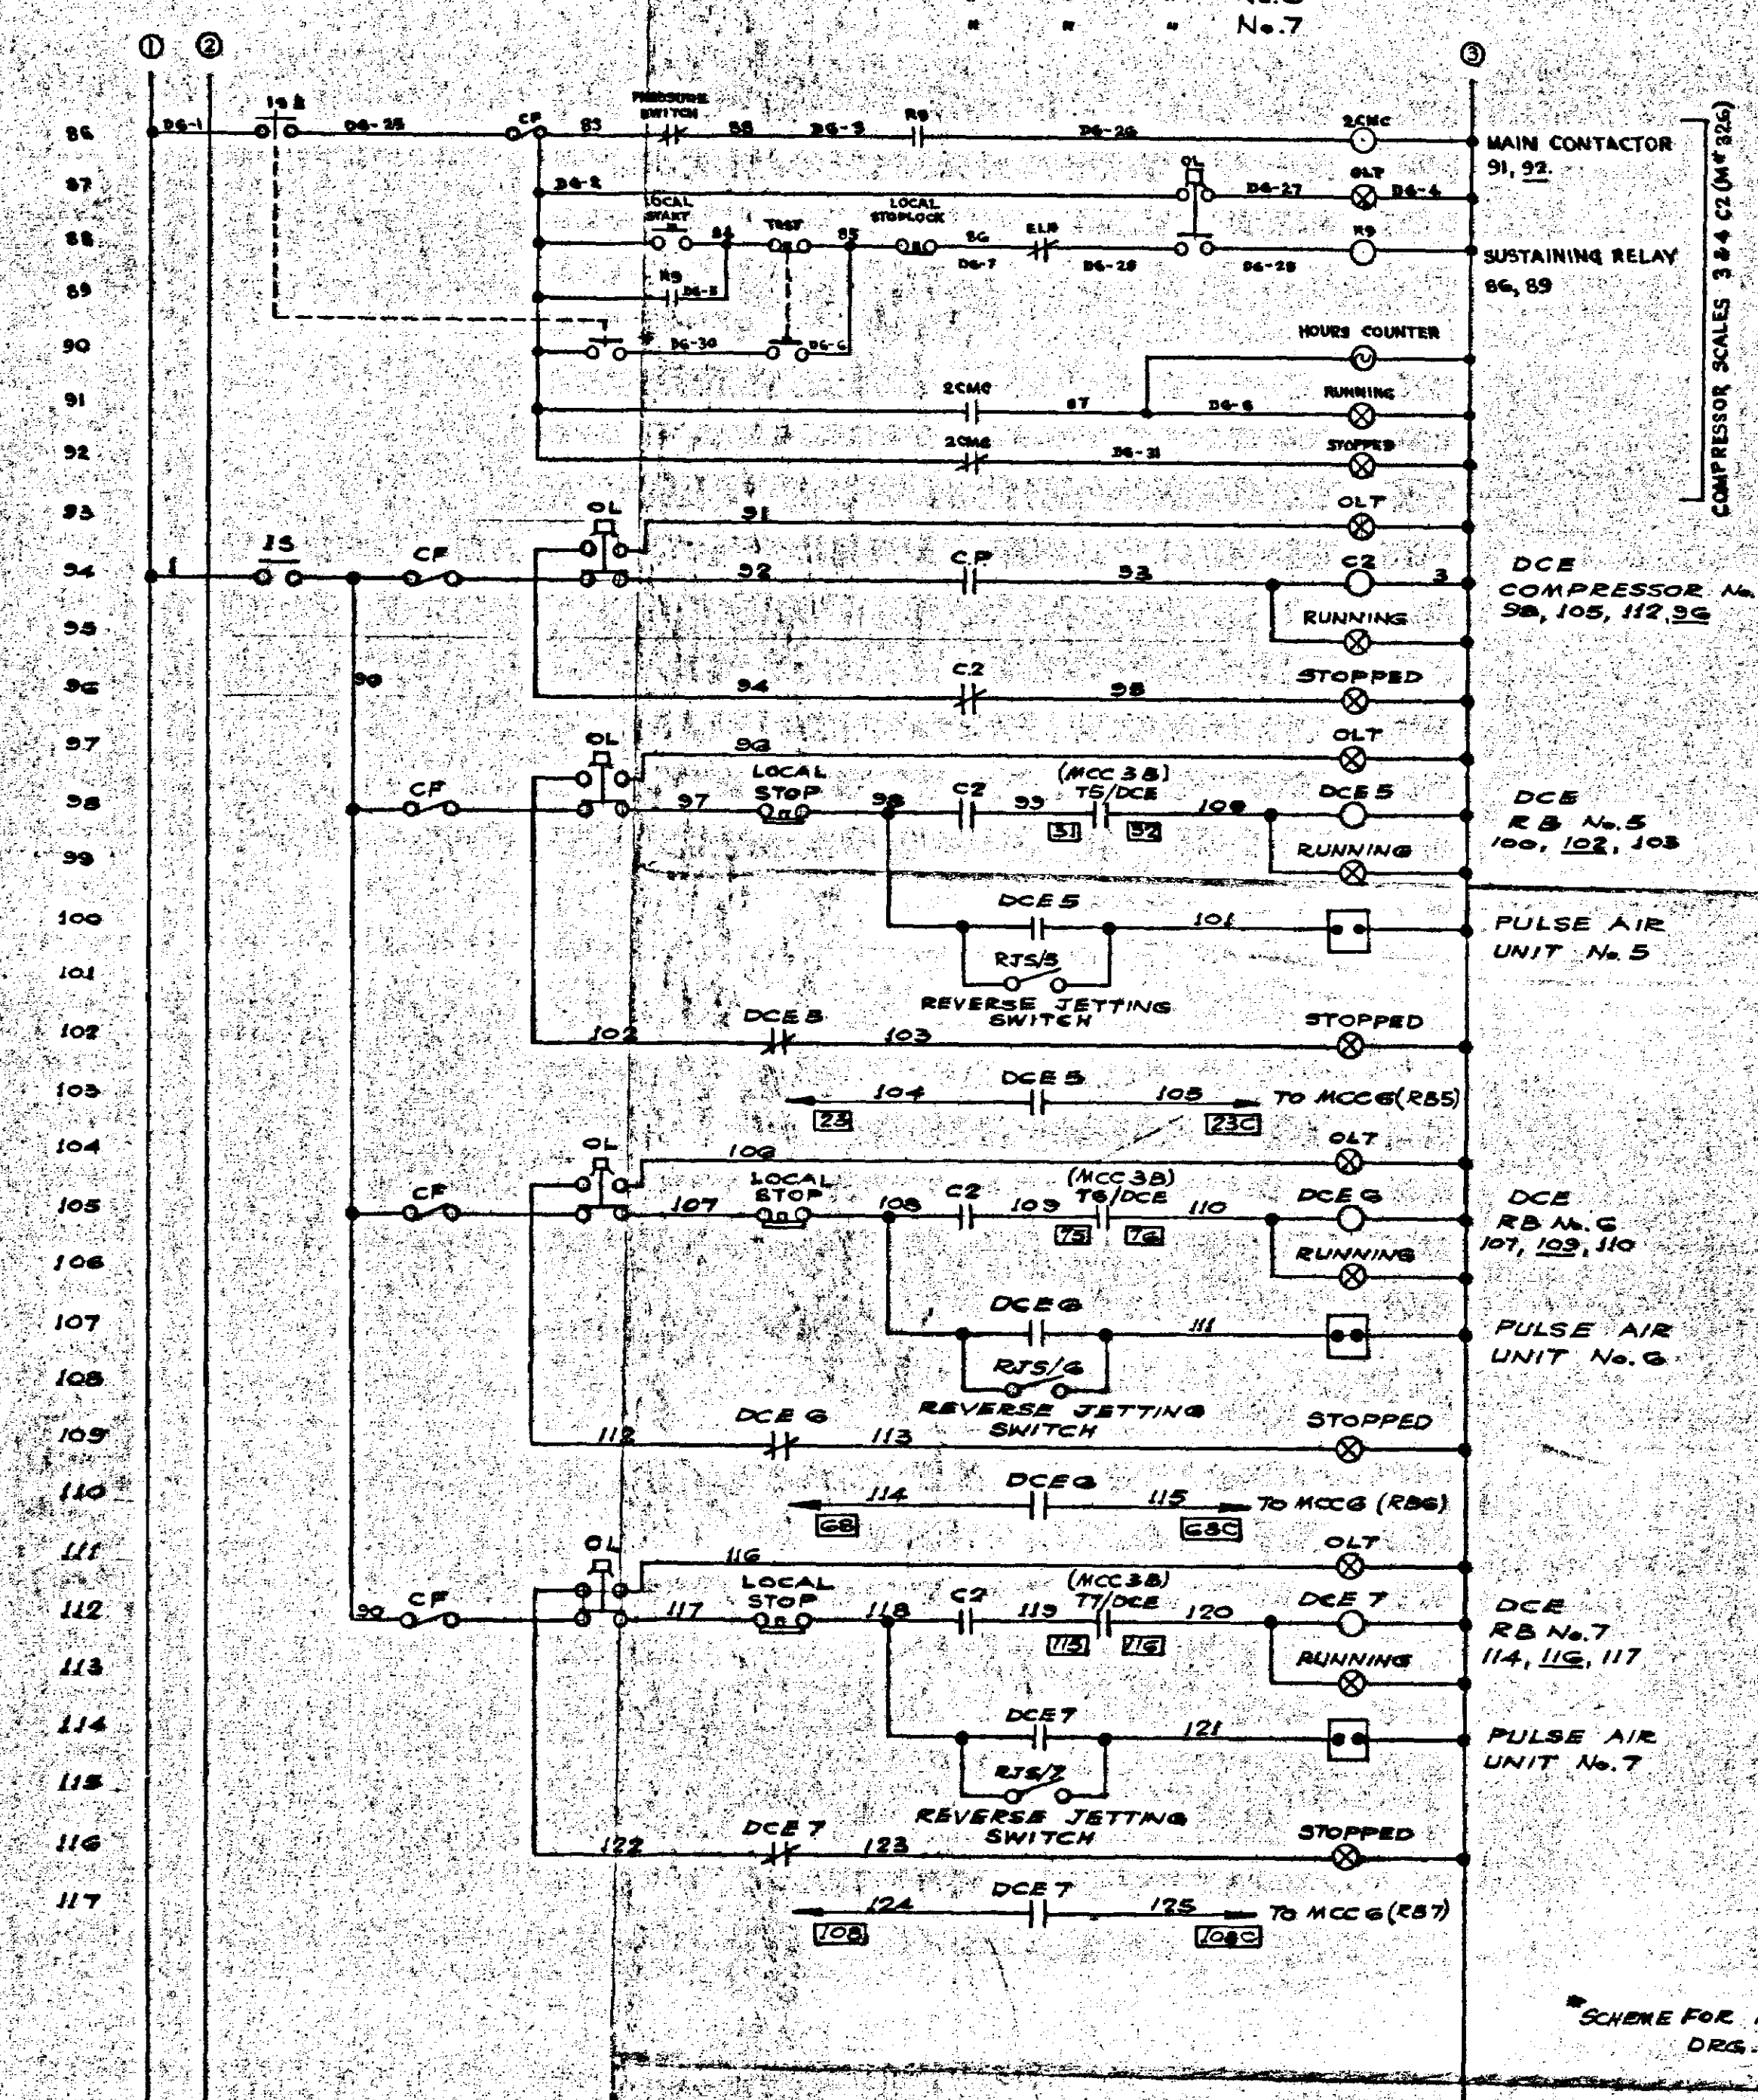
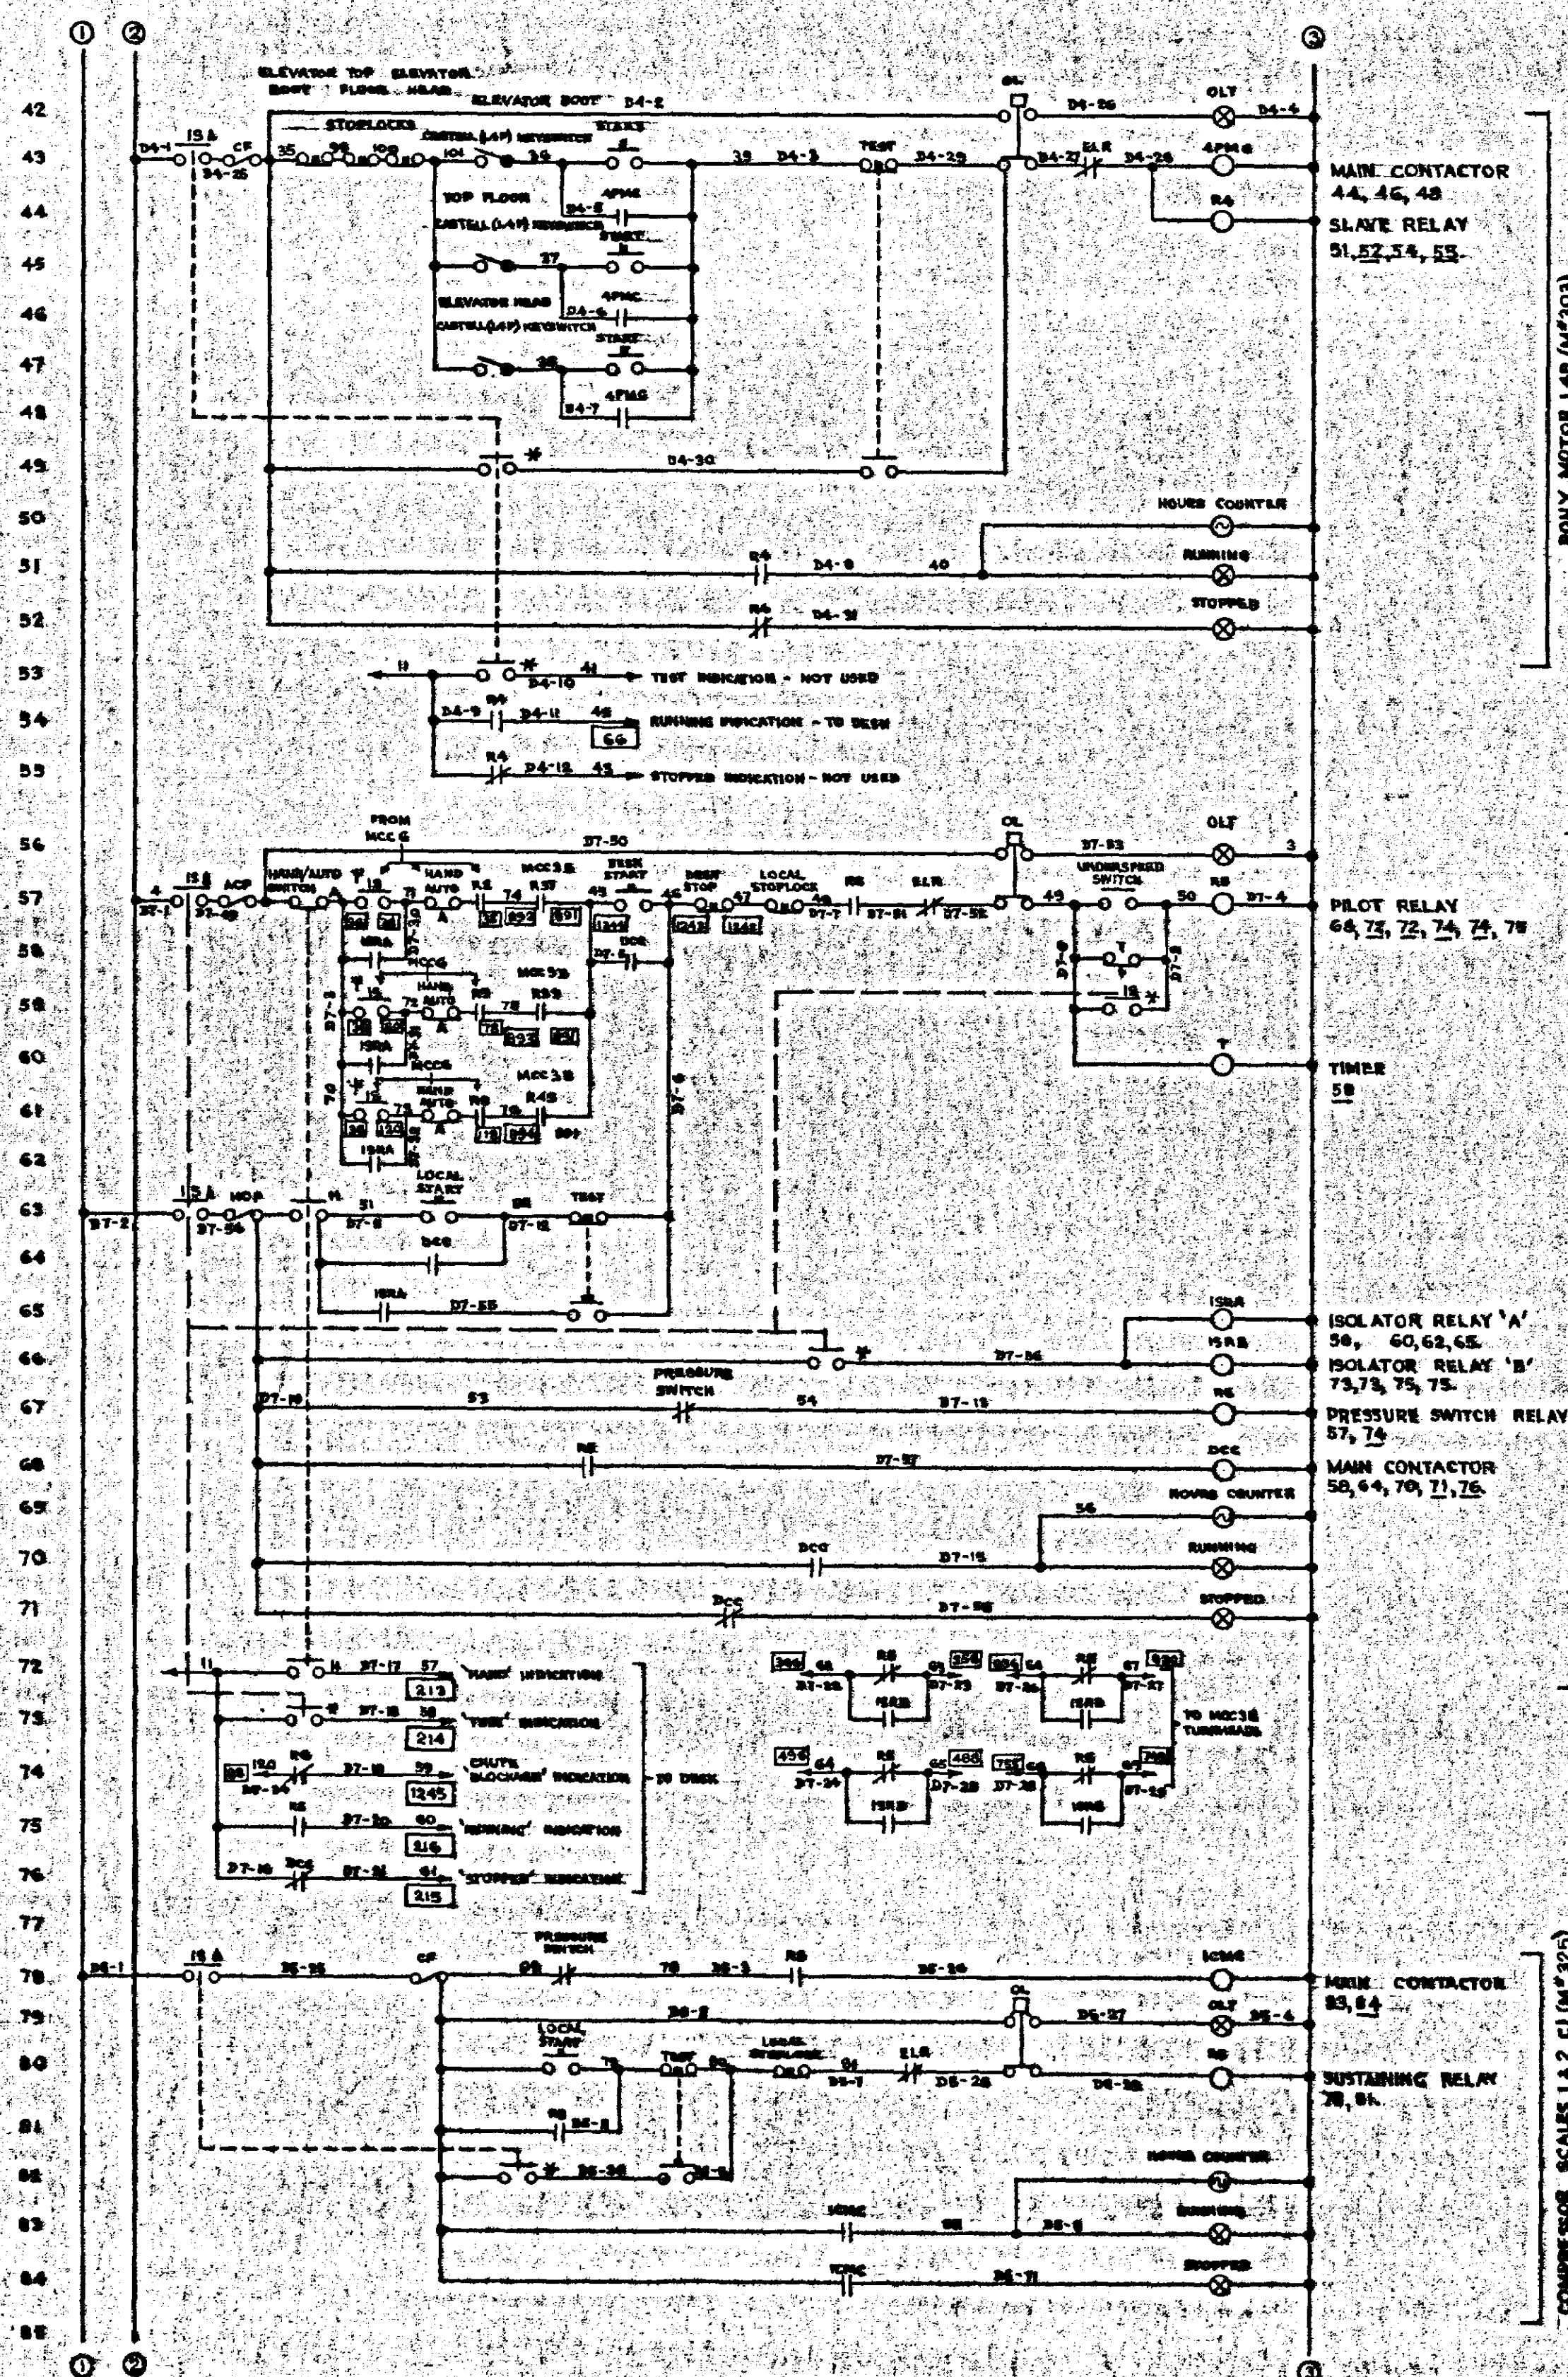
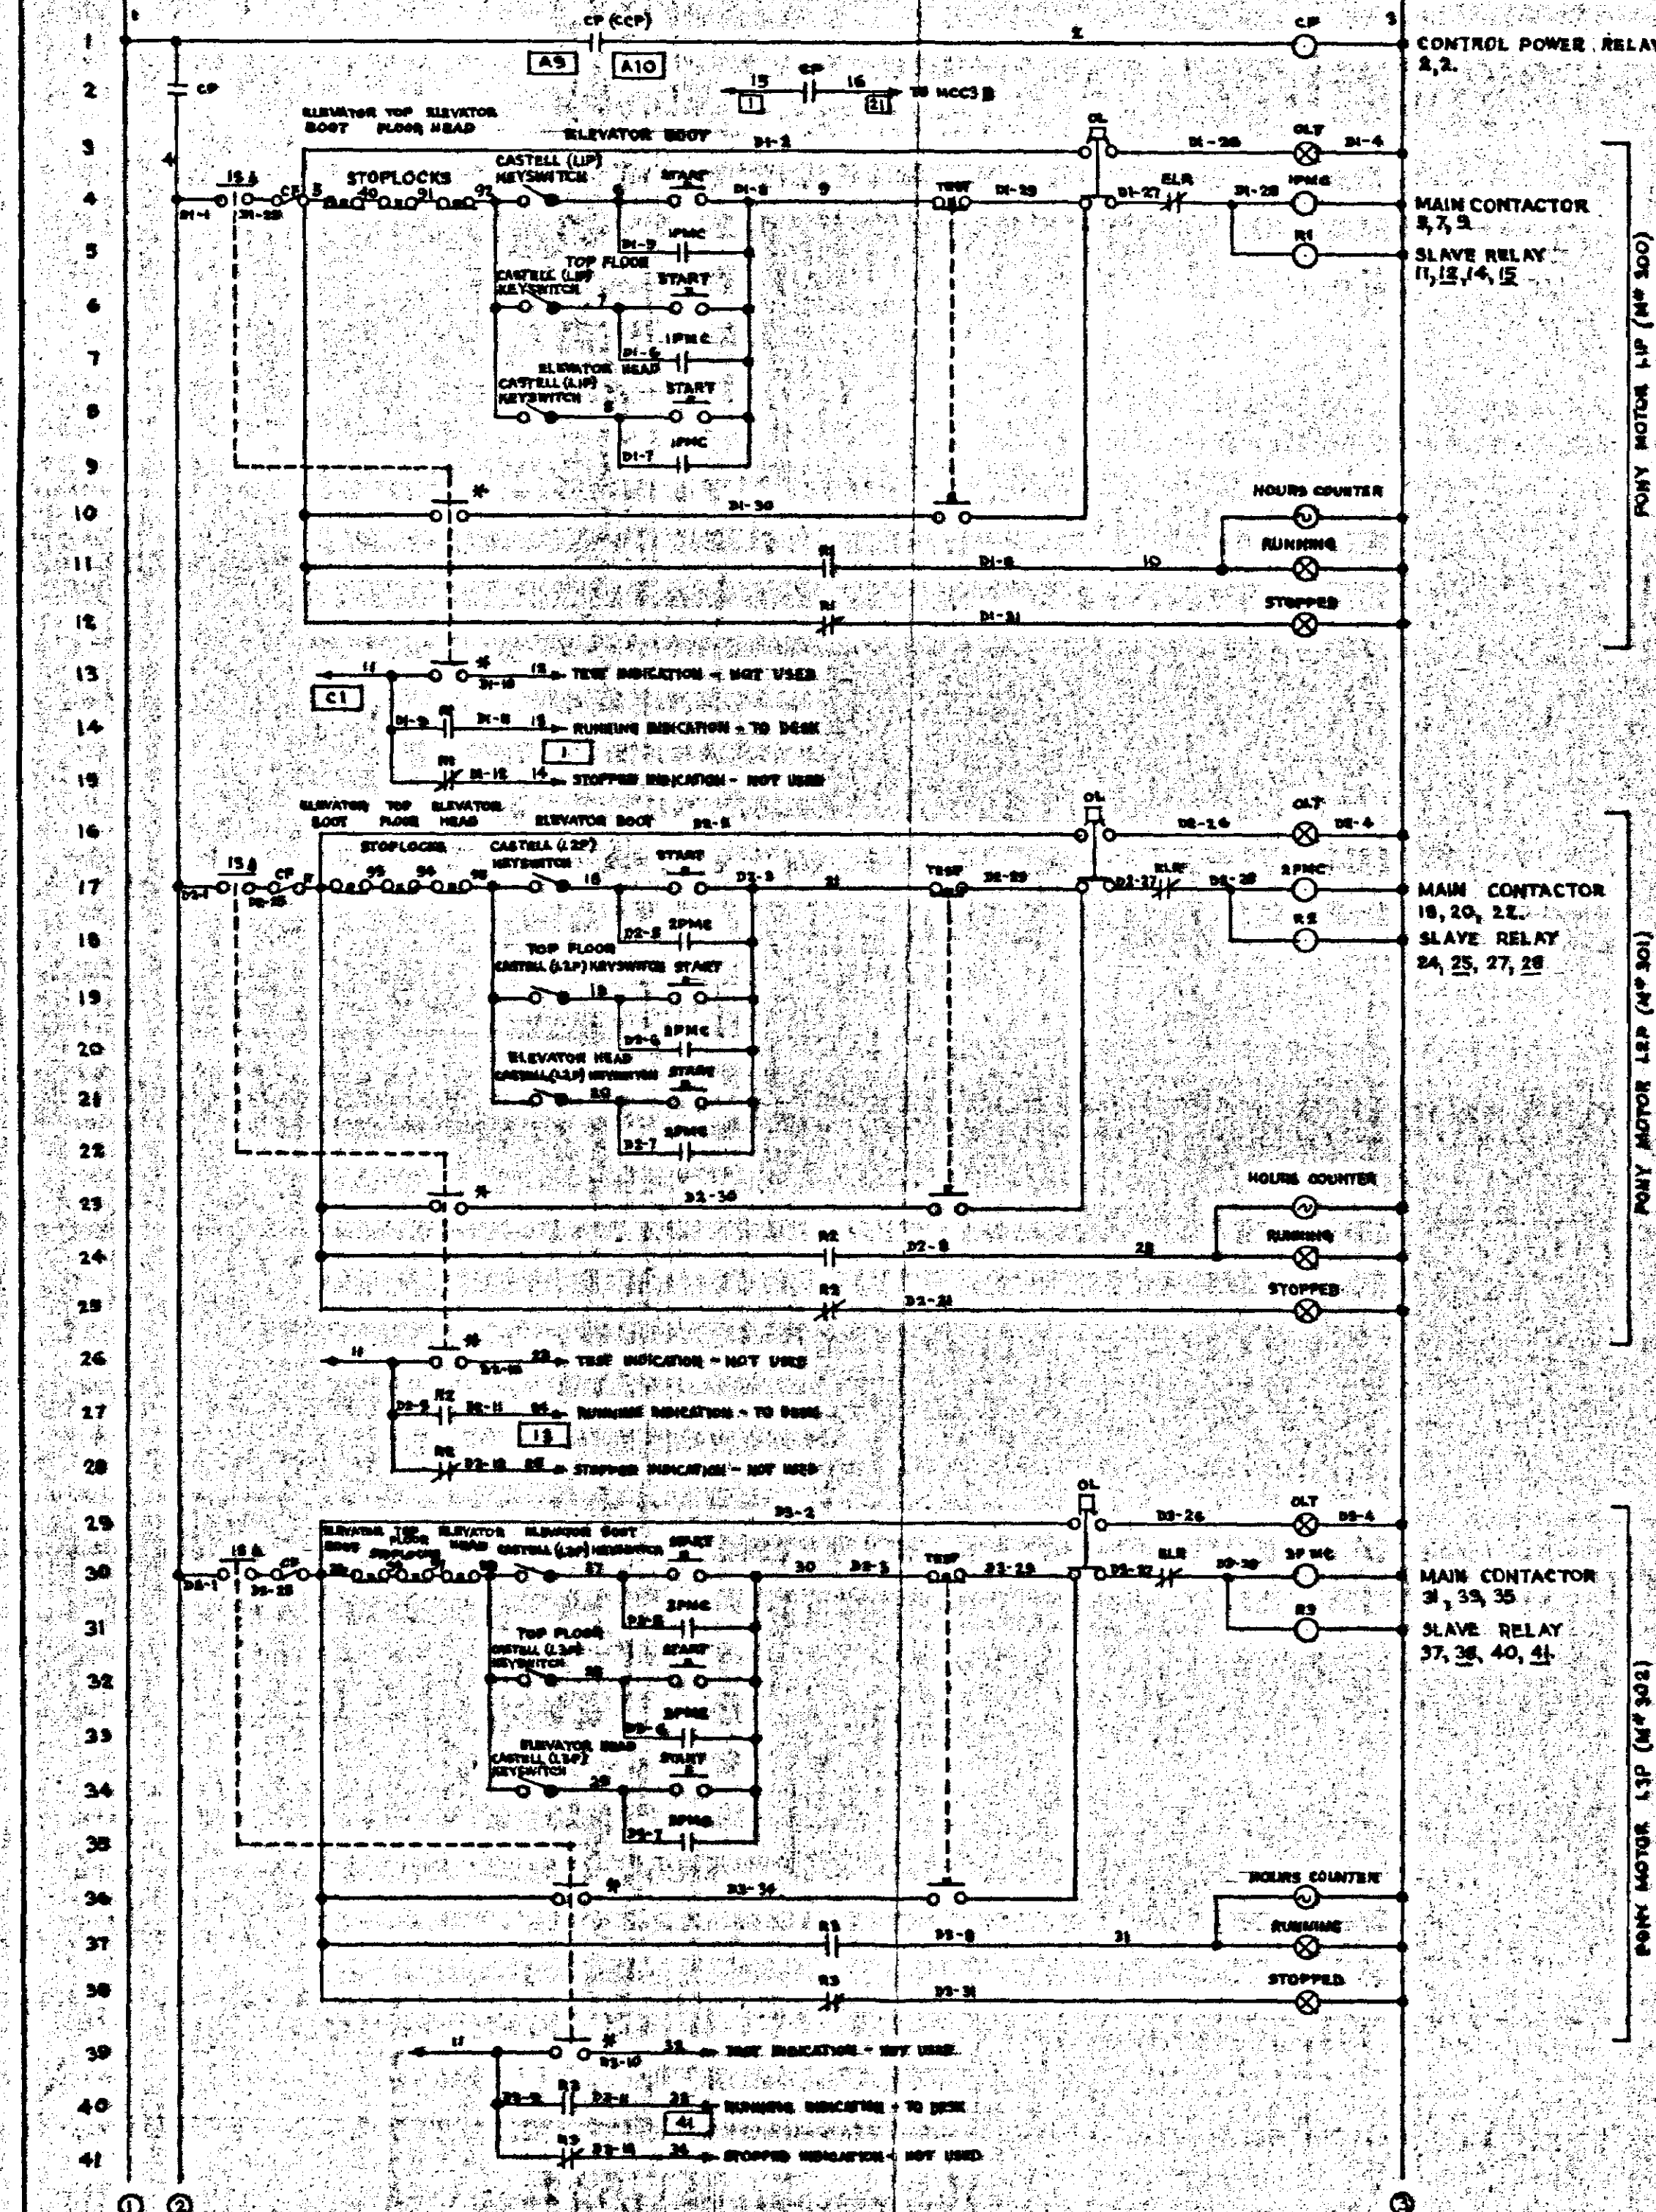


10738

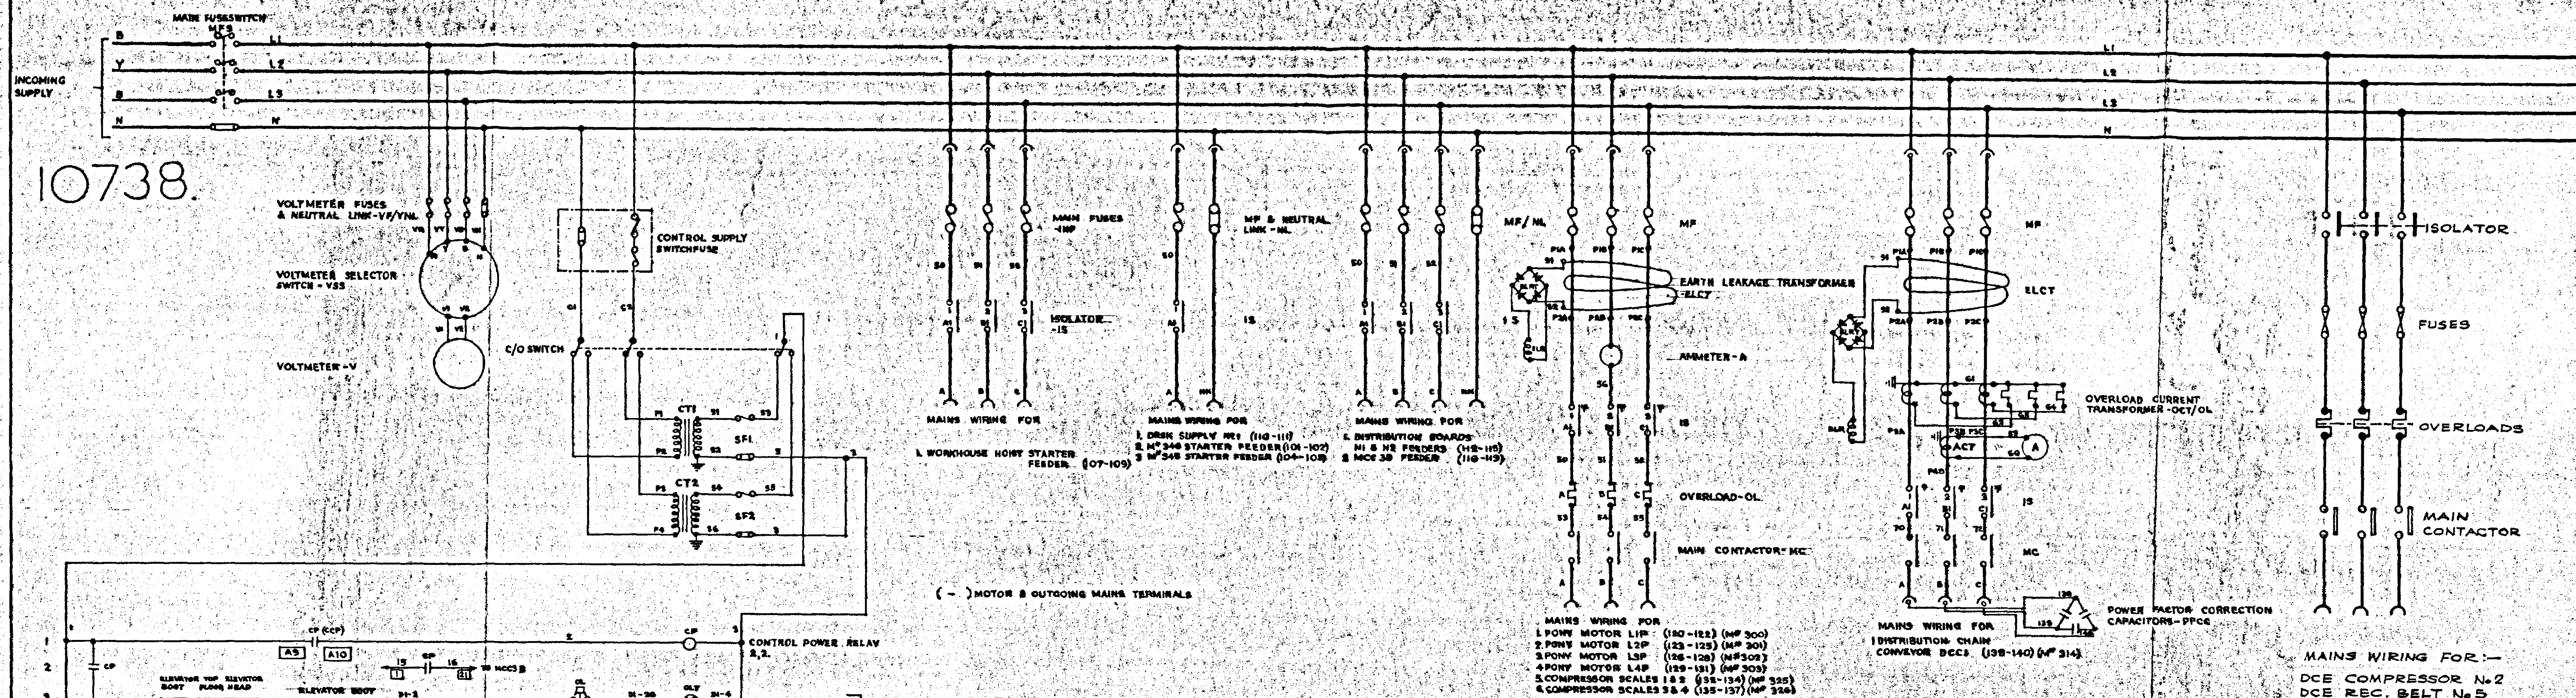

10738

**SCHEME FOR MCC 3A - SEAFORTH GRAIN
TERMINAL**

DTX 361V

DTX 361V

DEWHURST & PARTNER LTD.
MELBOURNE WORKS. HOUNSLOW.

SCHEME FOR MCC3A - SEAFORTH GRAIN TERMINAL

REVISION: 10 REASON: 10 PLANTS NO. 5, 6, 7, 8, 9 COMPRESSOR END OF RECEIVING END OF RECEIVING BELTS NO. 5, 6, 7 NO. 5, 6, 7, 8, 9	REVISION 9 REASON: 9 PLANTS NO. 5, 6, 7, 8, 9 COMPRESSOR END OF RECEIVING END OF RECEIVING BELTS NO. 5, 6, 7 NO. 5, 6, 7, 8, 9	REVISION 8 REASON: 8 PLANTS NO. 5, 6, 7, 8, 9 COMPRESSOR END OF RECEIVING END OF RECEIVING BELTS NO. 5, 6, 7 NO. 5, 6, 7, 8, 9	REVISION 7 REASON: 7 PLANTS NO. 5, 6, 7, 8, 9 COMPRESSOR END OF RECEIVING END OF RECEIVING BELTS NO. 5, 6, 7 NO. 5, 6, 7, 8, 9	INFORMATION CONTAINED IN THIS DRAWING IS THE EXCLUSIVE RIGHT OF DEWHURST & PARTNER LTD. AND MUST NOT BE COPIED OR USED FOR MANUFACTURING PURPOSES
---	--	--	--	--

ISSUE	1	2	3	4	5	6	7	8	9	10	11
-------	---	---	---	---	---	---	---	---	---	----	----

THE DESIGN AND MANUFACTURING
INFORMATION CONTAINED IN
THIS DRAWING IS THE EXCLUSIVE
RIGHT OF DEWHURST & PARTNER
LTD AND MUST NOT BE COPIED
OR USED FOR MANUFACTURING
PURPOSES