

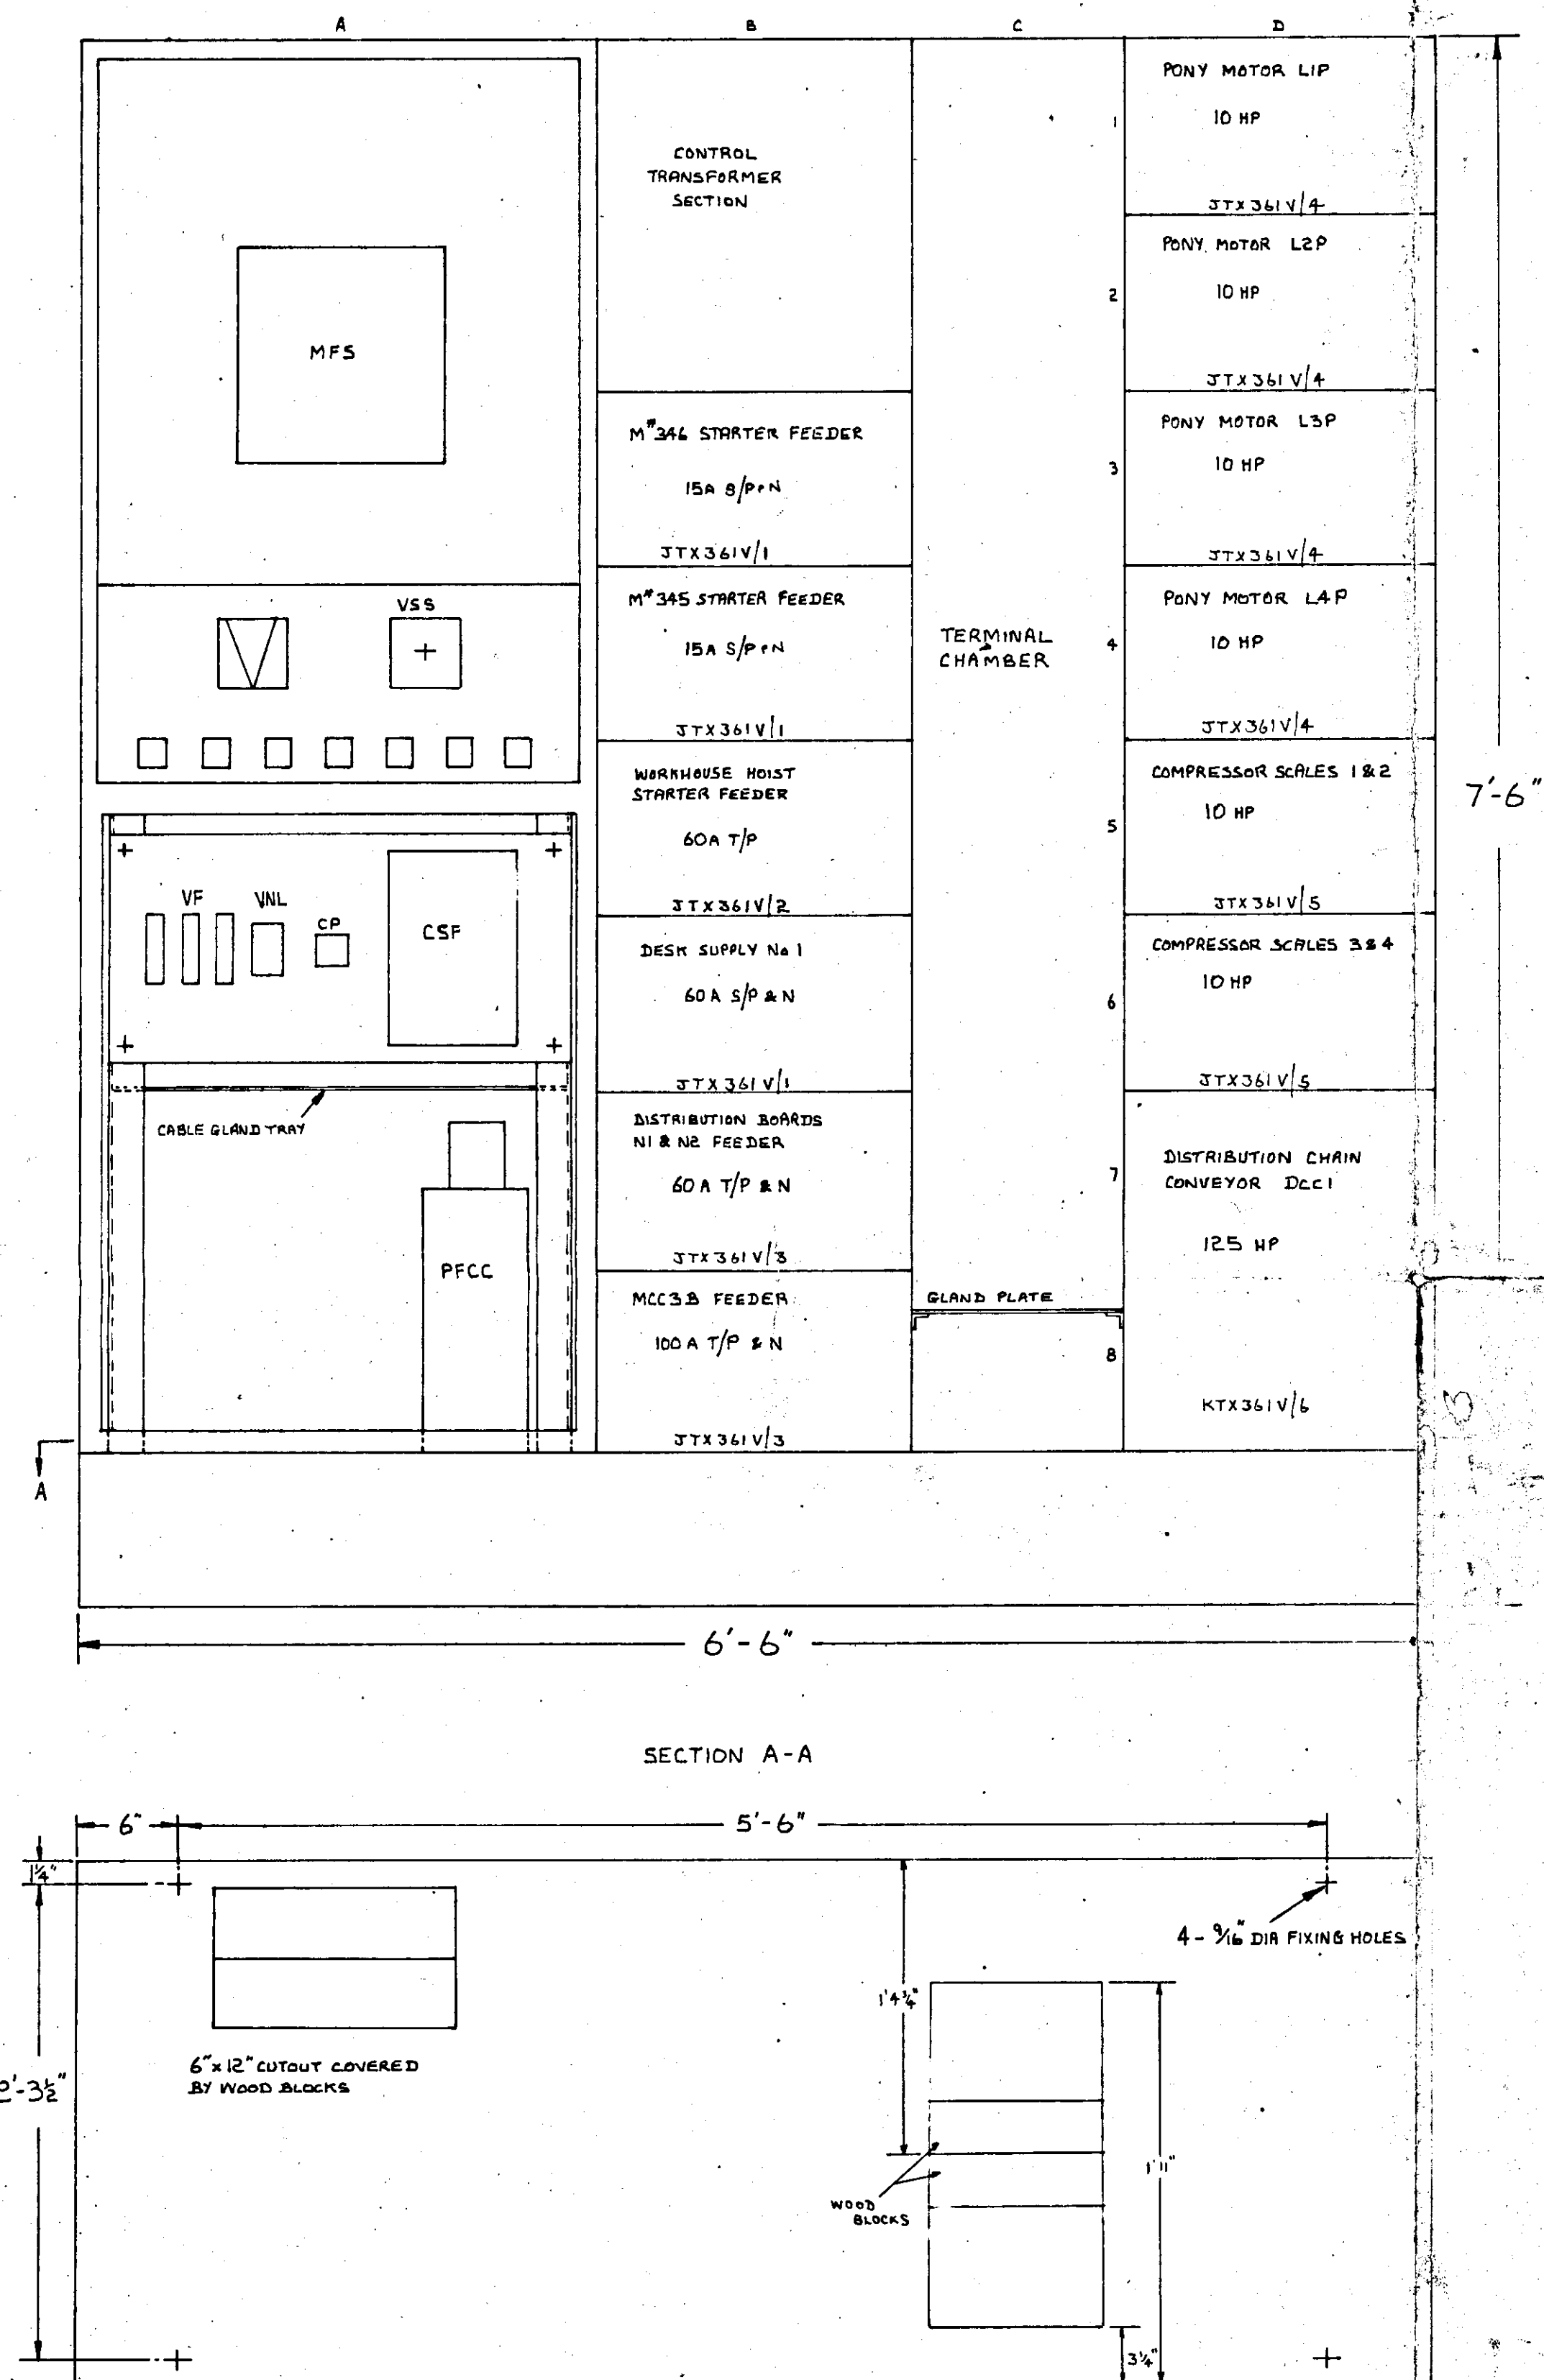


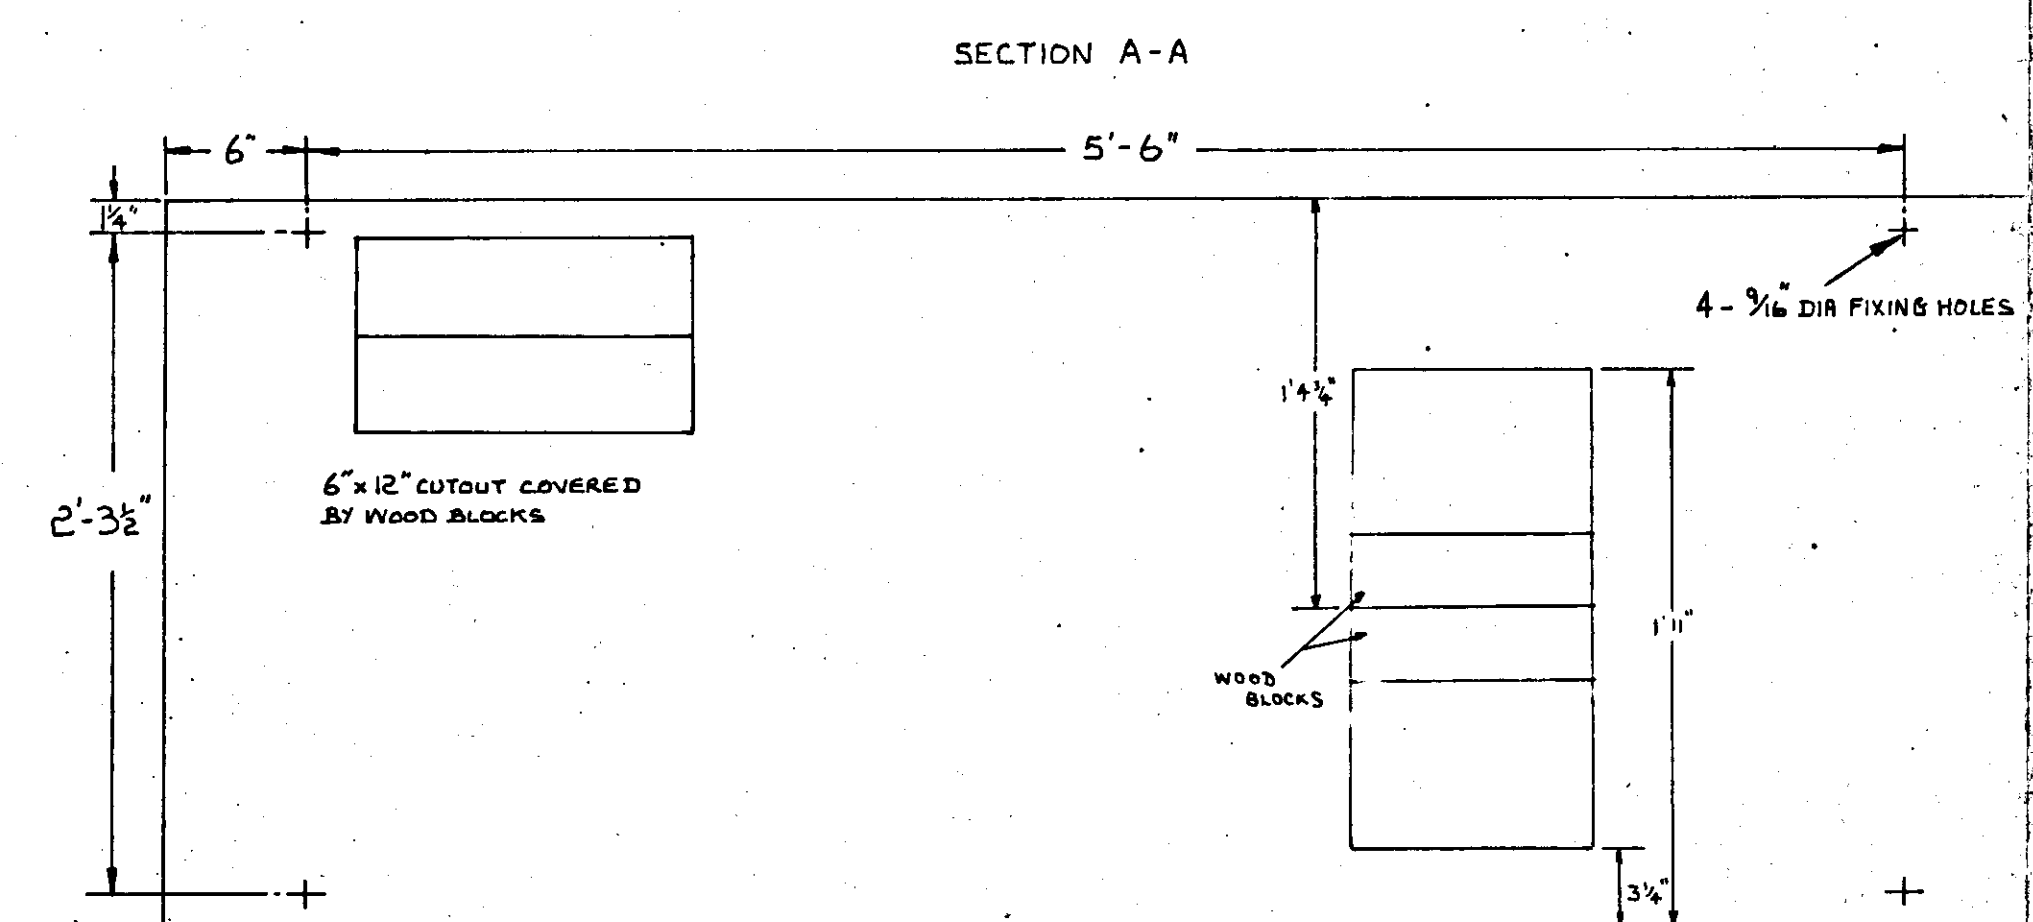

7'-6"

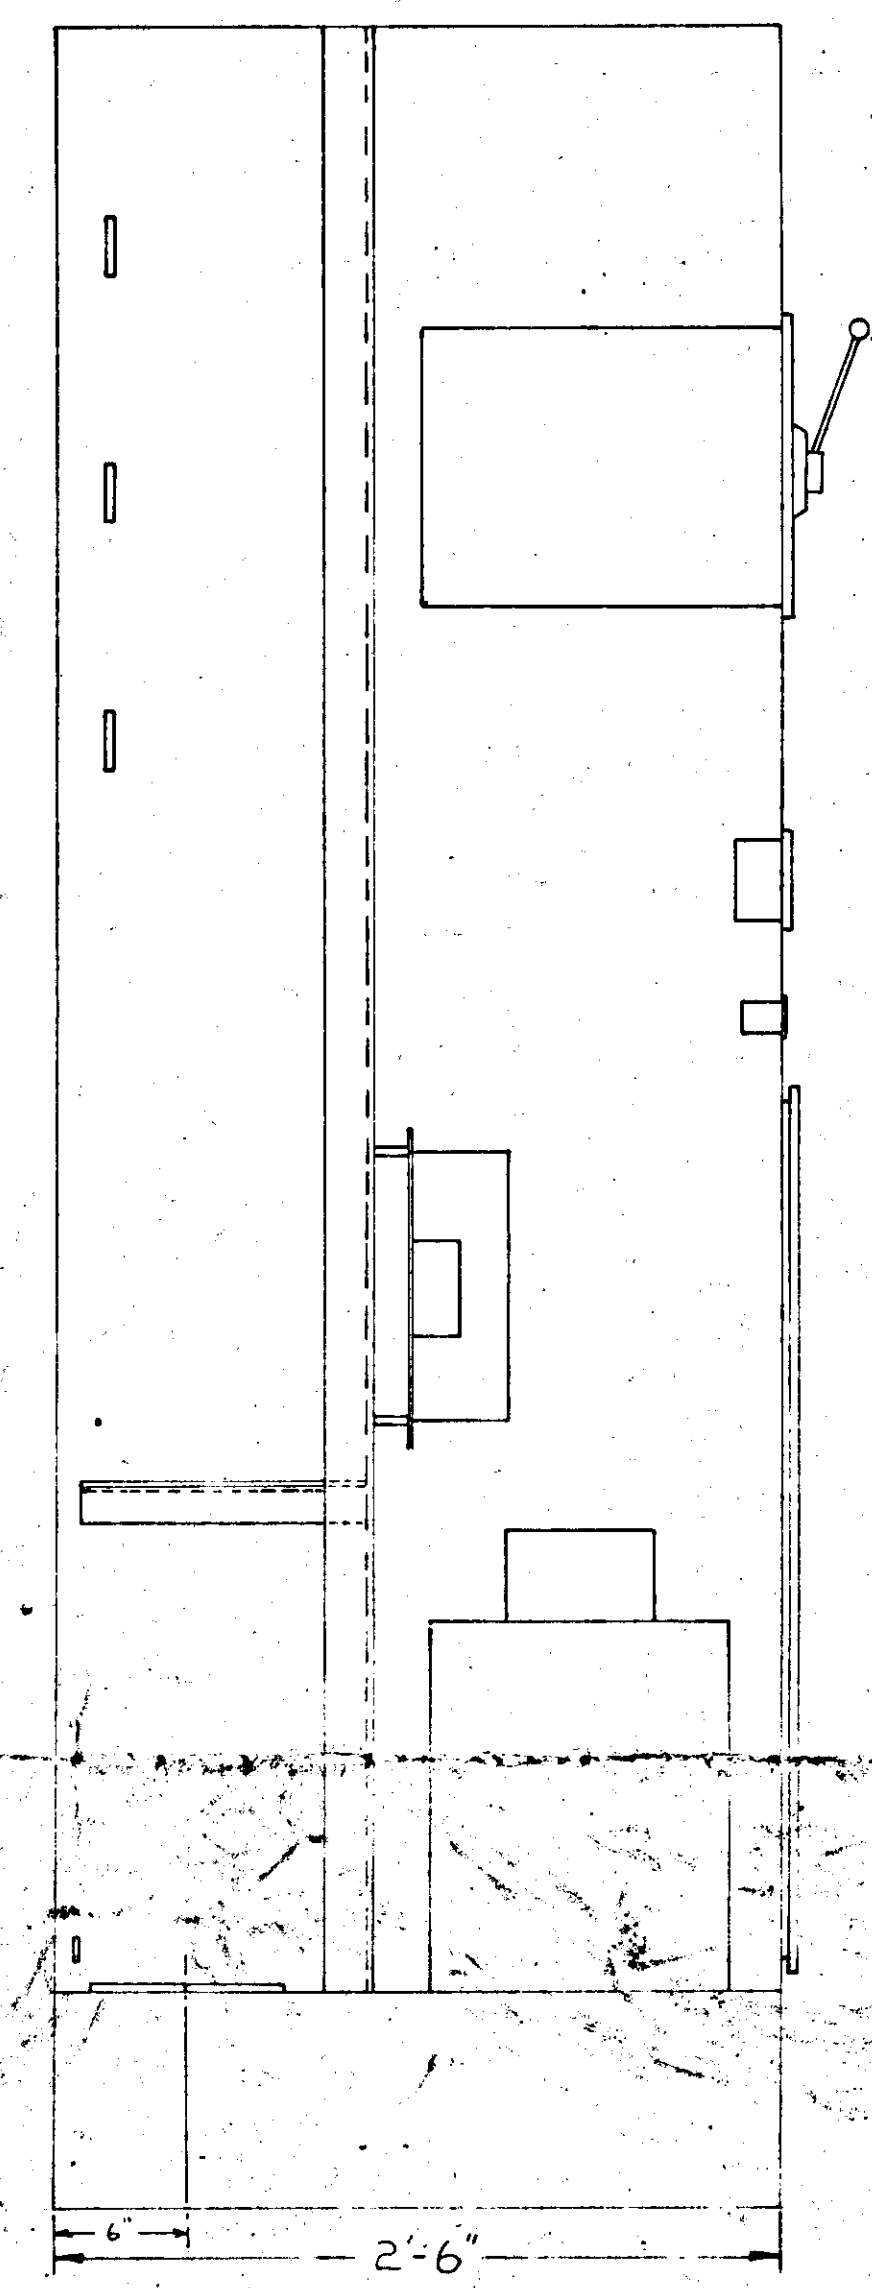

LAYOUT OF MCC3A - SEAFORTH GRAIN TERMINAL

DEWHURST & PARTNER LTD.
MELBOURNE WORKS HOUNSLOW

TITLE: LAYOUT OF MCC3A - SEAFORTH GRAIN TERMINAL

REVISION: 3 MODULE B4 WAS "M247 STARTER FEEDER"	REVISION: 2 TERMINAL CHAMBER CUT OUT MODIFIED.	REVISION: 1 MODULES B2 & B3 WERE 15A T/P 300. Now 400A.	DRAWN BY: <i>BJL</i> DATE: 22-10-70
ORIGIN: CUST 27/1/71 SG	ORIGIN: EISP 23/11/70 SGD	ORIGIN: EISP 19/12/70 SGD	CHECKED BY: APPROVED BY: DATE:

THE DESIGN AND MANUFACTURING INFORMATION CONTAINED IN THIS DRAWING IS THE EXCLUSIVE RIGHT OF DEWHURST & PARTNER LTD. AND MUST NOT BE COPIED OR USED FOR MANUFACTURING PURPOSES.	ISSUE: <i>1/2/3/4</i>
	GTX361V
	GTX361V
	21