



10709


## TRIPPER RELAY PANEL TRB 5

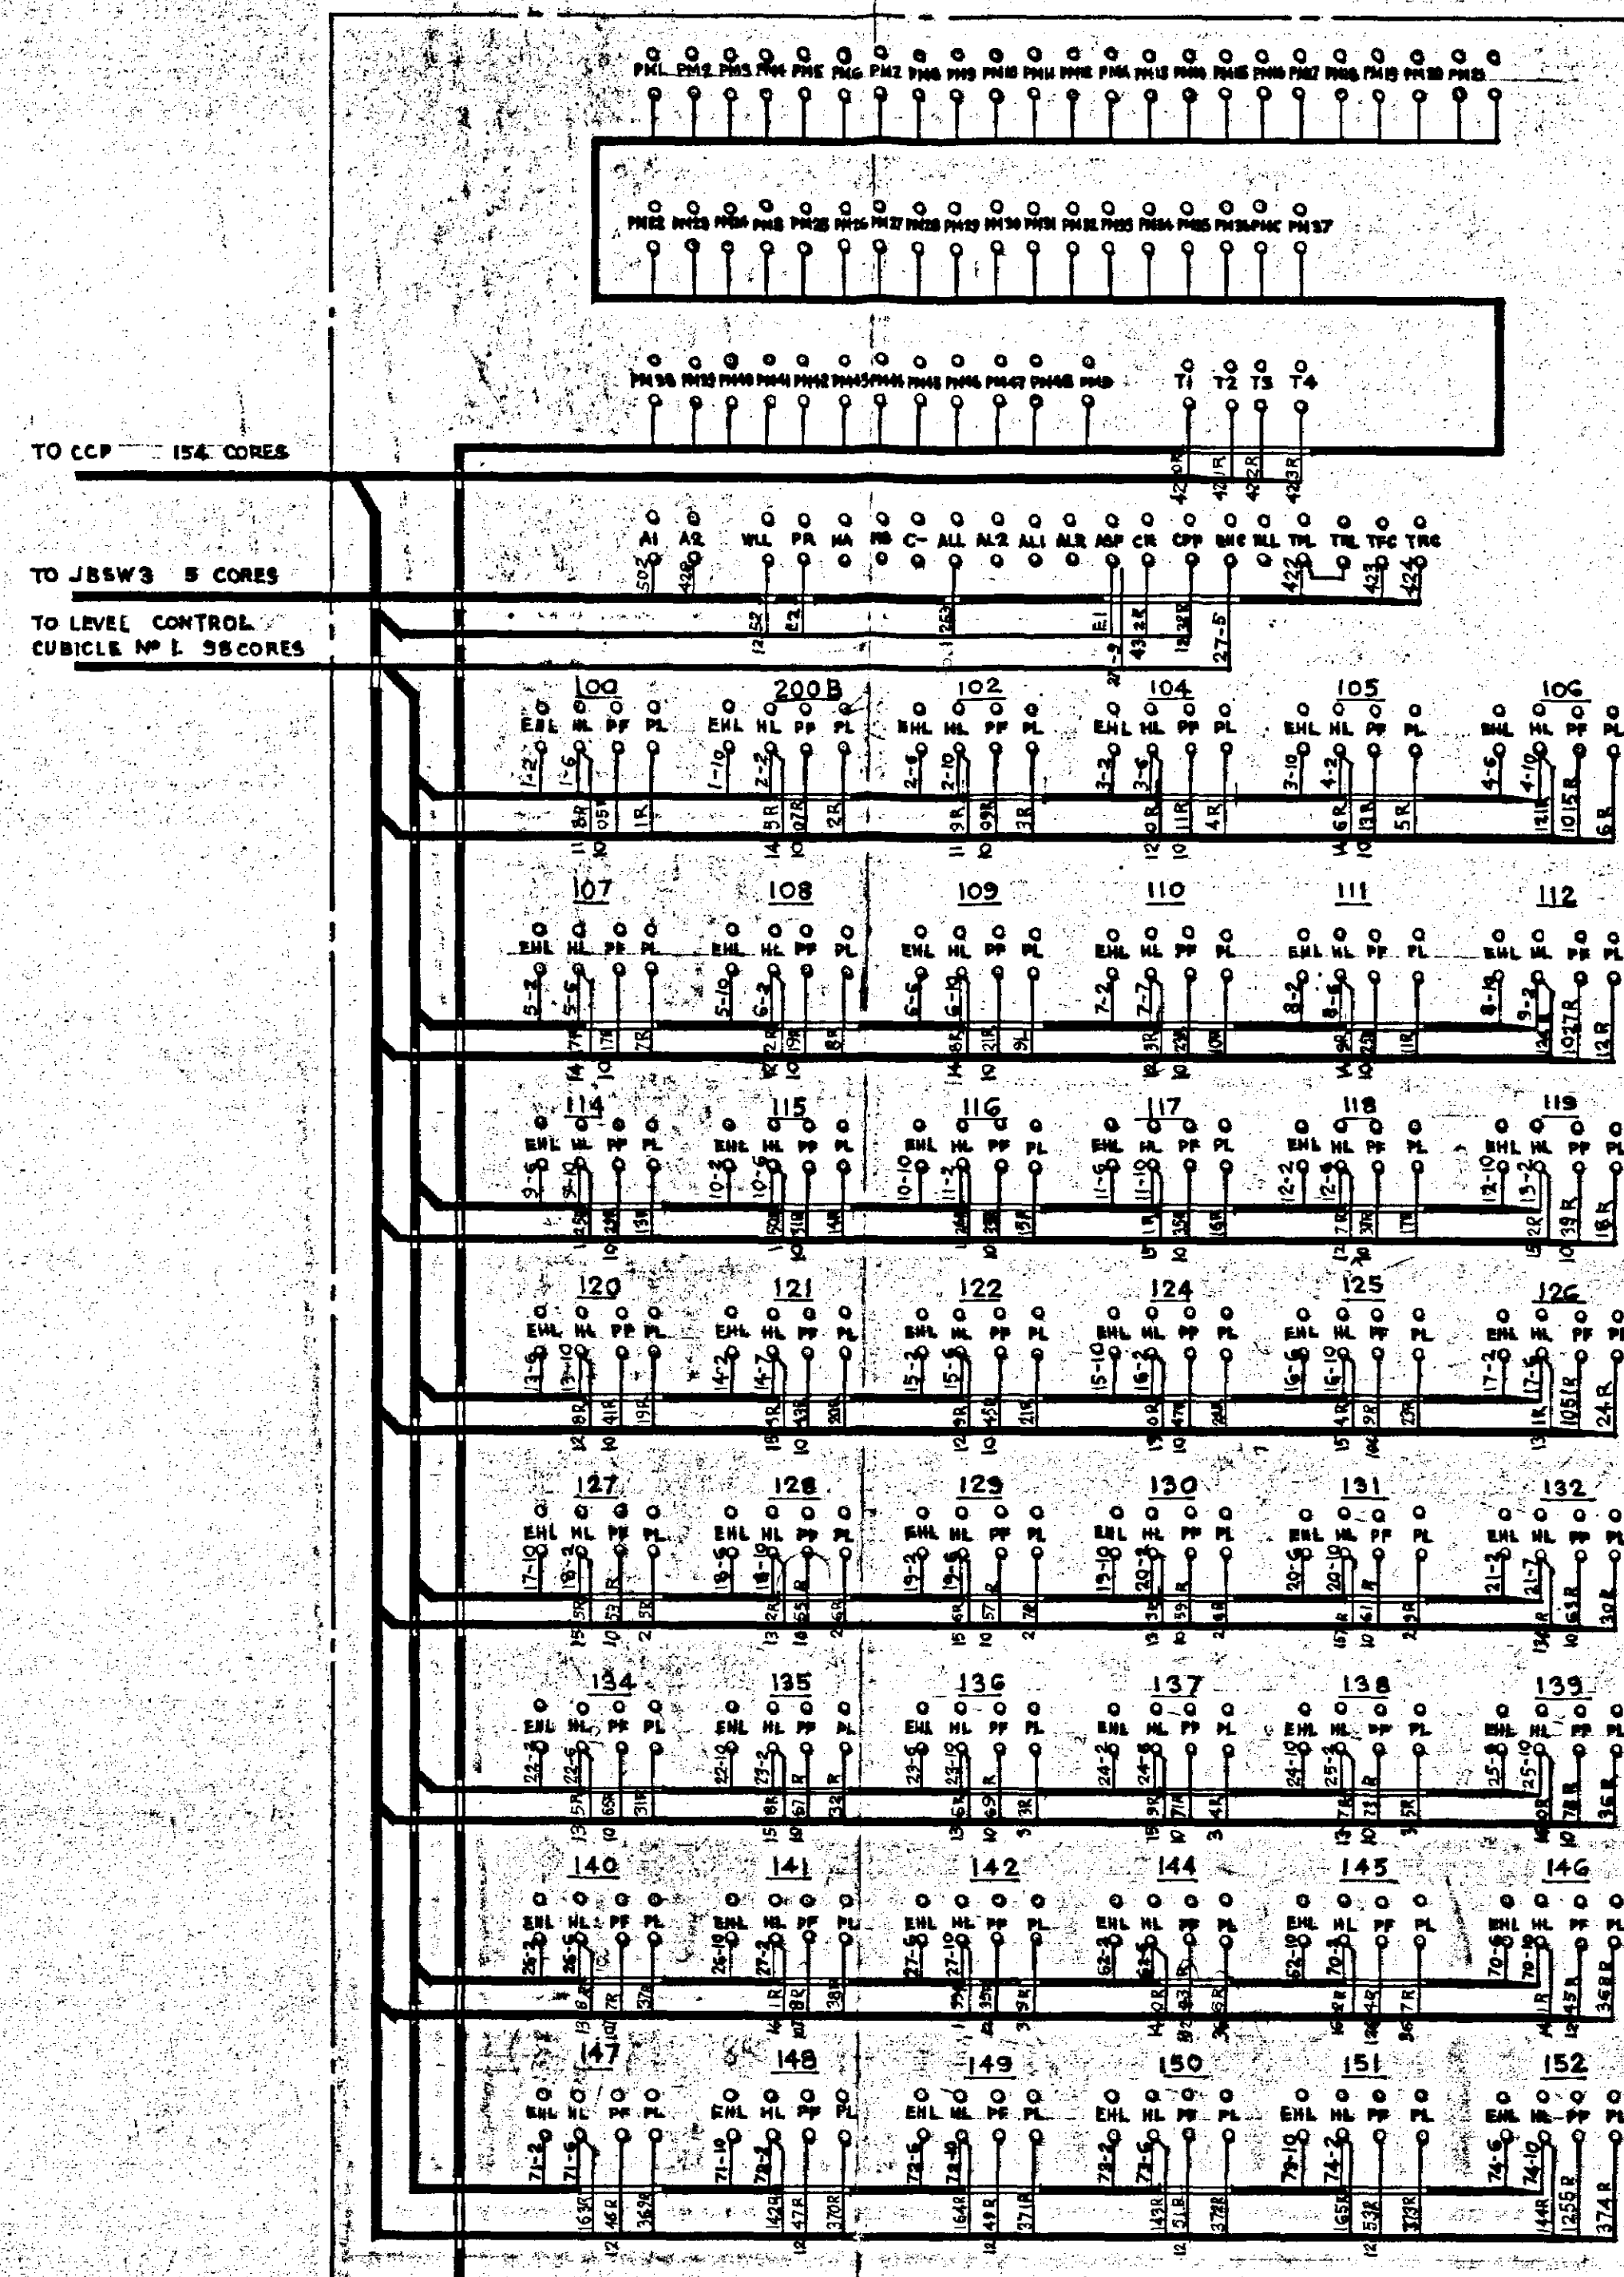

## TRIPPER RELAY PANEL TRB 6

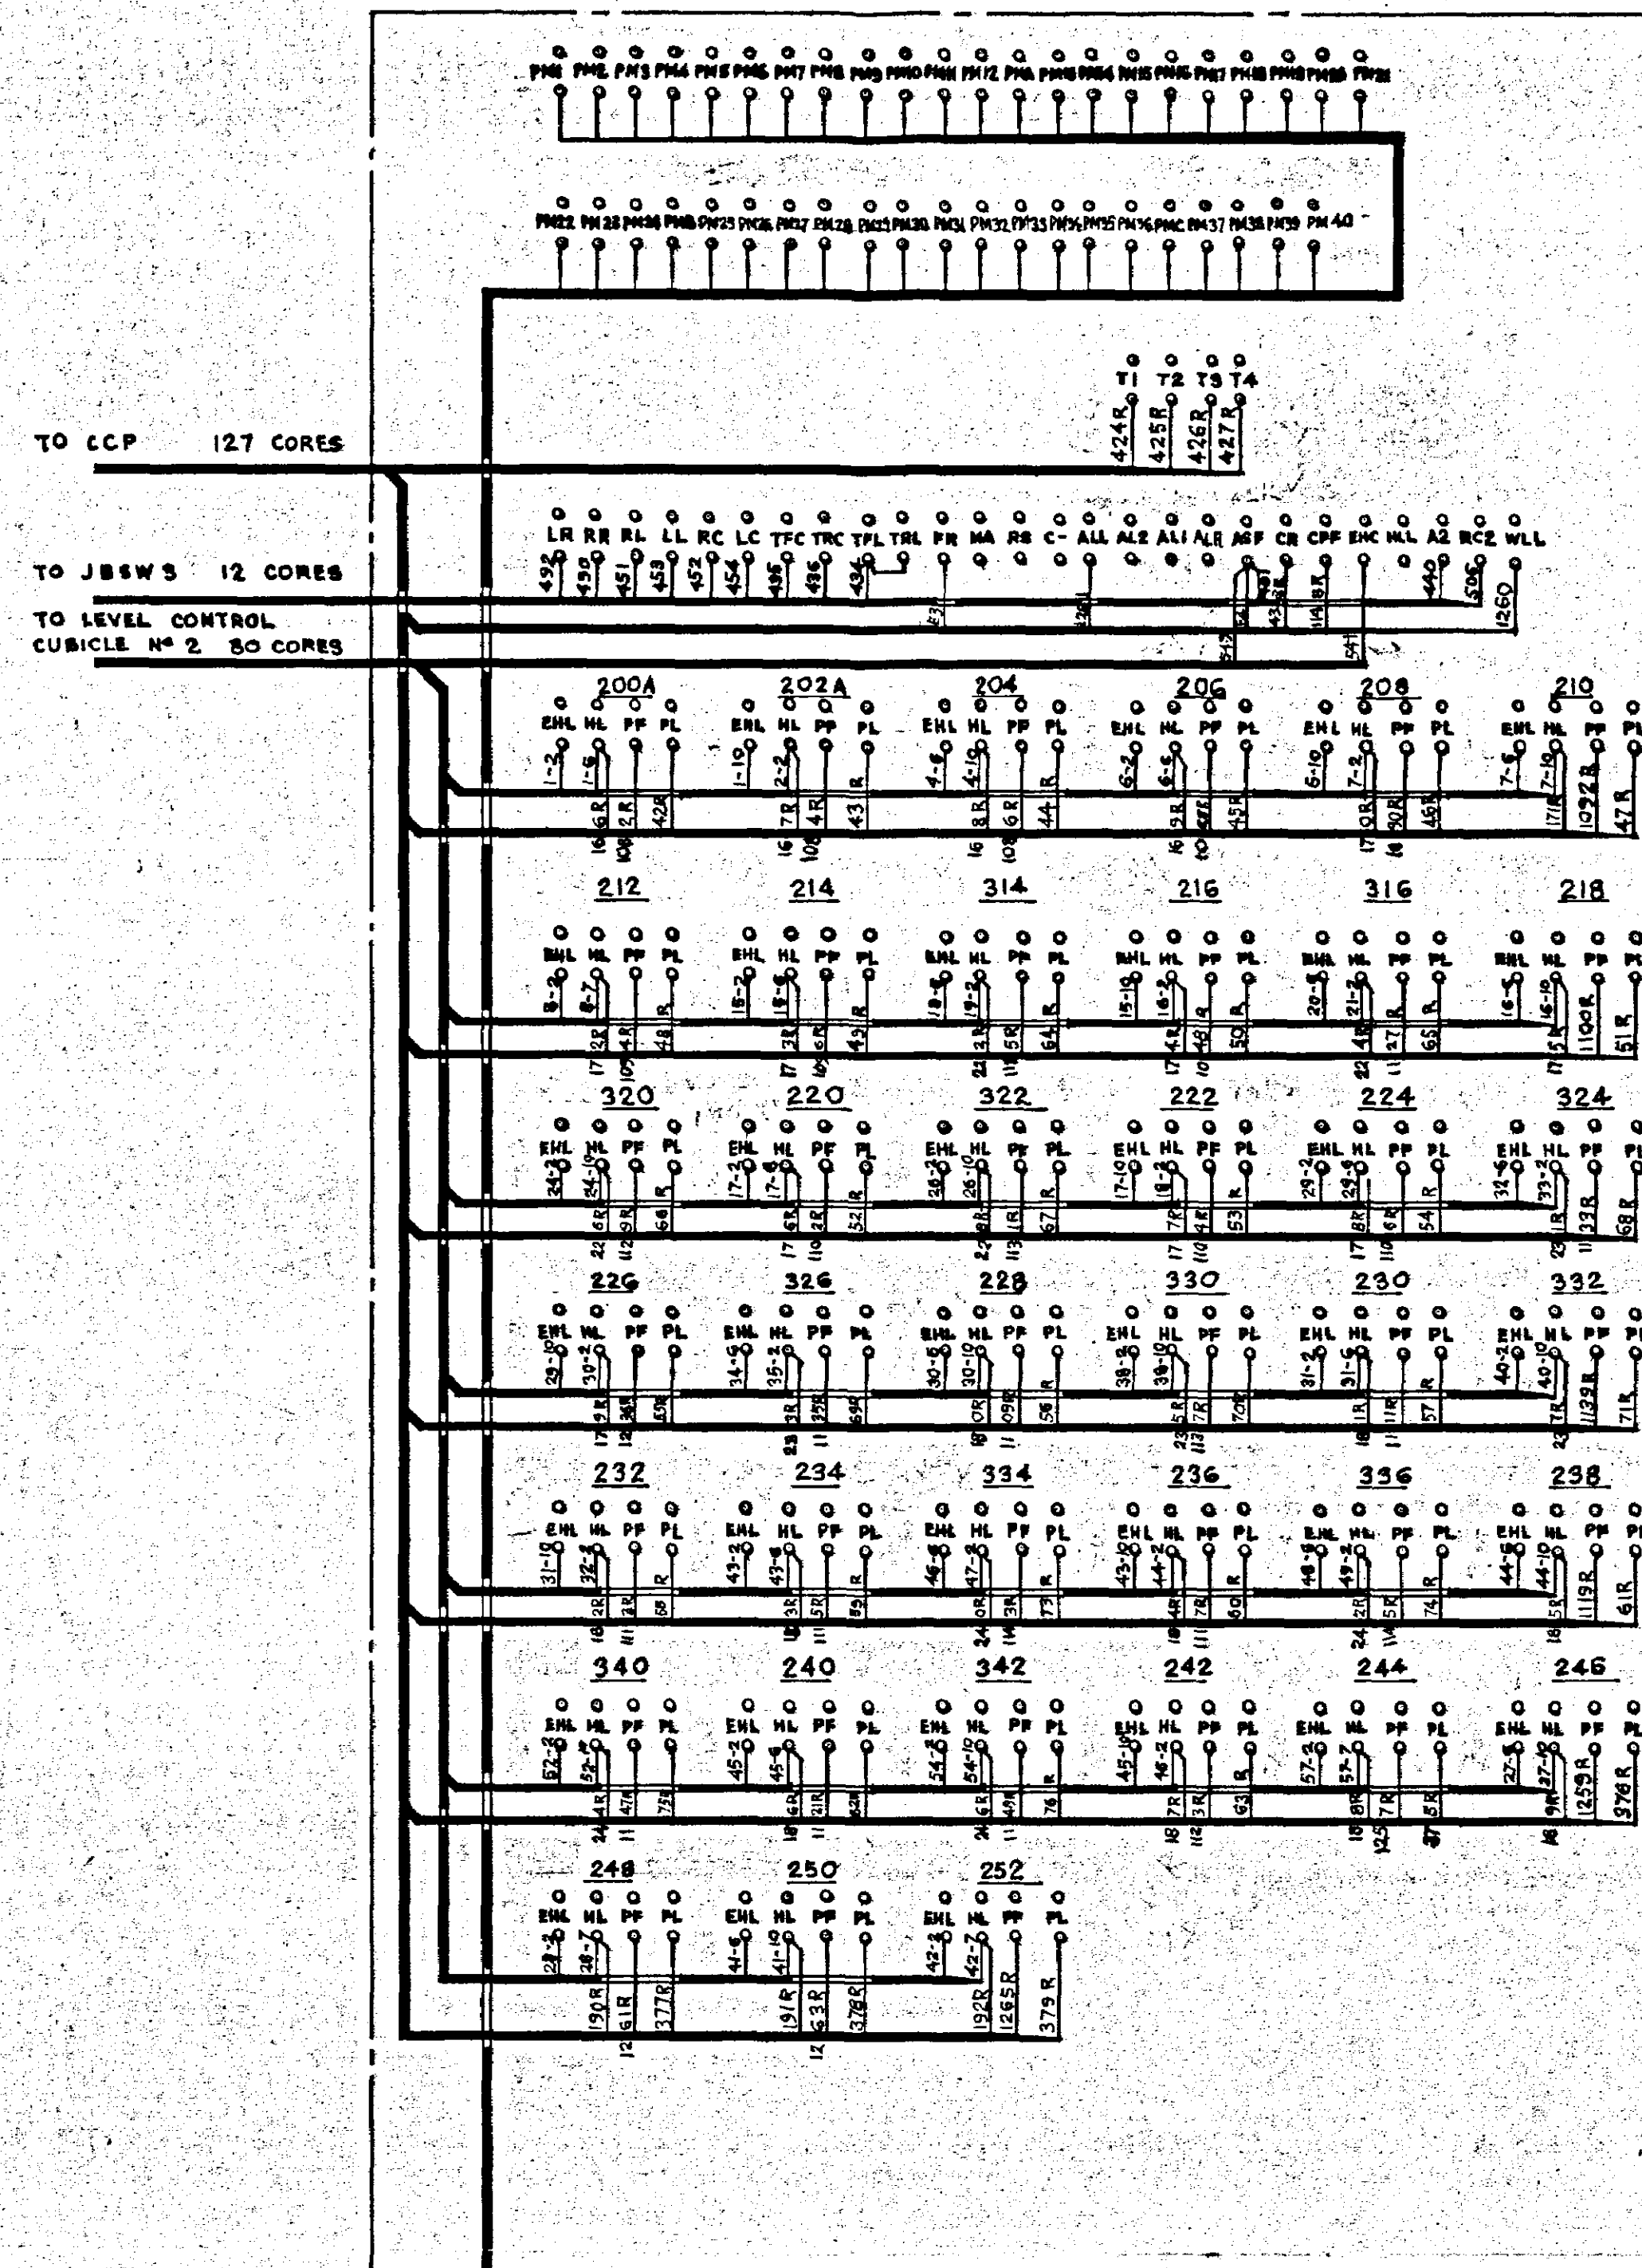

## TRIPPER RELAY PANEL TRB 7

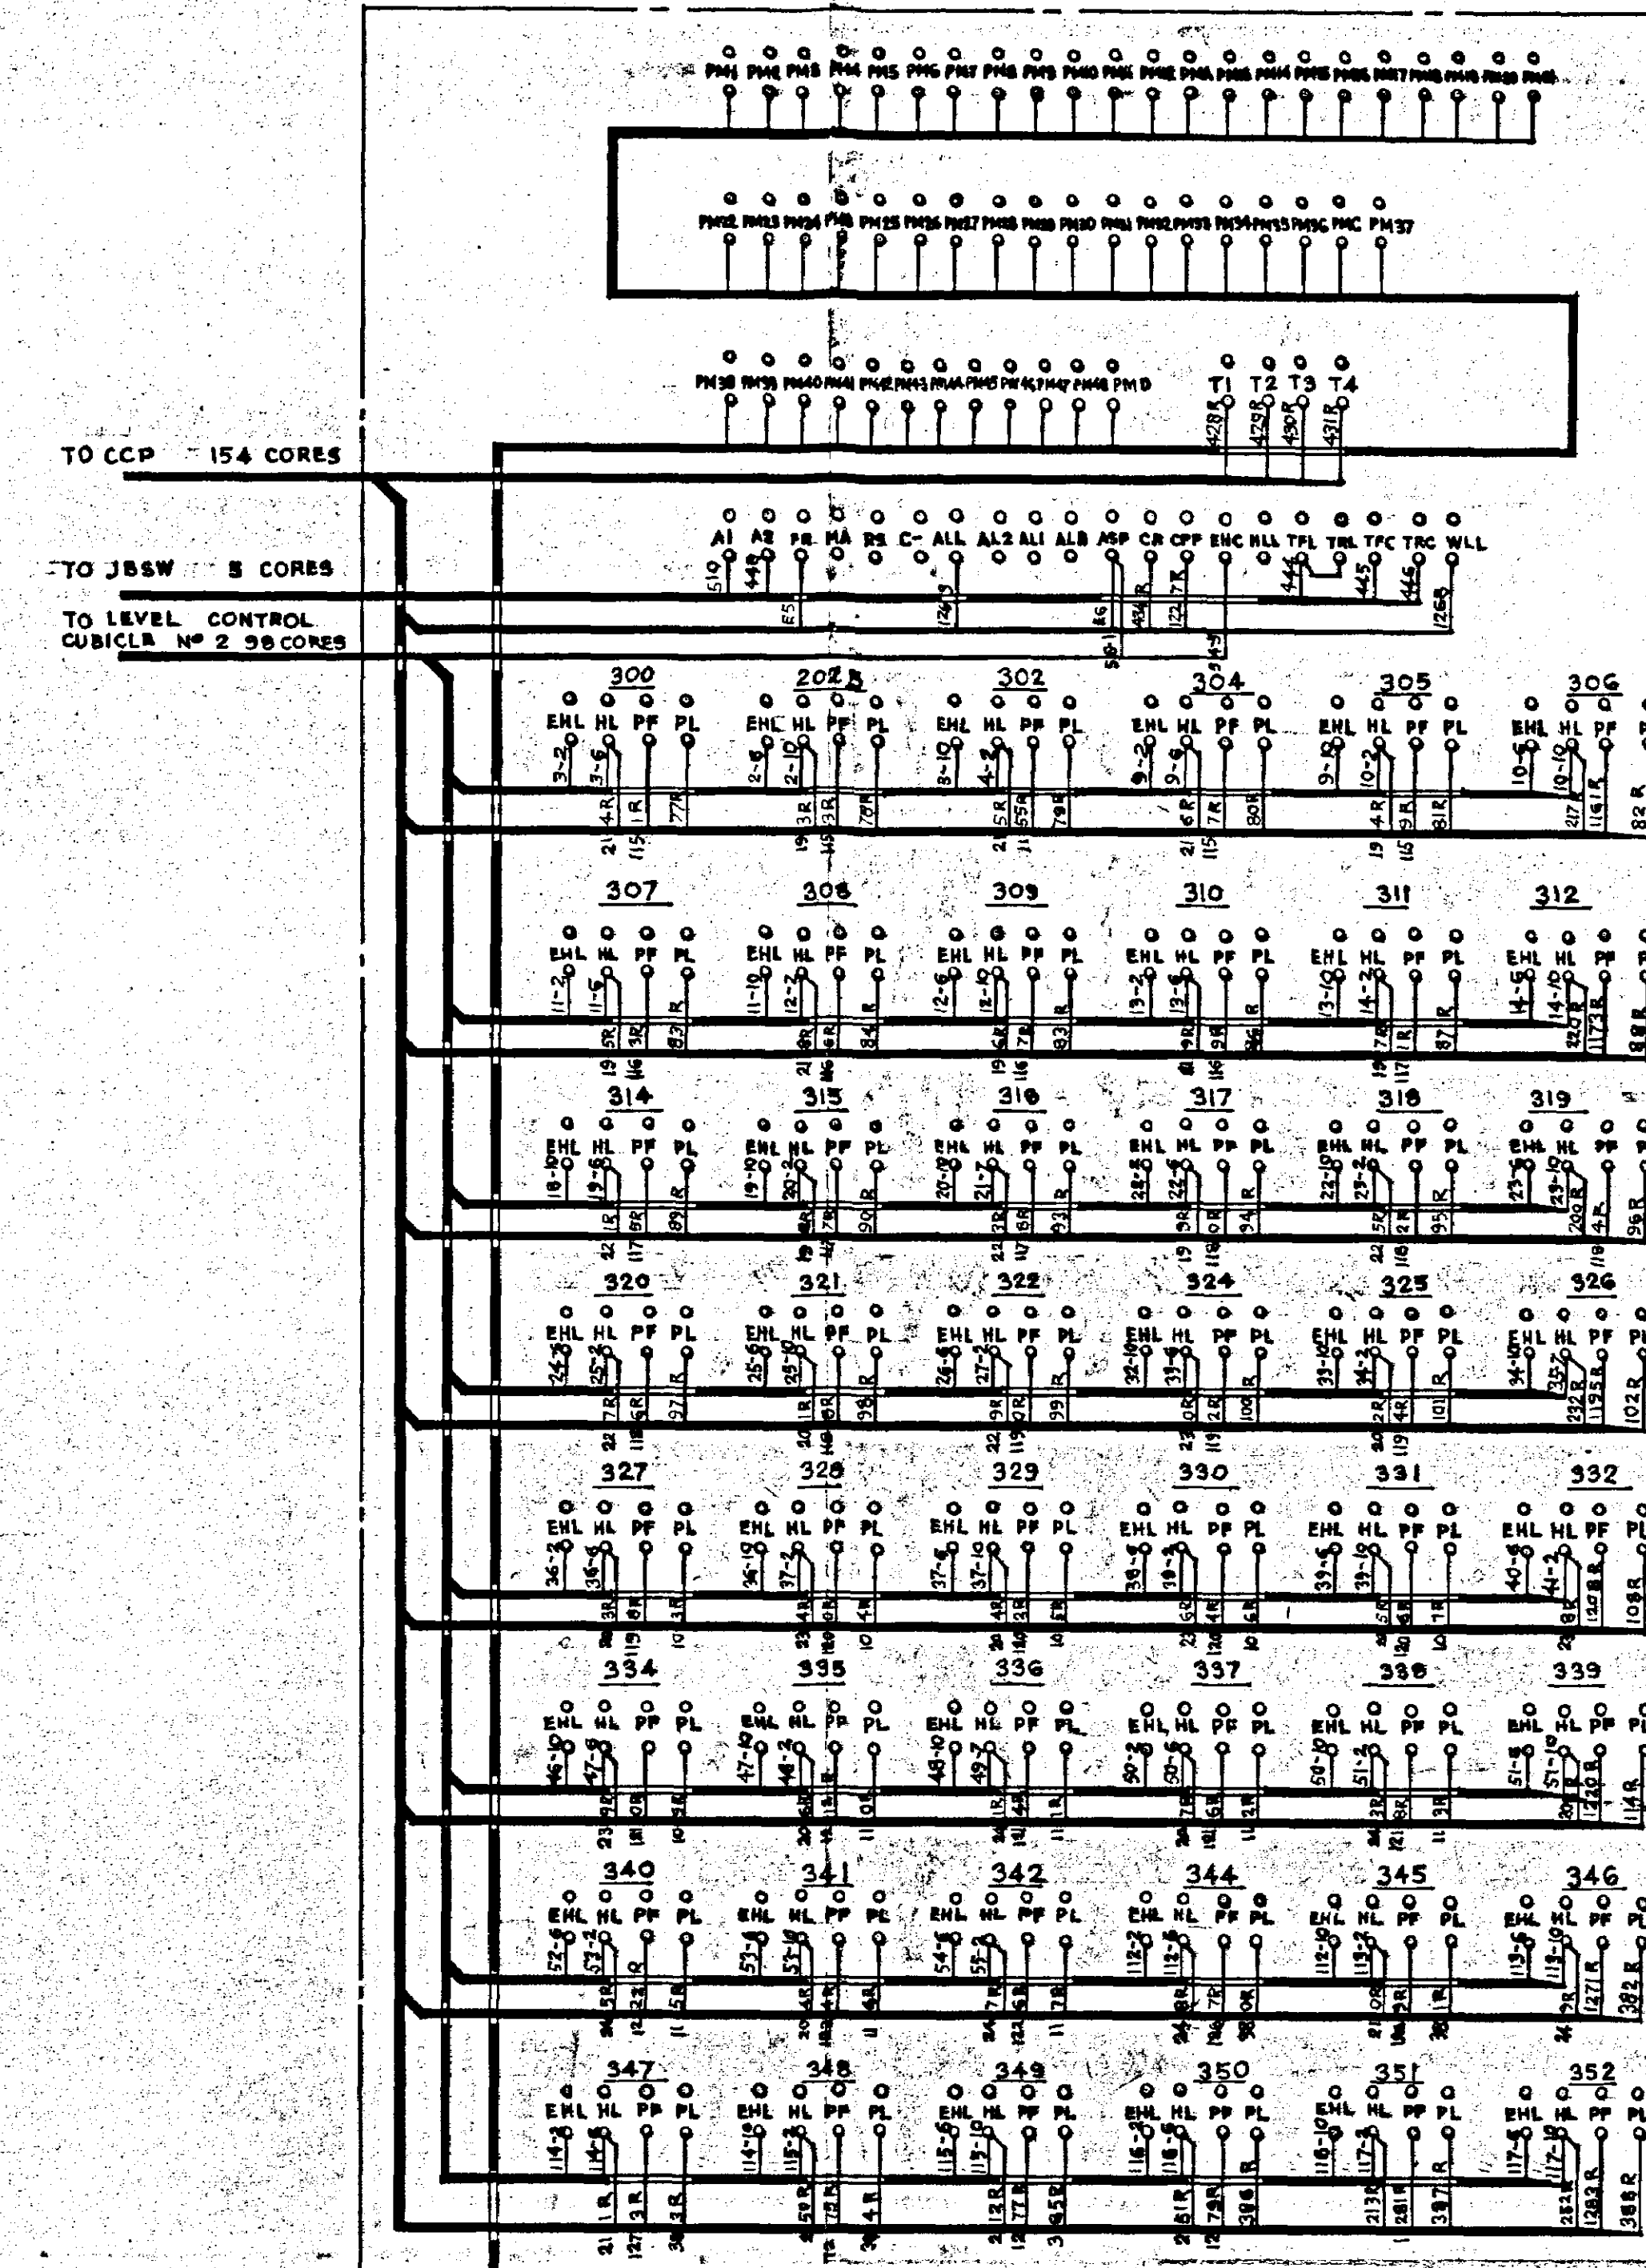

NUMBERS ADJACENT LOOMS  
INDICATE TERMINAL DESIGNATION  
ONLY - THESE ARE NOT WIRE NUMBERS

SEAFORTH GRAIN TERMINAL

DEWHURST & PARTNER LTD.  
MELBOURNE WORKS. HOUNSLOW.

TITLE:  
EXTERNAL WIRING DIAGRAM FOR TRIPPER RELAY PANELS TRB 5 TRB 6 TRB 7

REVISION:  
ORIGIN: 50D

REVISION:  
ORIGIN: 50D

REVISION: 3  
REVISION: 2  
REVISION: 1  
ORIGIN: 1CB  
15/1/78 SCD. JS.

REVISION: 2  
REVISION: 1  
ORIGIN: 1CB  
10/2/72 SCD. JS.

REVISION: 1  
ORIGIN: 1CB  
10/2/72 SCD. JS.

DRAWN BY L. THOMAS  
DATE: 15/6/71  
CHECKED BY  
APPROVED BY  
DATE

SEAFORTH GRAIN TERMINAL  
EXTERNAL WIRING DIAGRAM FOR TRIPPER  
RELAY PANELS TRB 5, TRB 6, TRB 7

THE DESIGN AND MANUFACTURING  
INFORMATION CONTAINED IN  
THIS DRAWING IS THE EXCLUSIVE  
RIGHT OF DEWHURST & PARTNER  
LTD AND MUST NOT BE COPIED  
OR USED FOR MANUFACTURING  
PURPOSES

ISSUE 12/14  
STX 361 AG  
STX 361 AG