




TRIPPER RELAY PANEL TRB5

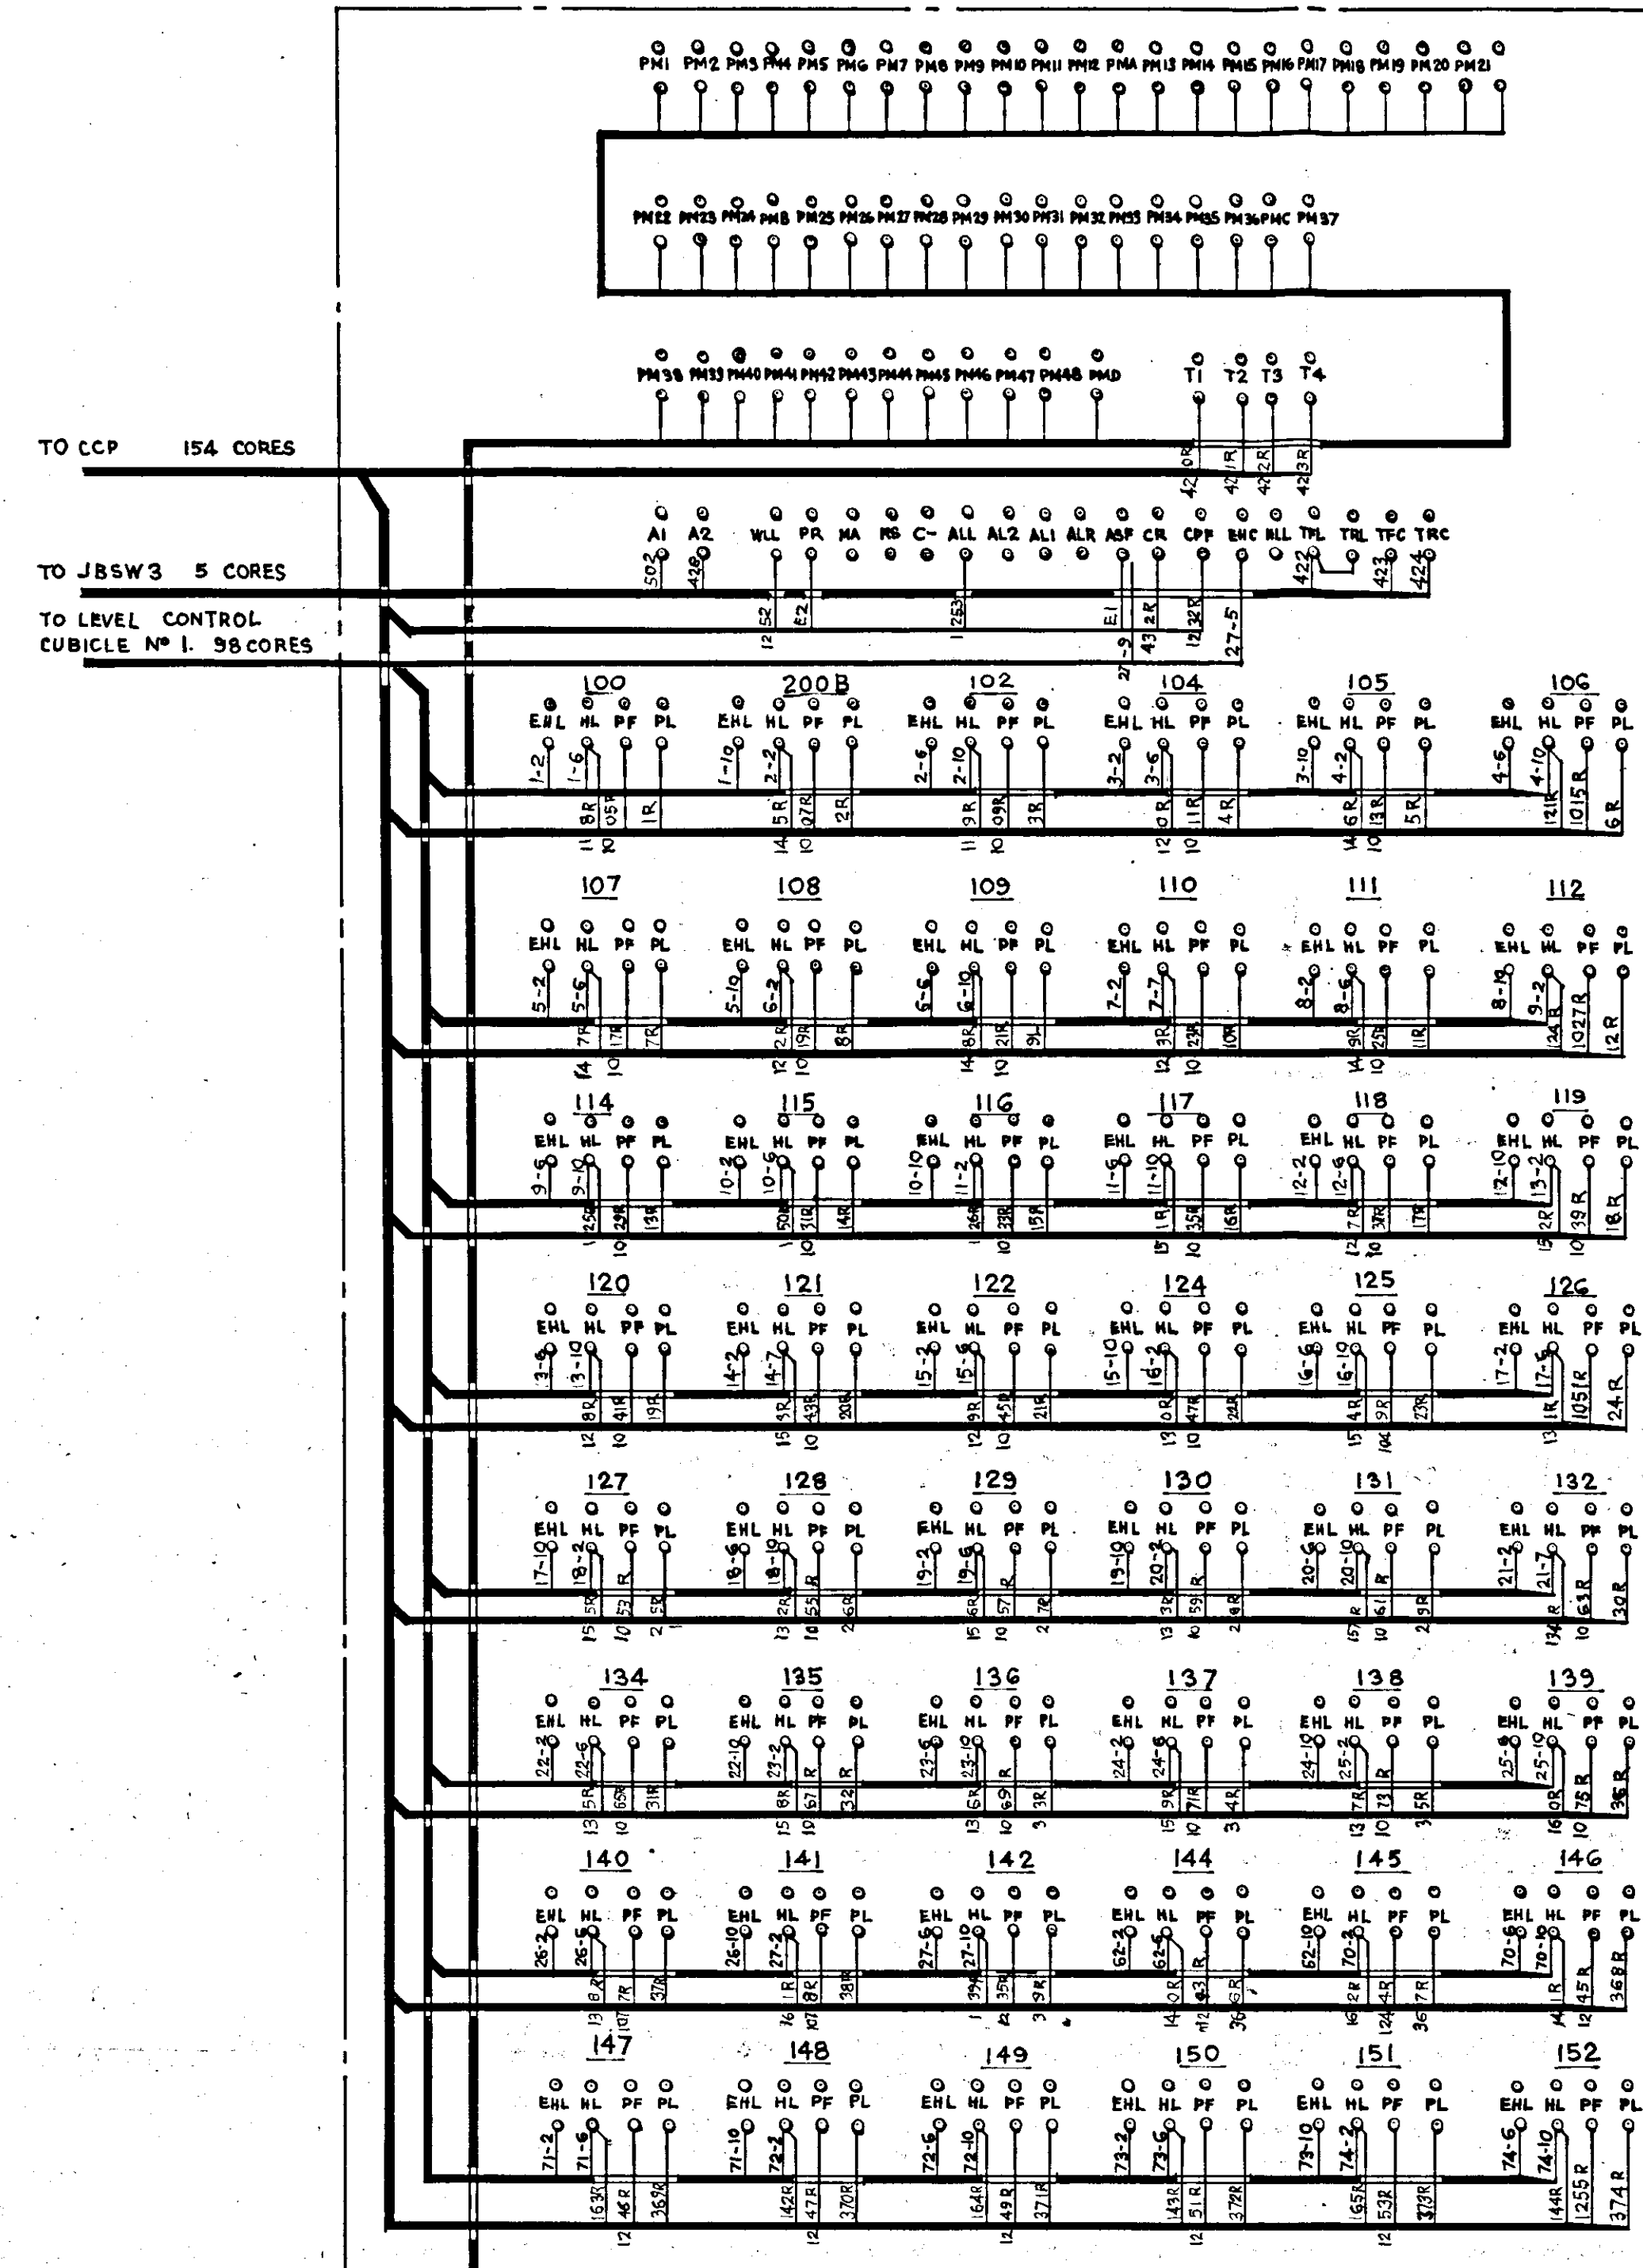


PERMANENT MAGNET PROXIMITY SWITCHES

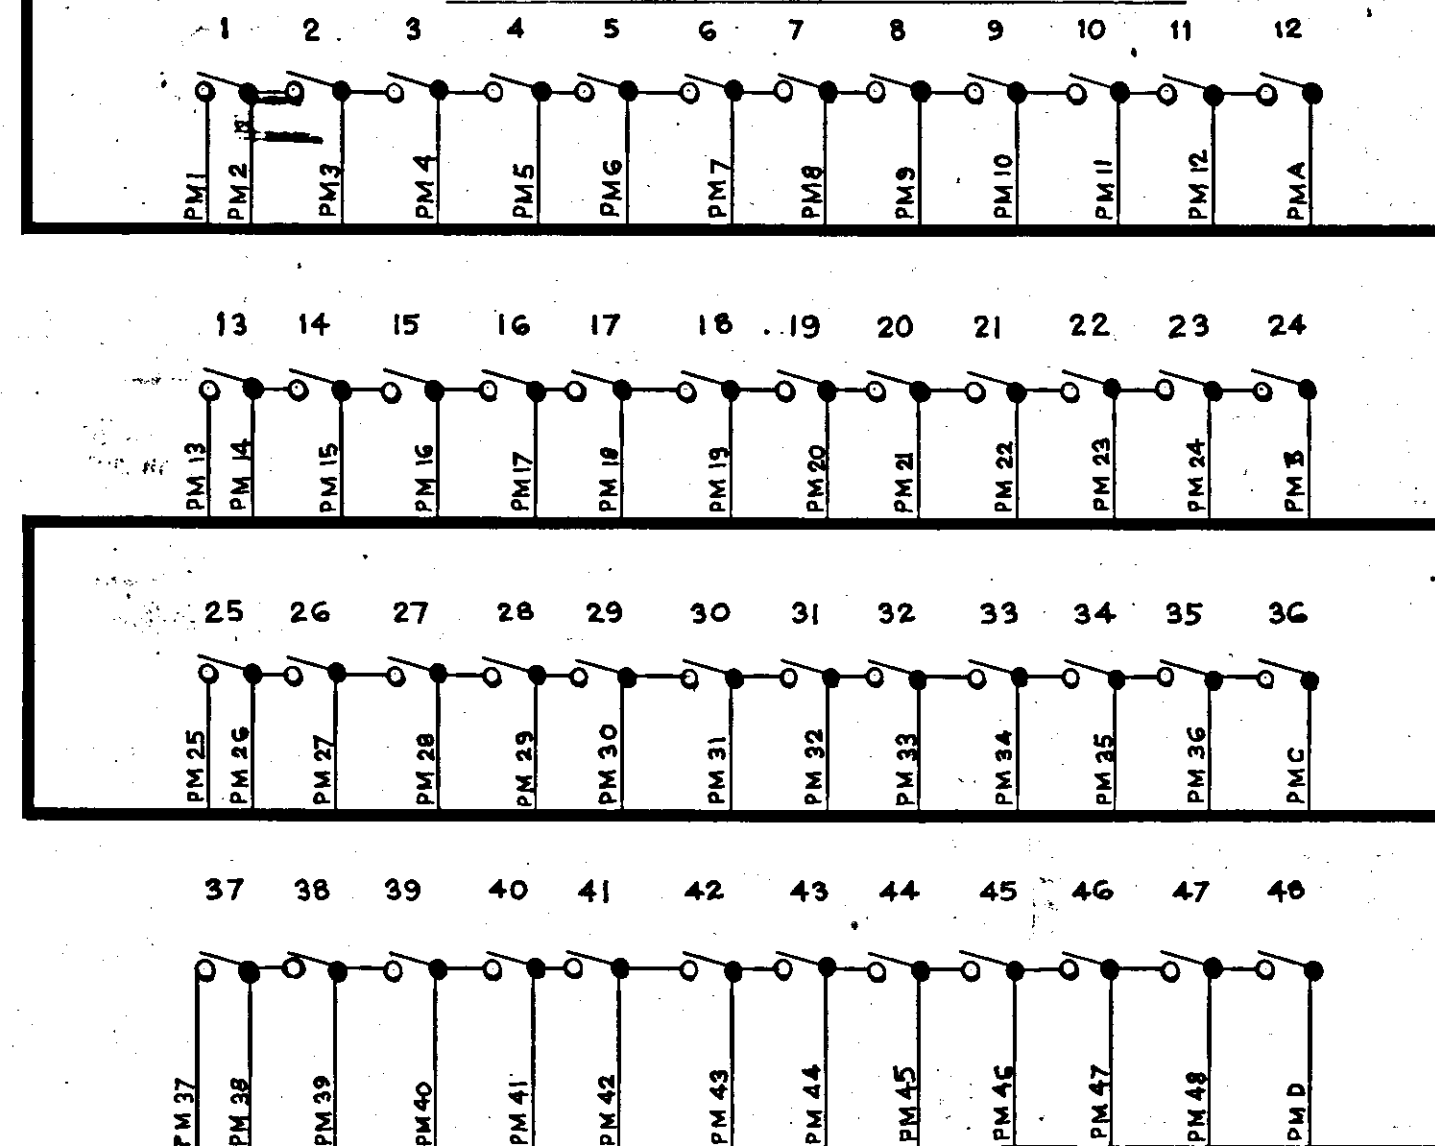

TRIPPER RELAY PANEL TRB6

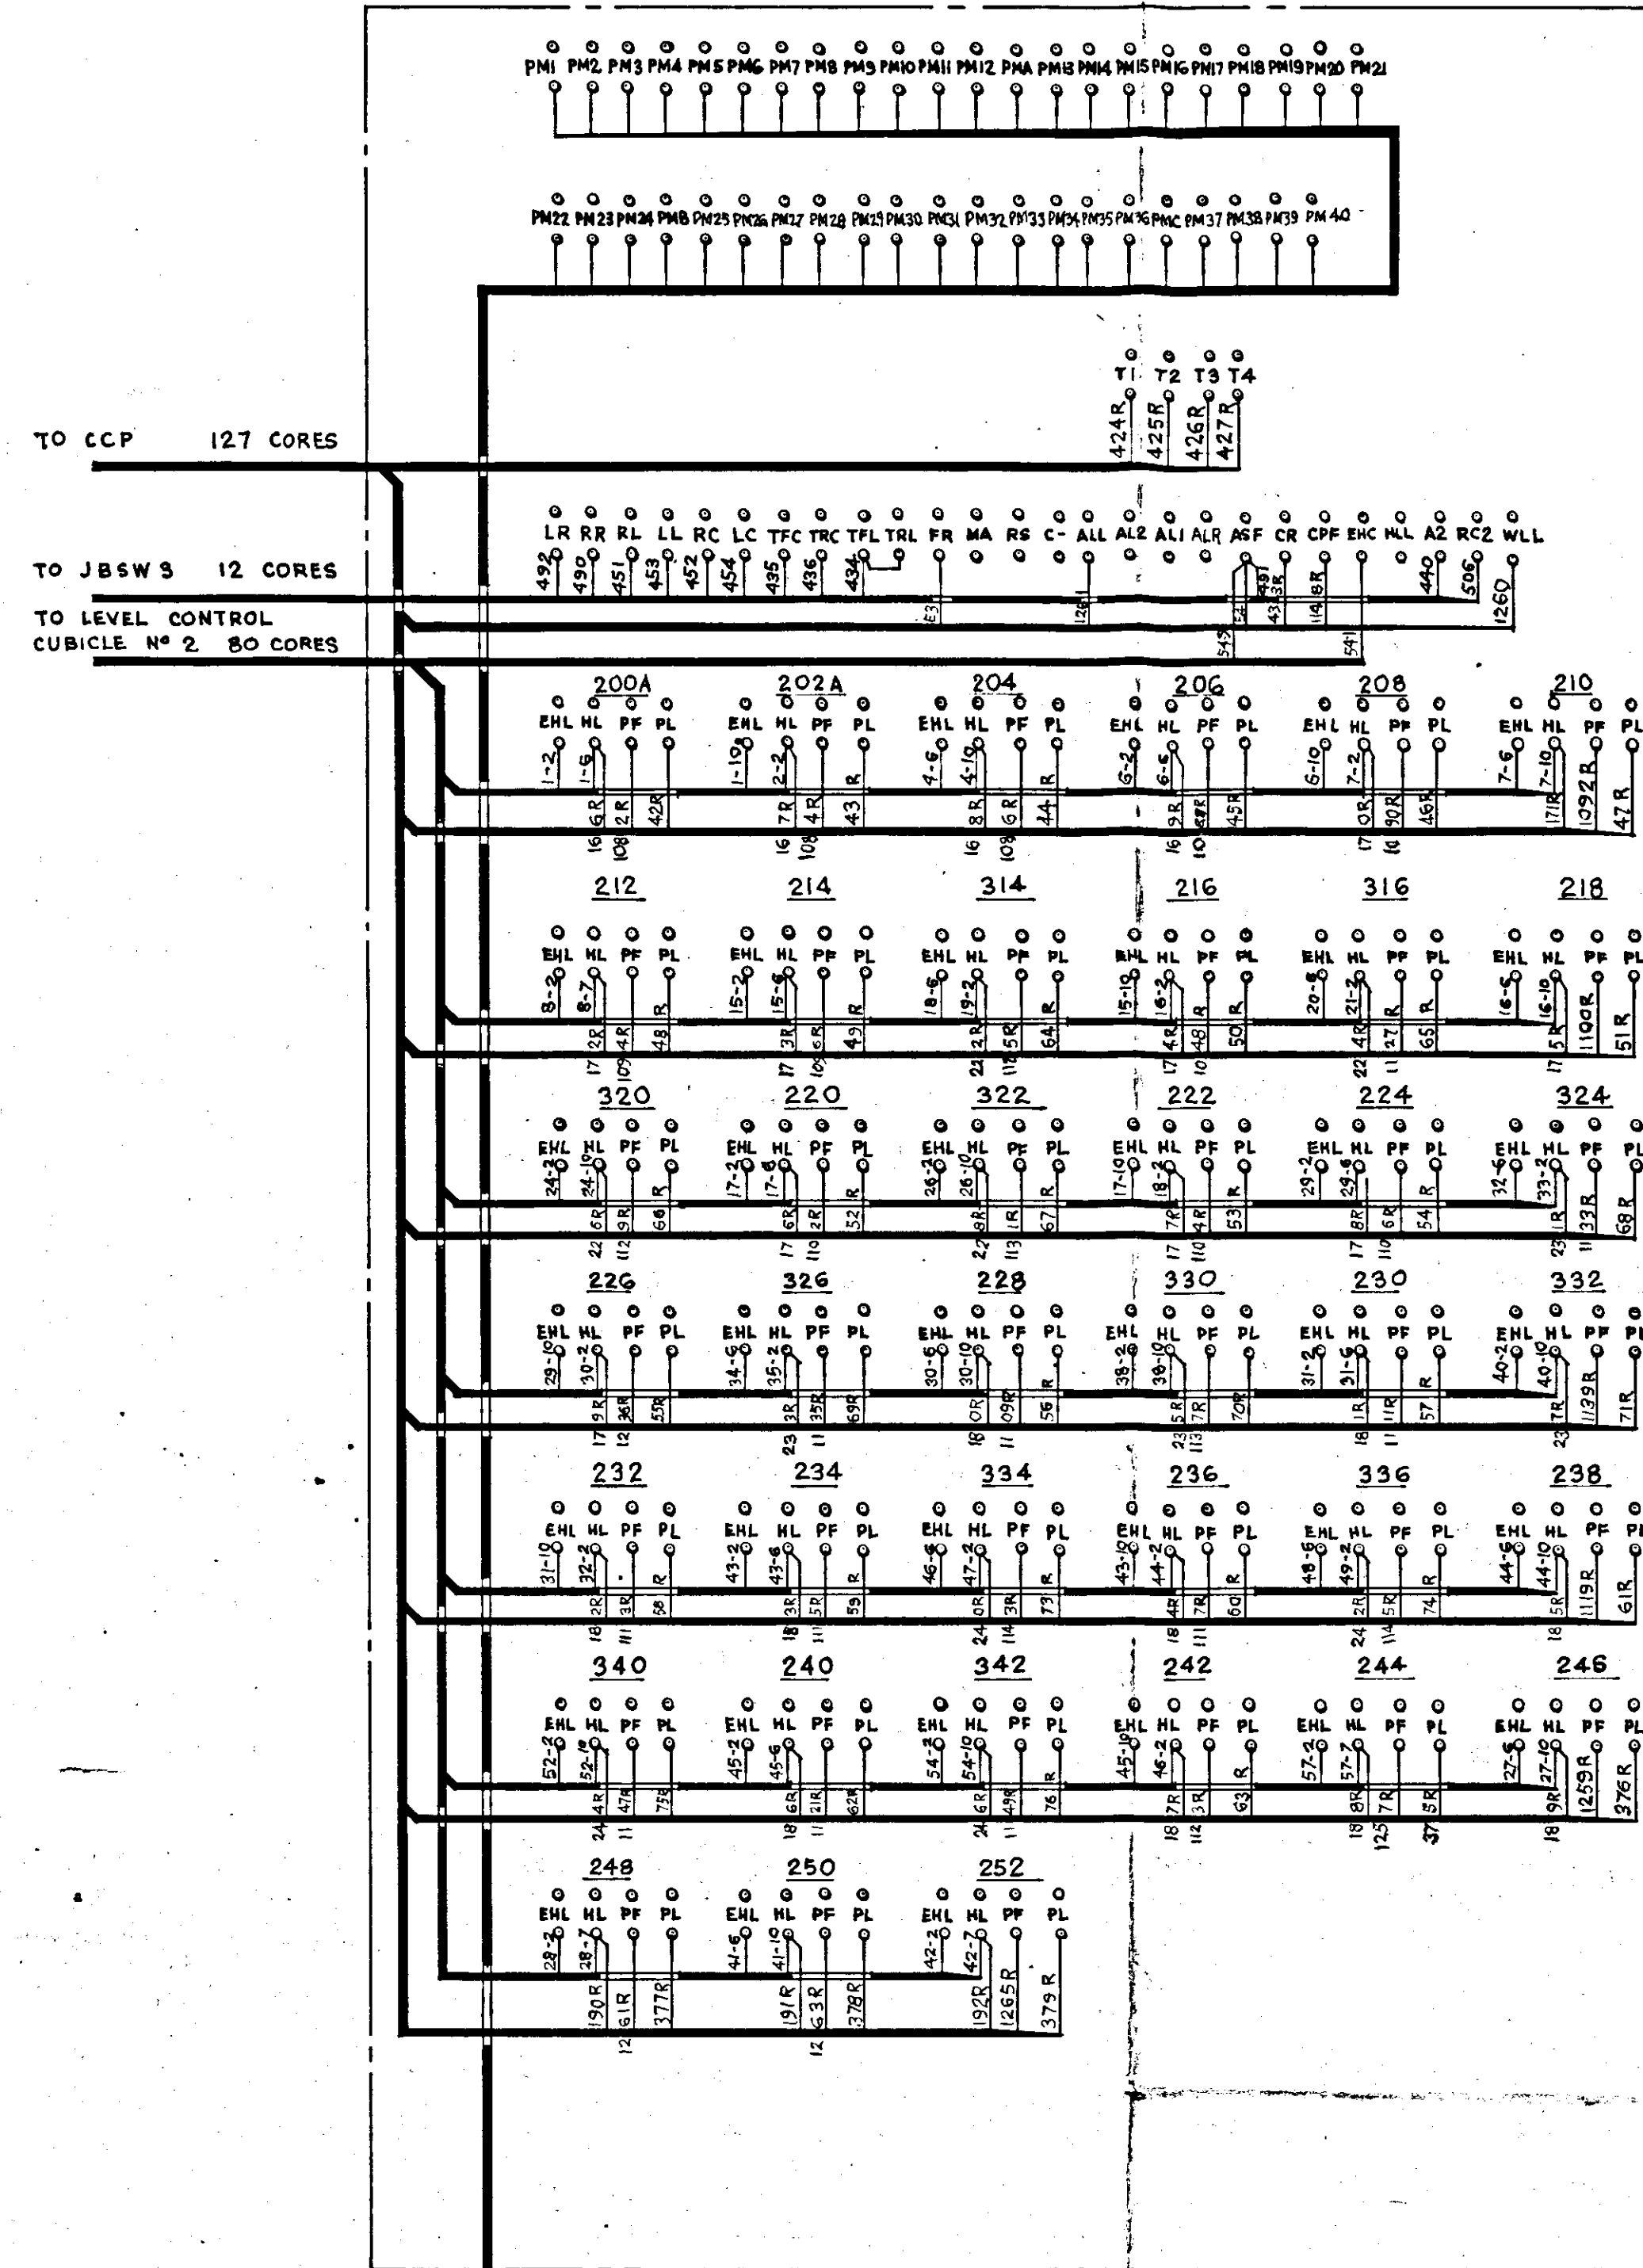

PERMANENT MAGNET PROXIMITY SWITCHES

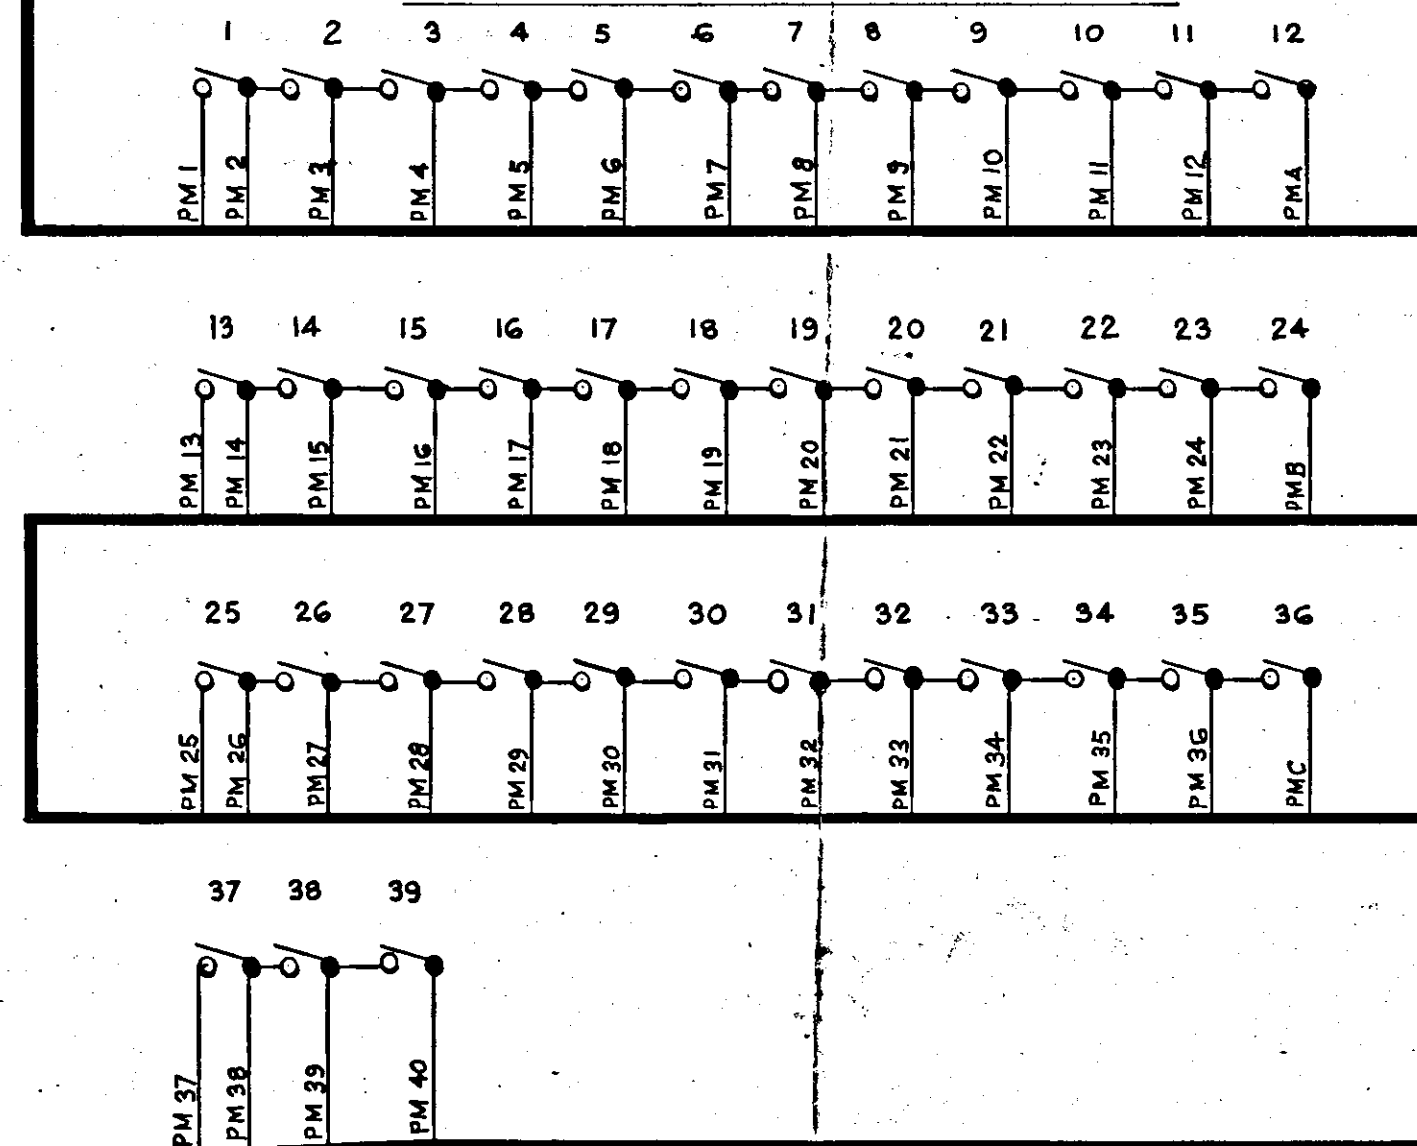

TRIPPER RELAY PANEL TRB7

