


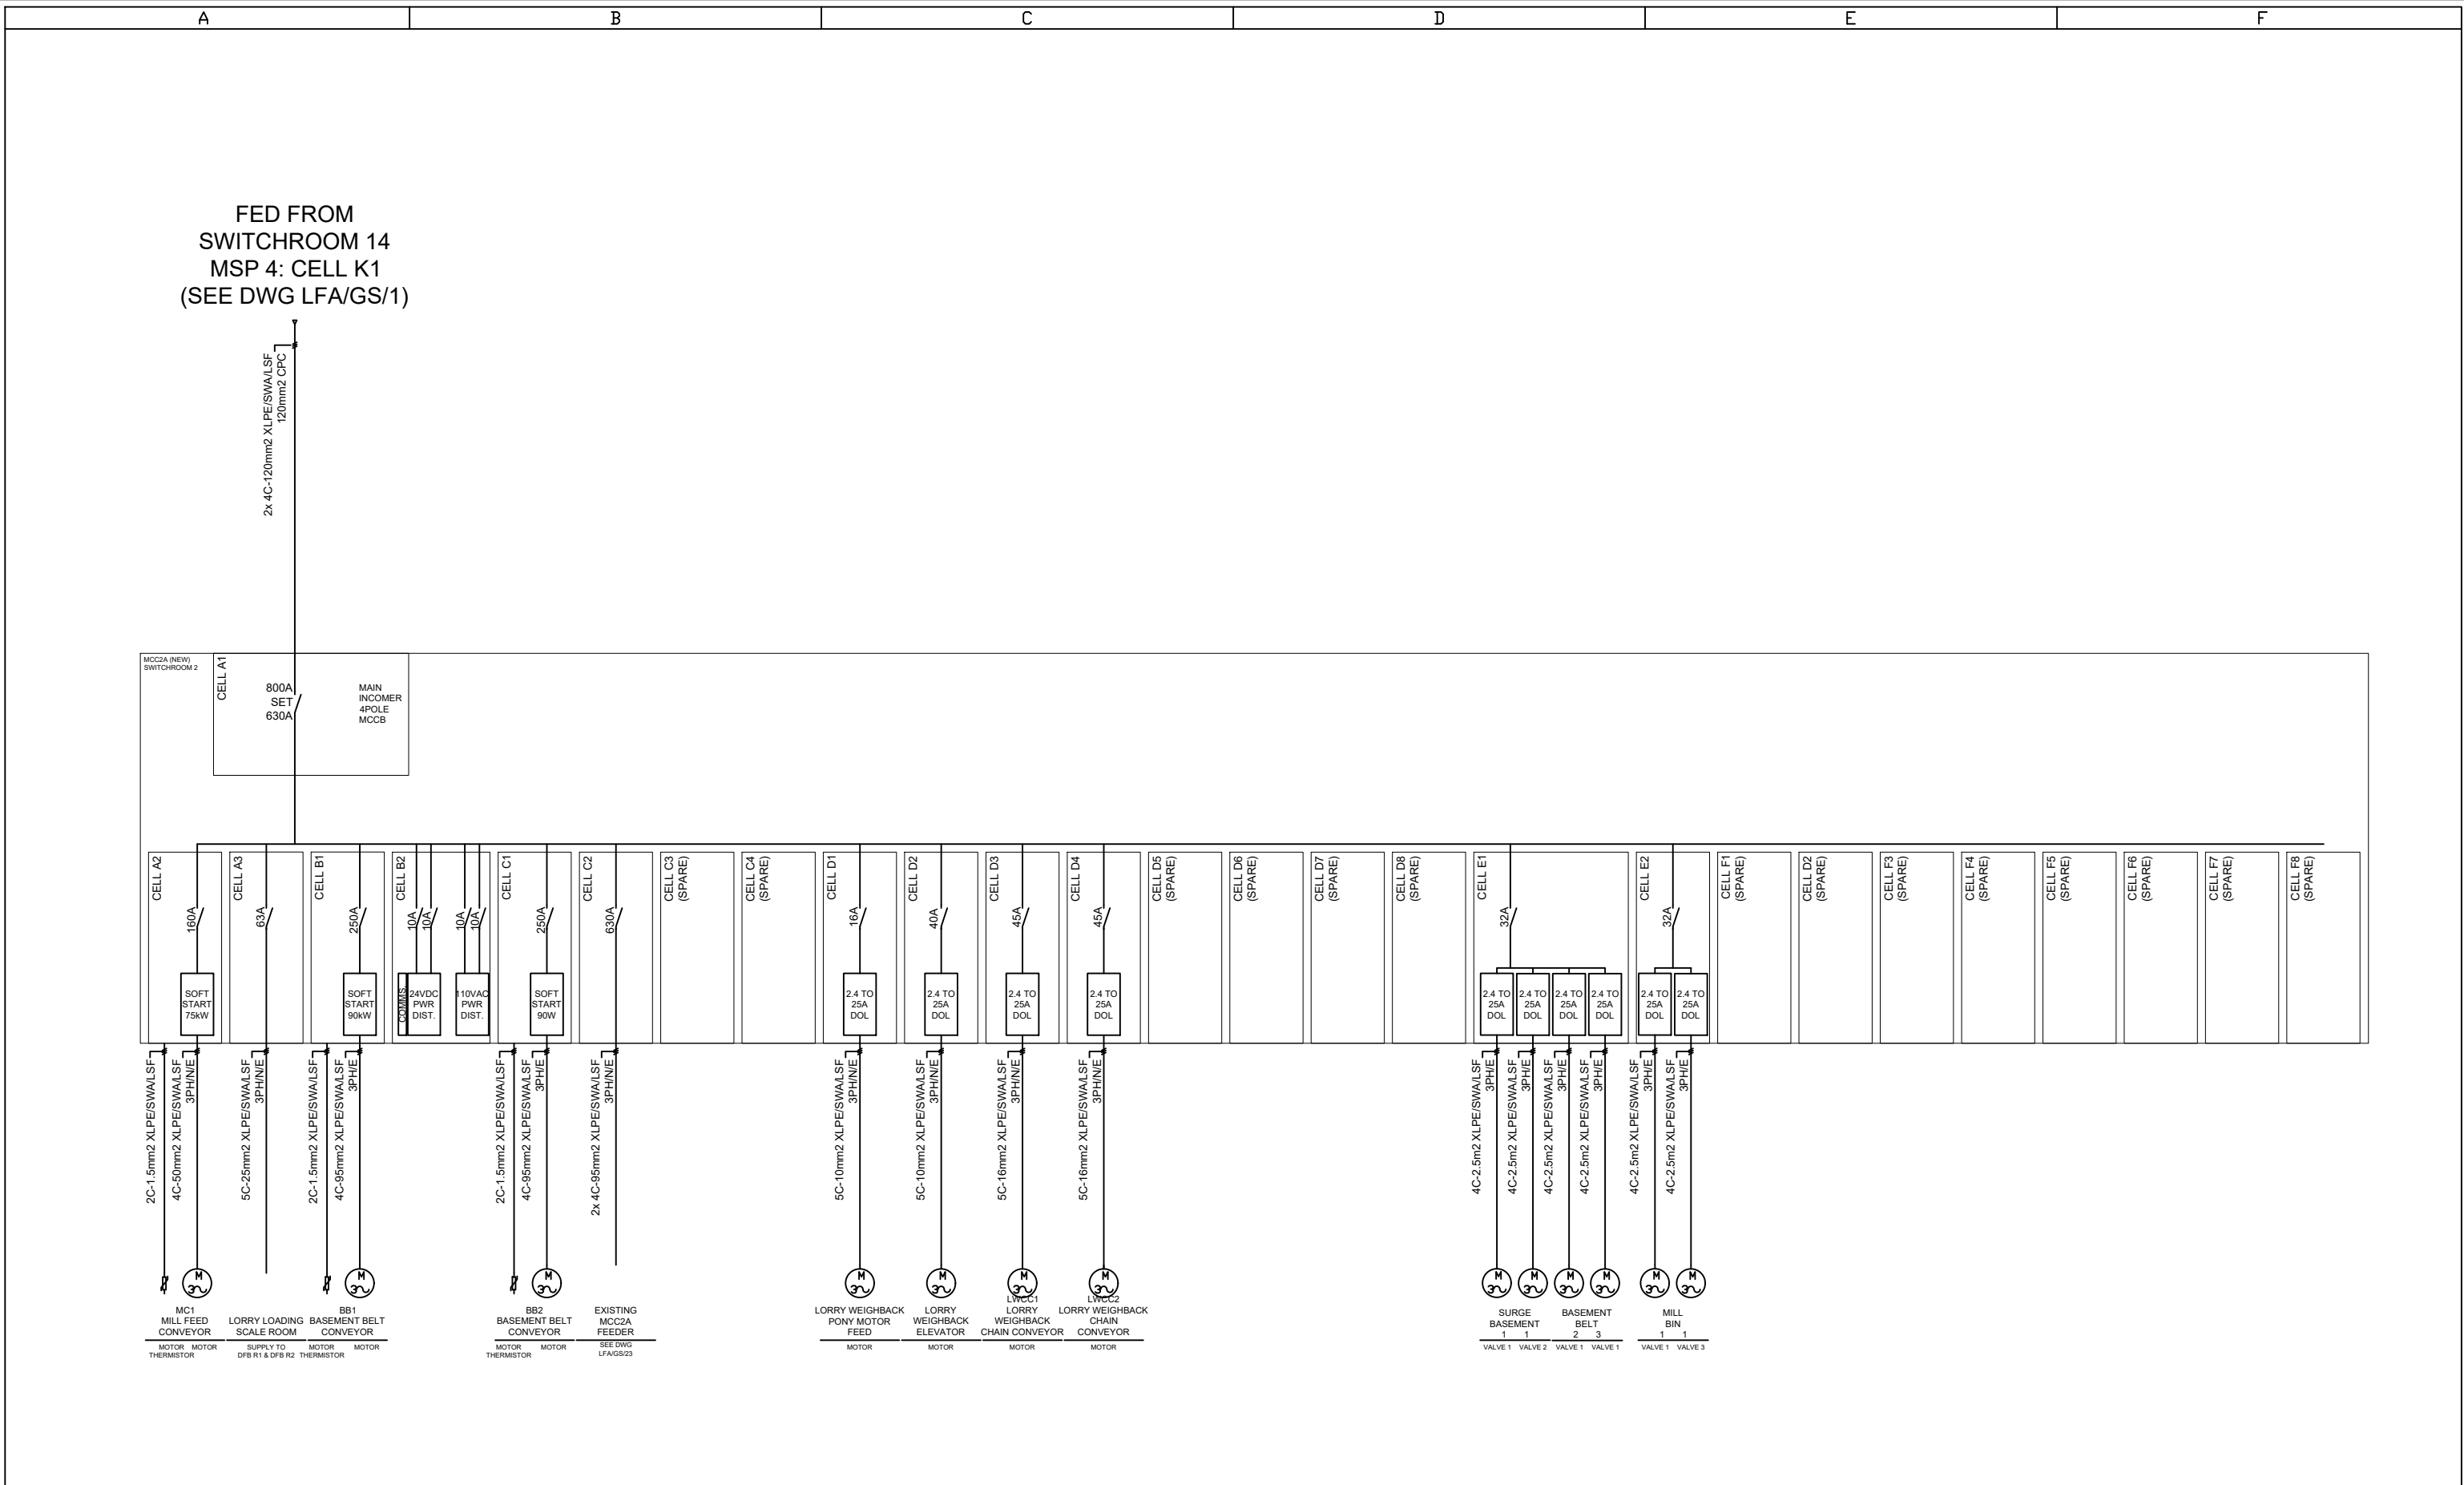

HF Controls Ltd
100 Albert Drive, Glasgow, G41 2SJ

Call 0800 783 9480

www.hf-group.co.uk

Glasgow Edinburgh Manchester Belfast Aberdeen



REV	DATE	DETAIL	CLIENT	PEEL PORTS	ENGINEERED	D.BAL DOCK
00	13/02/24	AS FITTED			DRAWN	D.BAL DOCK
01					CHECKED	W.RIGHT
02					DATE	15/08/23
03					DRG. No.:	284595_0203
04						
05						
06						
07						

TITLE	INSTALL	CLIENT	PEEL PORTS	DRAWING REVISION :	PAGE No.:
			MCC2A	00	01 OF 01
			SINGLE LINE POWER SUPPLY DRAWING		