


HF CONTROLS

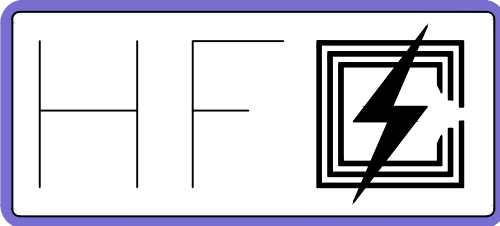

100 ALBERT DRIVE
GLASGOW G41 2SJ

TEL: +44 141 429 2277
EMAIL: hfcontrols.co.uk

PROJECT: RSGT

PROJECT LOCATION: LIVERPOOL

PROJECT REFERENCE NUMBER: 291926

CLIENT: PEEL PORTS

CLIENT ADDRESS: MARITIME CENTRE PORT OF LIVERPOOL

CLIENT ORDER NUMBER: ????

CONTROL SYSTEM DETAILS & SPECIFICATION

SYSTEM TYPE:	SAFE AREA
ENCLOSURE MATERIAL:	MILD STEEL
RATED VOLTAGE:	400V AC
RATED FREQUENCY:	50 Hz
RATED AMPERE:	??A
CONTROL VOLTAGE:	24V DC
DEGREE OF PROTECTION:	IP 55
PAINT FINISH:	POWDER COATED RAL7035
YEAR OF MANUFACTURE:	2022

DRAWING STATUS

FIRST DRAFT


FOR MANUFACTURE

SIGNED..... DATED.....

☐

☐

REV	DATE	DETAIL	CLIENT	PEEL PORT	ENGRD. D.BALDOCK	 HF Controls Ltd 100 Albert Drive, Glasgow G41 2SJ Tel: +44 (0)141 429 5575 Fax: +44 (0)141 420 1054 email: hf@hfcontrols.co.uk www.hf-group.co.uk
00	05/07/22	FIRST DRAFT			DRAWN. D.BALDOCK	
01	12/02/25	MC2 DUST PLANT FAN ADDED			CHECK M.WRIGHT	
02			DATE 12/02/25			
03			INSTALL	RSGT LIVERPOOL		
04						
05						
06			TITLE	MCC2A WIRING SCHEMATICS	DRG. No.:	
07					284595 / 1002 / 01	

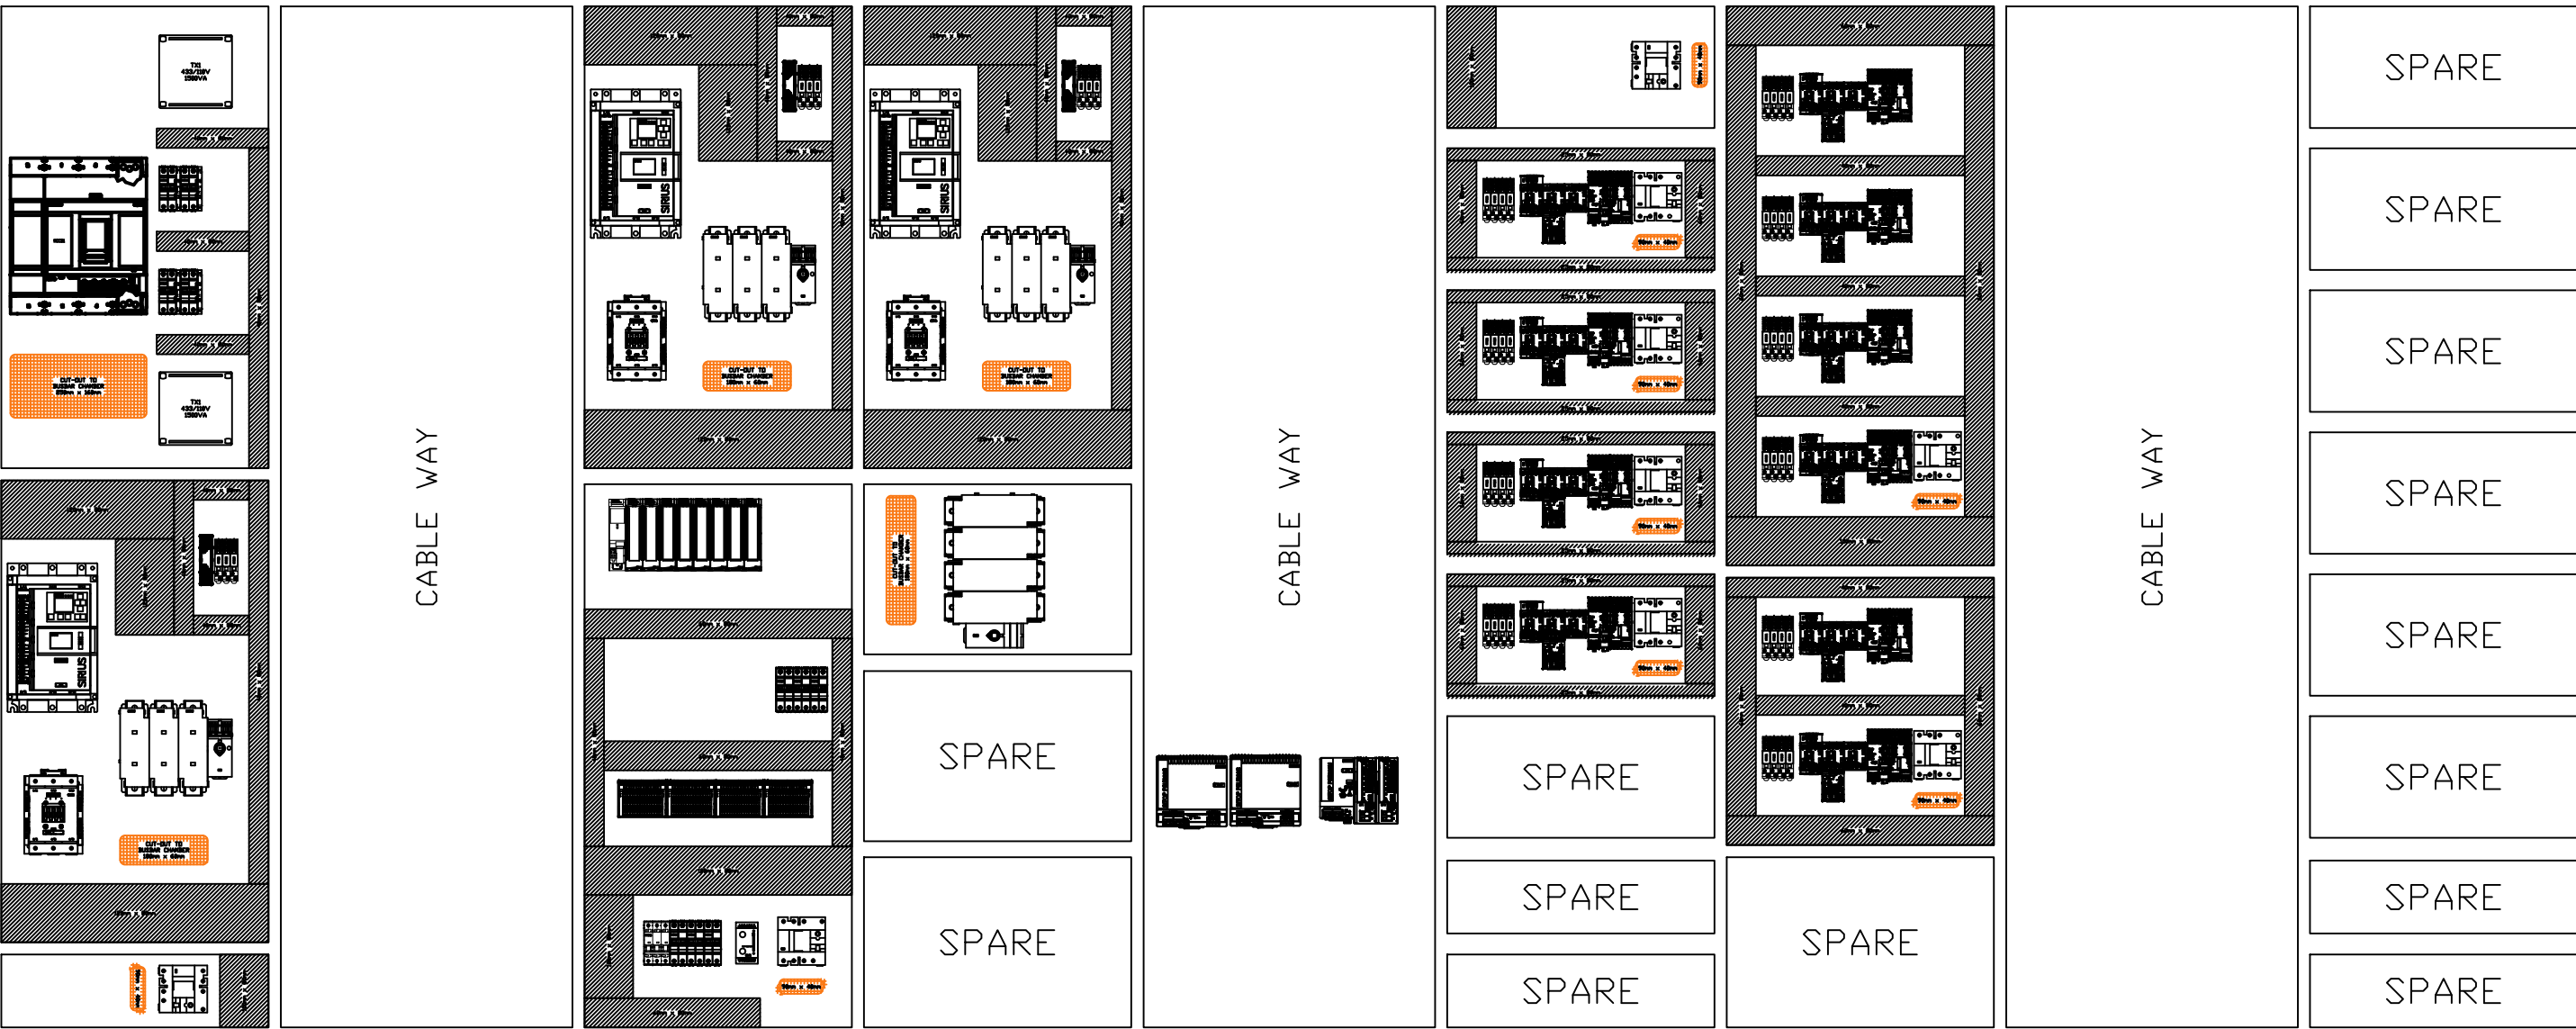

DRAWING STATUS

FIRST DRAFT ☐
FOR MANUFACTURE ☐
SIGNED..... DATED.....

REV	DATE	DETAIL
00	05/07/22	FIRST DRAFT
01	12/02/25	MC2 DUST PLANT FAN ADDED
02		
03		
04		
05		
06		
07		

CLIENT	PEEL PORT
INSTALL	RSGT LIVERPOOL
TITLE	MCC2A WIRING SCHEMATICS

ENGRD. D.BALDOCK DRAWN. D.BALDOCK CHECK M.WRIGHT DATE 12/02/25	 HF Controls Ltd 100 Albert Drive, Glasgow G41 2SJ Tel: +44 (0)141 429 5575 Fax: +44 (0)141 420 1054 email: hf@hfcontrols.co.uk www.hf-group.co.uk
DRG. No.:	284595 / 1002 / 01

MAIN INCOMER
110VAC CONTROL



CUT-OUT TO
BUSBAR CHAMBER
250mm x 160mm

TX1
433/110V
1500VA

TX1
433/110V
1500VA



40mm x 80mm

40mm x 80mm



40mm x 80mm

DRAWING STATUS

FIRST DRAFT ☐
FOR MANUFACTURE ☐
SIGNED..... DATED.....



REV	DATE	DETAIL
00	05/07/22	FIRST DRAFT
01	12/02/25	MC2 DUST PLANT FAN ADDED
02		
03		
04		
05		
06		
07		

TITLE	INSTALL	CLIENT
-------	---------	--------

PEEL PORT

RSGT
LIVERPOOL

MCC2A WIRING SCHEMATICS

ENGRD.	D.BALDOCK
DRAWN.	D.BALDOCK
CHECK	M.WRIGHT
DATE	12/02/25



DRG. No.:

284595 / 1002 / 01



HF Controls Ltd

100 Albert Drive, Glasgow G41 2SJ
Tel: +44 (0)141 429 5575 Fax: +44 (0)141 420 1054
email: hf@hfcontrols.co.uk www.hf-group.co.uk

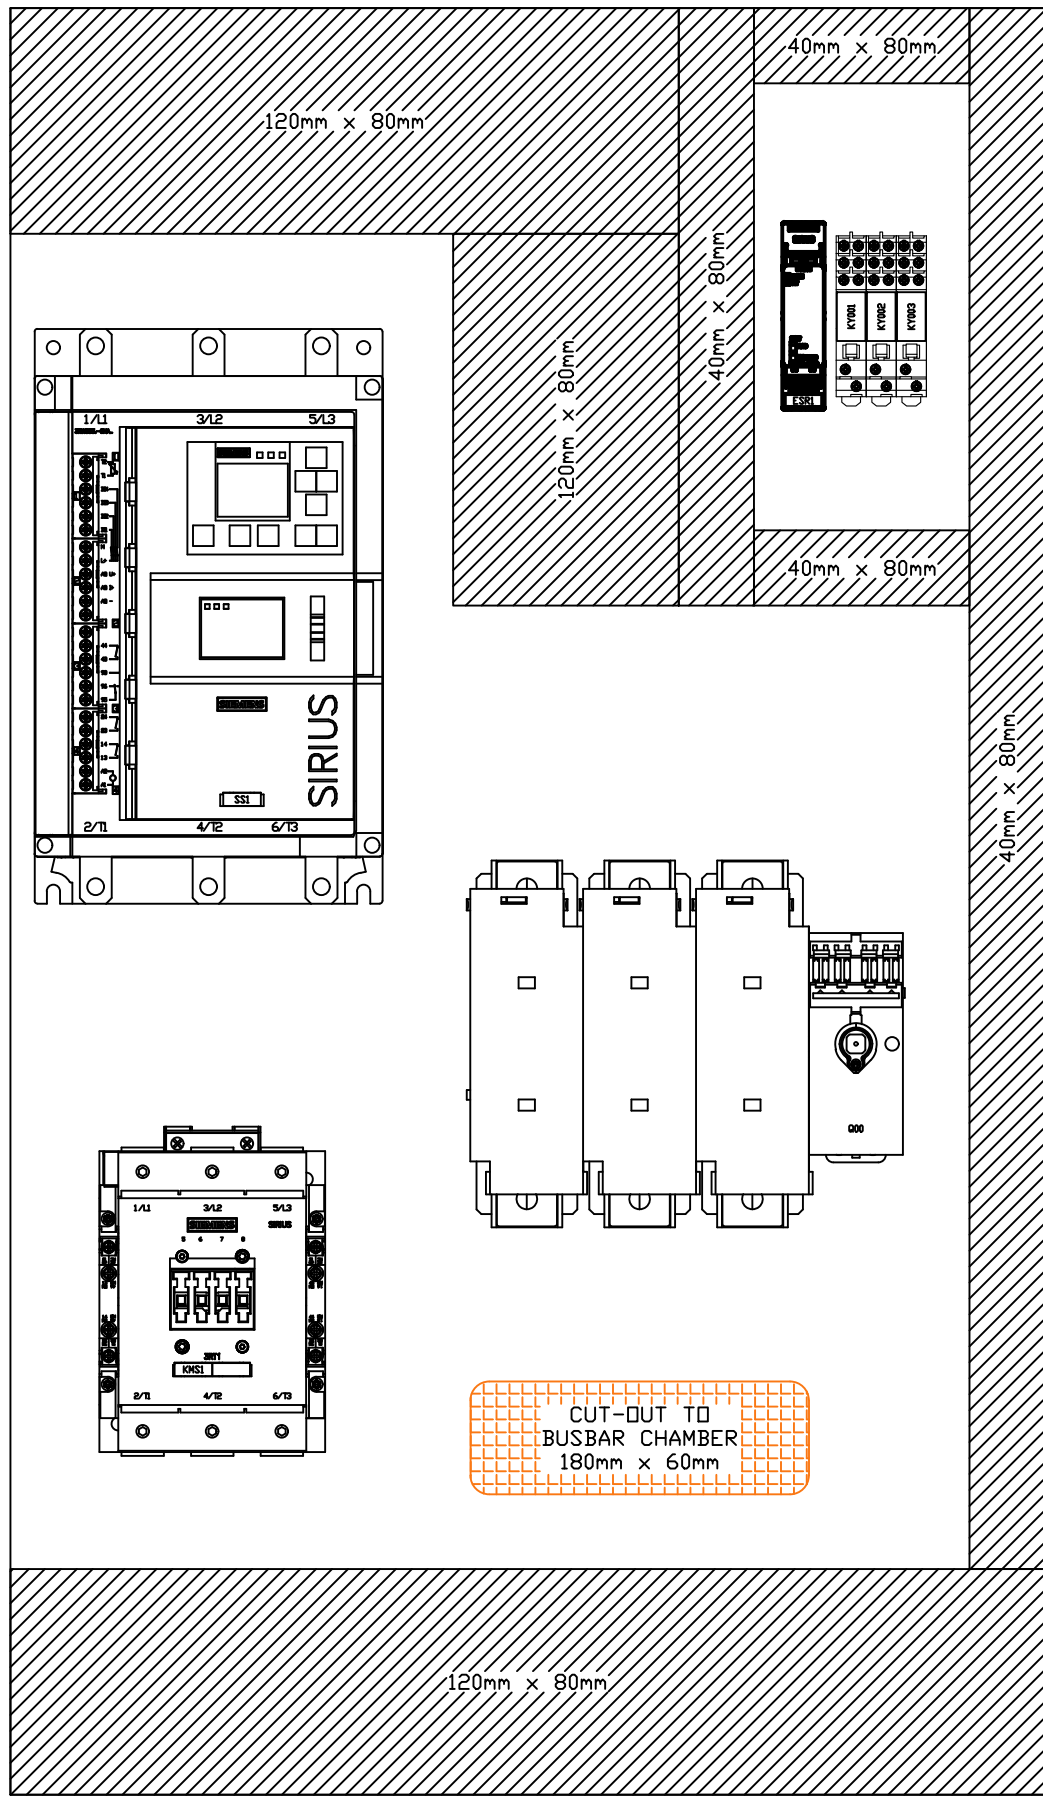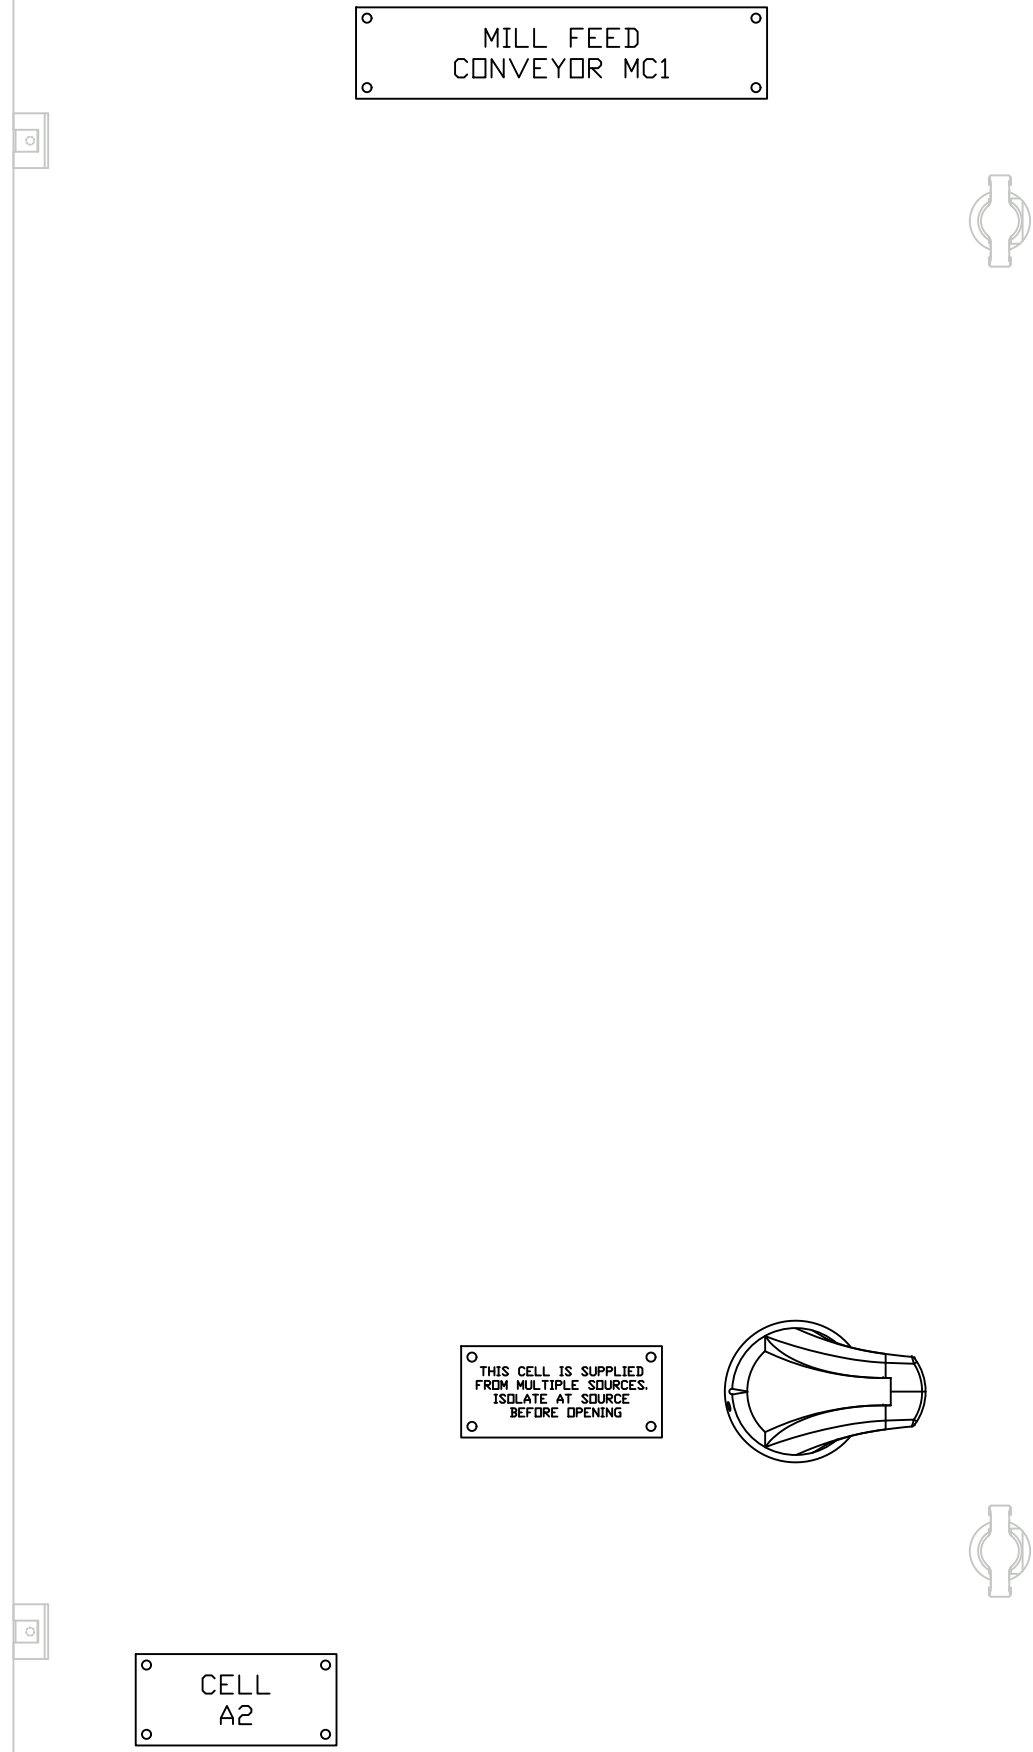

DRAWING STATUS

FIRST DRAFT

FOR MANUFACTURE

SIGNED..... DATED.....

 HF CONTROLS LTD.


© COPYRIGHT HF CONTROLS LTD. 2011

REV	DATE	DETAIL	CLIENT
00	05/07/22	FIRST DRAFT	PEEL PORT
01	12/02/25	MC2 DUST PLANT FAN ADDED	
02			
03			
04			RSGT LIVERPOOL
05			
06			
07			

TITLE	INSTALL	ENGRD.	DRAWN.	CHECK	DATE	DRG. No.:
MCC2A WIRING SCHEMATICS		D.BALDOCK	D.BALDOCK	M.WRIGHT	12/02/25	284595 / 1002 / 01

 HF Controls Ltd

100 Albert Drive, Glasgow G41 2SJ
Tel: +44 (0)141 429 5575 Fax: +44 (0)141 420 1054
email: hf@hfcontrols.co.uk www.hf-group.co.uk

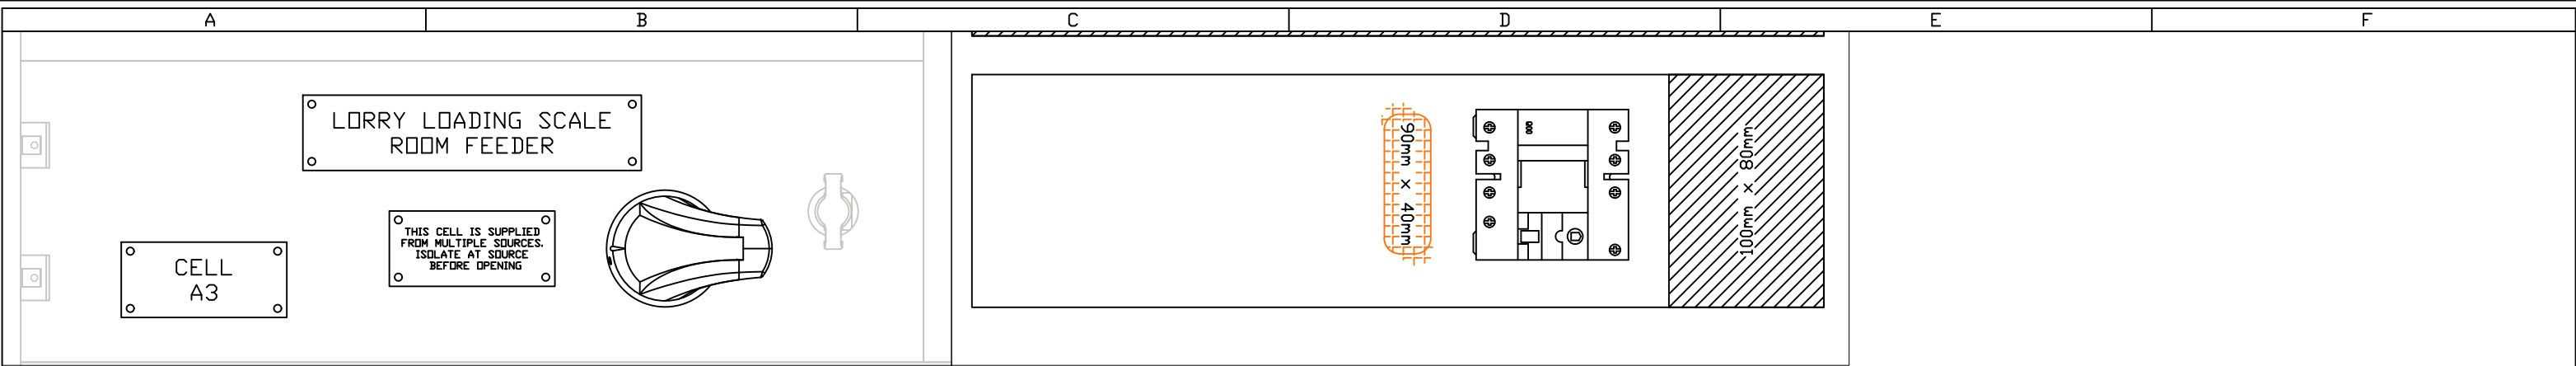

DRAWING STATUS


FIRST DRAFT

FOR MANUFACTURE


SIGNED..... DATED.....

 HF CONTROLS LTD.
© COPYRIGHT HF CONTROLS LTD. 2011

REV	DATE	DETAIL	CLIENT	PEEL PORT	ENGRD.	 HF Controls Ltd 100 Albert Drive, Glasgow G41 2SJ Tel: +44 (0)141 429 5575 Fax: +44 (0)141 420 1054 email: hf@hfcontrols.co.uk www.hf-group.co.uk
00	05/07/22	FIRST DRAFT			DRAWN.	
01	12/02/25	MC2 DUST PLANT FAN ADDED			D.BALDOCK	
02			INSTALL	RSGT LIVERPOOL	CHECK	
03					M.WRIGHT	
04					DATE	
05			TITLE	MCC2A WIRING SCHEMATICS	12/02/25	
06					DRG. No.:	
07					284595 / 1002 / 01	

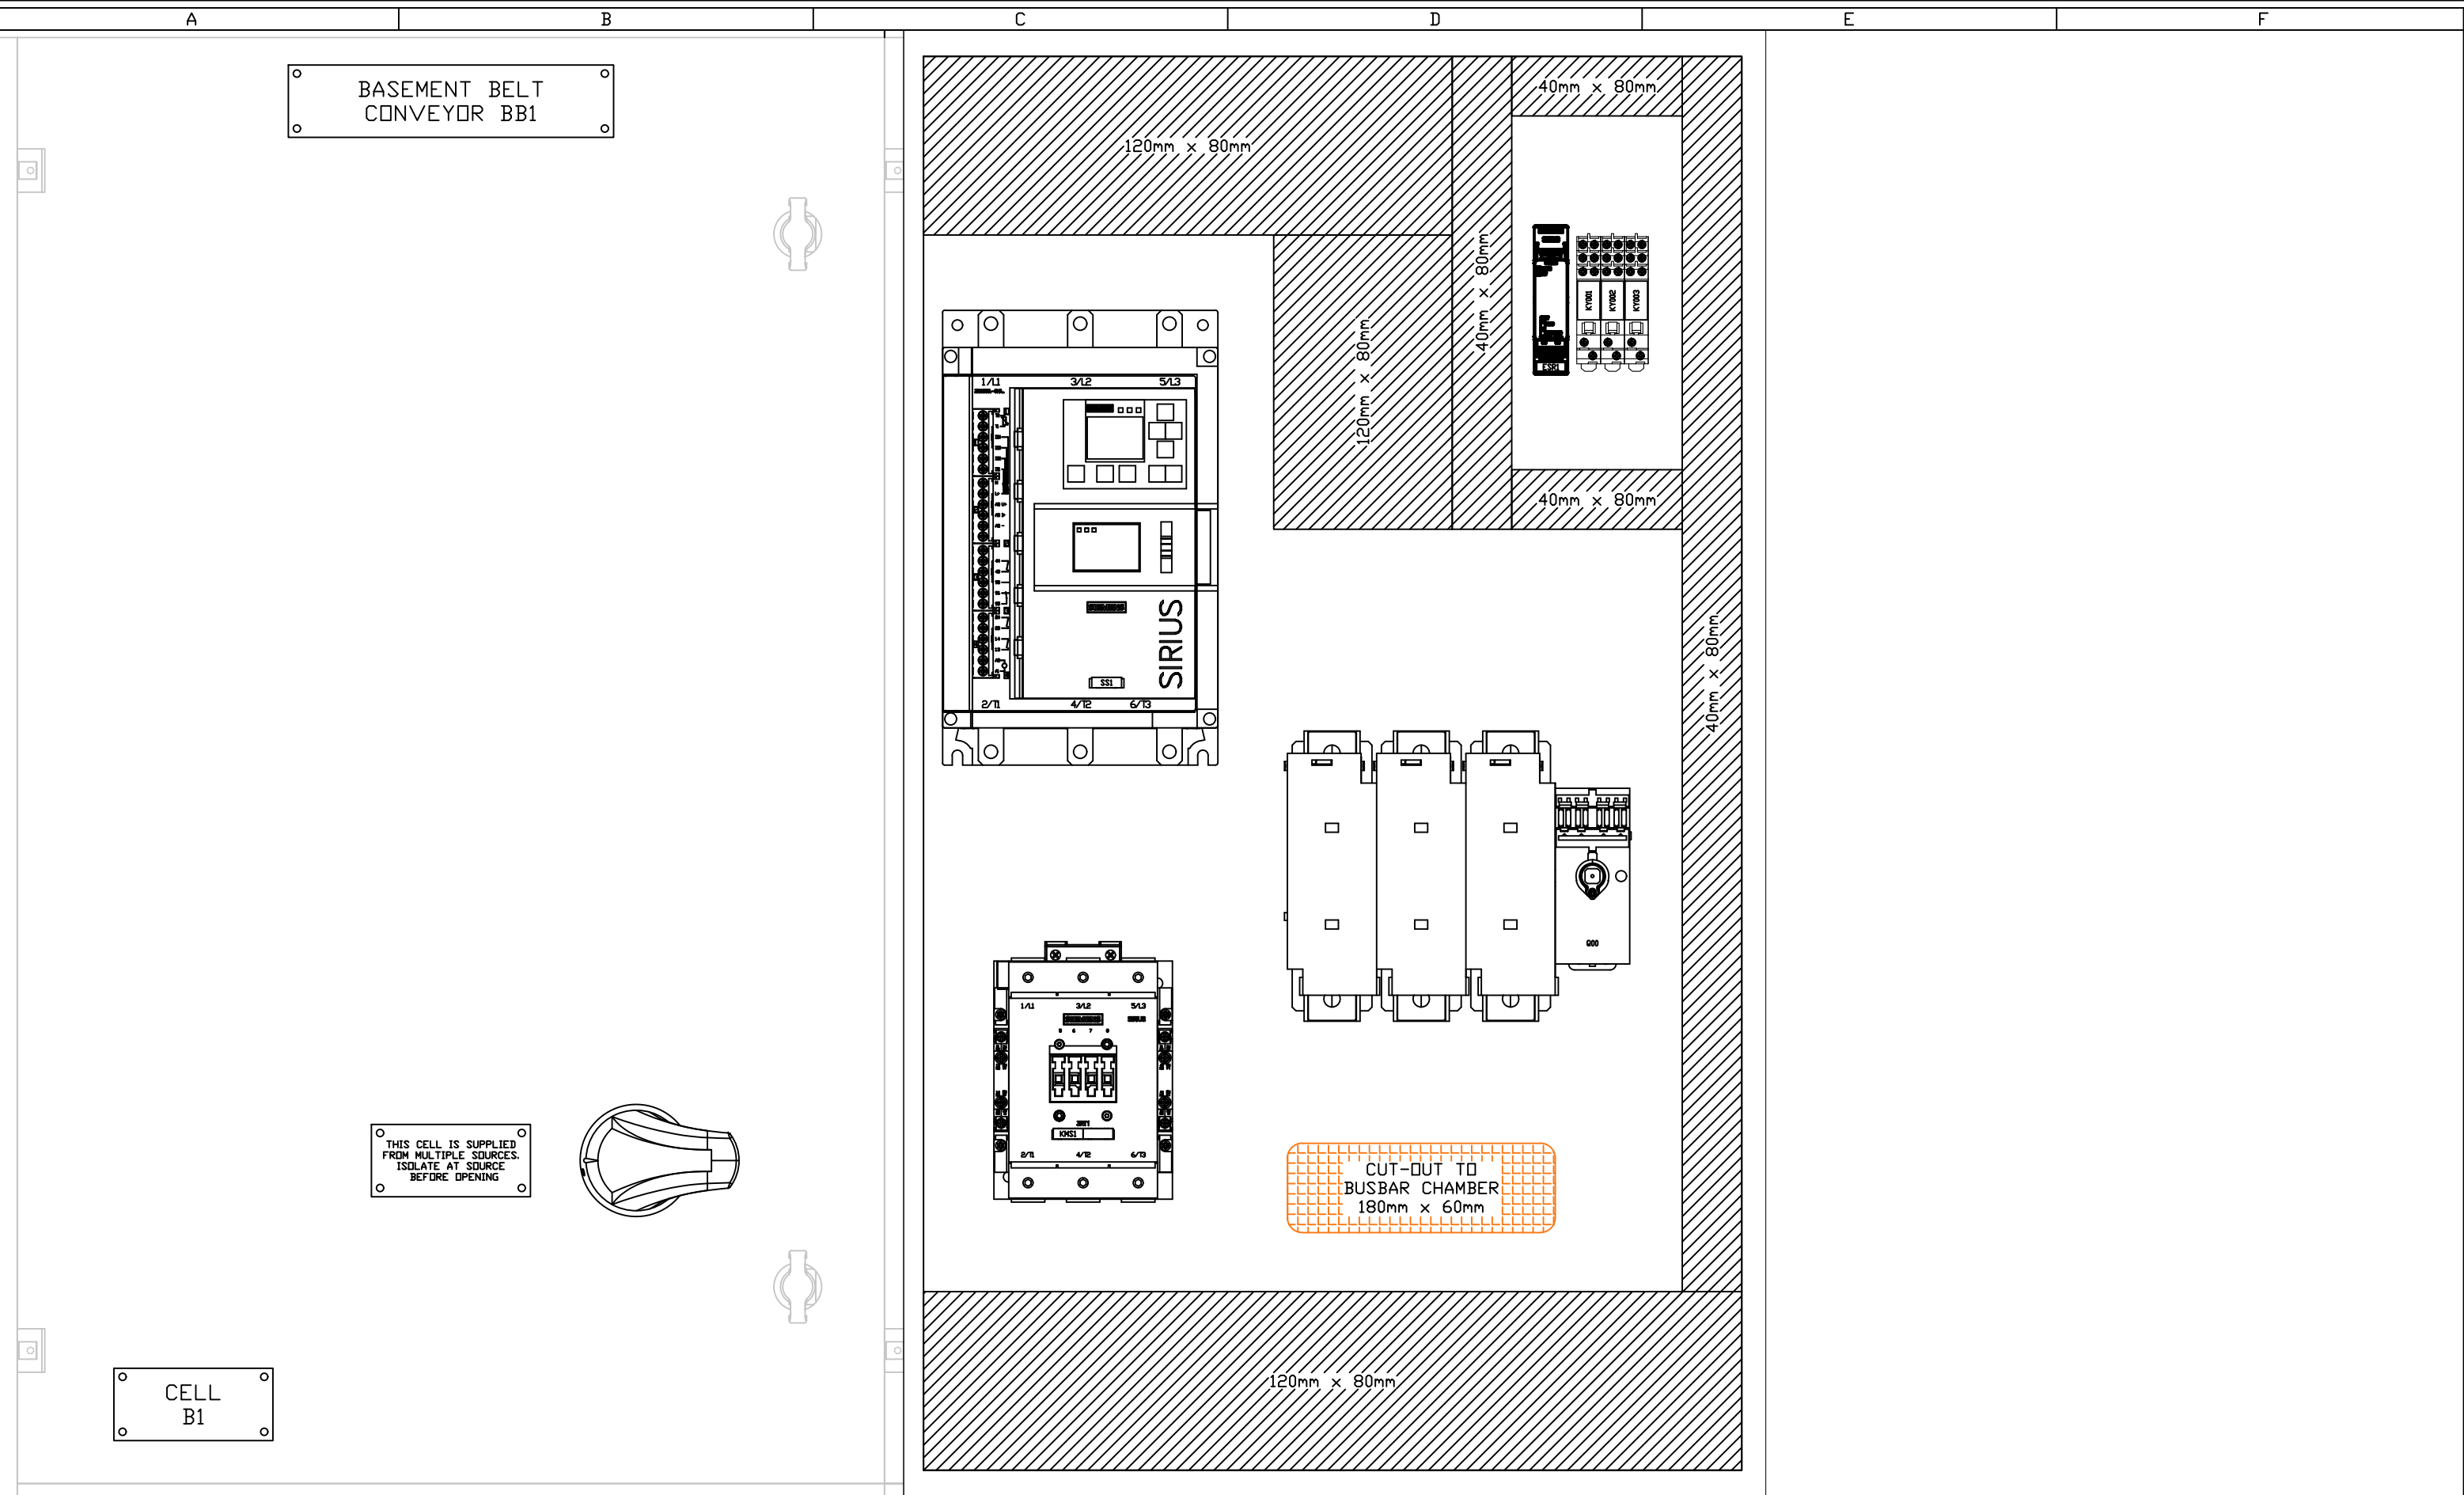

DRAWING STATUS		REV	DATE	DETAIL	CLIENT	PEEL PORT	ENGRD. D.BALDOCK DRAWN. D.BALDOCK	 HF Controls Ltd 100 Albert Drive, Glasgow G41 2SJ Tel: +44 (0)141 429 5575 Fax: +44 (0)141 420 1054 email: hf@hfcontrols.co.uk www.hf-group.co.uk
FIRST DRAFT	☐							
FOR MANUFACTURE	☐	01	12/02/25	MC2 DUST PLANT FAN ADDED	INSTALL	RSGT LIVERPOOL	CHECK M.WRIGHT	DRG. No.: 284595 / 1002 / 01
SIGNED..... DATED.....		02					DATE 12/02/25	
 HF CONTROLS LTD. © COPYRIGHT HF CONTROLS LTD. 2011		03			TITLE	MCC2A WIRING SCHEMATICS		
		04						
		05						
		06						
		07						

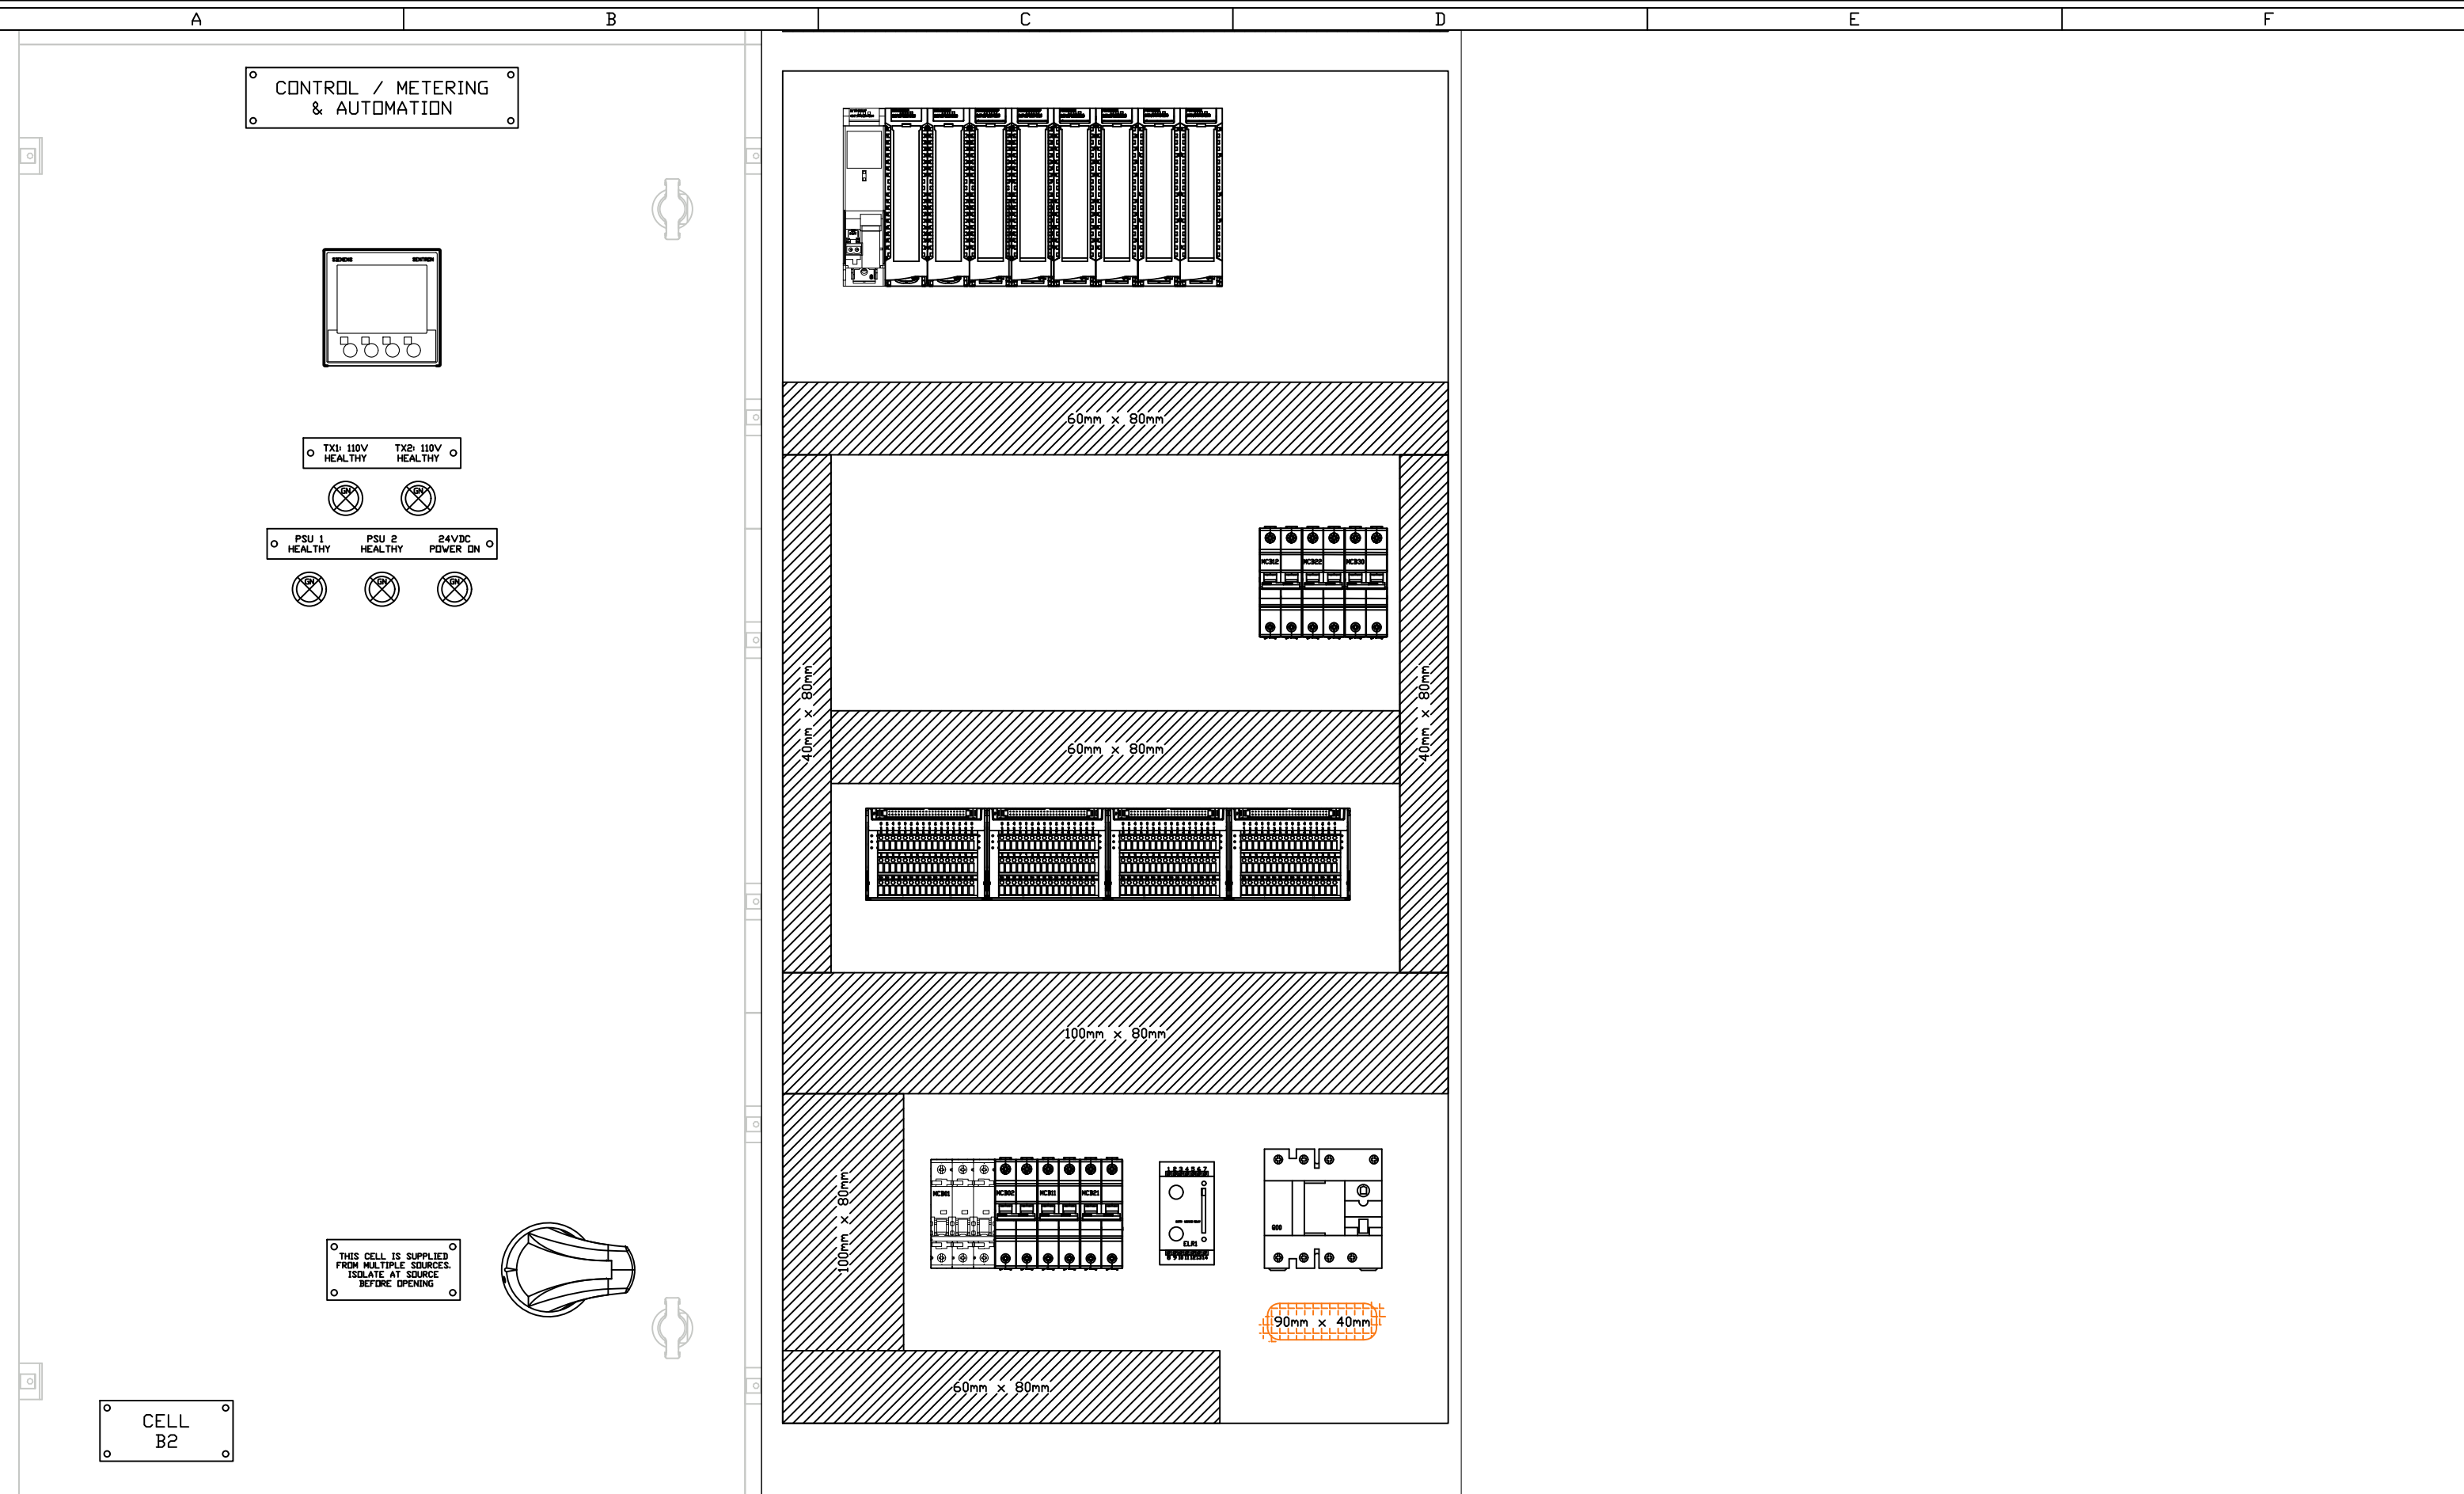

DRAWING STATUS

FIRST DRAFT

FOR MANUFACTURE

SIGNED..... DATED.....

 HF CONTROLS LTD.

© COPYRIGHT HF CONTROLS LTD. 2011

REV	DATE	DETAIL
00	05/07/22	FIRST DRAFT
01	12/02/25	MC2 DUST PLANT FAN ADDED
02		
03		
04		
05		
06		
07		

TITLE	INSTALL	CLIENT
MCC2A WIRING SCHEMATICS	RSGT LIVERPOOL	PEEL PORT

ENGRD.
D.BALDOCK

DRAWN.
D.BALDOCK

CHECK
M.WRIGHT


DATE
12/02/25

DRG. No.:

284595 / 1002 / 01


HF Controls Ltd
100 Albert Drive, Glasgow G41 2SJ
Tel: +44 (0)141 429 5575 Fax: +44 (0)141 420 1054
email: hf@hfcontrols.co.uk www.hf-group.co.uk



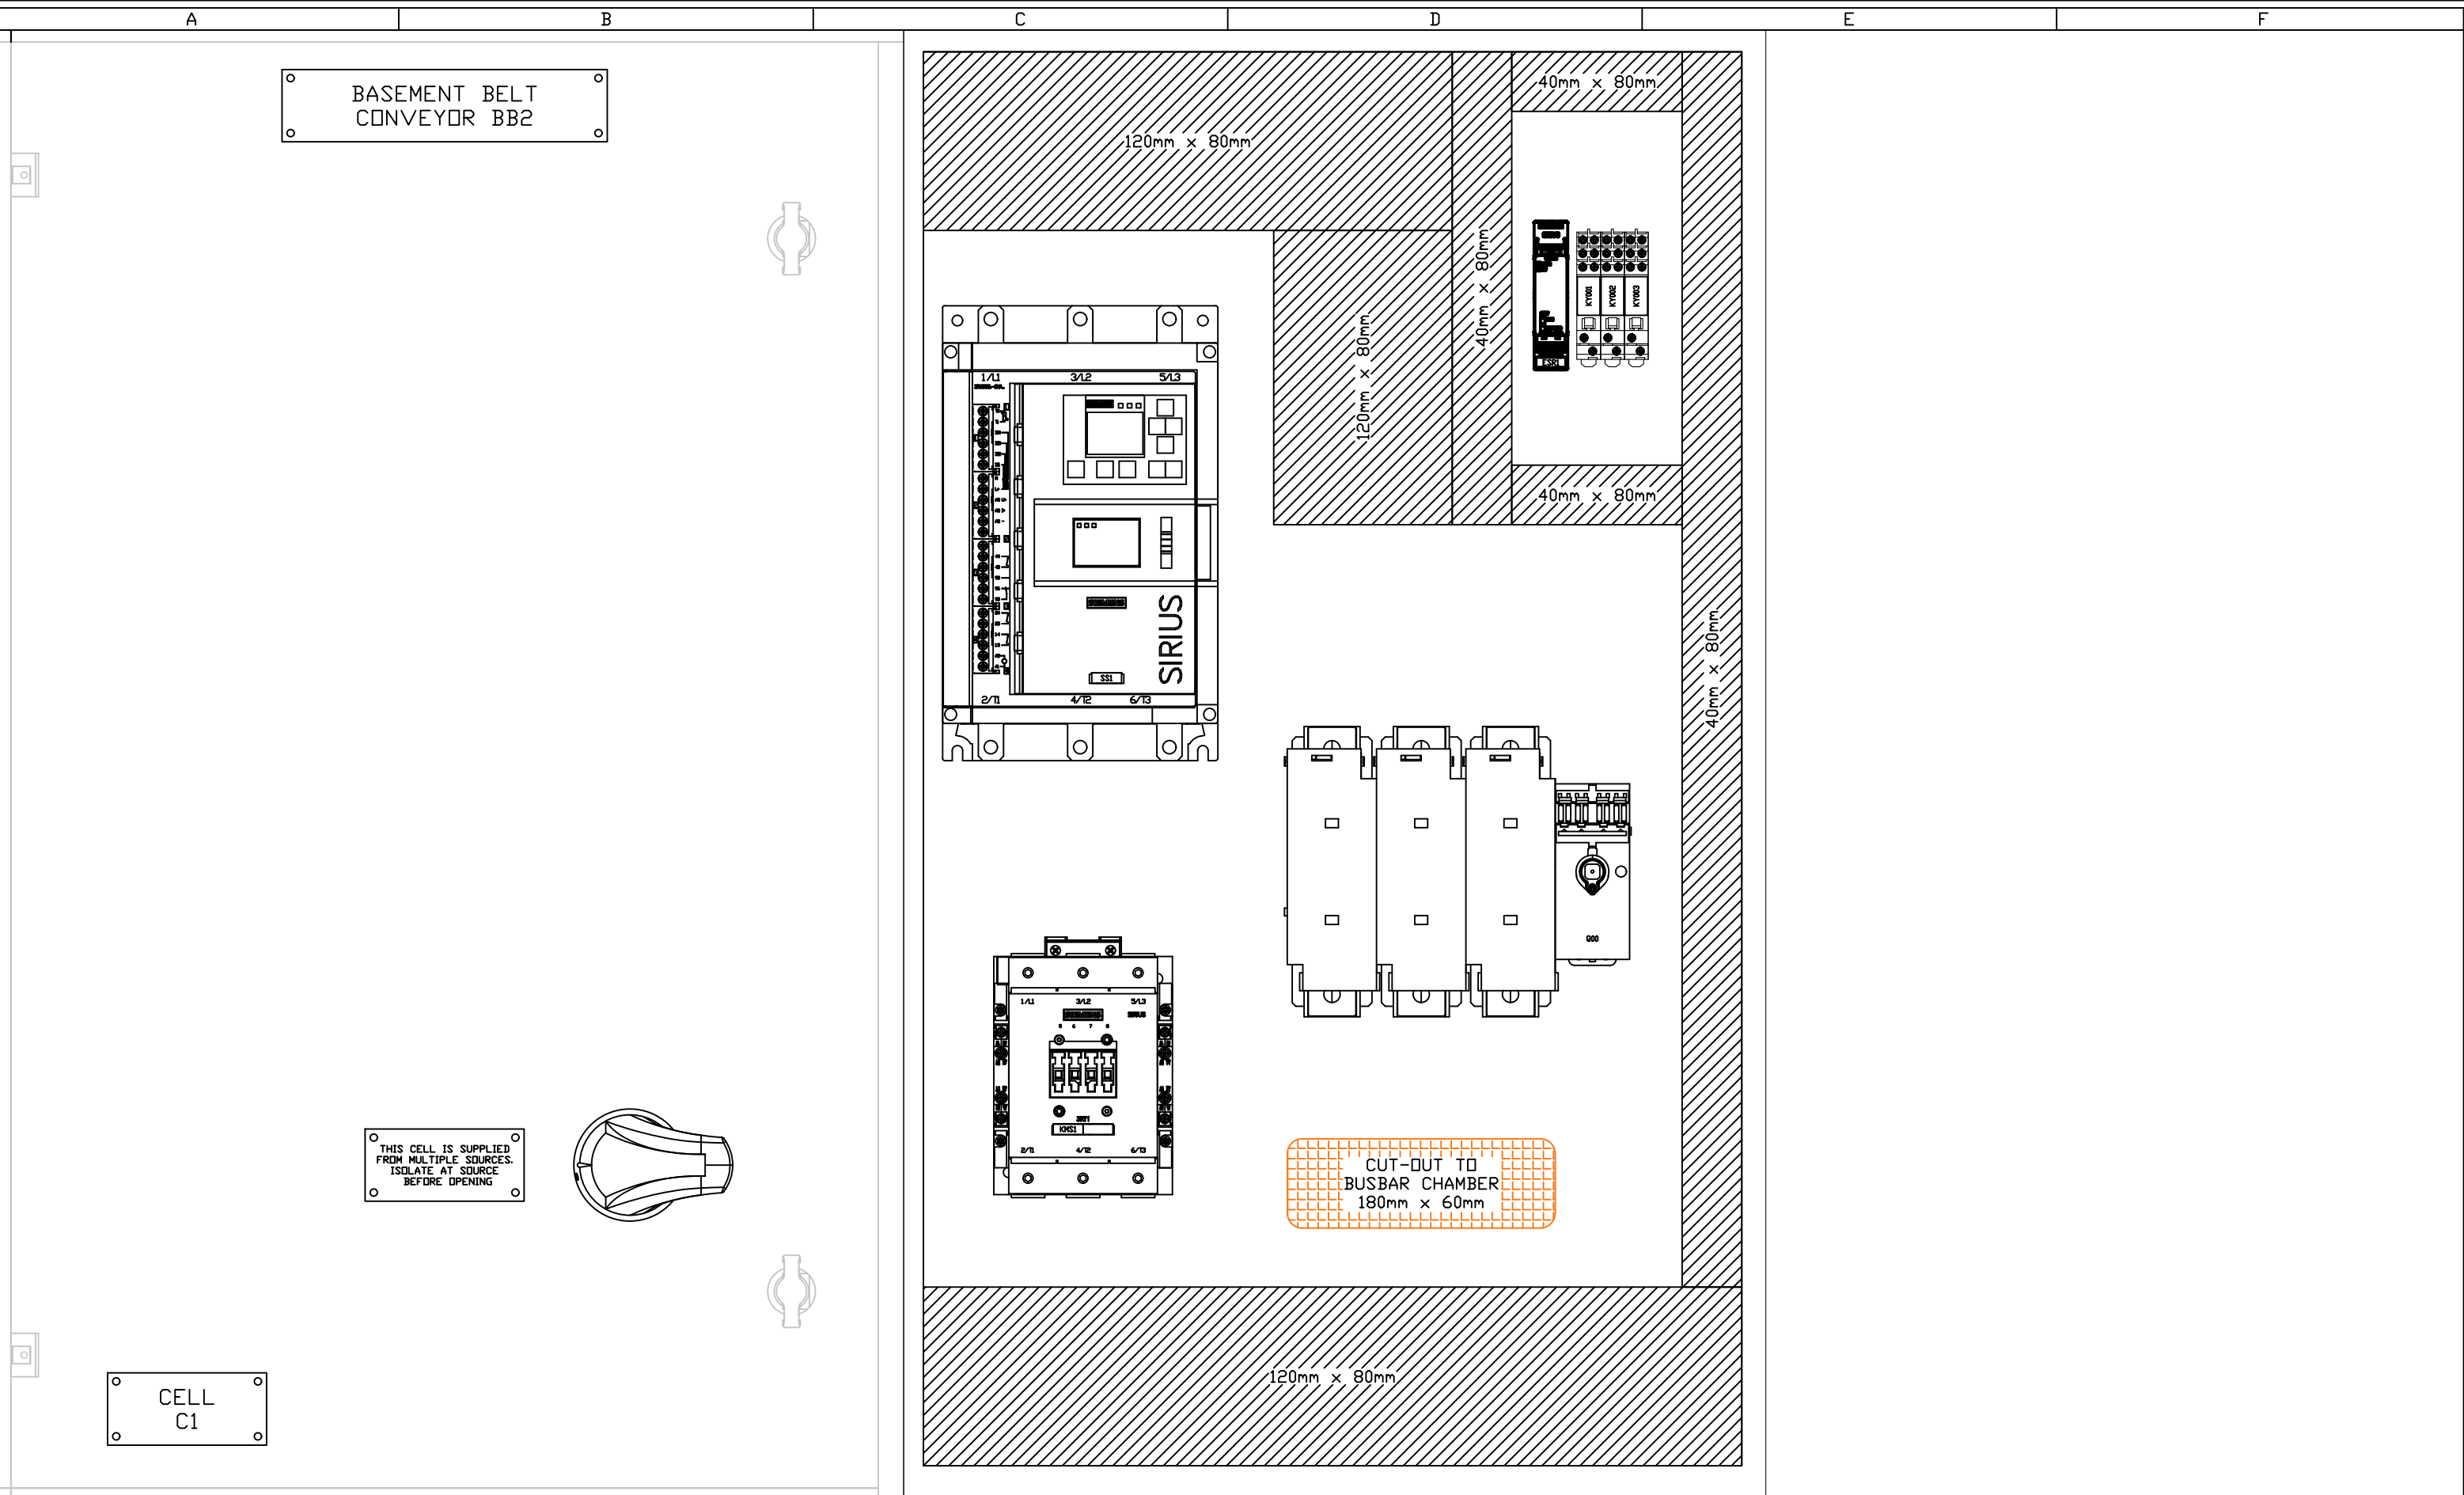

DRAWING STATUS

FIRST DRAFT ☐
FOR MANUFACTURE ☐
SIGNED..... DATED.....


 HF CONTROLS LTD.
© COPYRIGHT HF CONTROLS LTD. 2011

REV	DATE	DETAIL	CLIENT
00	05/07/22	FIRST DRAFT	INSTALL
01	12/02/25	MC2 DUST PLANT FAN ADDED	
02			
03			
04			TITLE
05			
06			
07			

PEEL PORT	ENGRD. D.BALDOCK DRAWN. D.BALDOCK CHECK M.WRIGHT DATE 12/02/25
RSGT LIVERPOOL	
MCC2A WIRING SCHEMATICS	DRG. No.: 284595 / 1002 / 01



HF Controls Ltd
100 Albert Drive, Glasgow G41 2SJ
Tel: +44 (0)141 429 5575 Fax: +44 (0)141 420 1054
email: hf@hfcontrols.co.uk www.hf-group.co.uk

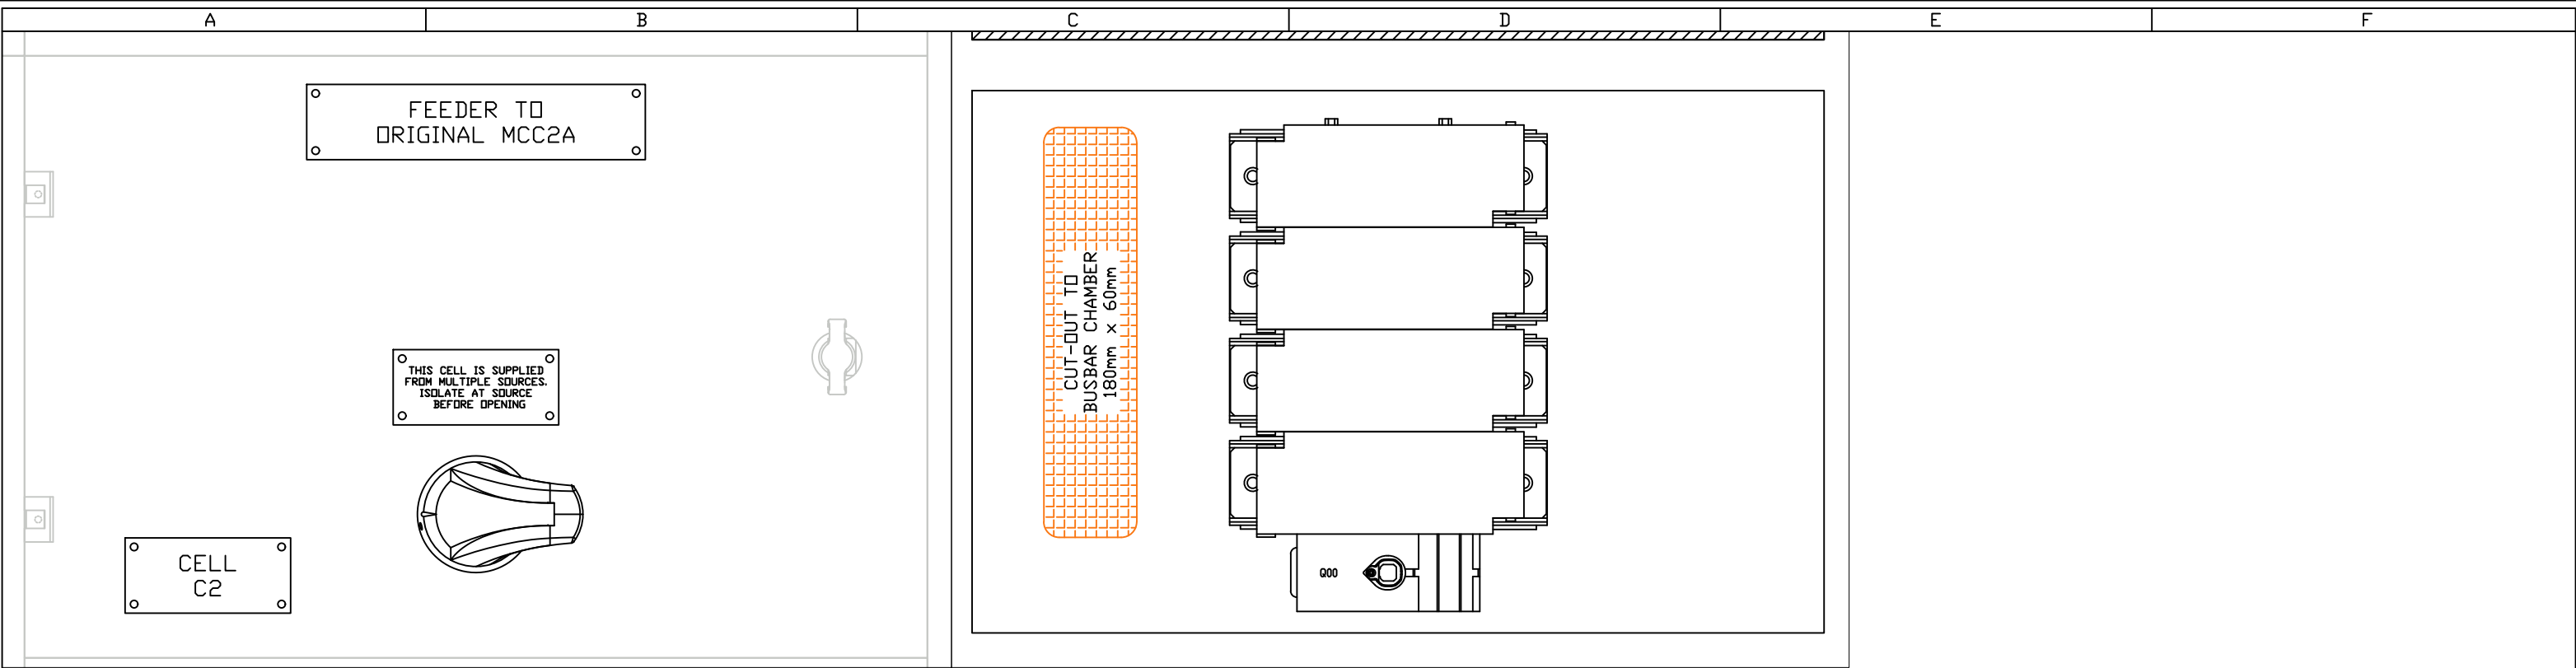

DRAWING STATUS

FIRST DRAFT

FOR MANUFACTURE


SIGNED..... DATED.....

 HF CONTROLS LTD.
© COPYRIGHT HF CONTROLS LTD. 2011


REV	DATE	DETAIL
00	05/07/22	FIRST DRAFT
01	12/02/25	MC2 DUST PLANT FAN ADDED
02		
03		
04		
05		
06		
07		

CLIENT	PEEL PORT	ENGRD. D.BALDOCK
		DRAWN. D.BALDOCK
INSTALL	RSGT LIVERPOOL	CHECK M.WRIGHT
		DATE 12/02/25
TITLE	MCC2A WIRING SCHEMATICS	DRG. No.: 284595 / 1002 / 01


HF Controls Ltd
100 Albert Drive, Glasgow G41 2SJ
Tel: +44 (0)141 429 5575 Fax: +44 (0)141 420 1054
email: hf@hfcontrols.co.uk www.hf-group.co.uk

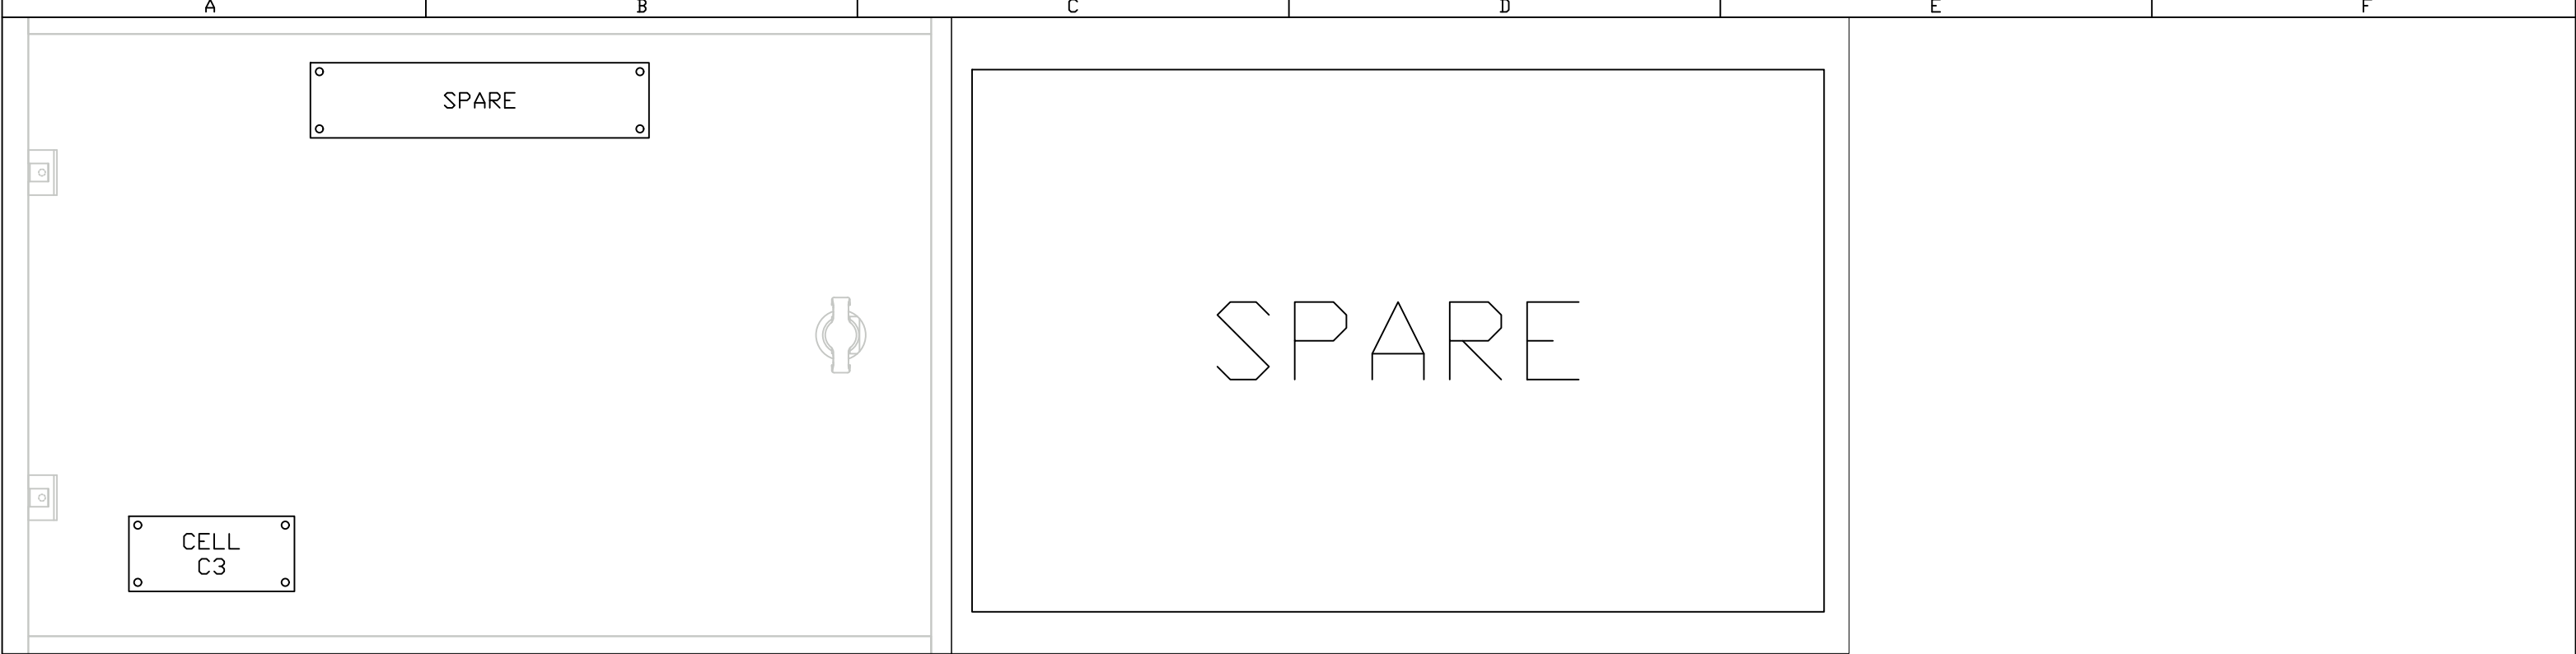

DRAWING STATUS		REV		DATE	DETAIL	CLIENT	PEEL PORT	ENGRD. D.BALDOCK	 HF Controls Ltd 100 Albert Drive, Glasgow G41 2SJ Tel: +44 (0)141 429 5575 Fax: +44 (0)141 420 1054 email: hf@hfcontrols.co.uk www.hf-group.co.uk
FIRST DRAFT	☐	00	05/07/22	FIRST DRAFT				DRAWN. D.BALDOCK	
FOR MANUFACTURE	☐	01	12/02/25	MC2 DUST PLANT FAN ADDED					
SIGNED.....	DATED.....	02				INSTALL	RSGT LIVERPOOL	CHECK M.WRIGHT	
		03						DATE 12/02/25	
		04							
		05				TITLE	MCC2A WIRING SCHEMATICS	DRG. No.:	
		06						284595 / 1002 / 01	
		07							

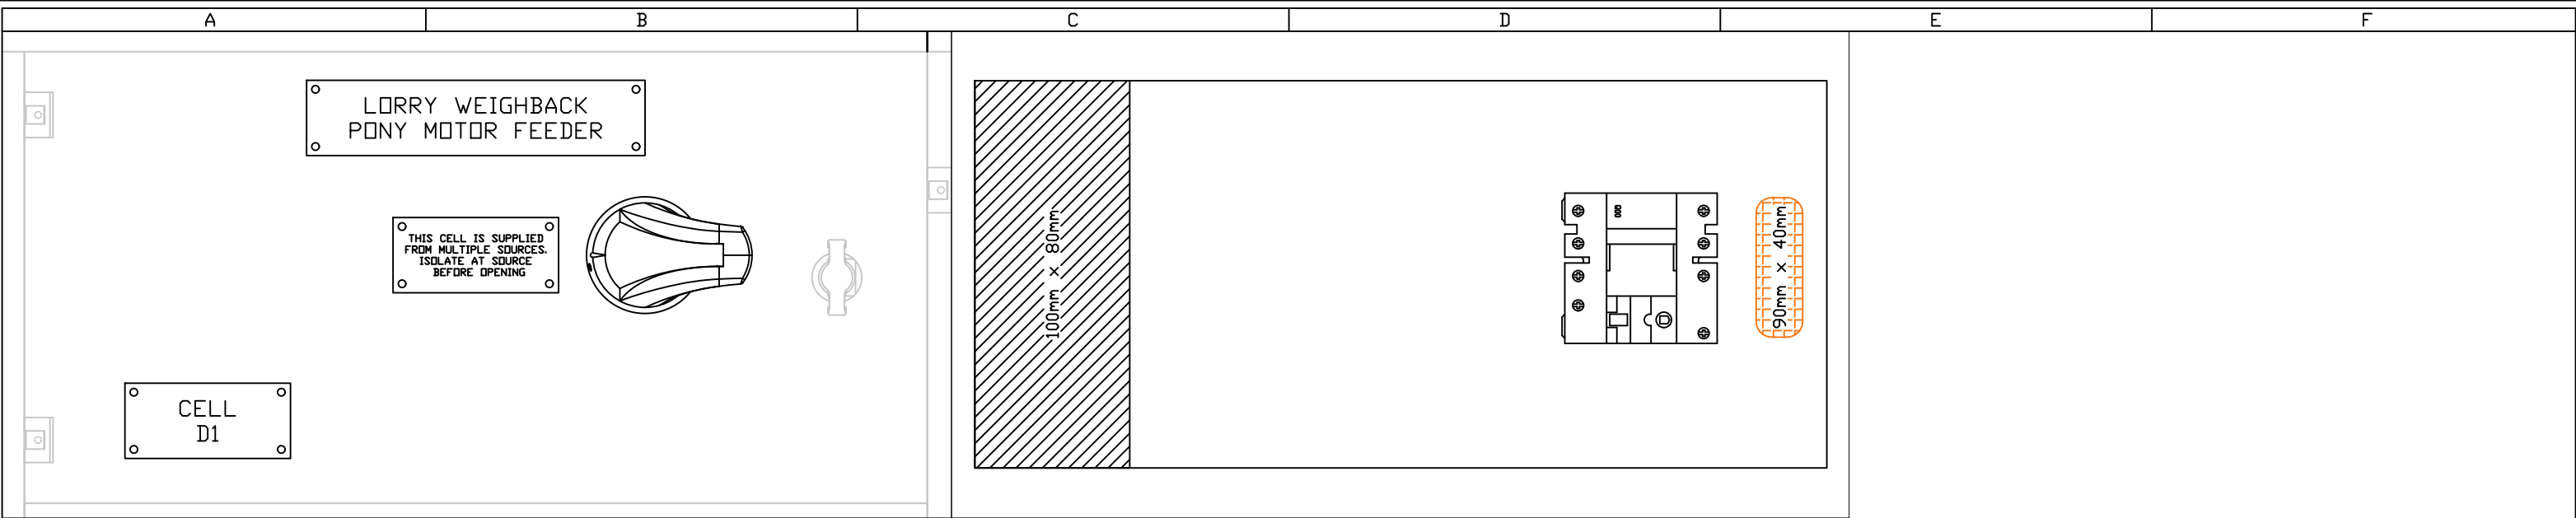

DRAWING STATUS	
FIRST DRAFT	☐
FOR MANUFACTURE	☐
SIGNED.....	DATED.....
 HF CONTROLS LTD. © COPYRIGHT HF CONTROLS LTD. 2011	


REV	DATE	DETAIL
00	05/07/22	FIRST DRAFT
01	12/02/25	MC2 DUST PLANT FAN ADDED
02		
03		
04		
05		
06		
07		

CLIENT	PEEL PORT	ENGRD. D.BALDOCK
		DRAWN. D.BALDOCK
INSTALL	RSGT LIVERPOOL	CHECK M.WRIGHT
		DATE 12/02/25
TITLE	MCC2A WIRING SCHEMATICS	DRG. No.: 284595 / 1002 / 01



HF Controls Ltd
100 Albert Drive, Glasgow G41 2SJ
Tel: +44 (0)141 429 5575 Fax: +44 (0)141 420 1054
email: hf@hfcontrols.co.uk www.hf-group.co.uk



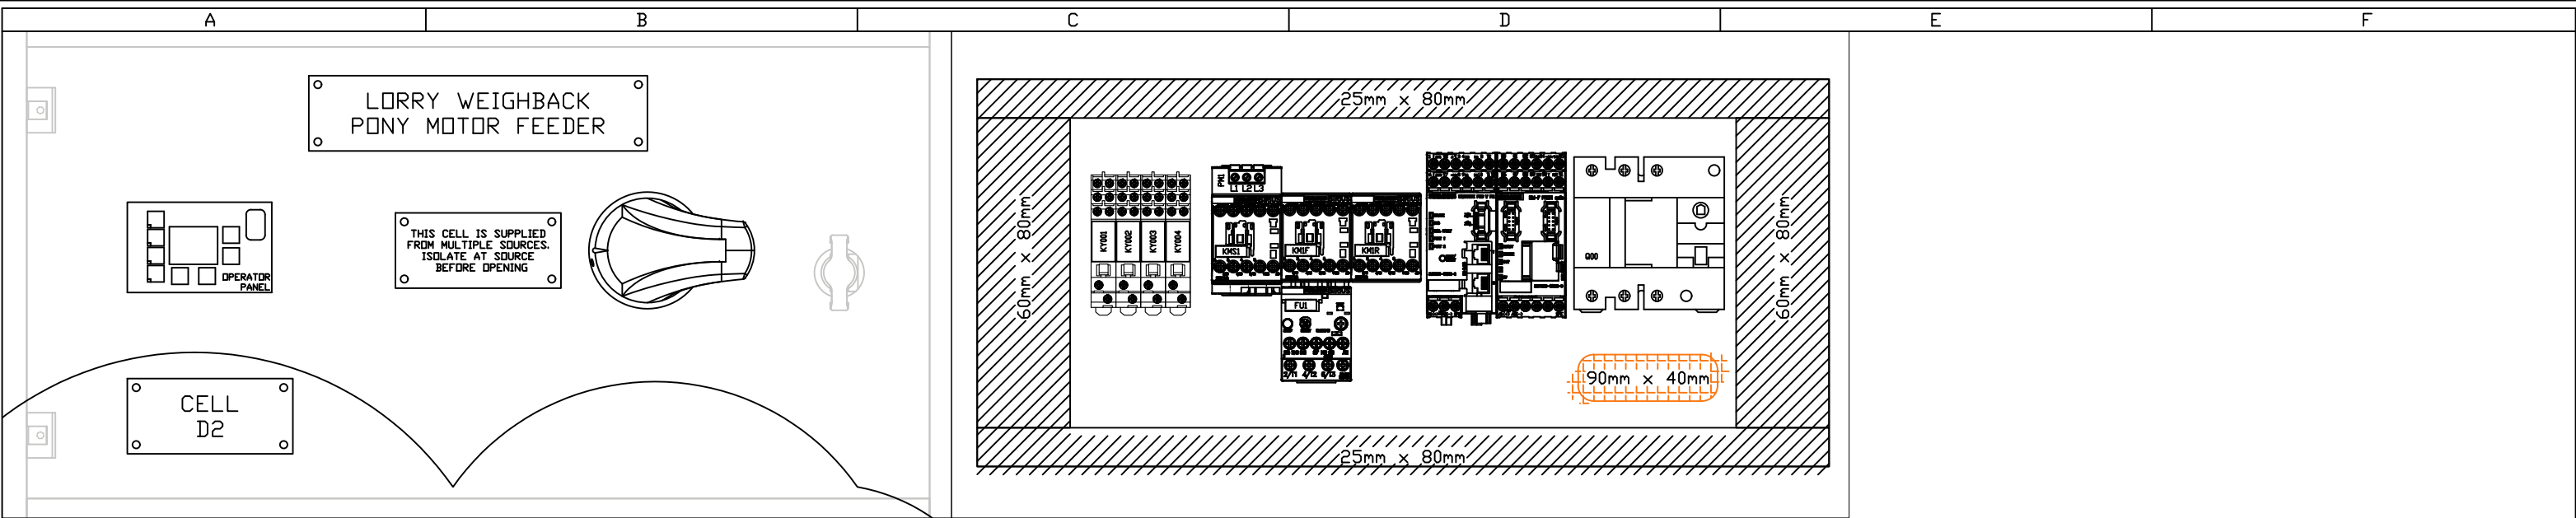

DRAWING STATUS


FIRST DRAFT

FOR MANUFACTURE

SIGNED..... DATED.....

 HF CONTROLS LTD.
© COPYRIGHT HF CONTROLS LTD. 2011

REV	DATE	DETAIL	CLIENT	PEEL PORT	ENGRD.	 HF Controls Ltd 100 Albert Drive, Glasgow G41 2SJ Tel: +44 (0)141 429 5575 Fax: +44 (0)141 420 1054 email: hf@hfcontrols.co.uk www.hf-group.co.uk
00	05/07/22	FIRST DRAFT			DRAWN.	
01	12/02/25	MC2 DUST PLANT FAN ADDED			D.BALDOCK	
02			INSTALL	RSGT LIVERPOOL	CHECK	
03					M.WRIGHT	
04					DATE	
					12/02/25	
05			TITLE	MCC2A WIRING SCHEMATICS	DRG. No.:	
06					284595 / 1002 / 01	
07						

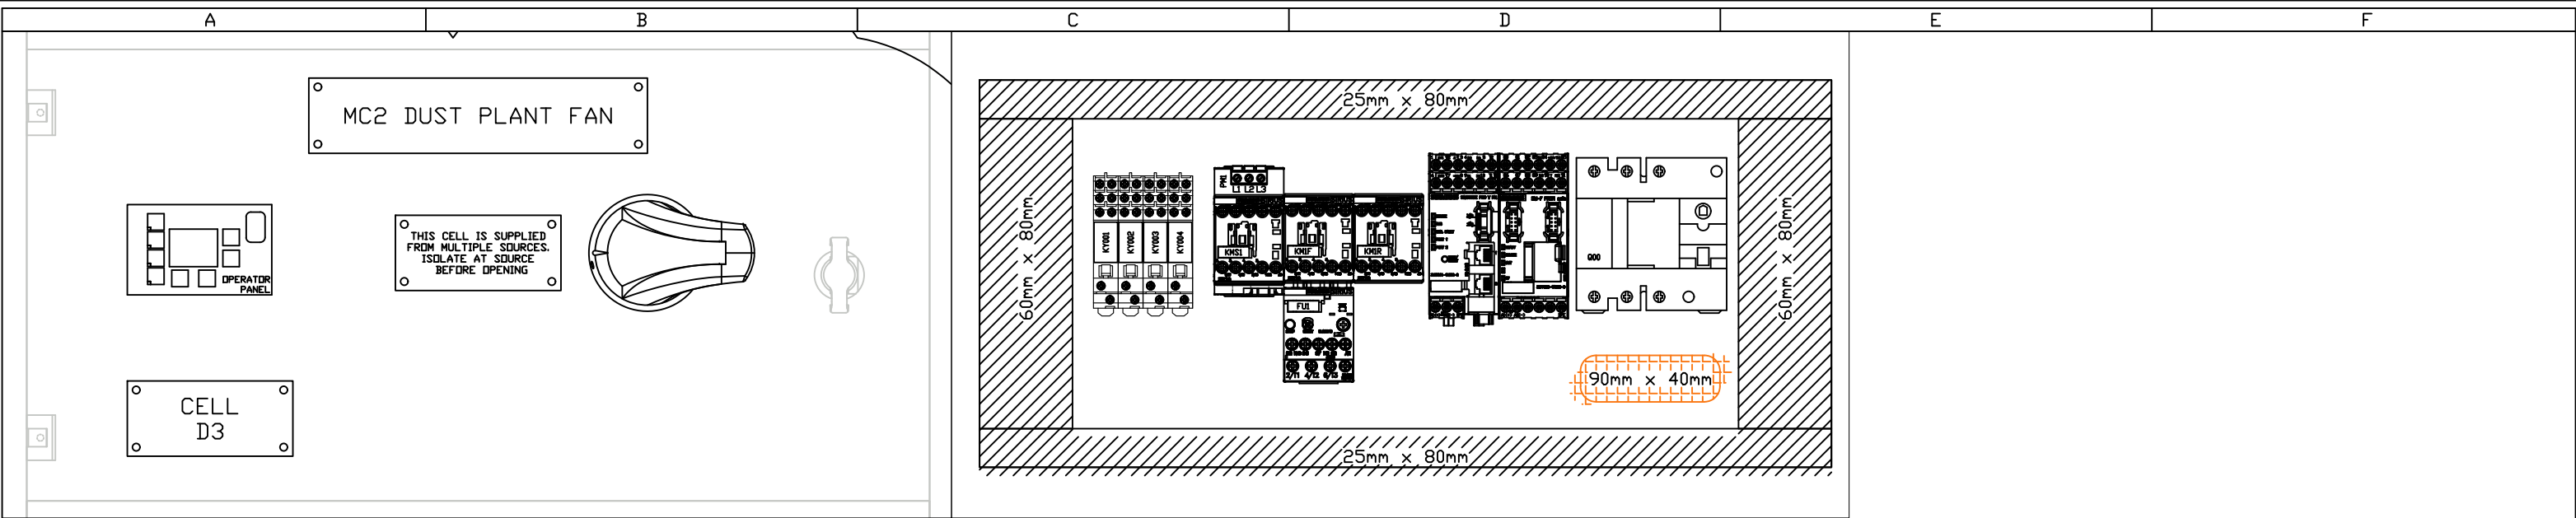

DRAWING STATUS

FIRST DRAFT

FOR MANUFACTURE

SIGNED..... DATED.....


 HF CONTROLS LTD.
© COPYRIGHT HF CONTROLS LTD. 2011

REV	DATE	DETAIL	CLIENT
00	05/07/22	FIRST DRAFT	
01	12/02/25	MC2 DUST PLANT FAN ADDED	
02			
03			INSTALL
04			
05			
06			
07			TITLE

PEEL PORT	ENGRD. D.BALDOCK
	DRAWN. D.BALDOCK
	CHECK M.WRIGHT
	DATE 12/02/25
RSGT LIVERPOOL	
MCC2A WIRING SCHEMATICS	


HF Controls Ltd
100 Albert Drive, Glasgow G41 2SJ
Tel: +44 (0)141 429 5575 Fax: +44 (0)141 420 1054
email: hf@hfcontrols.co.uk www.hf-group.co.uk

DRG. No.:
284595 / 1002 / 01

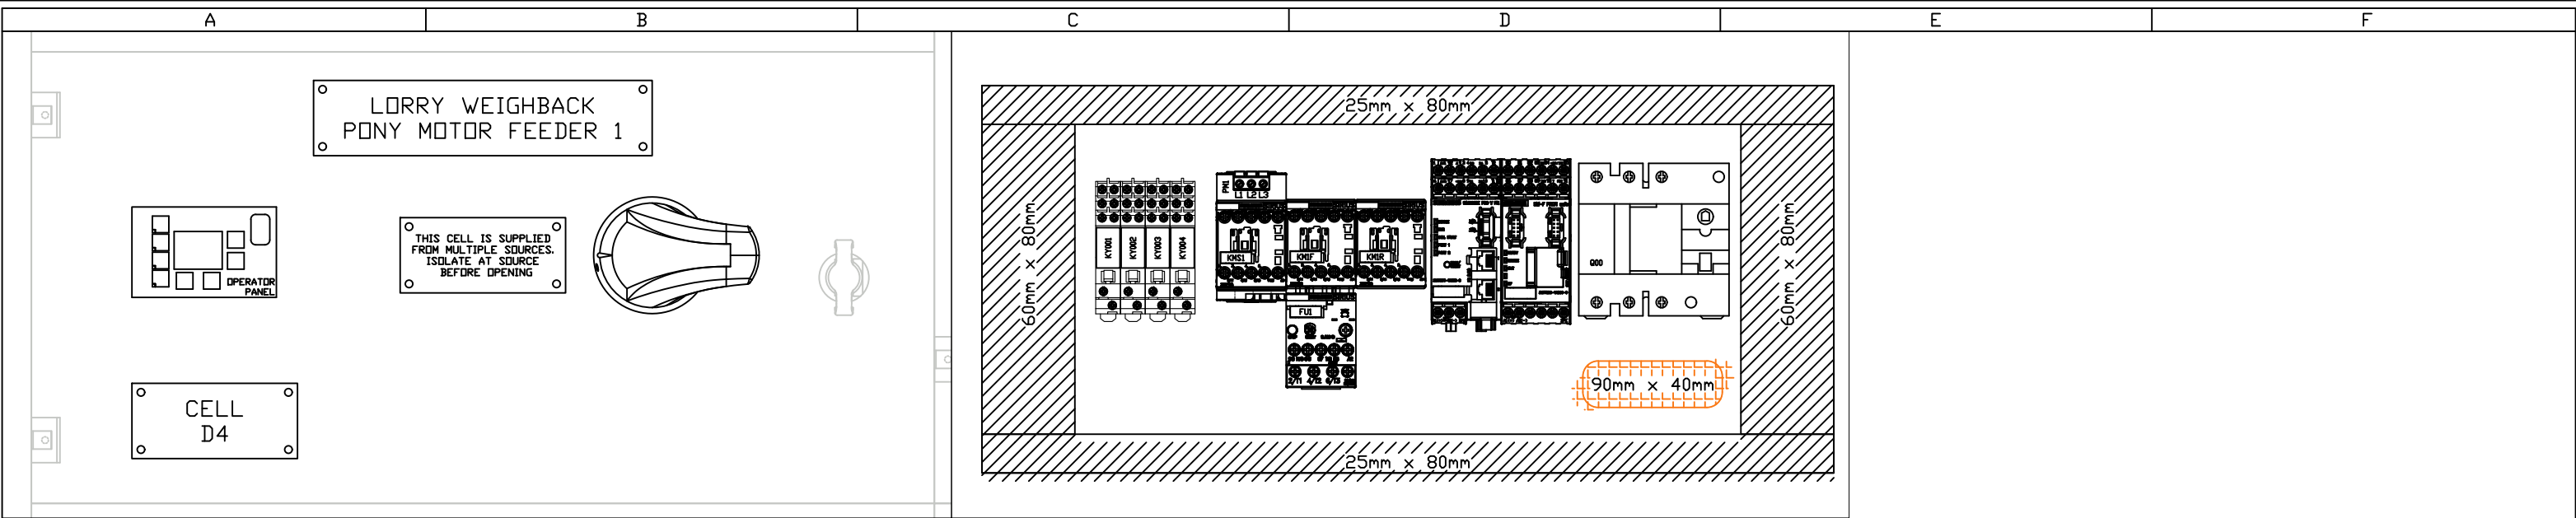

DRAWING STATUS	
FIRST DRAFT	☐
FOR MANUFACTURE	☐
SIGNED.....	DATED.....
 HF CONTROLS LTD. © COPYRIGHT HF CONTROLS LTD. 2011	


REV	DATE	DETAIL	CLIENT
00	05/07/22	FIRST DRAFT	PEEL PORT
01	12/02/25	MC2 DUST PLANT FAN ADDED	
02			
03			
04			
05			RSGT LIVERPOOL
06			
07			

TITLE	INSTALL	ENGRD.	DRAWN.	CHECK	DATE
MCC2A WIRING SCHEMATICS		D.BALDOCK	D.BALDOCK	M.WRIGHT	12/02/25



HF Controls Ltd
100 Albert Drive, Glasgow G41 2SJ
Tel: +44 (0)141 429 5575 Fax: +44 (0)141 420 1054
email: hf@hfcontrols.co.uk www.hf-group.co.uk

DRG. No.:
284595 / 1002 / 01

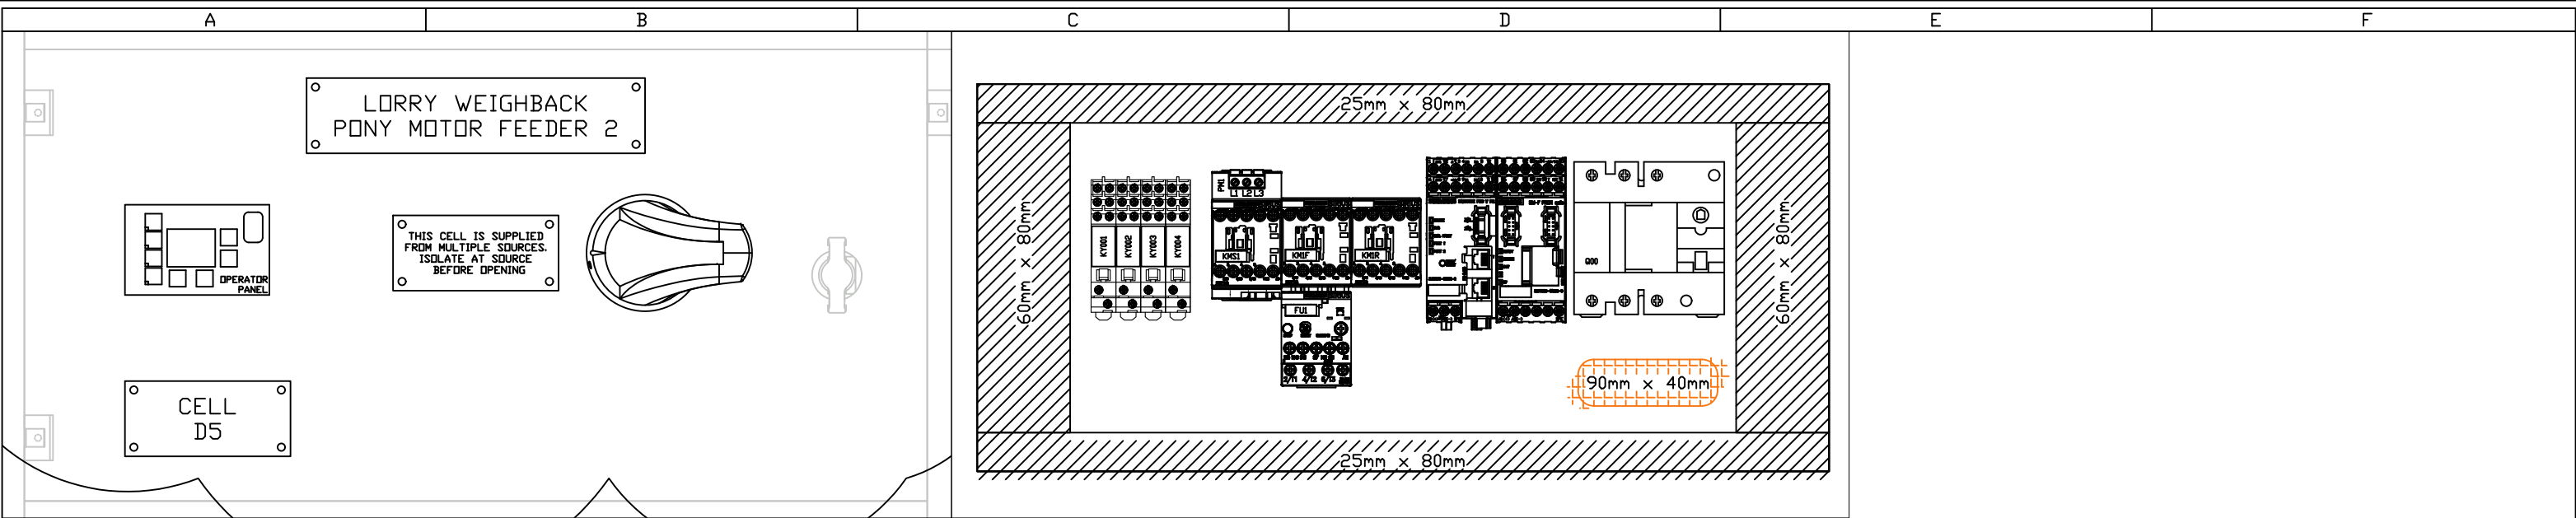

DRAWING STATUS

FIRST DRAFT ☐

FOR MANUFACTURE ☐


SIGNED..... DATED.....

 HF CONTROLS LTD.
© COPYRIGHT HF CONTROLS LTD. 2011

REV	DATE	DETAIL
00	05/07/22	FIRST DRAFT
01	12/02/25	MC2 DUST PLANT FAN ADDED
02		
03		
04		
05		
06		
07		

CLIENT	PEEL PORT
INSTALL	RSGT LIVERPOOL
TITLE	MCC2A WIRING SCHEMATICS

ENGRD. D.BALDOCK	 HF Controls Ltd 100 Albert Drive, Glasgow G41 2SJ Tel: +44 (0)141 429 5575 Fax: +44 (0)141 420 1054 email: hf@hfcontrols.co.uk www.hf-group.co.uk
DRAWN. D.BALDOCK	
CHECK M.WRIGHT	
DATE 12/02/25	
DRG. No.:	284595 / 1002 / 01

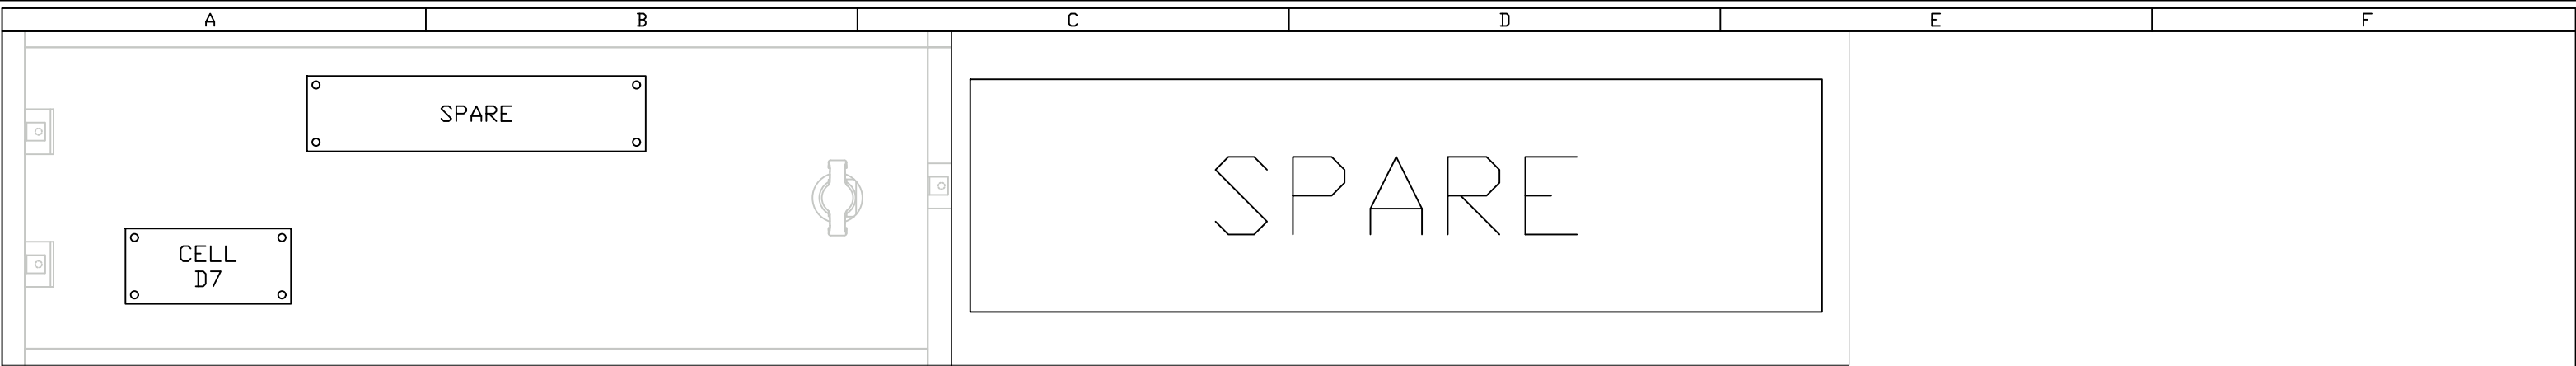

DRAWING STATUS

FIRST DRAFT

FOR MANUFACTURE

SIGNED..... DATED.....

HF CONTROLS LTD.
© COPYRIGHT HF CONTROLS LTD. 2011


REV	DATE	DETAIL
00	05/07/22	FIRST DRAFT
01	12/02/25	MC2 DUST PLANT FAN ADDED
02		
03		
04		
05		
06		
07		

CLIENT	PEEL PORT	ENGRD. D.BALDOCK
		DRAWN. D.BALDOCK
		CHECK M.WRIGHT
		DATE 12/02/25
INSTALL	RSGT LIVERPOOL	
TITLE	MCC2A WIRING SCHEMATICS	

HF Controls Ltd
100 Albert Drive, Glasgow G41 2SJ
Tel: +44 (0)141 429 5575 Fax: +44 (0)141 420 1054
email: hf@hfcontrols.co.uk www.hf-group.co.uk


DRG. No.:

284595 / 1002 / 01

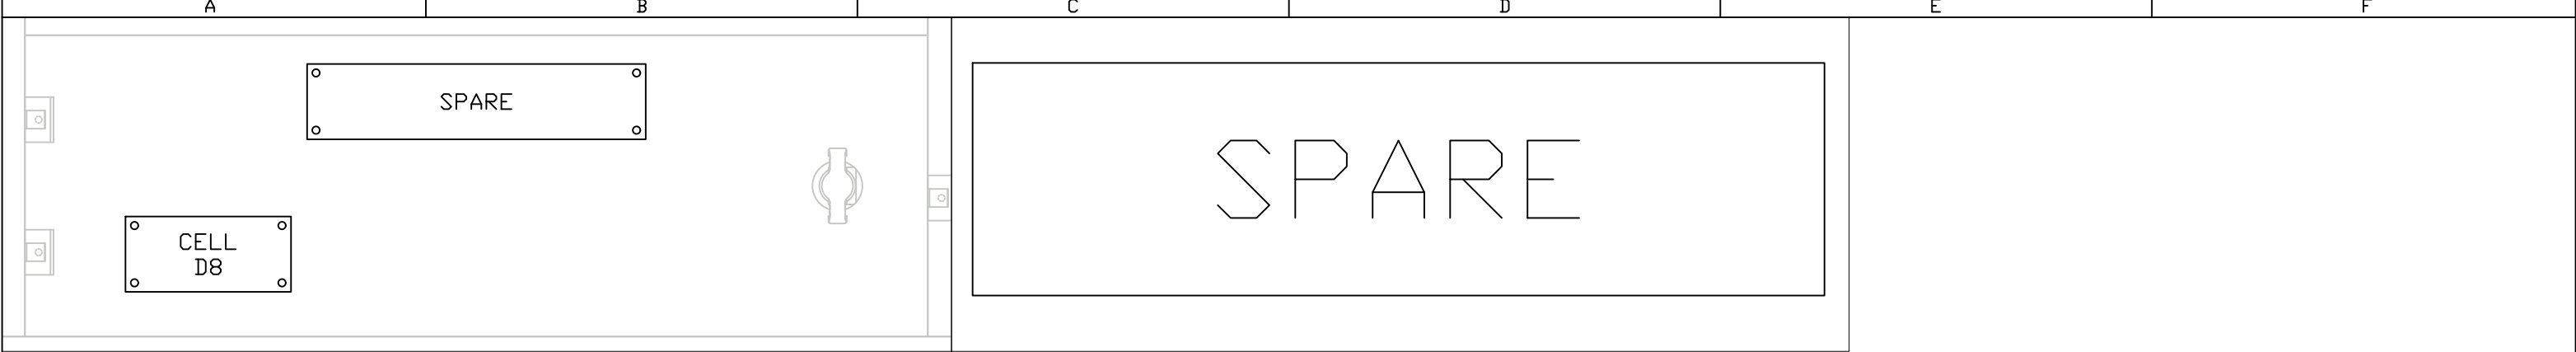


DRAWING STATUS		REV	DATE	DETAIL	CLIENT	PEEL PORT	ENGRD. D.BALDOCK	 HF Controls Ltd 100 Albert Drive, Glasgow G41 2SJ Tel: +44 (0)141 429 5575 Fax: +44 (0)141 420 1054 email: hf@hfcontrols.co.uk www.hf-group.co.uk
FIRST DRAFT	☐	00	05/07/22	FIRST DRAFT			DRAWN. D.BALDOCK	
FOR MANUFACTURE	☐	01	12/02/25	MC2 DUST PLANT FAN ADDED			CHECK M.WRIGHT	
SIGNED.....	DATED.....	02			INSTALL	RSGT LIVERPOOL	DATE 12/02/25	
 HF CONTROLS LTD. © COPYRIGHT HF CONTROLS LTD. 2011		03					DRG. No.:	
		04					284595 / 1002 / 01	
		05						
		06			TITLE	MCC2A WIRING SCHEMATICS		
		07						

SURGE BIN &
BASEMENT BELT VALVES

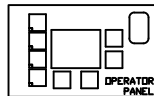


**OPERATOR
PANEL**

THIS CELL IS SUPPLIED
FROM MULTIPLE SOURCES.
ISOLATE AT SOURCE
BEFORE OPENING

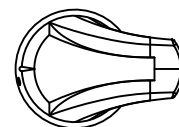


CELL
E1


60mm x 80mm

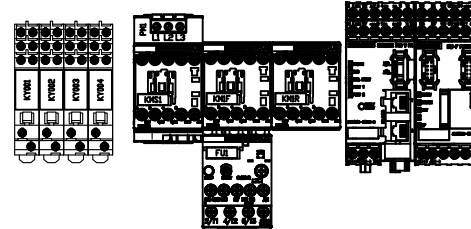


40mm x 80mm

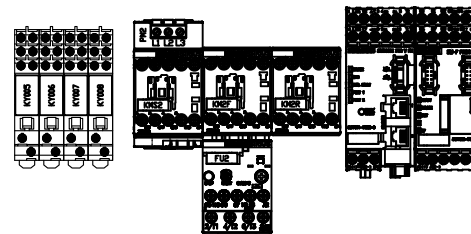

40mm x 80mm

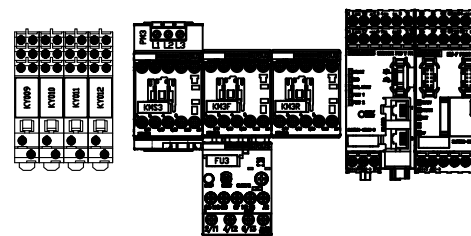

40mm x 80mm

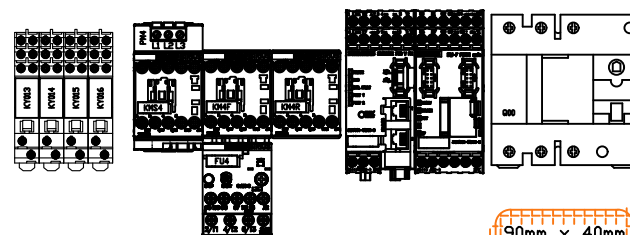

90mm x 40mm

100mm x 80mm

DRAWING STATUS

FIRST DRAFT ☐
FOR MANUFACTURE ☐
SIGNED..... DATED.....



 HF CONTROLS LTD.
© COPYRIGHT HF CONTROLS LTD. 2011

REV	DATE	DETAIL
00	05/07/22	FIRST DRAFT
01	12/02/25	MC2 DUST PLANT FAN ADDED
02		
03		
04		
05		
06		
07		

PEEL PORT

RSGT
LIVERPOOL

MCC2A

WIRING SCHEMATICS

ENGRD.	D.BALDOCK
DRAWN.	D.BALDOCK
CHECK	M.WRIGHT
DATE	12/02/25


DRG. No.:	
-----------	--

284595 / 1002 / 01




HF Controls Ltd

100 Albert Drive, Glasgow G41 2SJ
Tel: +44 (0)141 429 5575 Fax: +44 (0)141 420 1054
email: hf@hfcontrols.co.uk www.hf-group.co.uk

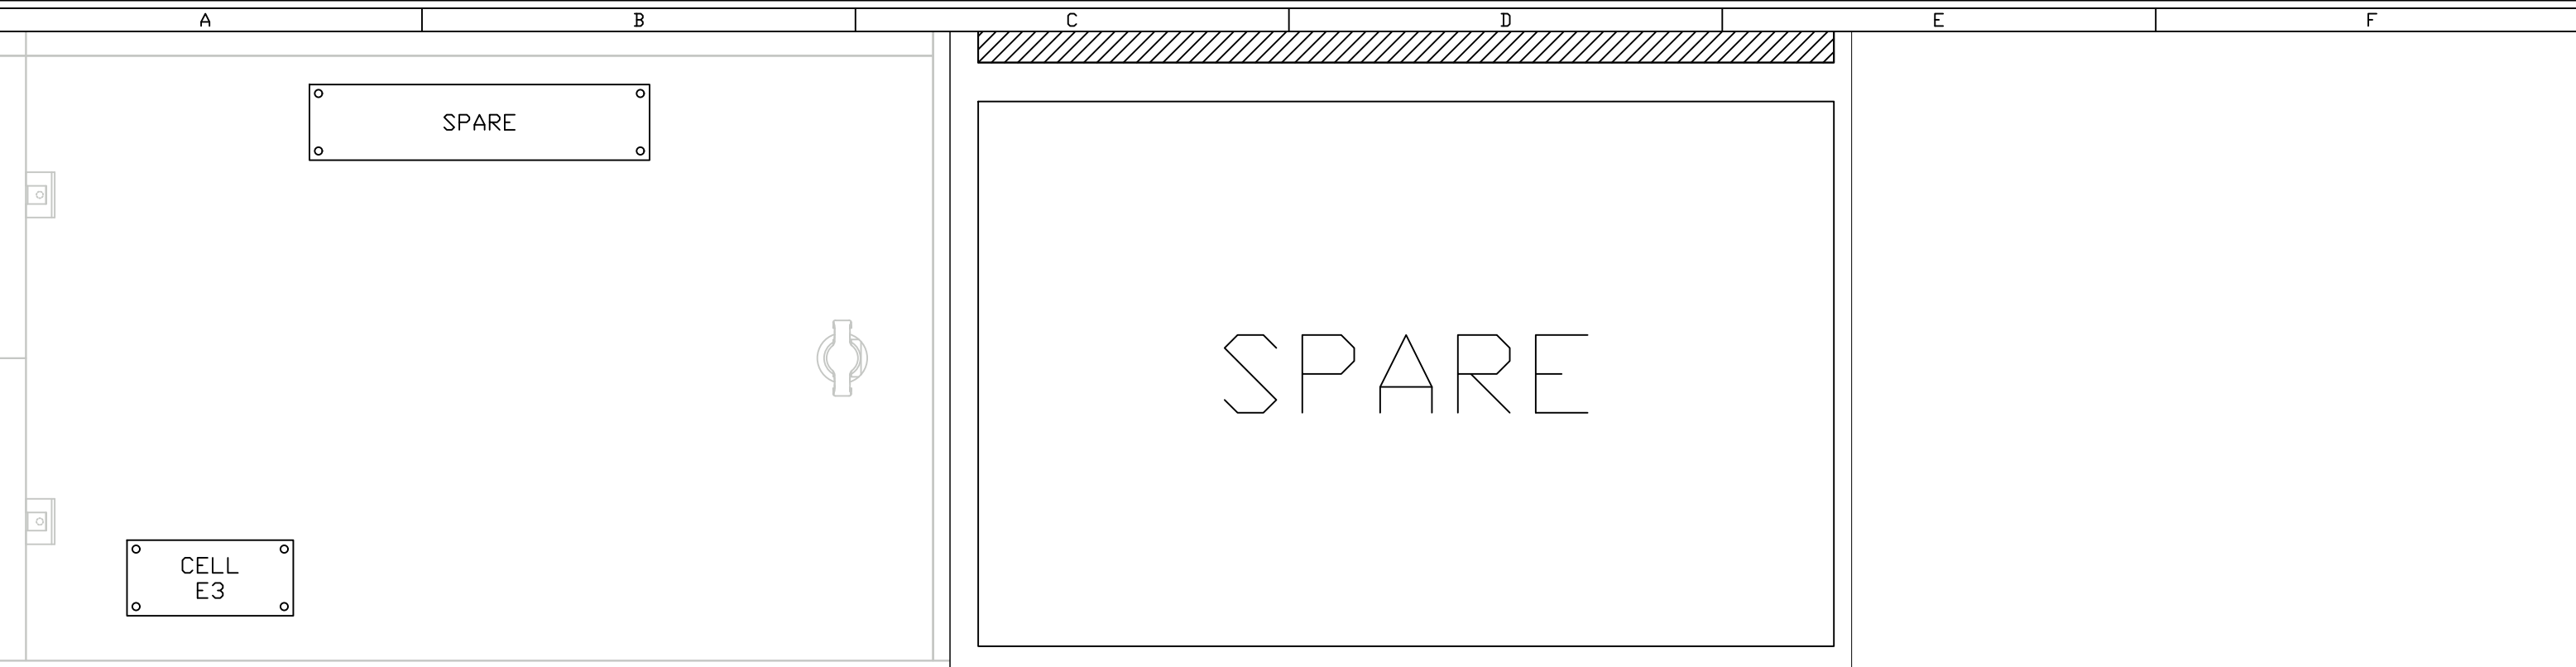

DRAWING STATUS		REV		DATE		DETAIL		CLIENT	PEEL PORT	ENGRD. D.BALDOCK		 HF Controls Ltd 100 Albert Drive, Glasgow G41 2SJ Tel: +44 (0)141 429 5575 Fax: +44 (0)141 420 1054 email: hf@hfcontrols.co.uk www.hf-group.co.uk
FIRST DRAFT	☐	00	05/07/22	FIRST DRAFT						DRAWN. D.BALDOCK		
FOR MANUFACTURE	☐	01	12/02/25	MCC2A DUST PLANT FAN ADDED				INSTALL	RSGT LIVERPOOL	CHECK M.WRIGHT		
SIGNED.....	DATED.....	02								DATE 12/02/25		
		03										
		04										
		05						TITLE	MCC2A WIRING SCHEMATICS	DRG. No.:		
		06								284595 / 1002 / 01		
		07										


 **HF CONTROLS LTD.**
© COPYRIGHT HF CONTROLS LTD. 2011

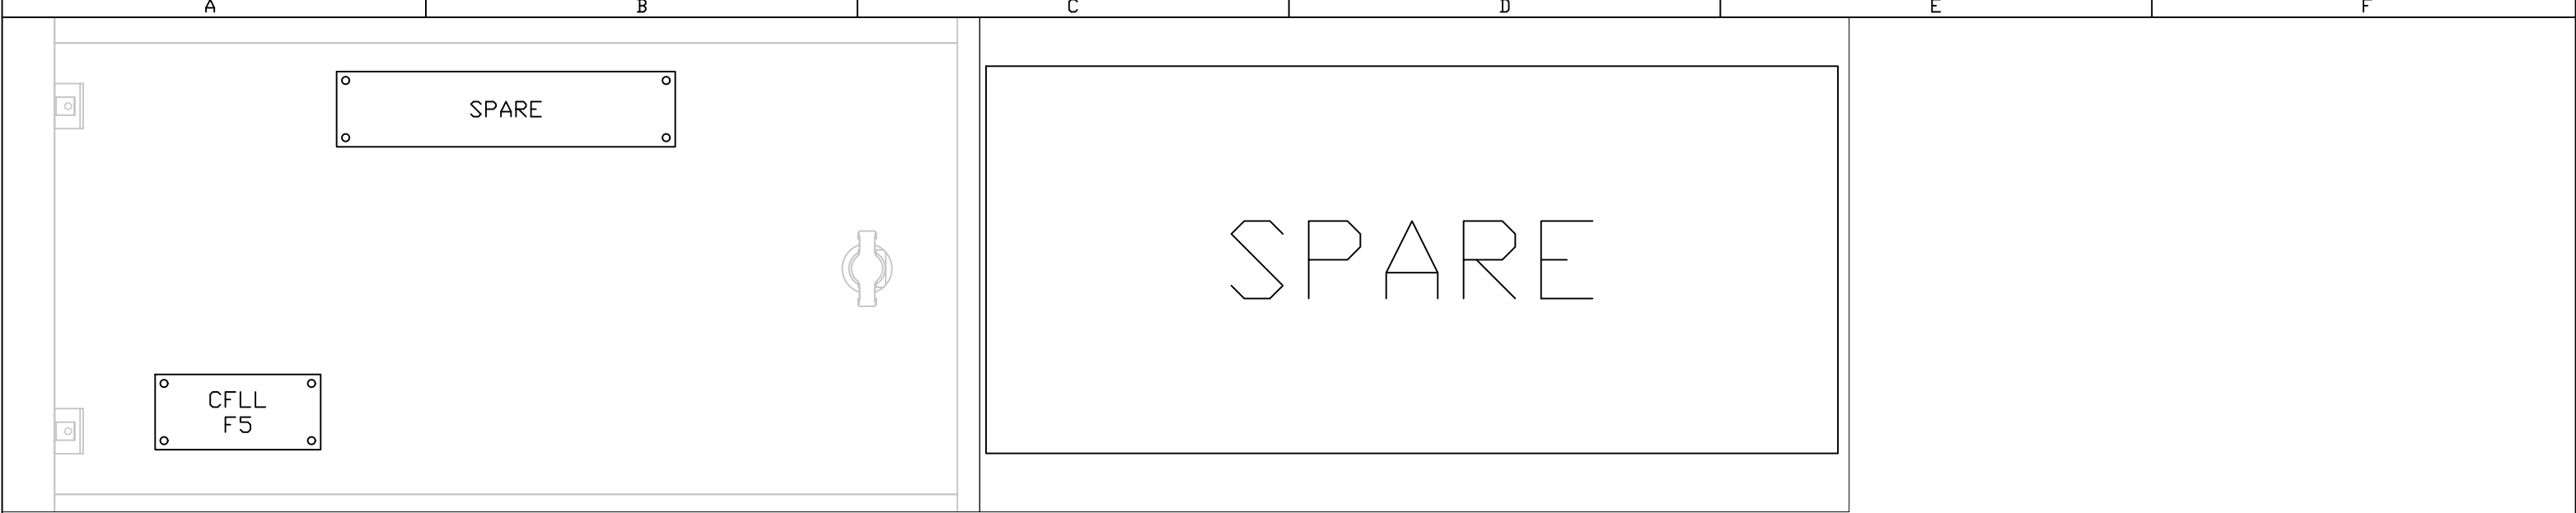

DRAWING STATUS		REV	DATE	DETAIL	CLIENT	PEEL PORT	ENGRD. D.BALDOCK	 HF Controls Ltd 100 Albert Drive, Glasgow G41 2SJ Tel: +44 (0)141 429 5575 Fax: +44 (0)141 420 1054 email: hf@hfcontrols.co.uk www.hf-group.co.uk
FIRST DRAFT ☐		00	05/07/22	FIRST DRAFT			DRAWN. D.BALDOCK	
FOR MANUFACTURE ☐		01	12/02/25	MC2 DUST PLANT FAN ADDED				
SIGNED.....	DATED.....	02			INSTALL	RSGT LIVERPOOL	CHECK M.WRIGHT	
		03					DATE 12/02/25	
		04						
		05			TITLE	MCC2A WIRING SCHEMATICS	DRG. No.:	
		06					284595 / 1002 / 01	
		07						




HF Controls Ltd
100 Albert Drive, Glasgow G41 2SJ
Tel: +44 (0)141 429 5575 Fax: +44 (0)141 420 1054
email: hf@hfcontrols.co.uk www.hf-group.co.uk

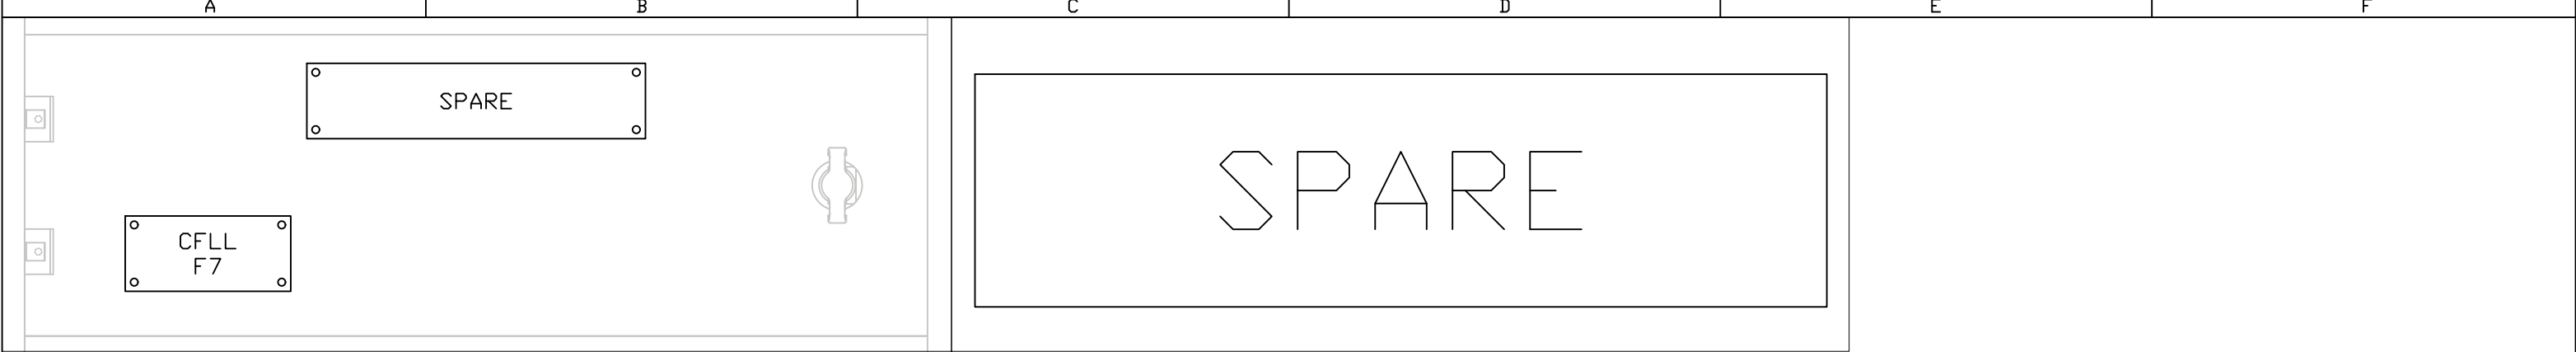

DRAWING STATUS

FIRST DRAFT

FOR MANUFACTURE

SIGNED..... DATED.....


 HF CONTROLS LTD.
© COPYRIGHT HF CONTROLS LTD. 2011

REV	DATE	DETAIL
00	05/07/22	FIRST DRAFT
01	12/02/25	MC2 DUST PLANT FAN ADDED
02		
03		
04		
05		
06		
07		

CLIENT	PEEL PORT	ENGRD. D.BALDOCK
		DRAWN. D.BALDOCK
INSTALL	RSGT LIVERPOOL	CHECK M.WRIGHT
		DATE 12/02/25
TITLE	MCC2A WIRING SCHEMATICS	DRG. No.: 284595 / 1002 / 01


HF Controls Ltd
100 Albert Drive, Glasgow G41 2SJ
Tel: +44 (0)141 429 5575 Fax: +44 (0)141 420 1054
email: hf@hfcontrols.co.uk www.hf-group.co.uk



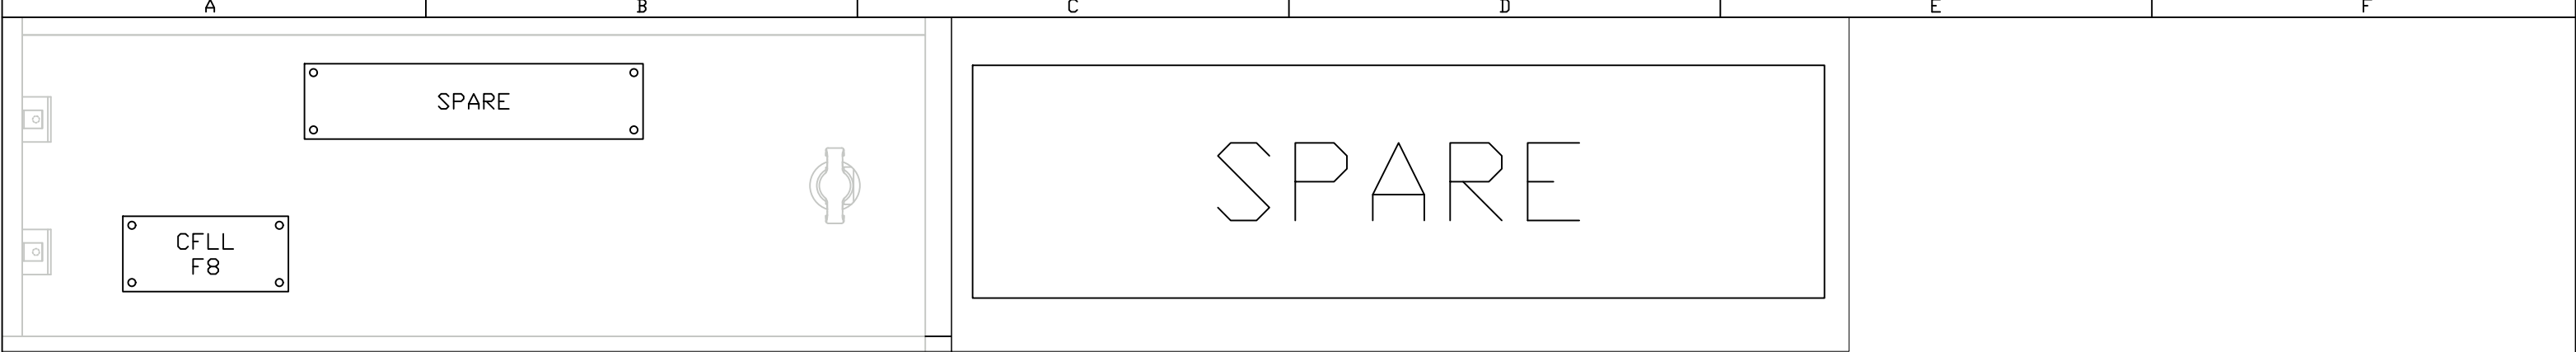

DRAWING STATUS		<table><tr><td>REV</td><td>DATE</td><td>DETAIL</td></tr><tr><td>00</td><td>05/07/22</td><td>FIRST DRAFT</td></tr><tr><td>01</td><td>12/02/25</td><td>MC2 DUST PLANT FAN ADDED</td></tr><tr><td>02</td><td></td><td></td></tr><tr><td>03</td><td></td><td></td></tr><tr><td>04</td><td></td><td></td></tr><tr><td>05</td><td></td><td></td></tr><tr><td>06</td><td></td><td></td></tr><tr><td>07</td><td></td><td></td></tr></table>			REV	DATE	DETAIL	00	05/07/22	FIRST DRAFT	01	12/02/25	MC2 DUST PLANT FAN ADDED	02			03			04			05			06			07			<table><tr><td rowspan="4">CLIENT</td><td>PEEL PORT</td><td>ENGRD. D.BALDOCK</td></tr><tr><td></td><td>DRAWN. D.BALDOCK</td></tr><tr><td rowspan="2">RSGT LIVERPOOL</td><td>CHECK M.WRIGHT</td></tr><tr><td>DATE 12/02/25</td></tr></table>		CLIENT	PEEL PORT	ENGRD. D.BALDOCK		DRAWN. D.BALDOCK	RSGT LIVERPOOL	CHECK M.WRIGHT	DATE 12/02/25	HF HF Controls Ltd 100 Albert Drive, Glasgow G41 2SJ Tel: +44 (0)141 429 5575 Fax: +44 (0)141 420 1054 email: hf@hfcontrols.co.uk www.hf-group.co.uk
REV	DATE	DETAIL	
00	05/07/22	FIRST DRAFT	
01	12/02/25	MC2 DUST PLANT FAN ADDED	
02	
03	
04	
05	
06	
07	
CLIENT	PEEL PORT	ENGRD. D.BALDOCK	
		DRAWN. D.BALDOCK	
	RSGT LIVERPOOL	CHECK M.WRIGHT	
		DATE 12/02/25	
TITLE		MCC2A WIRING SCHEMATICS	DRG. No.: 284595 / 1002 / 01																																							
<table><tr><td> HF CONTROLS LTD. © COPYRIGHT HF CONTROLS LTD. 2011 </td><td colspan="3"></td></tr></table>		HF CONTROLS LTD. © COPYRIGHT HF CONTROLS LTD. 2011	
HF CONTROLS LTD. © COPYRIGHT HF CONTROLS LTD. 2011	