

HF Controls Ltd

100 Albert Drive, Glasgow, G41 2SJ

www.hf-group.co.uk

Call 0800 783 9480

Glasgow

Edinburgh

Manchester

Belfast

Aberdeen

PROJECT: RSGT

PROJECT LOCATION: LIVERPOOL

PROJECT REFERENCE NUMBER: 284595

CLIENT: PEEL PORTS

CLIENT ADDRESS: MARITIME CENTRE PORT OF LIVERPOOL

CLIENT ORDER NUMBER:

CONTROL SYSTEM DETAILS & SPECIFICATION

SYSTEM TYPE: SAFE AREA

ENCLOSURE MATERIAL: MILD STEEL

RATED VOLTAGE: 230V AC

RATED FREQUENCY: 50 Hz

RATED AMPERE:	16A
---------------	-----

CONTROL VOLTAGE: 24V DC

DEGREE OF PROTECTION: IP 55

PAINT FINISH: POWDER COATED RAL7035

YEAR OF MANUFACTURE:	2023
----------------------	------



HF Controls Ltd
100 Albert Drive, Glasgow, G41 2SJ


Call 0800 783 9480



www.hf-group.co.uk

Glasgow Edinburgh Manchester Belfast Aberdeen

REV	DATE	DETAIL	CLIENT	PEEL PORTS	ENGINEERED	M.WRIGHT
00	26/06/24	AS FITTED			DRAWN	M.WRIGHT
01					CHECKED	D.BALDOCK
02			INSTALL	RSGT LIVERPOOL	DATE	17/03/2023
03					DRG. No.:	284595_2102
04						
05						
06			TITLE	CP02 IS PLC PANEL GENERAL ARRANGEMENT	DRAWING REVISION :	PAGE No.:
07					00	01 OF 04

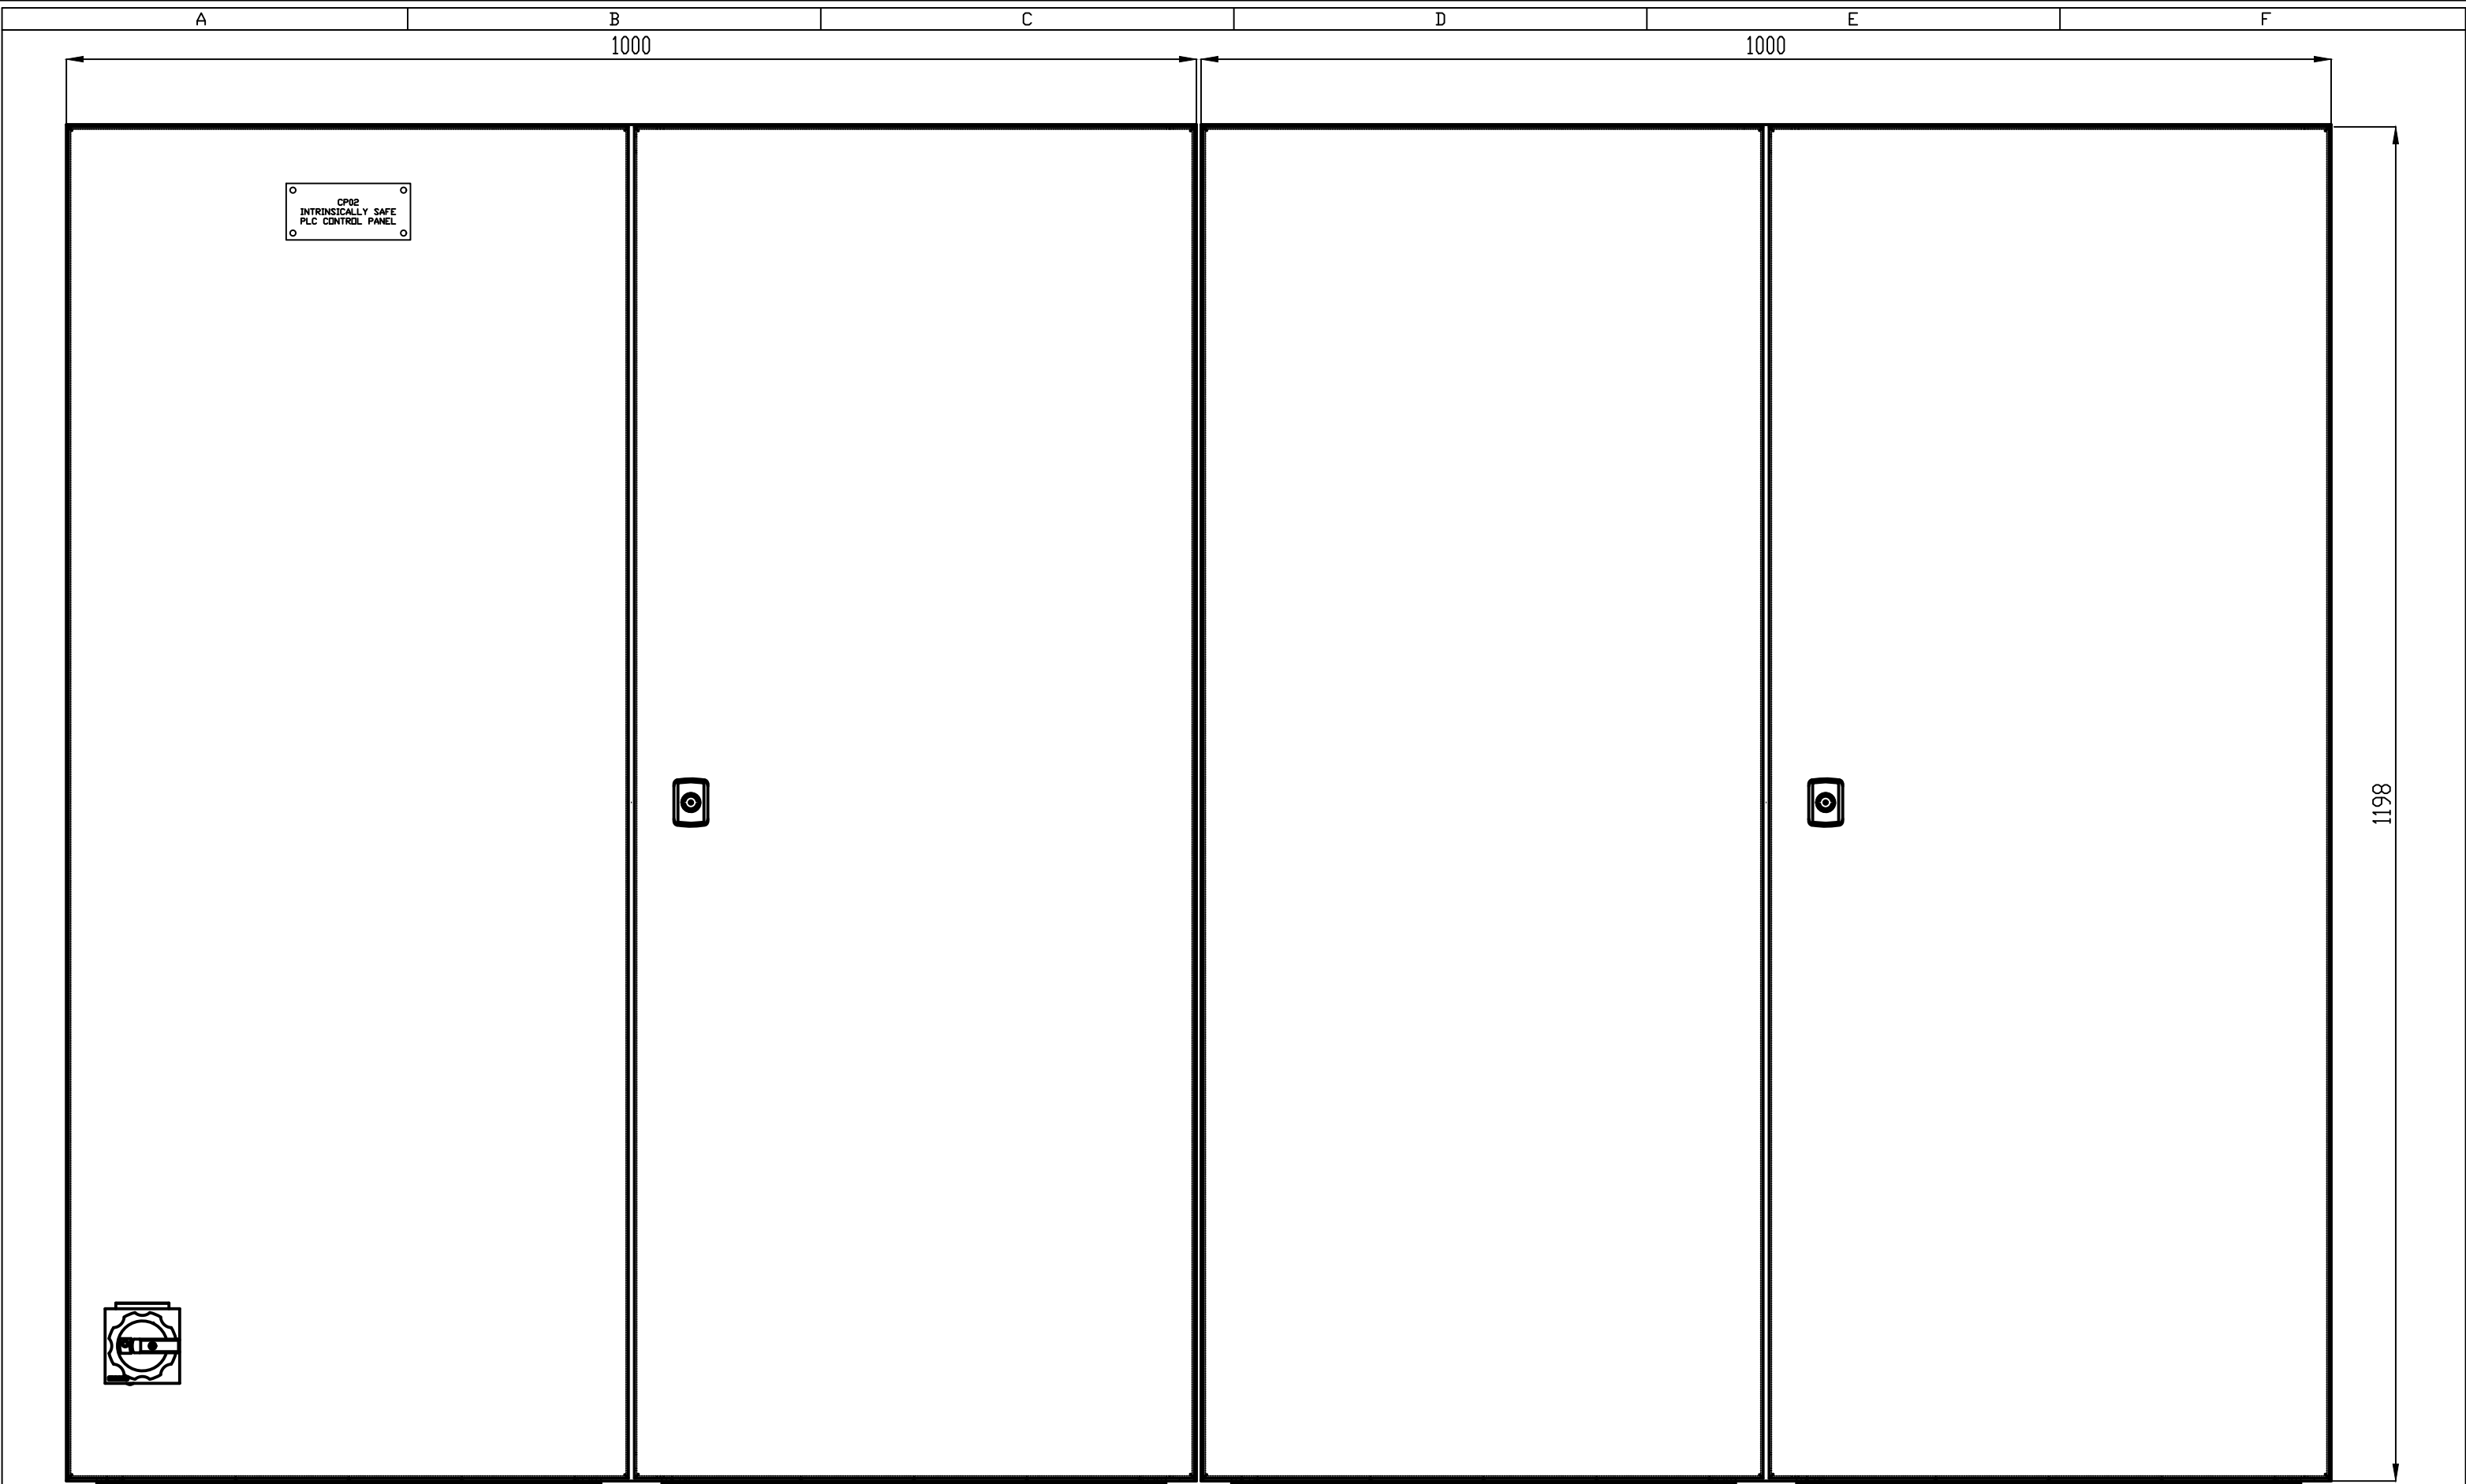


HF Controls Ltd
100 Albert Drive, Glasgow, G41 2SJ
Call 0800 783 9480 www.hf-group.co.uk

Glasgow Edinburgh Manchester Belfast Aberdeen



REV	DATE	DETAIL	CLIENT	PEEL PORTS	ENGINEERED	M.WRIGHT
00	26/06/24	AS FITTED			DRAWN	M.WRIGHT
01					CHECKED	D.BALDOCK
02					DATE	17/03/2023
03					DRG. No.:	
04			INSTALL	RSGT LIVERPOOL	284595_2102	
05						
06						
07						
			TITLE	CP02 IS PLC PANEL GENERAL ARRANGEMENT	DRAWING REVISION :	
					00	PAGE No.:
						02 OF 04

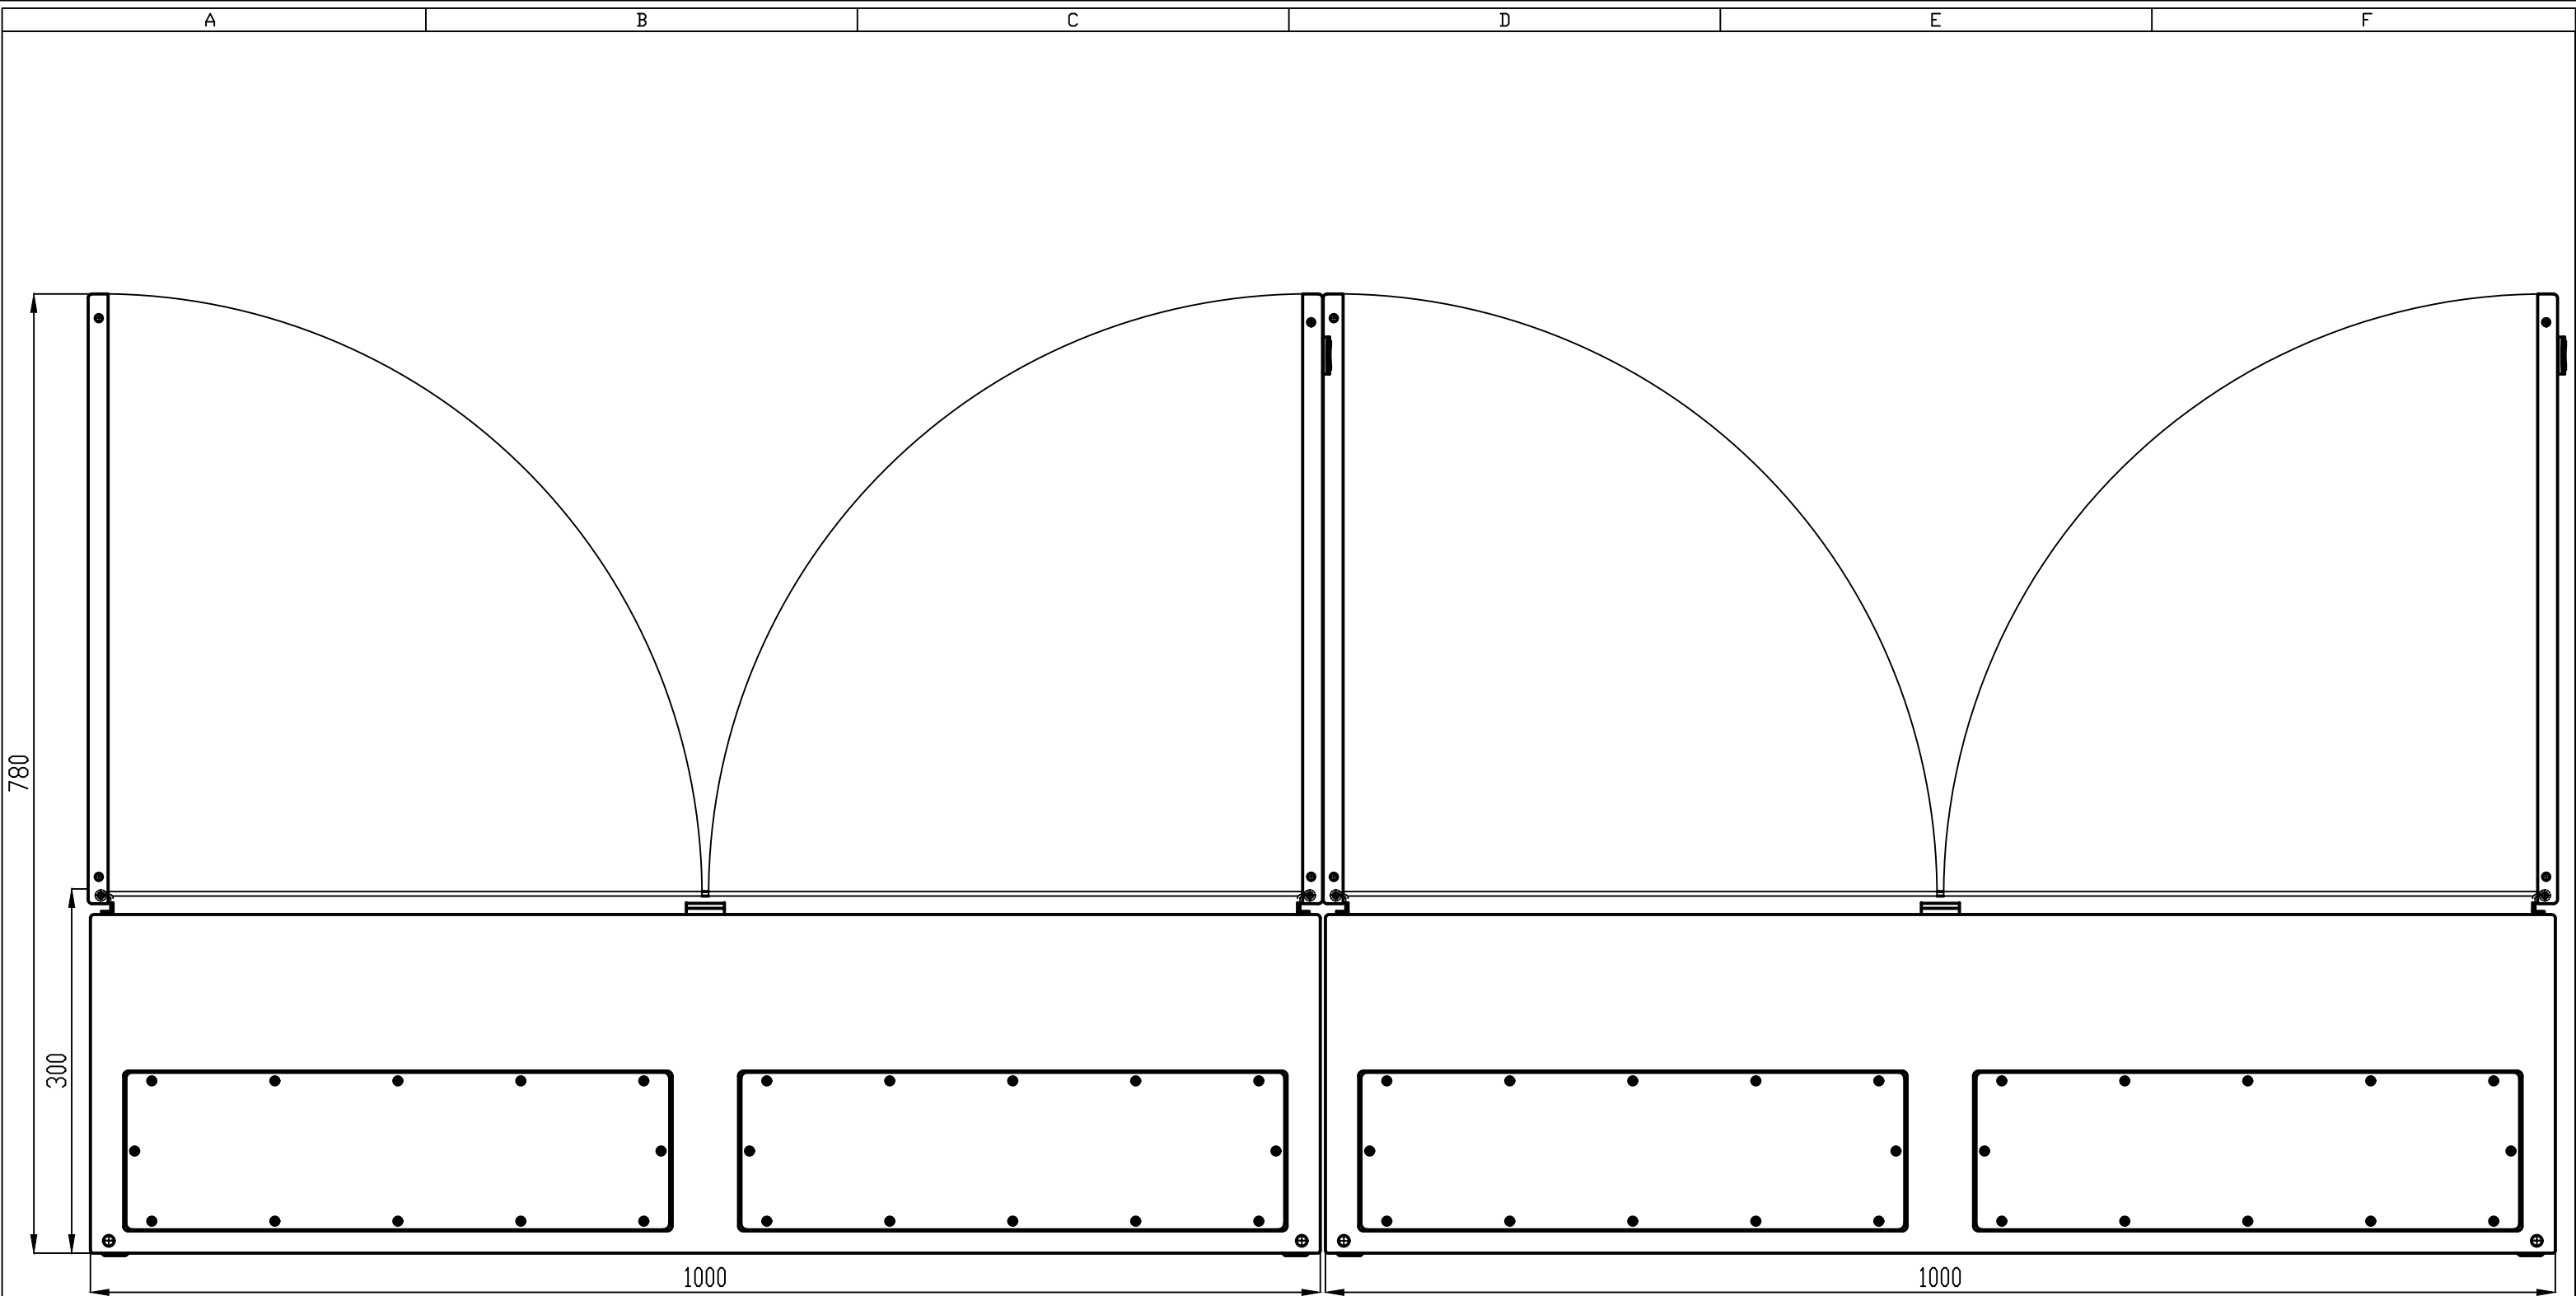

100 Albert Drive, Glasgow, G41 2SJ


Call 0800 783 9480

www.hf-group.co.uk

Glasgow Edinburgh Manchester Belfast Aberdeen



REV	DATE	DETAIL	CLIENT	PEEL PORTS	ENGINEERED	M.WRIGHT
00	26/06/24	AS FITTED			DRAWN	M.WRIGHT
01					CHECKED	D.BALDOCK
02					DATE	17/03/2023
03			INSTALL	RSGT LIVERPOOL	DRG. No.: 284595_2102	
04						
05						
06			TITLE	CP02 IS PLC PANEL GENERAL ARRANGEMENT	DRAWING REVISION :	PAGE No.:
07					00	03 OF 04

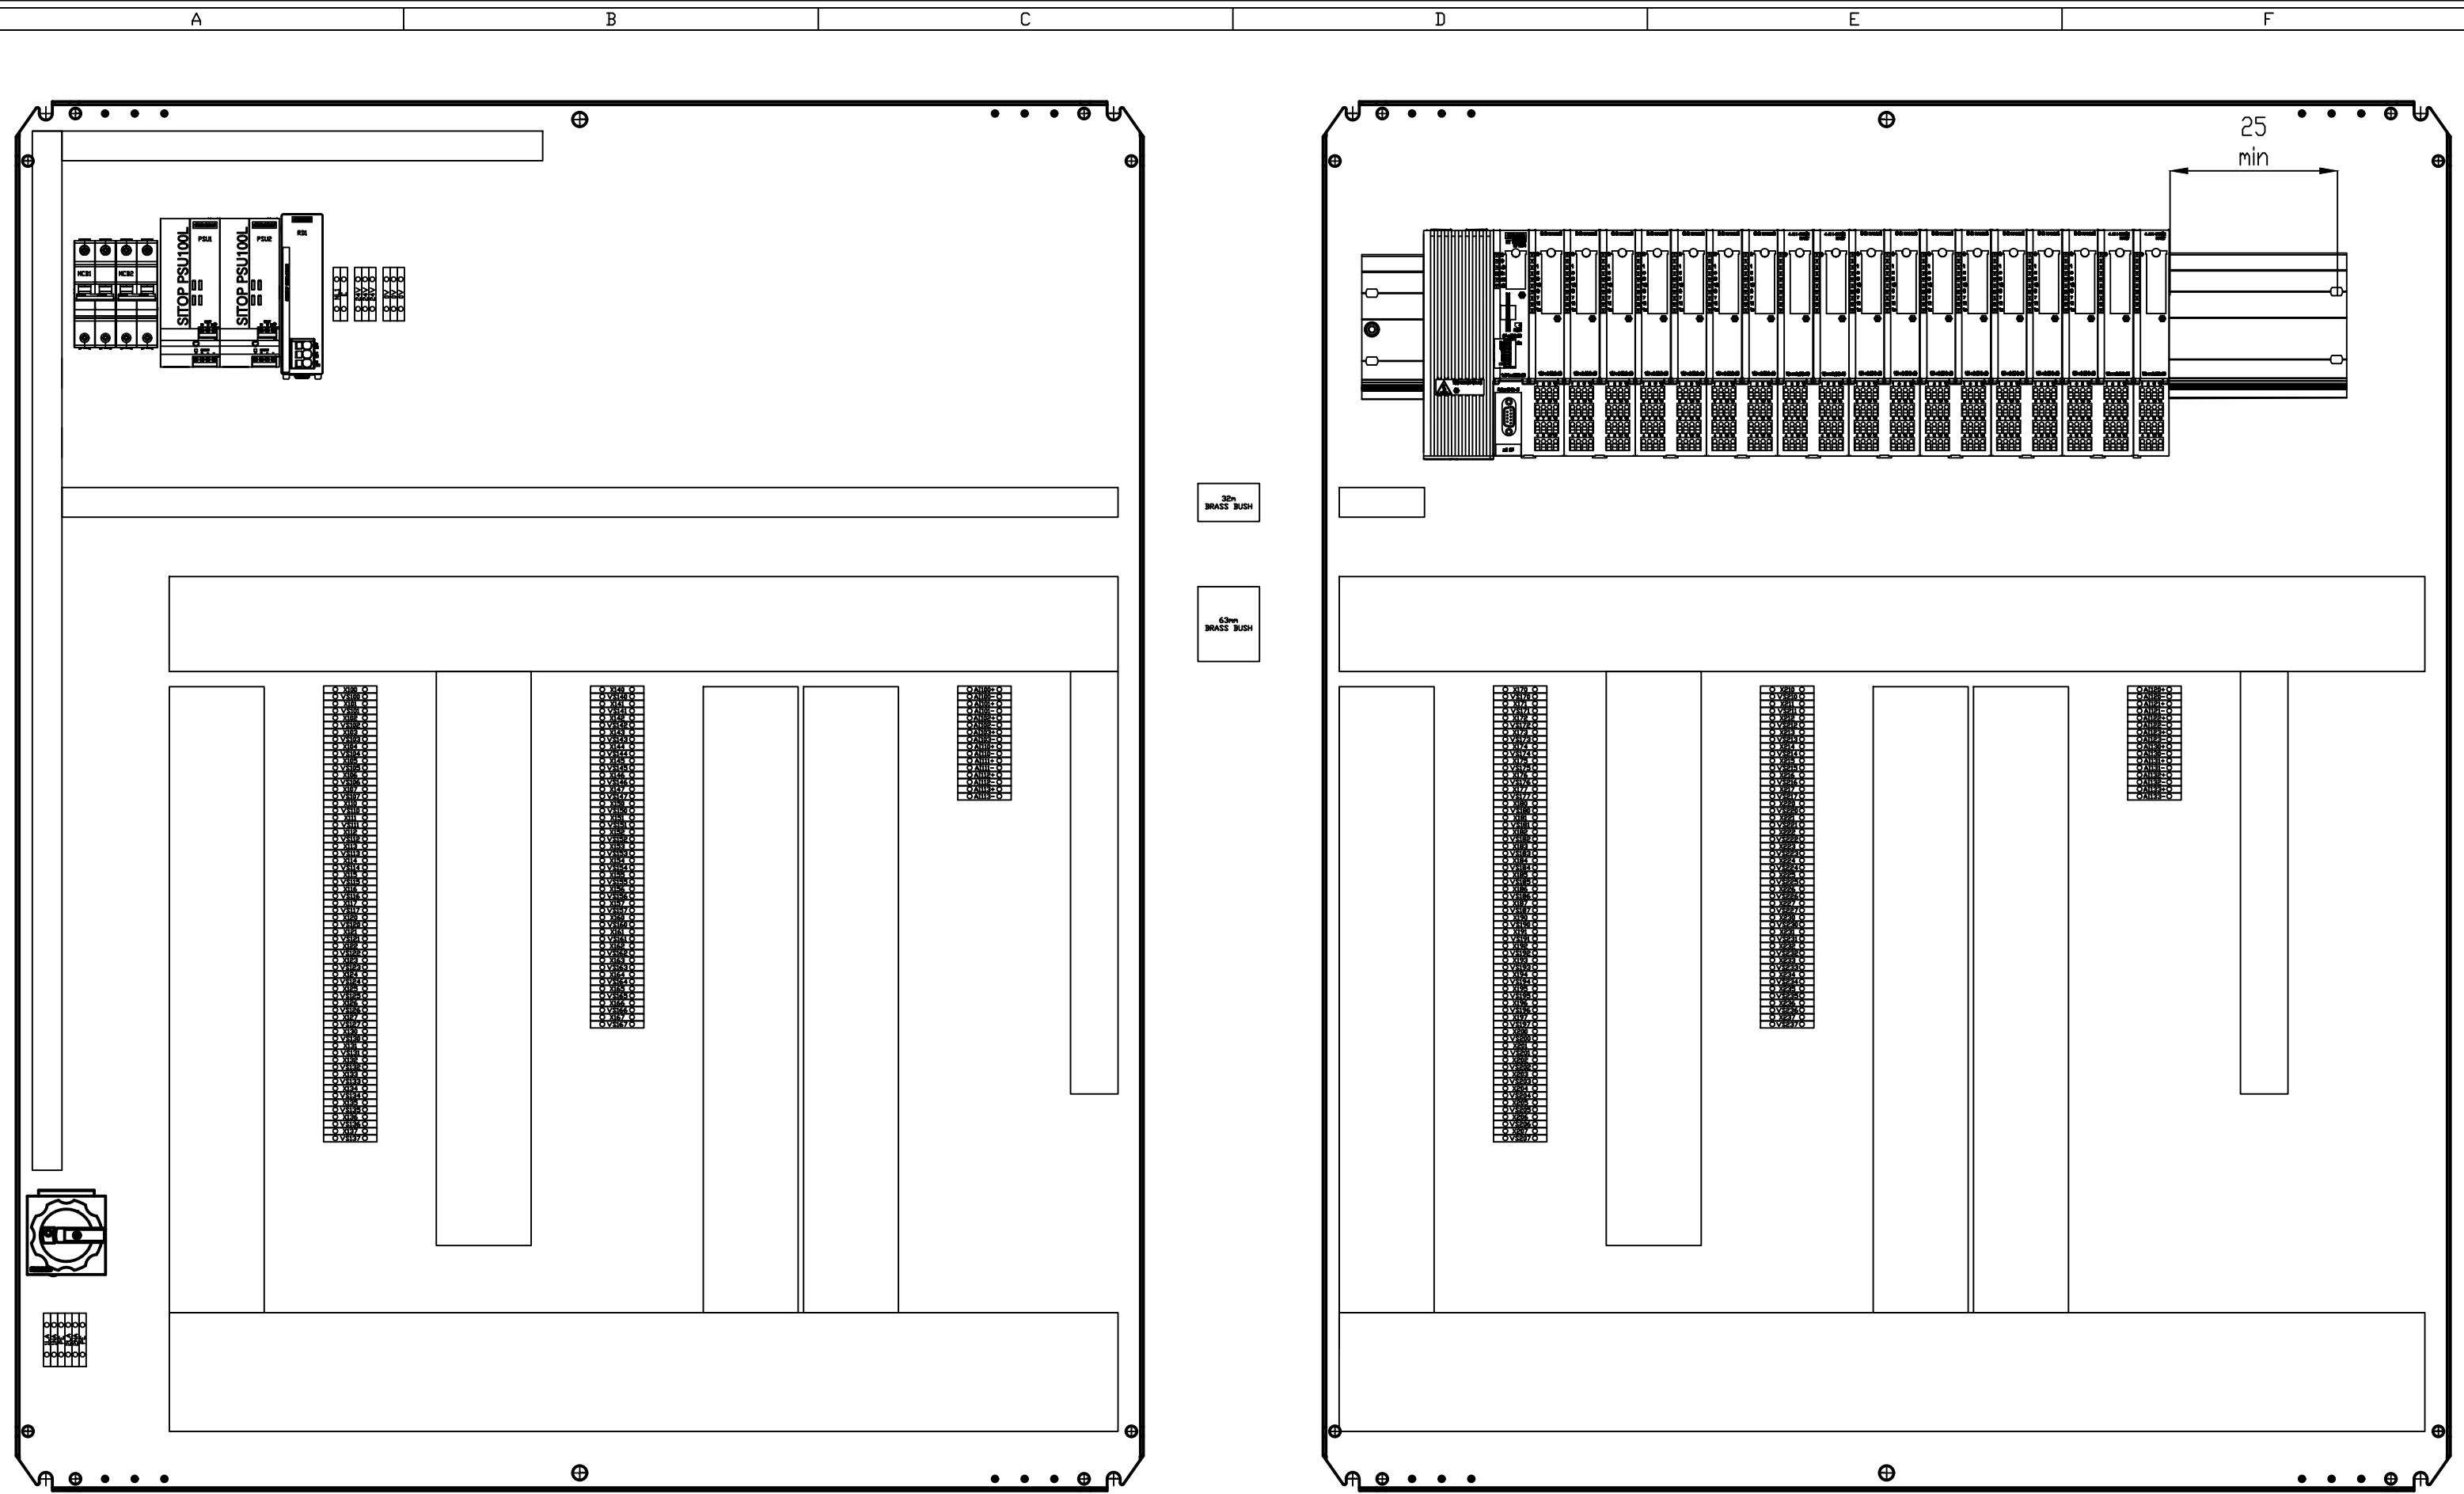

REV	DATE	DETAIL	CLIENT	PEEL PORTS	ENGINEERED	M.WRIGHT
00	26/06/24	AS FITTED			DRAWN	M.WRIGHT
01					CHECKED	D.BALDOCK
02					DATE	17/03/2023
03			INSTALL	RSGT LIVERPOOL	DRG. No.:	
04					284595_2102	
05					DRAWING REVISION :	
06					00	
07			TITLE	CP02 IS PLC PANEL GENERAL ARRANGEMENT	PAGE No.:	
					04 OF 04	