


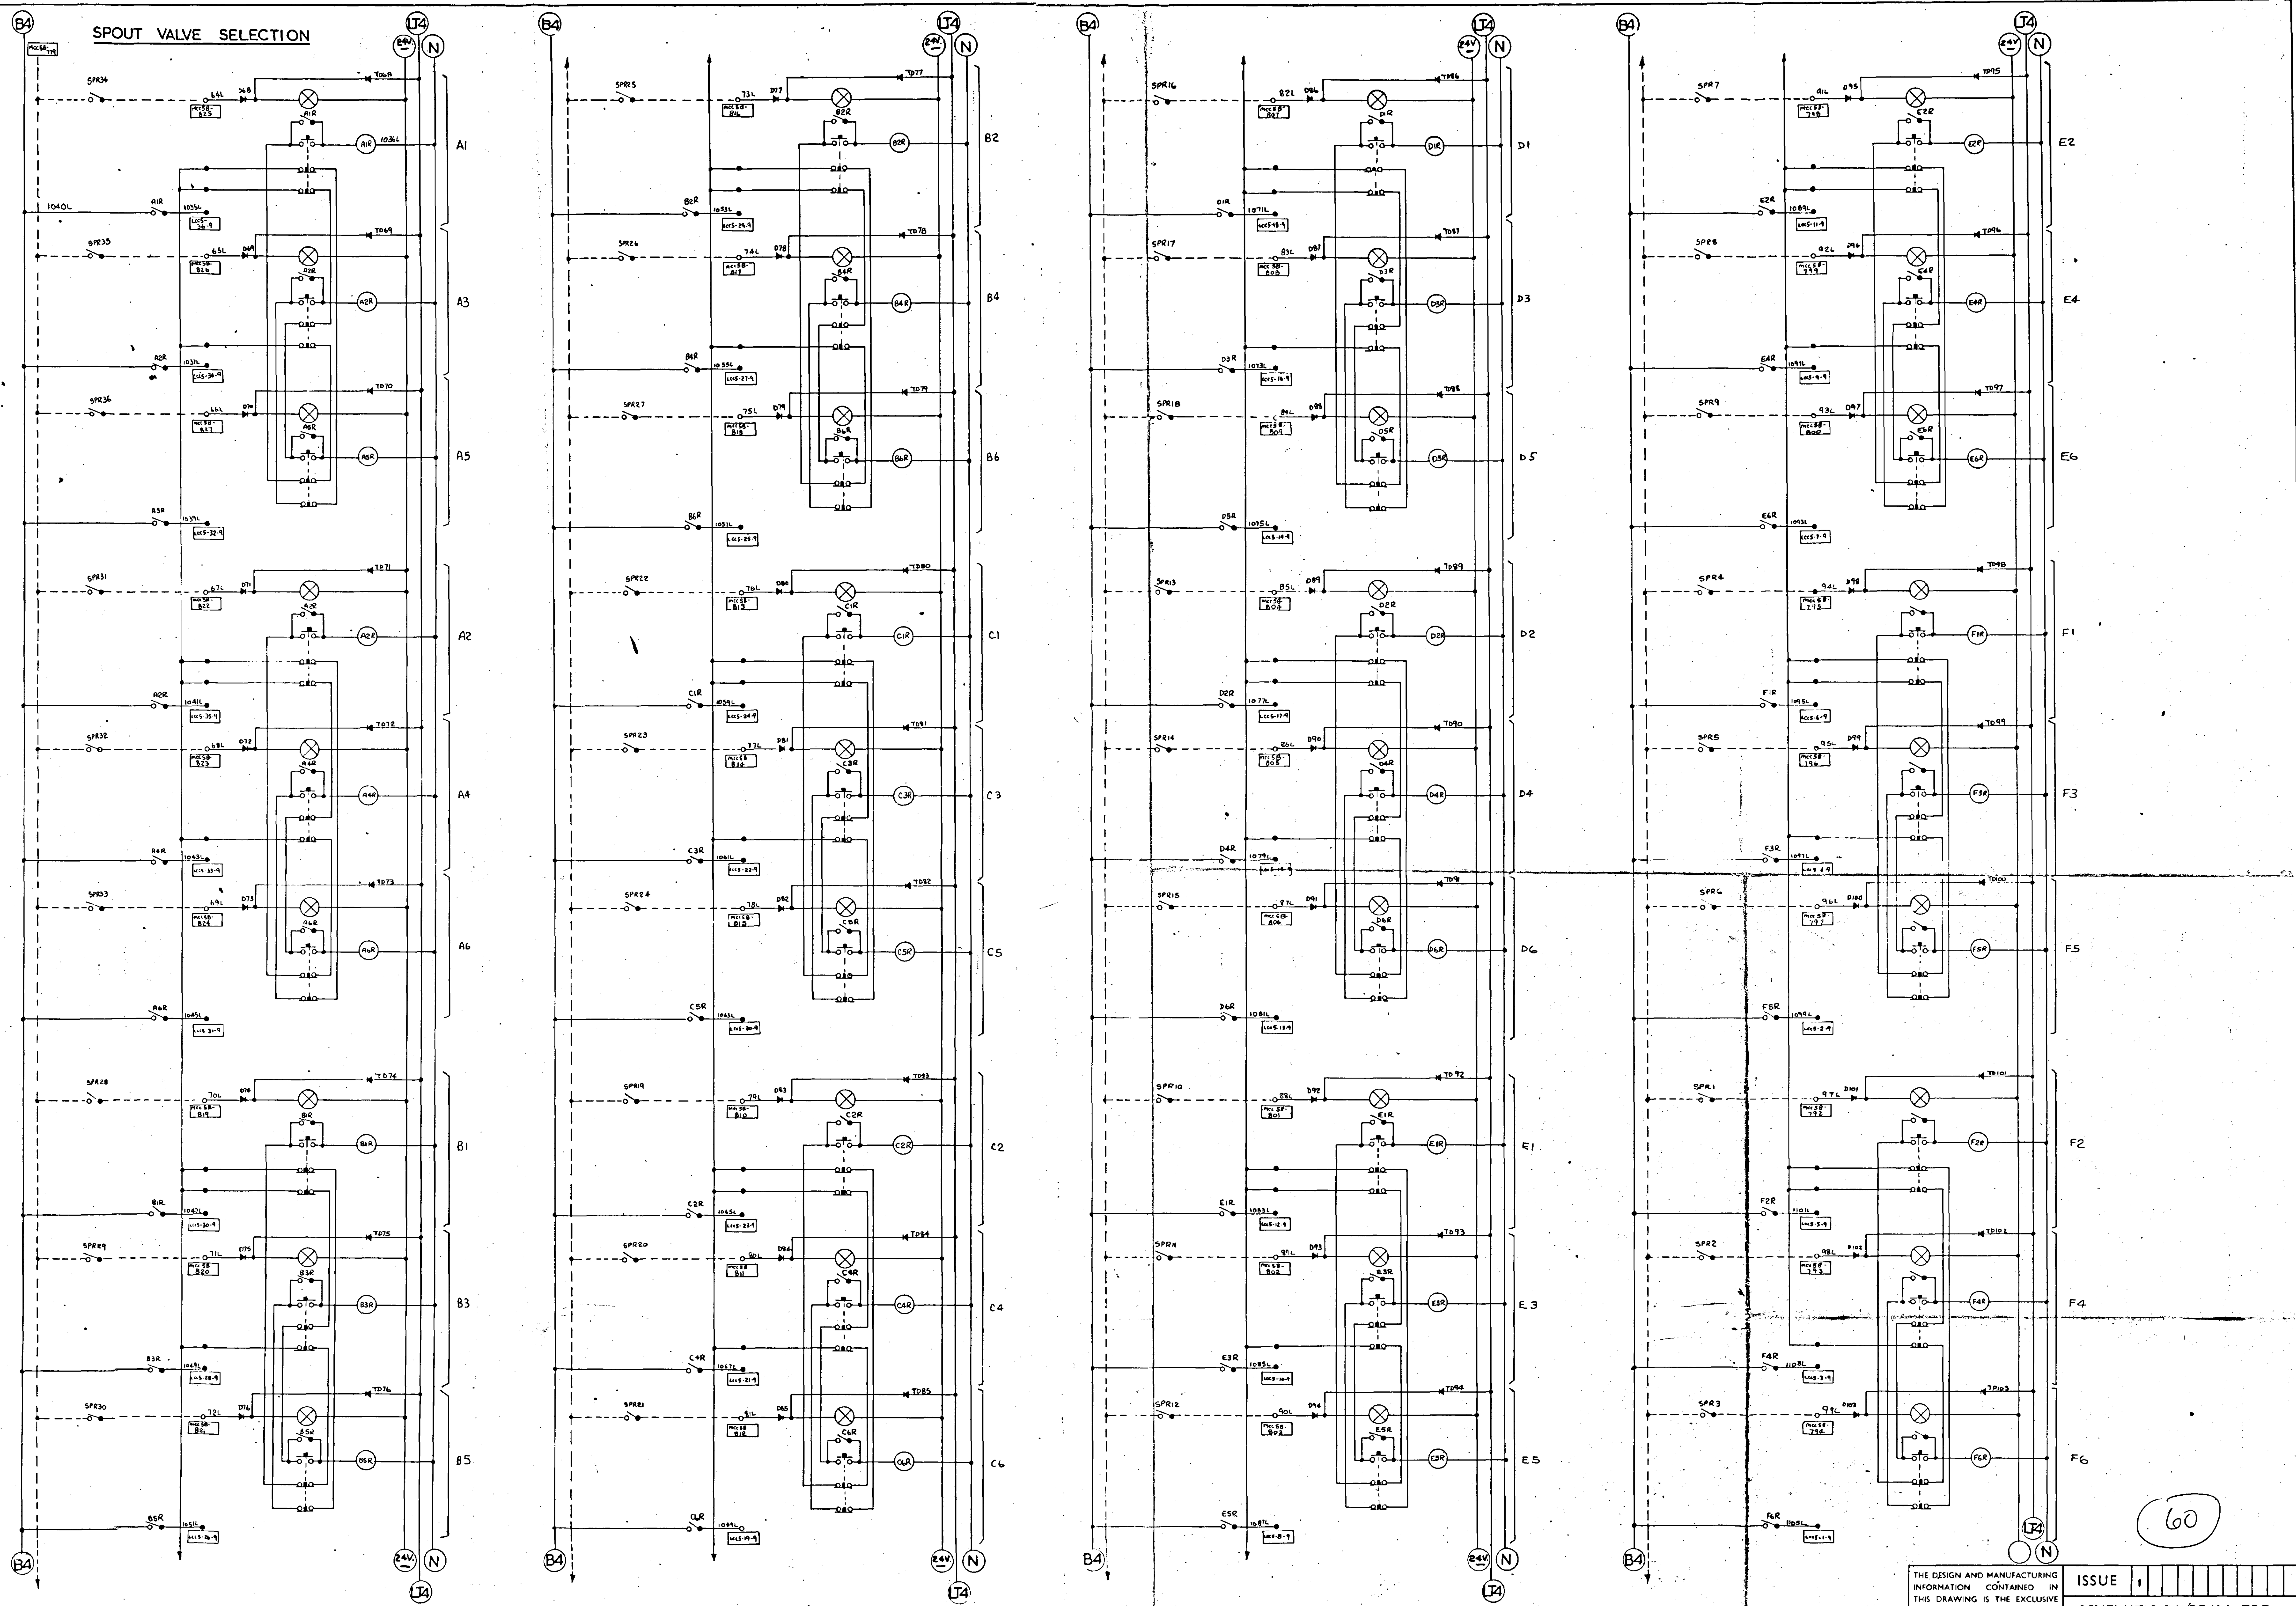

DEWHURST & PARTNER LTD.
MELBOURNE WORKS HOUNSLOW

TITLE
SCHEMATIC DIAGRAM FOR SUPERVISORY CONTROL PANEL - SEAFORTH GRAIN TERMINAL

REVISION:	REVISION:	REVISION:	REVISION:	REVISION:
ORIGIN: / / SGD	ORIGIN: / / SGD	ORIGIN: / / SGD	ORIGIN: / / SGD	ORIGIN: / / SGD

11138

DRAWN BY: <i>W. J. J. J.</i>	KEY DIAG. No.
CHECKED BY:	EXT. DIAG. No.
APPROVED BY:	REL. DIAG. No.
DATE:	PANEL LAYOUT No.

ISSUE	1
SCHEMATIC DIAGRAM FOR SUPERVISORY CONTROL PANEL SHEET 11 OF 12	
DTX 361AR/ 11	