
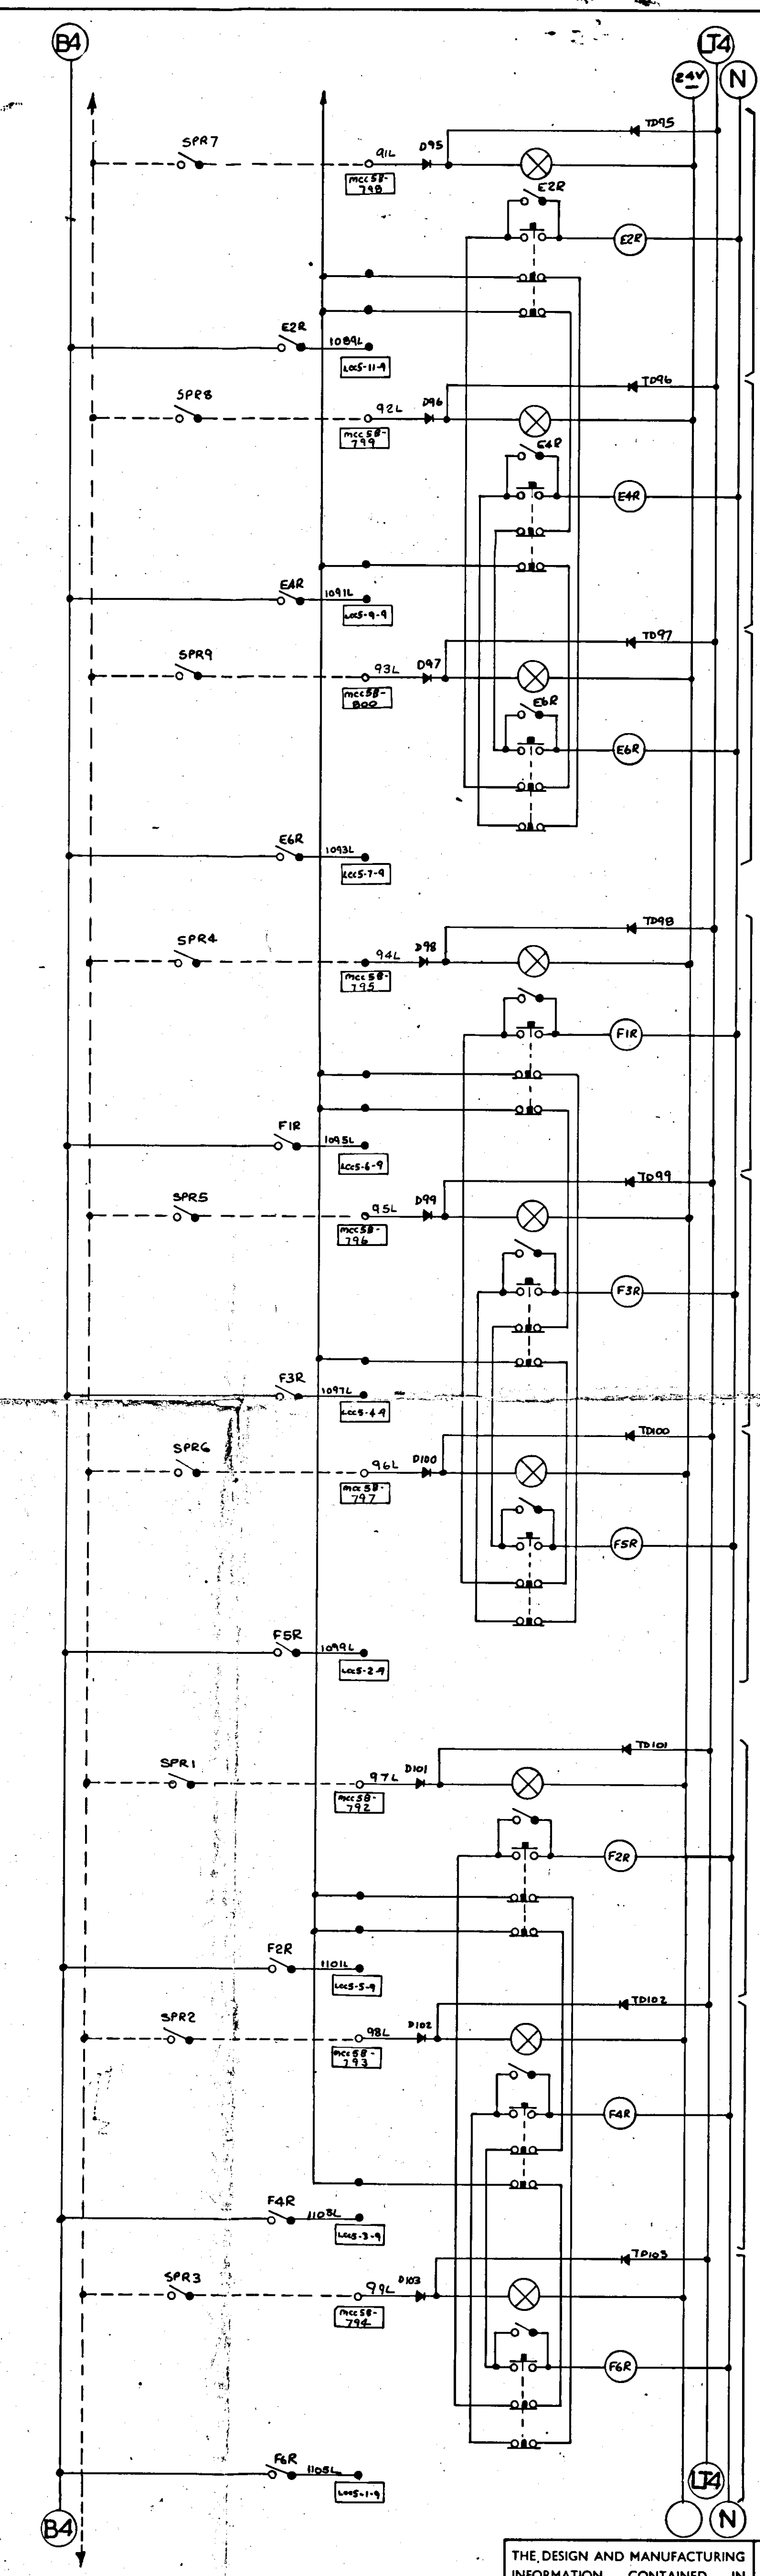
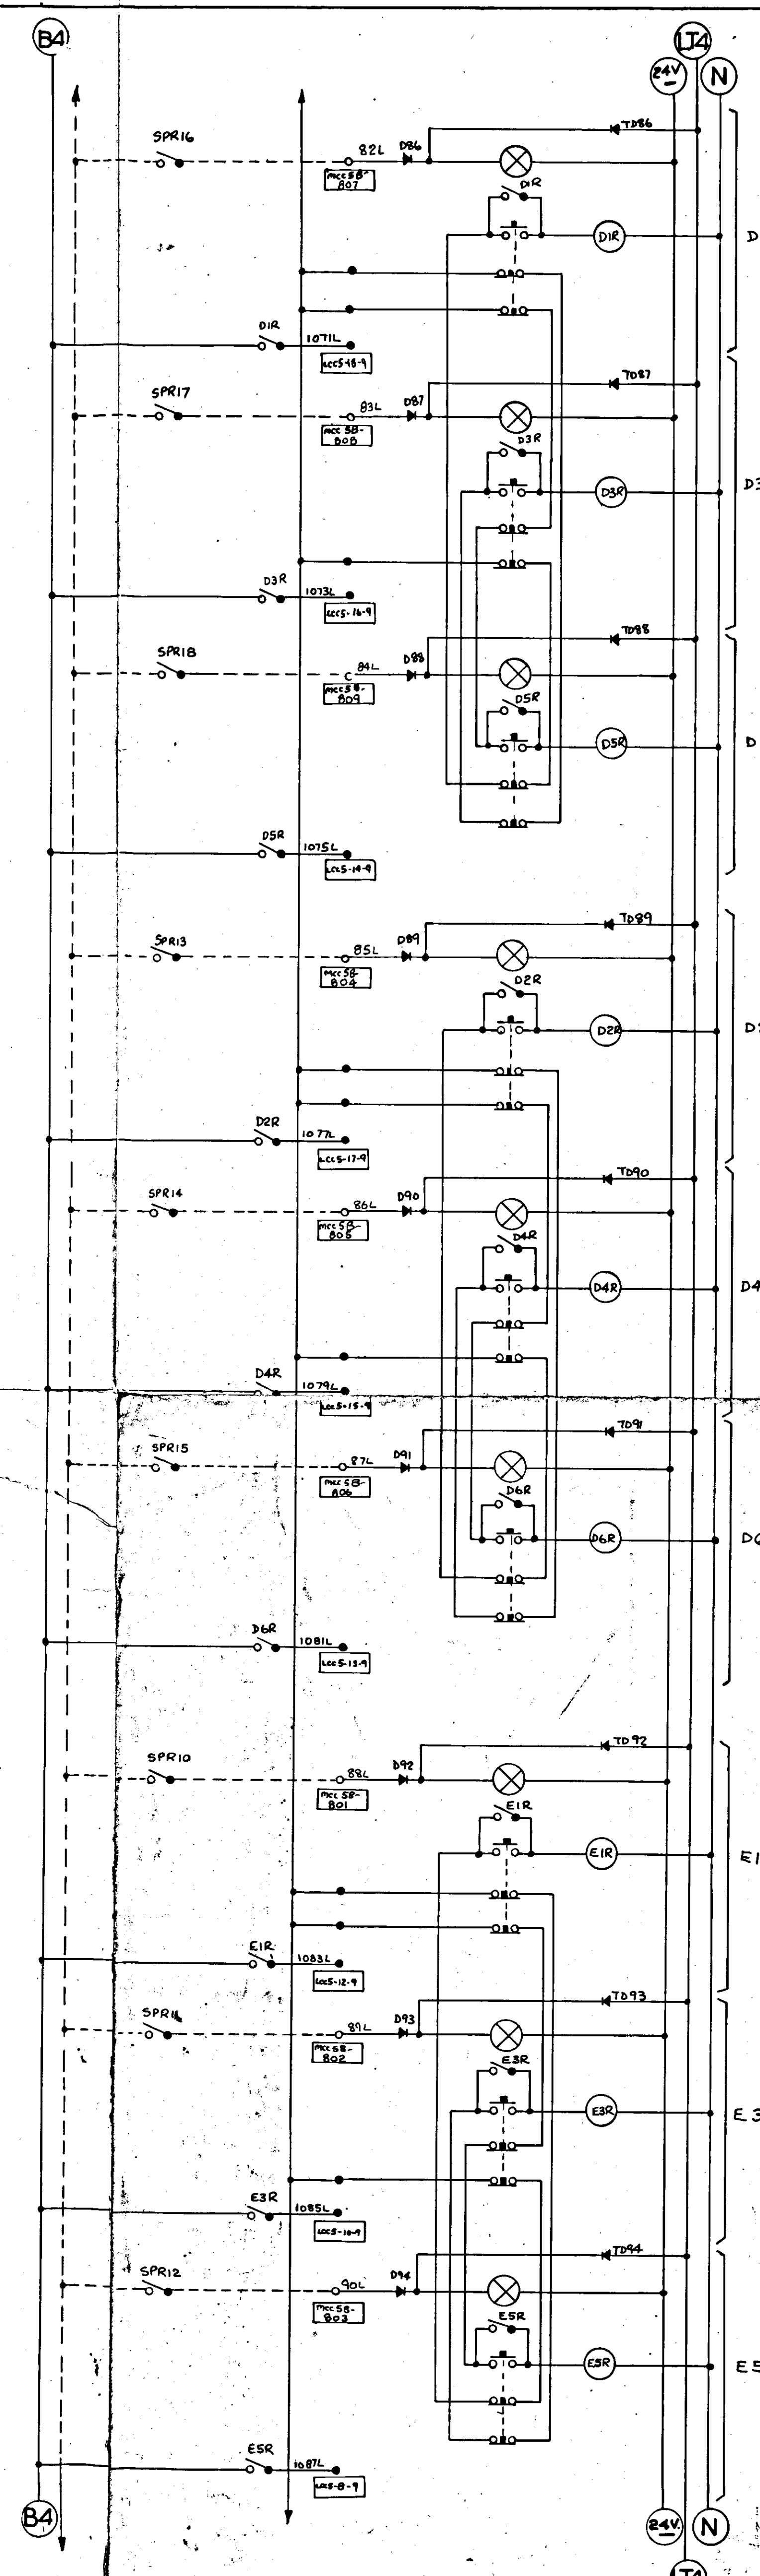
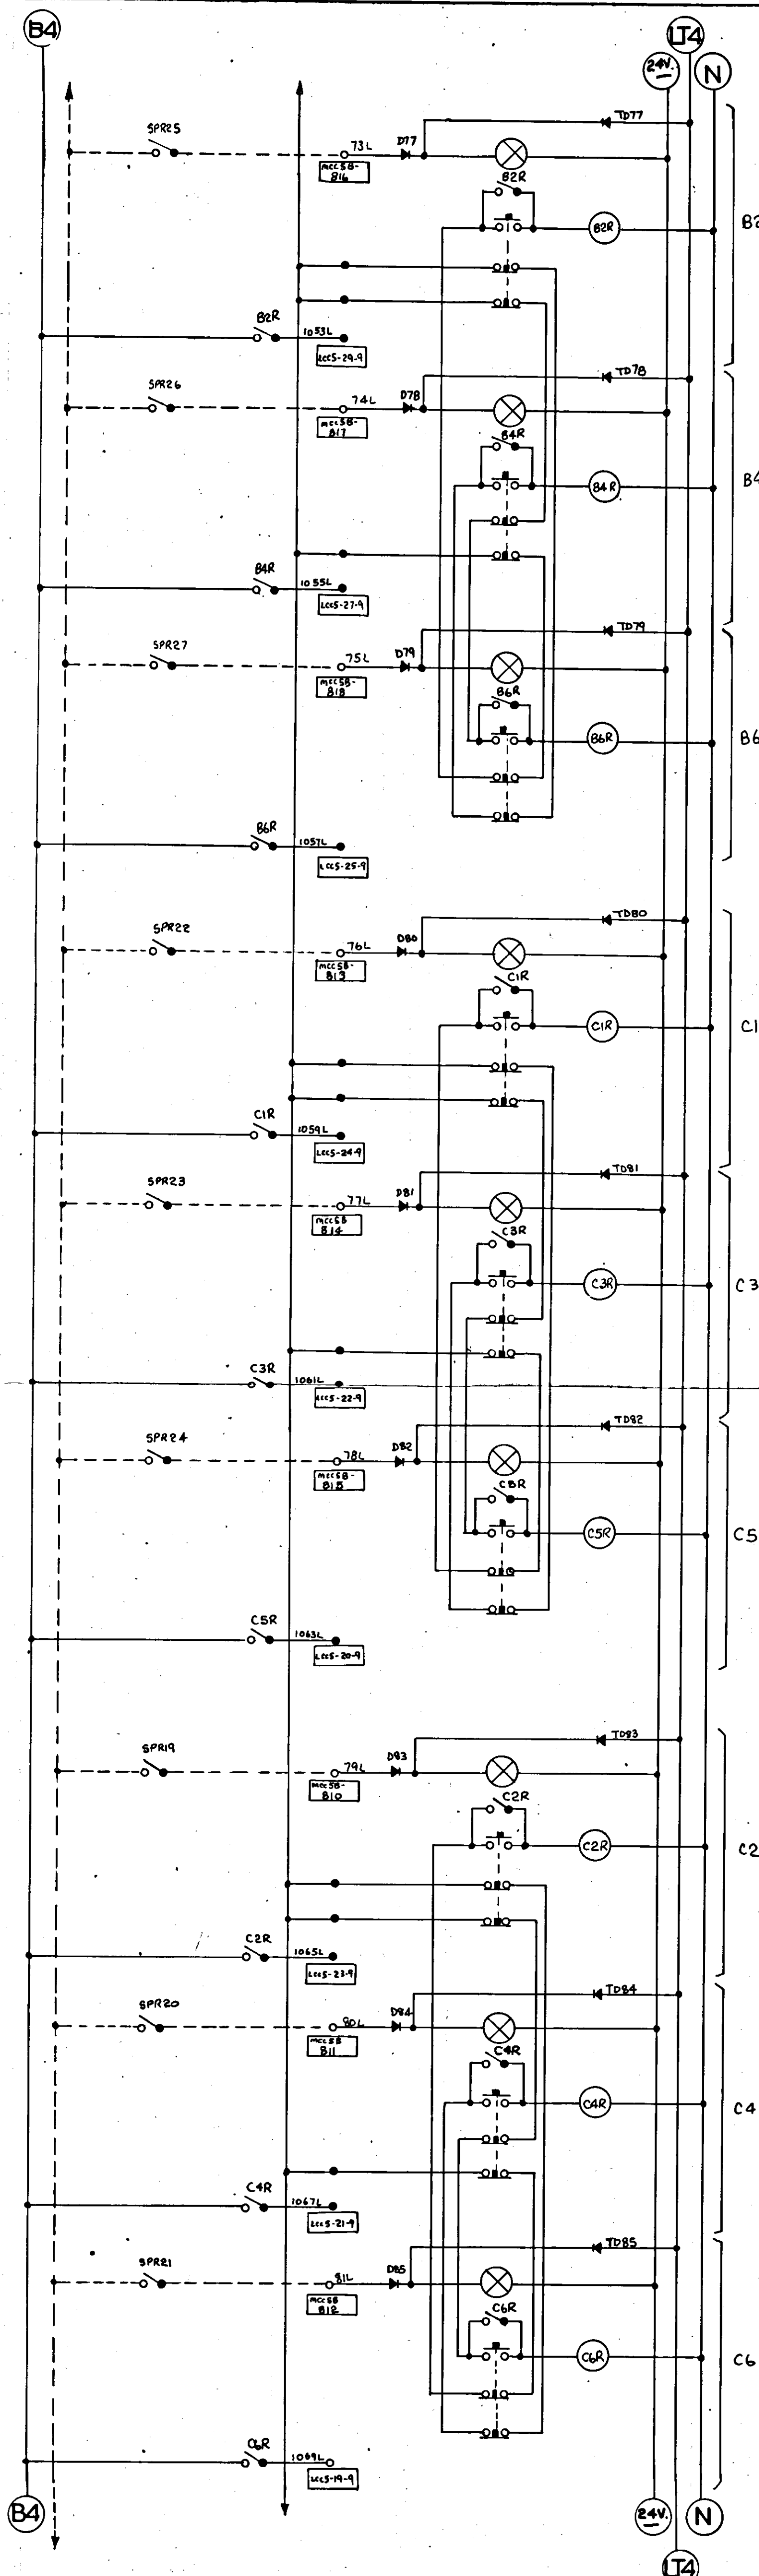


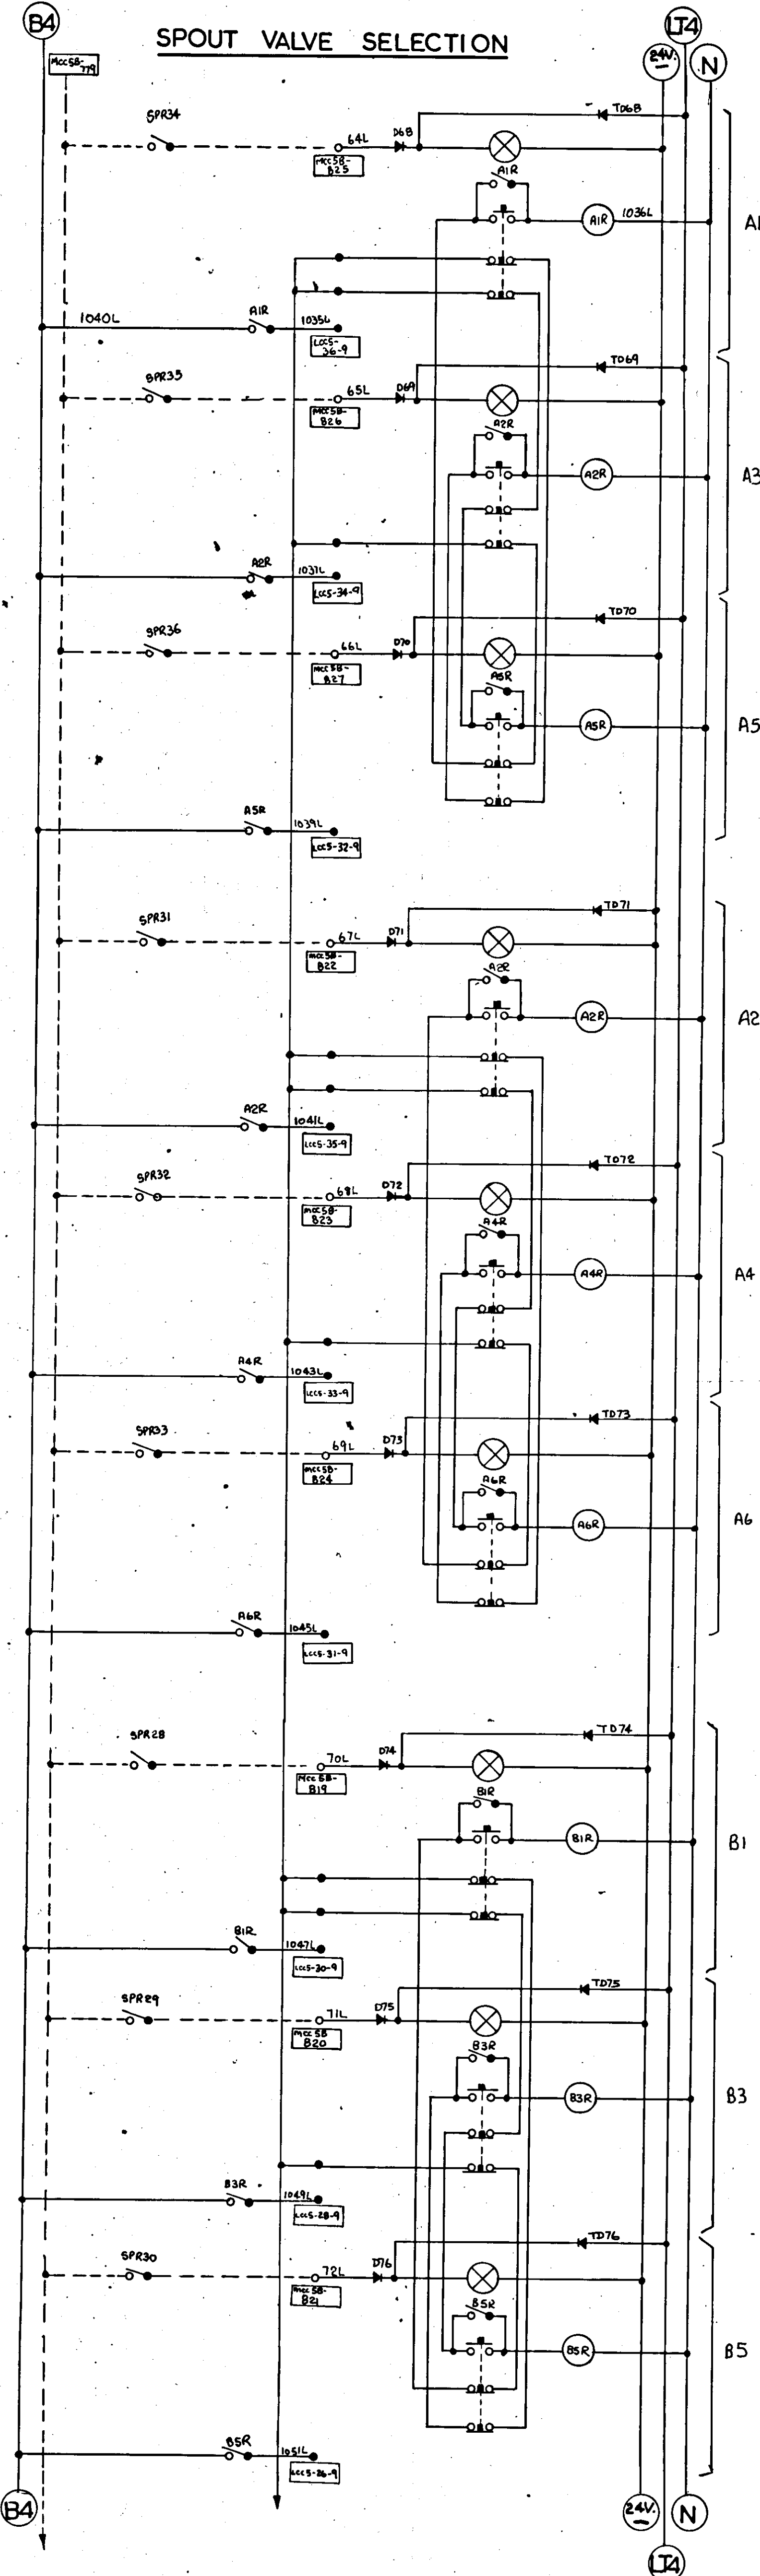

DEWHURST & PARTNER LTD.
MELBOURNE WORKS HOUNSLOW

TITLE: **SCHEMATIC DIAGRAM FOR SUPERVISORY CONTROL PANEL - SEAFORTH GRAIN TERMINAL**

REVISION:	REVISION:	REVISION:	REVISION:	REVISION:
ORIGIN: / / SGD.	ORIGIN: / / SGD.	ORIGIN: / / SGD.	ORIGIN: / / SGD.	ORIGIN: / / SGD.

THE DESIGN AND MANUFACTURING INFORMATION CONTAINED IN THIS DRAWING IS THE EXCLUSIVE RIGHT OF DEWHURST & PARTNER LTD. AND MUST NOT BE COPIED OR USED FOR MANUFACTURING PURPOSES.

ISSUE 1

SCHEMATIC DIAGRAM FOR SUPERVISORY CONTROL PANEL SHEET 11 OF 12

DTX 361AR/ 11

60