
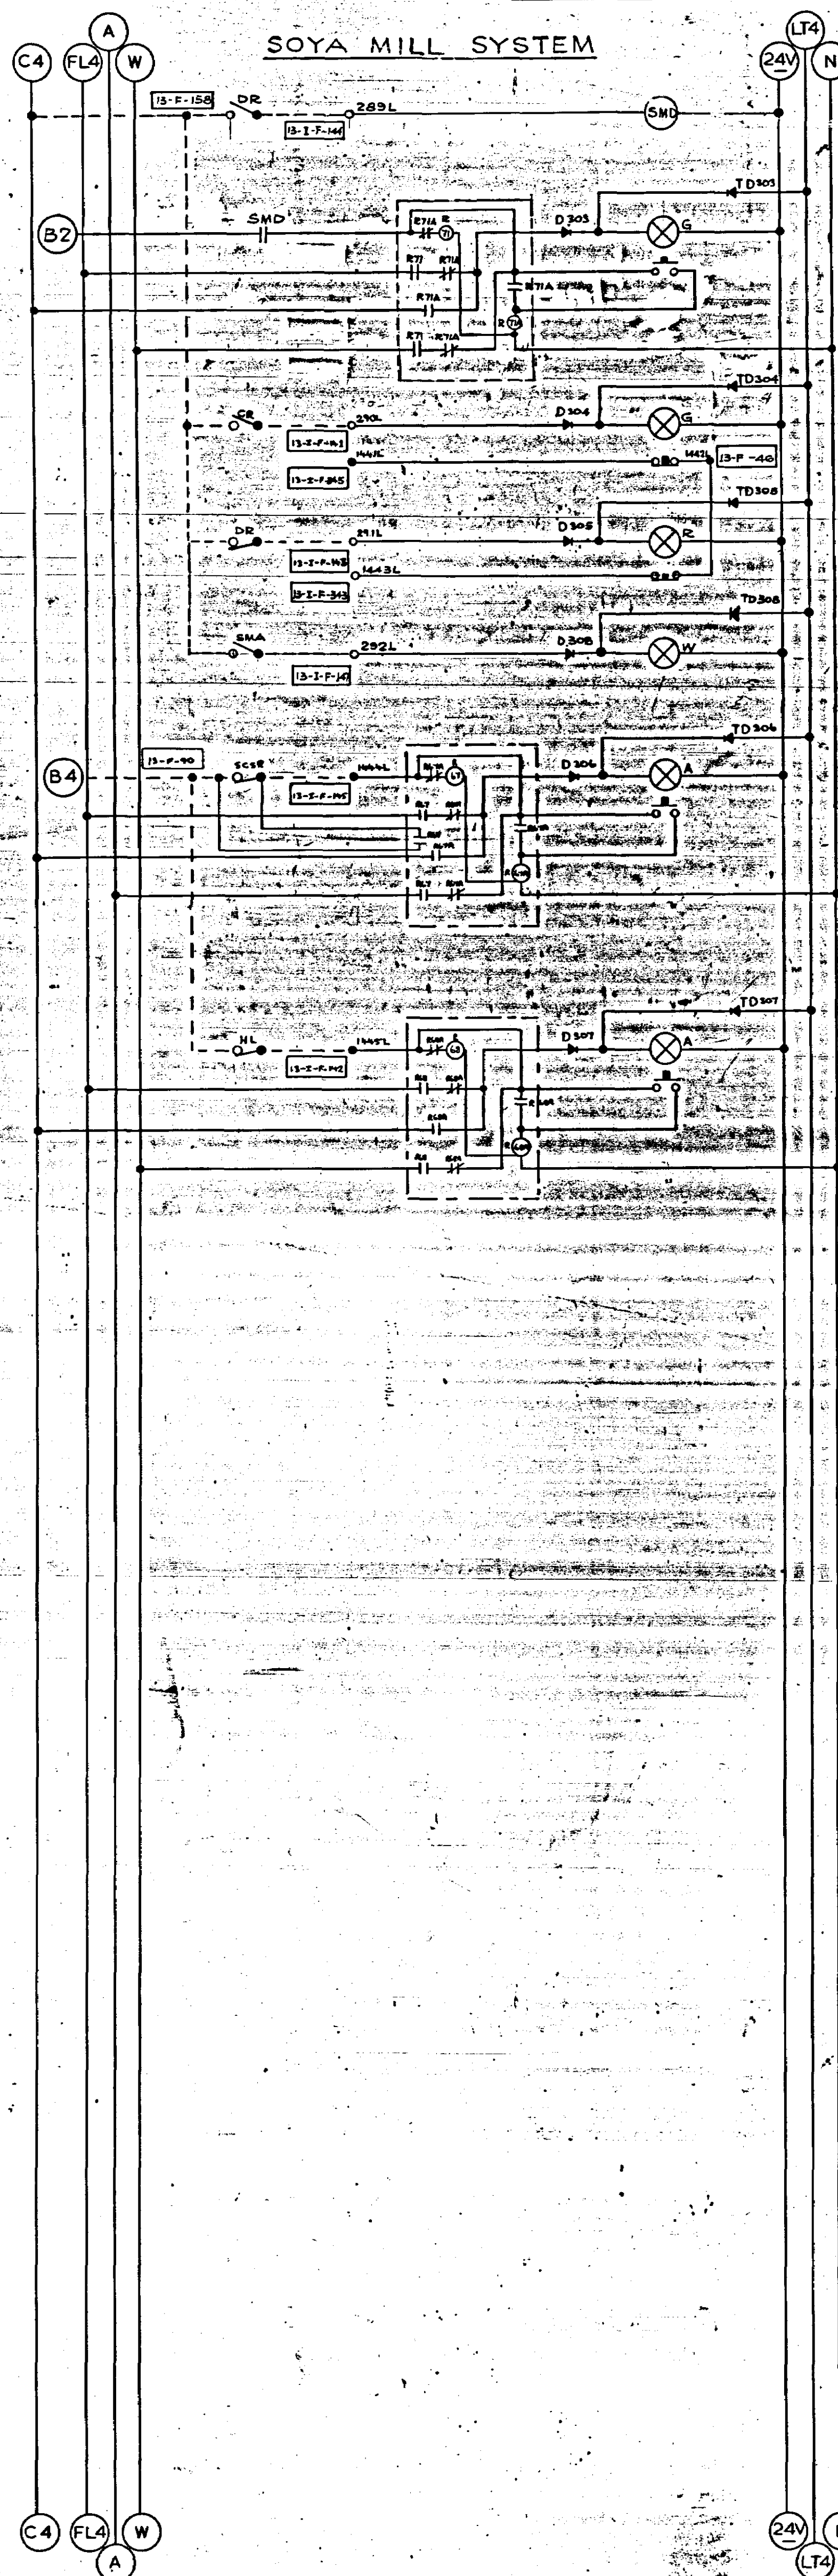


10862

LEFT HAND WING

SOYA MILL SYSTEM

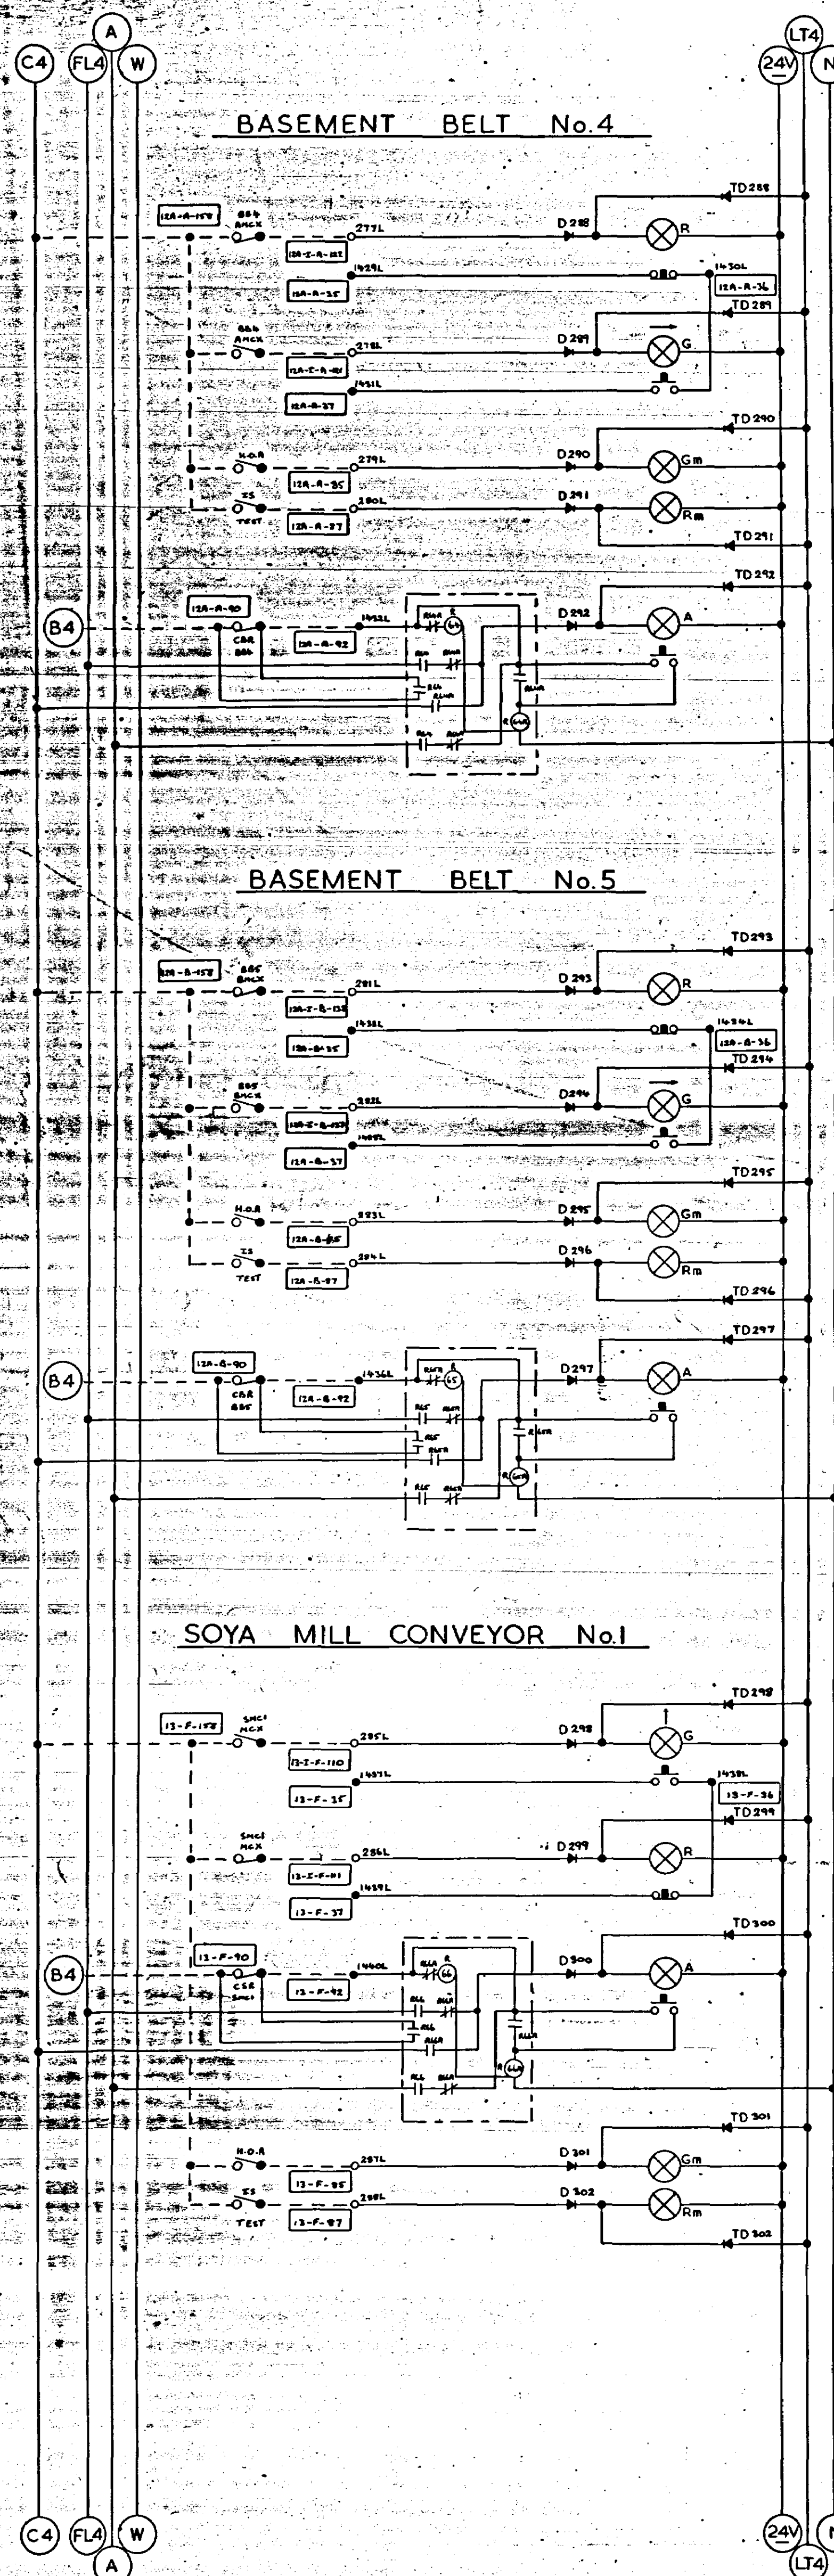

DEMAND

CONFIRM

STOP

SOYA MILL

CHÖKE

SOYA

CHUTE BLOCK

68

10862

DEWHURST & PARTNER LTD.
MELBOURNE WORKS HOUNSLOW

SCHEMATIC DIAGRAM FOR SUPERVISORY CONTROL PANEL EXTENSION SEAFORTH GRAIN TERMINAL

REVISION: 6
RELAYS SMD-RH-RTA
ADDED ON SOYA MILL
SYSTEM DEMAND BUTTON
FOR SGP
ORIGIN: 110
14/5/50 SGP. B.E.P.

REVISION: 4
SOYA MILL EXTENSION
14. TERMINAL NO. 101
ORIGIN: 110
14/5/50 SGP. B.E.P.

REVISION: 3
TERMINAL NO. 101
ORIGIN: 110
14/5/50 SGP. B.E.P.

REVISION: 2
SOYA MILL SYSTEM
ORIGIN: 110
14/5/50 SGP. B.E.P.

REVISION: 1
SOYA MILL SYSTEM
ORIGIN: 110
14/5/50 SGP. B.E.P.

DRAWN BY A. G. W.
DATE 8.11.76
CHECKED BY
APPROVED BY
DATE

THE DESIGN AND MANUFACTURING
INFORMATION CONTAINED IN
THIS DRAWING IS THE EXCLUSIVE
RIGHT OF DEWHURST & PARTNER
LTD. AND MUST NOT BE COPIED
OR USED FOR MANUFACTURING
PURPOSES.

ISSUE 123456
SCHEMATIC DIAGRAM
FOR S.C.P. EXTENSION
SHEET

DTX361AR/17