


LEFT HAND WING

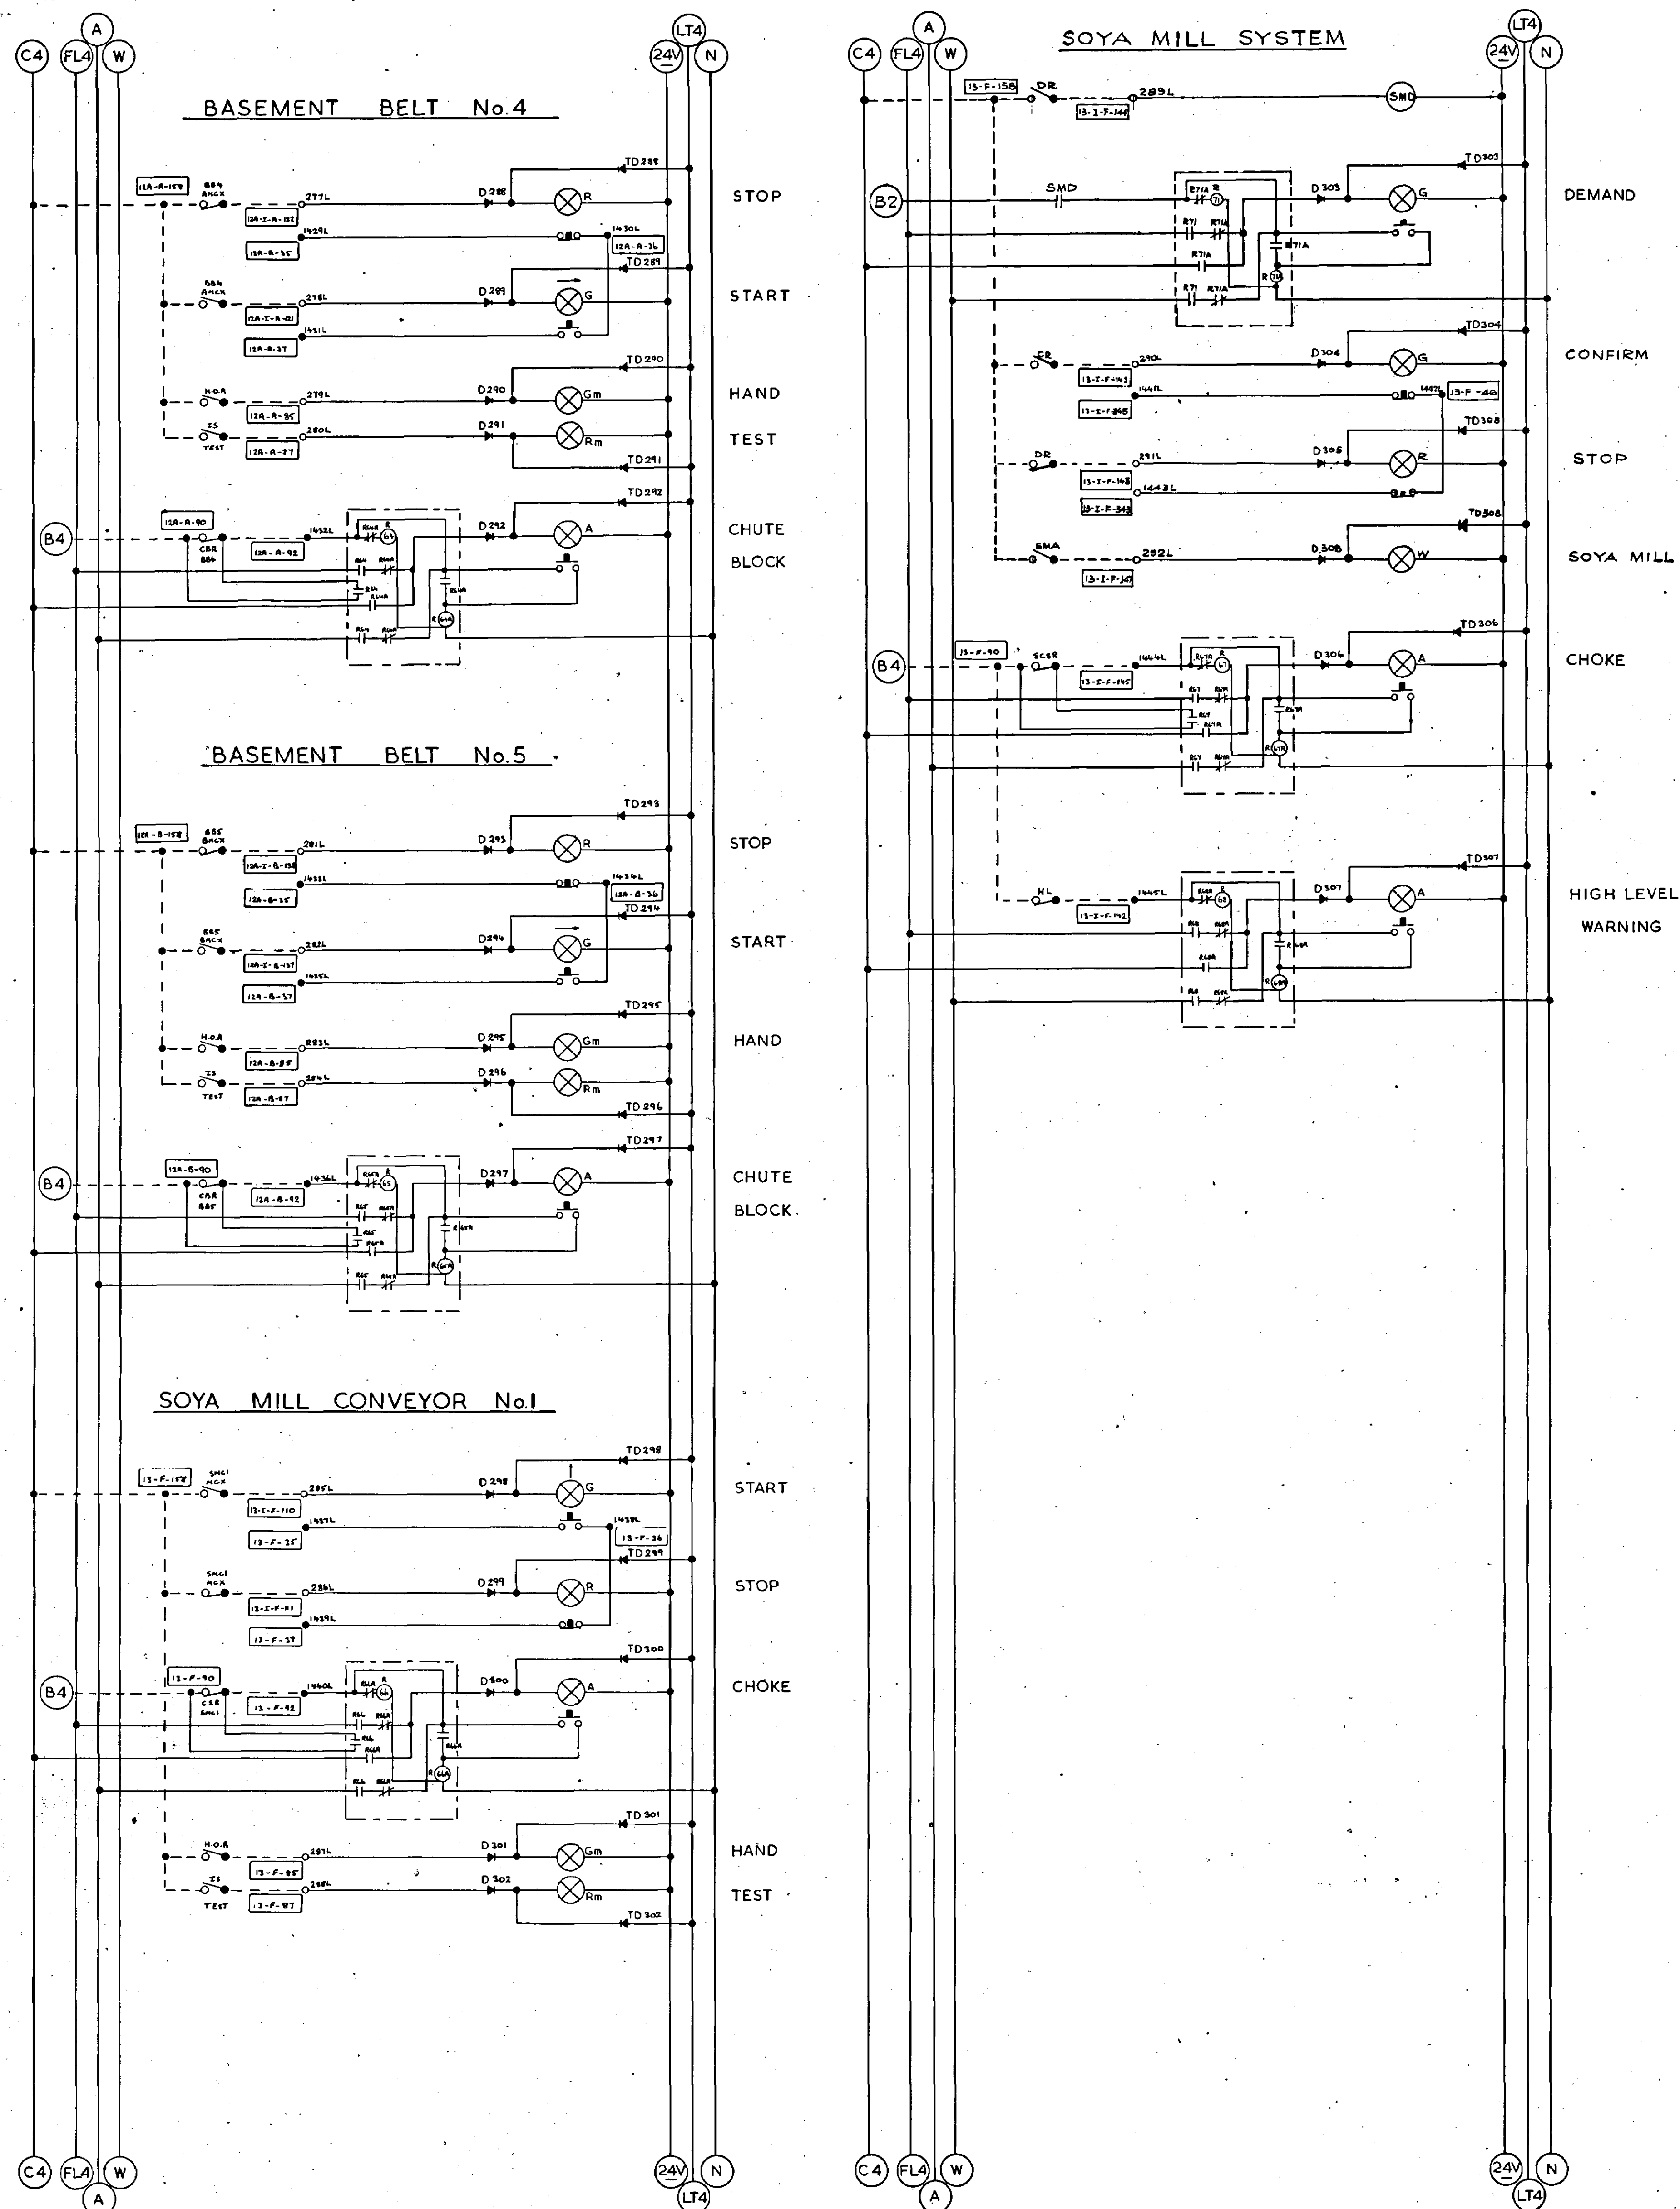

DEWHURST & PARTNER LTD.

MELBOURNE WORKS HOUNSLOW

TITLE: SCHEMATIC DIAGRAM FOR SUPERVISORY CONTROL PANEL EXTENSION SEAFORTH GRAIN TERMINAL

REVISION: 5
 RELAYS SMD-R71-R74
 ADDED TO SOYA MILL
 SYSTEM DEMAND BUTTON
 AND STARTER STOPPER
 ORIGIN: 14/5/90 SGD. E.R.P.

REVISION: 4
 SOYA MILL CONVEYOR ARMED
 IS TERMINAL AND STOP
 ORIGIN: 14/5/90 SGD. A.D.T.B.

REVISION: 3
 TERMINAL 13-F-36 ARMED
 ORIGIN: 14/5/90 SGD. A.D.T.B.

REVISION: 2
 SOYA MILL SYSTEM
 ORIGIN: 14/5/90 SGD. A.D.T.B.

REVISION: 1
 CHUTE BLOCK ARMED
 TO SOYA MILL
 ORIGIN: 14/5/90 SGD. A.D.T.B.

DRAWN BY: A.B.
 DATE: 8.11.76
 CHECKED BY:
 APPROVED BY:
 DATE:

THE DESIGN AND MANUFACTURING
 INFORMATION CONTAINED IN
 THIS DRAWING IS THE EXCLUSIVE
 RIGHT OF DEWHURST & PARTNER
 LTD. AND MUST NOT BE COPIED
 OR USED FOR MANUFACTURING
 PURPOSES

ISSUE 123456
 SCHEMATIC DIAGRAM
 FOR S.C.P. EXTENSION
 SHEET

DTX361AR/17