


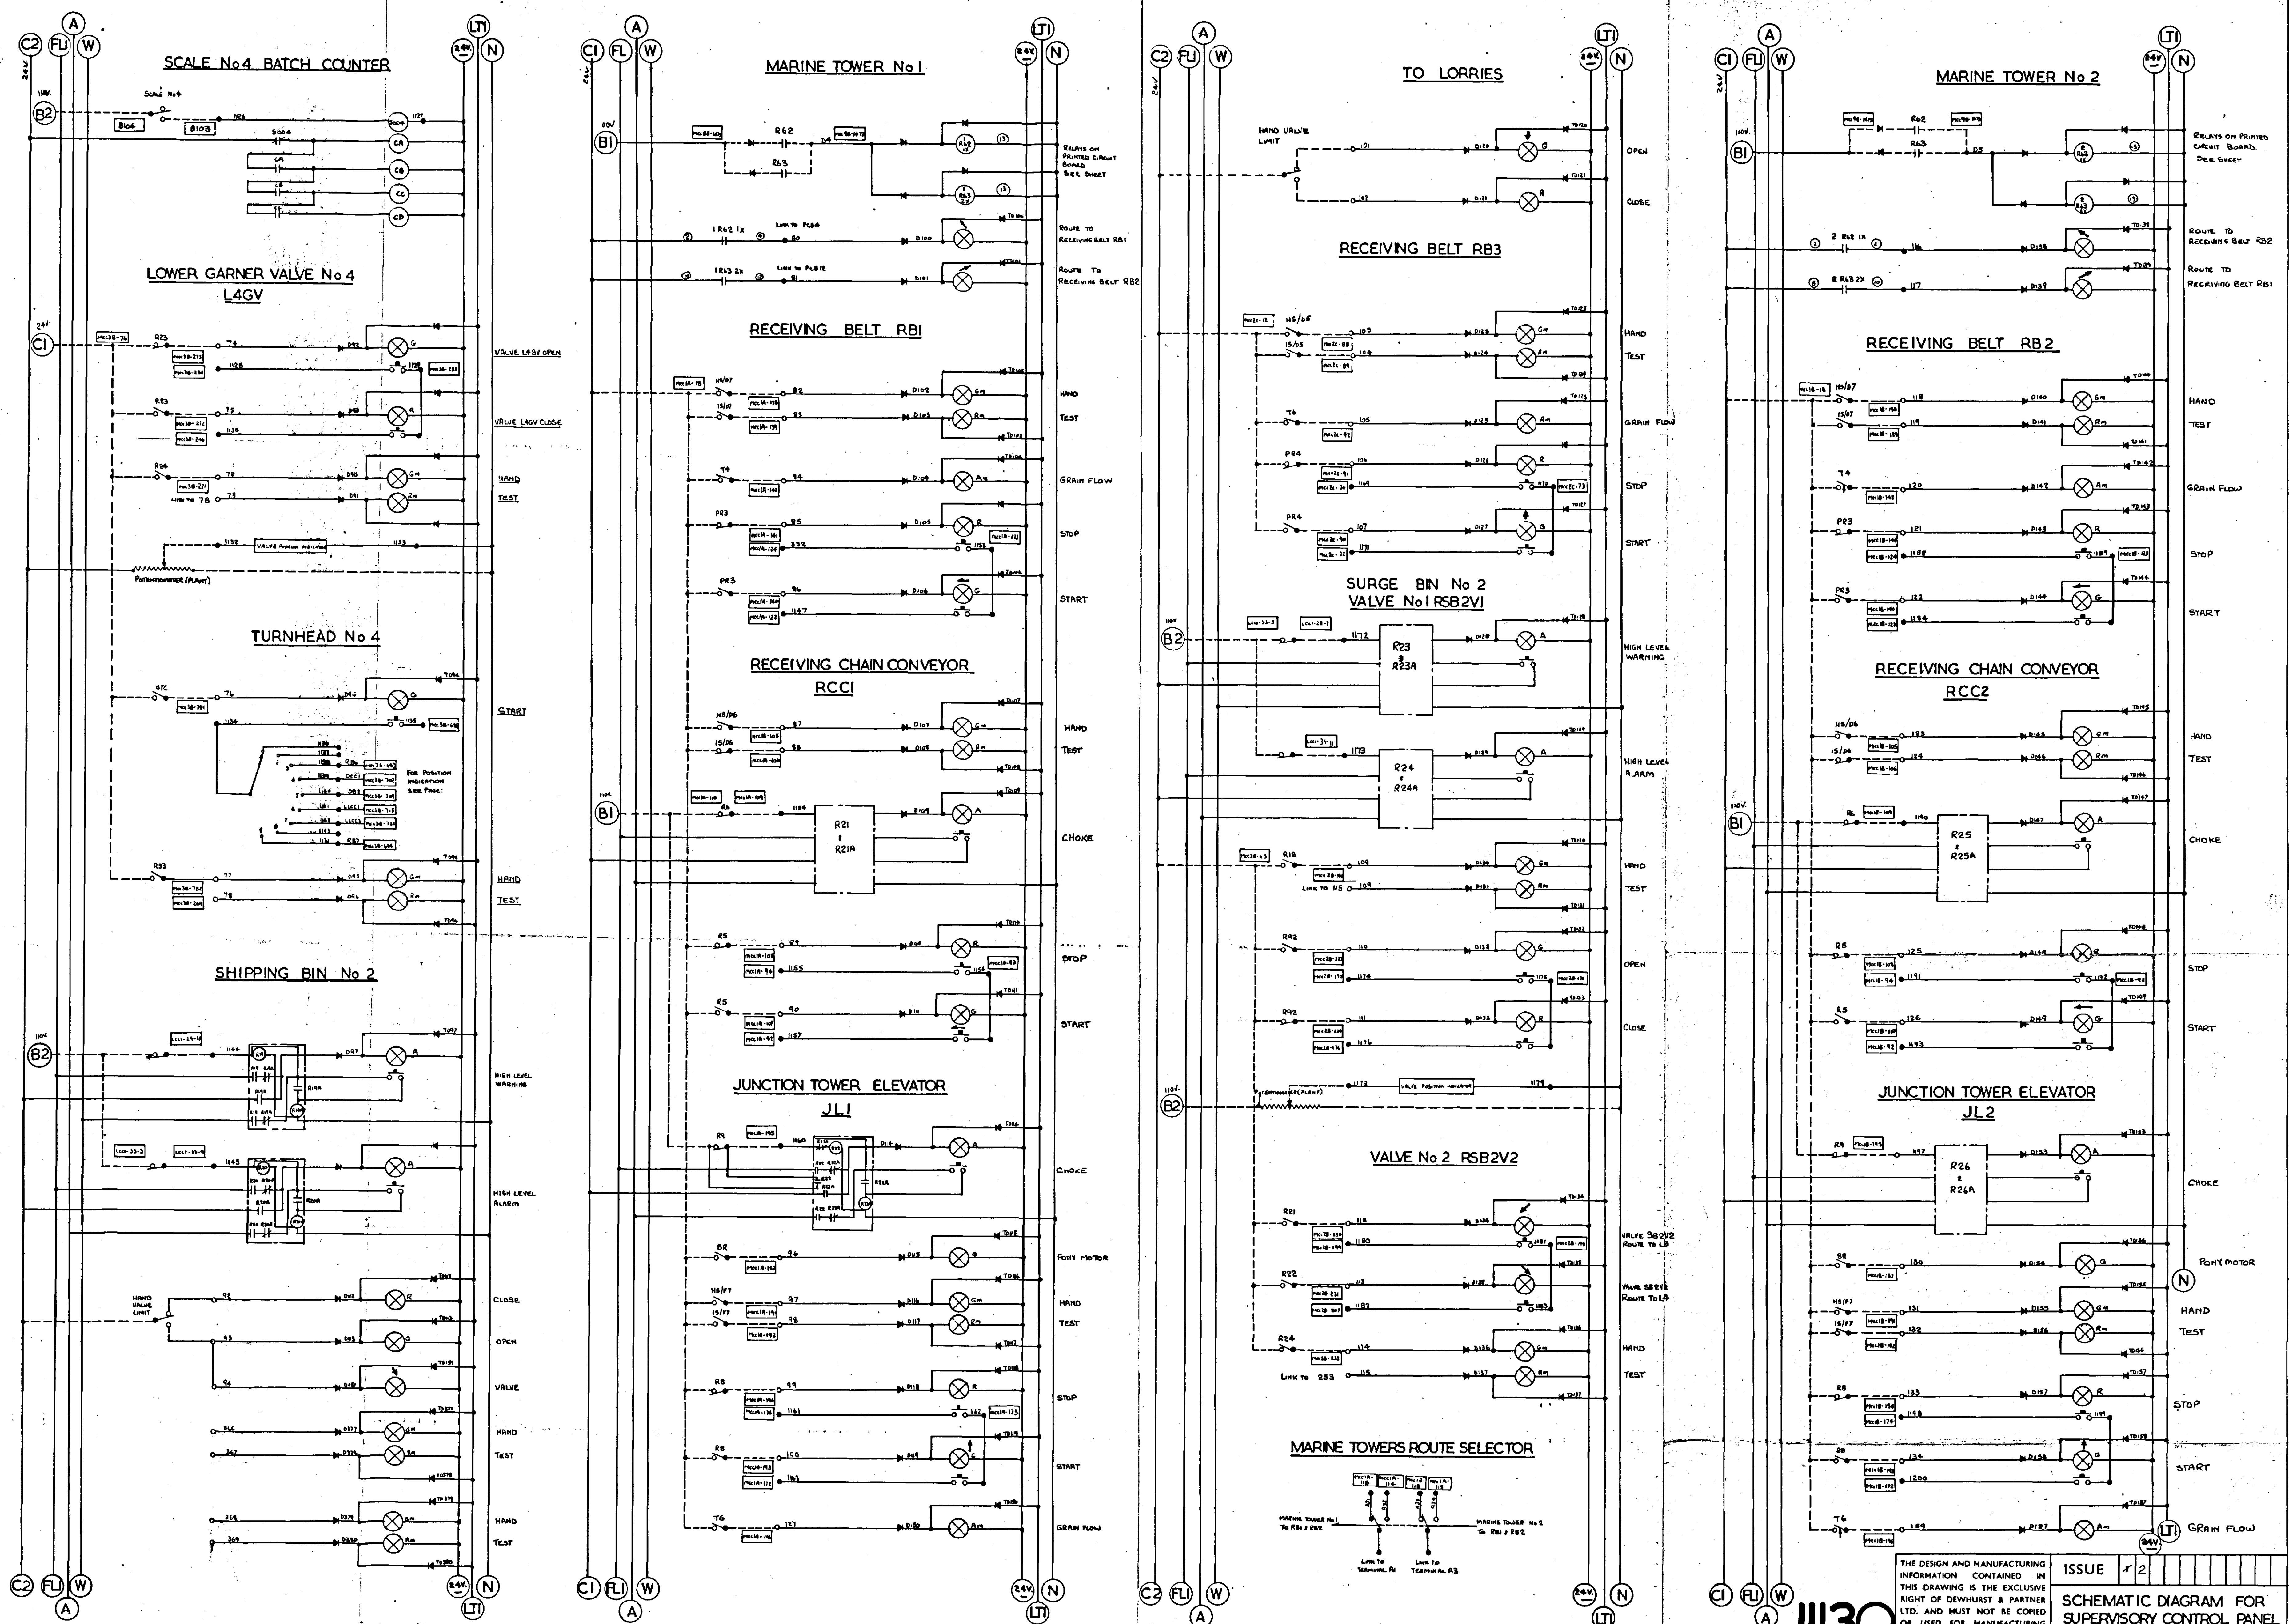

DEWHURST & PARTNER LTD.  
MELBOURNE WORKS HOUNSLOW

TITLE: SCHEMATIC DIAGRAM FOR SUPERVISORY CONTROL PANEL - SEAFORTH GRAIN TERMINAL

|                  |                  |                  |                  |
|------------------|------------------|------------------|------------------|
| REVISION:        | REVISION:        | REVISION:        | REVISION:        |
| ORIGIN: / / SGD. | ORIGIN: / / SGD. | ORIGIN: / / SGD. | ORIGIN: / / SGD. |

|                  |                       |                             |
|------------------|-----------------------|-----------------------------|
| REVISION: 1      | DRAWN BY: J. J. J.    | KEY DIAG. No.               |
| DATE: 15/7/77    | CHECKED BY: J. J. J.  | EXT. DIAG. No.              |
| ORIGIN: J. J. J. | APPROVED BY: J. J. J. | REL. DIAG. No.              |
| DATE: 15/7/77    | DATE: 15/7/77         | PANEL LAYOUT No. NTS 361 AR |

THE DESIGN AND MANUFACTURING INFORMATION CONTAINED IN THIS DRAWING IS THE EXCLUSIVE RIGHT OF DEWHURST & PARTNER LTD. AND MUST NOT BE COPIED OR USED FOR MANUFACTURING PURPOSES.

ISSUE 1 2

SCHEMATIC DIAGRAM FOR SUPERVISORY CONTROL PANEL SHEET 3 OF 12

DTX 361 AR/3