
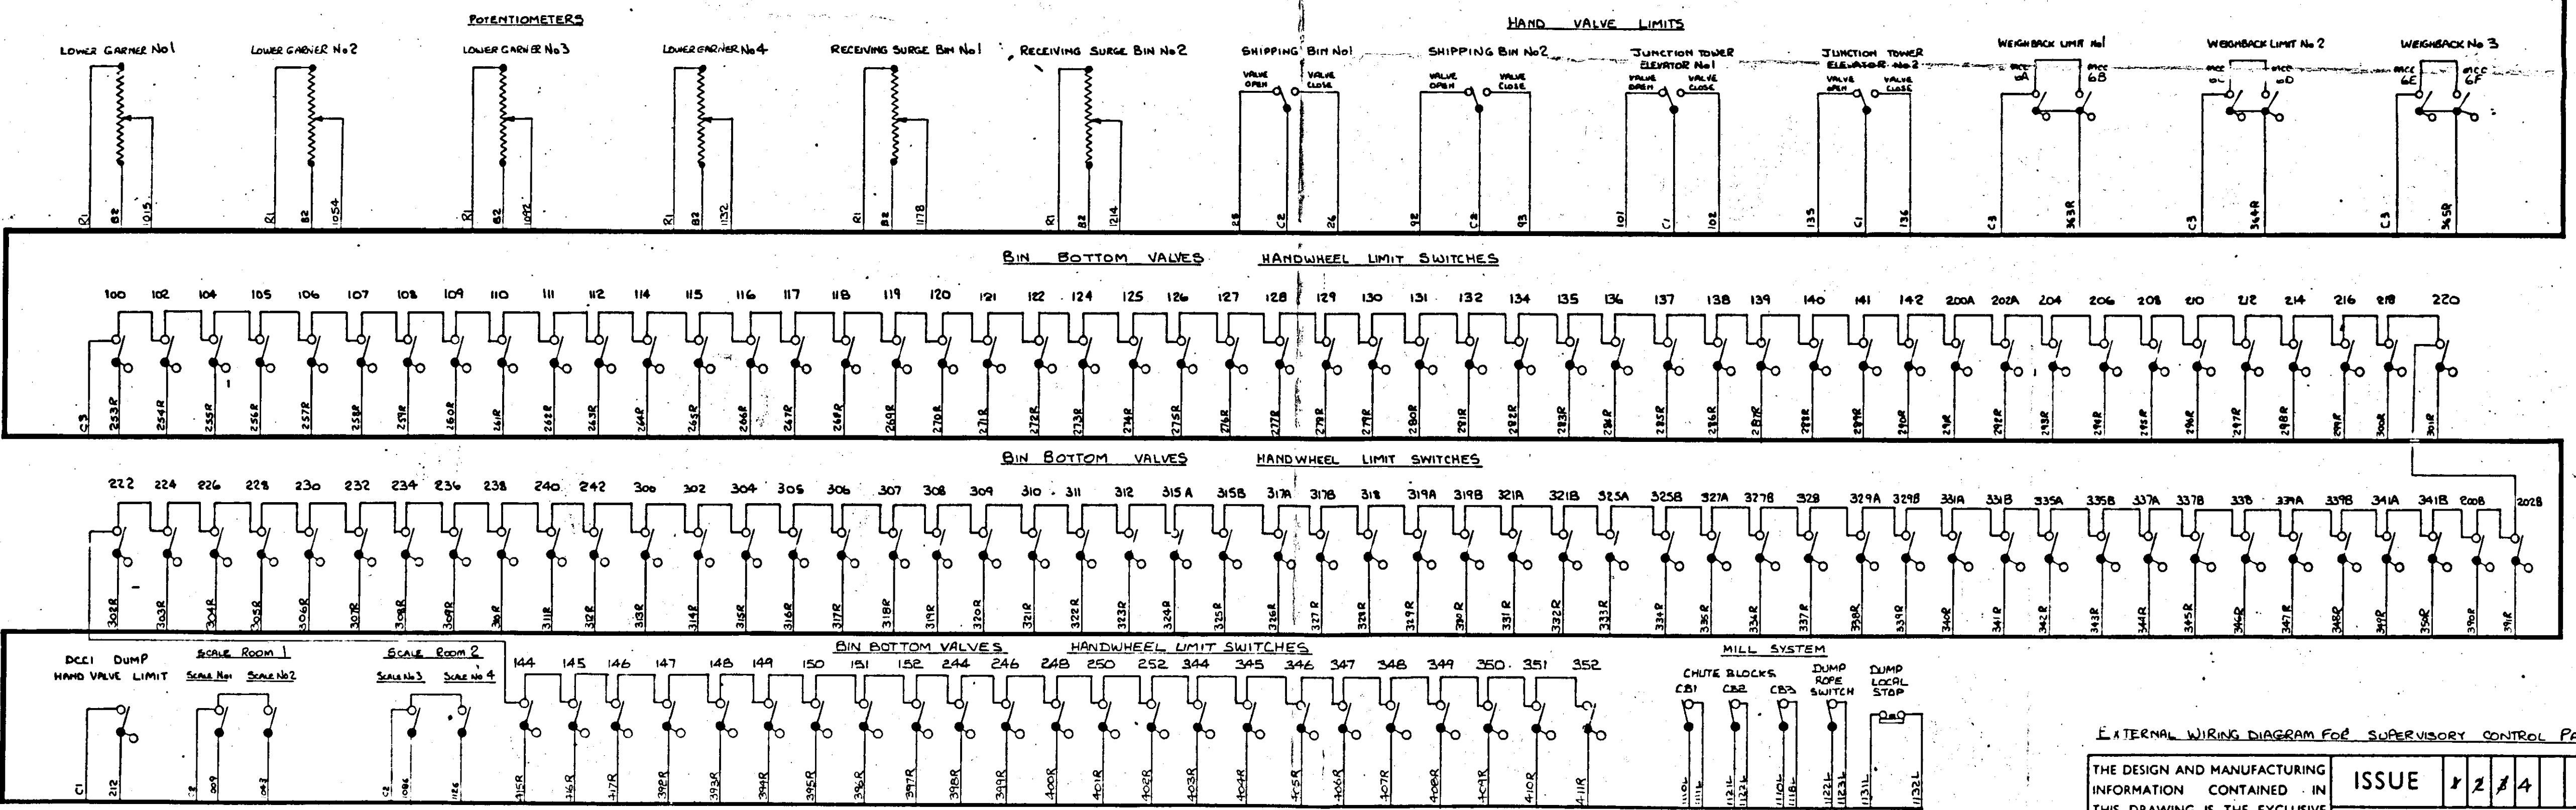


63

63

- JBSW1 37 CORES
- JBSW2 31 CORES
- JBSW3 100 CORES
- JBSW4 88 CORES
- JBSW5 86 CORES
- LCC1 9 CORES
- LCC5 3 CORES
- LCC6 8 CORES
- LCC7 9 CORES
- TRB5 85 CORES
- TRB6 42 CORES
- TRB7 75 CORES
- TRB8 31 CORES
- MCC6 85 CORES
- MCC6A 3 CORES
- MCC6B 2 CORES
- MCC6C 2 CORES
- MCC6D 2 CORES
- MCC6E 2 CORES
- MCC6F 2 CORES
- ALL 1 CORE
- MCC9B 2 CORES
- MCC9B 2 CORES

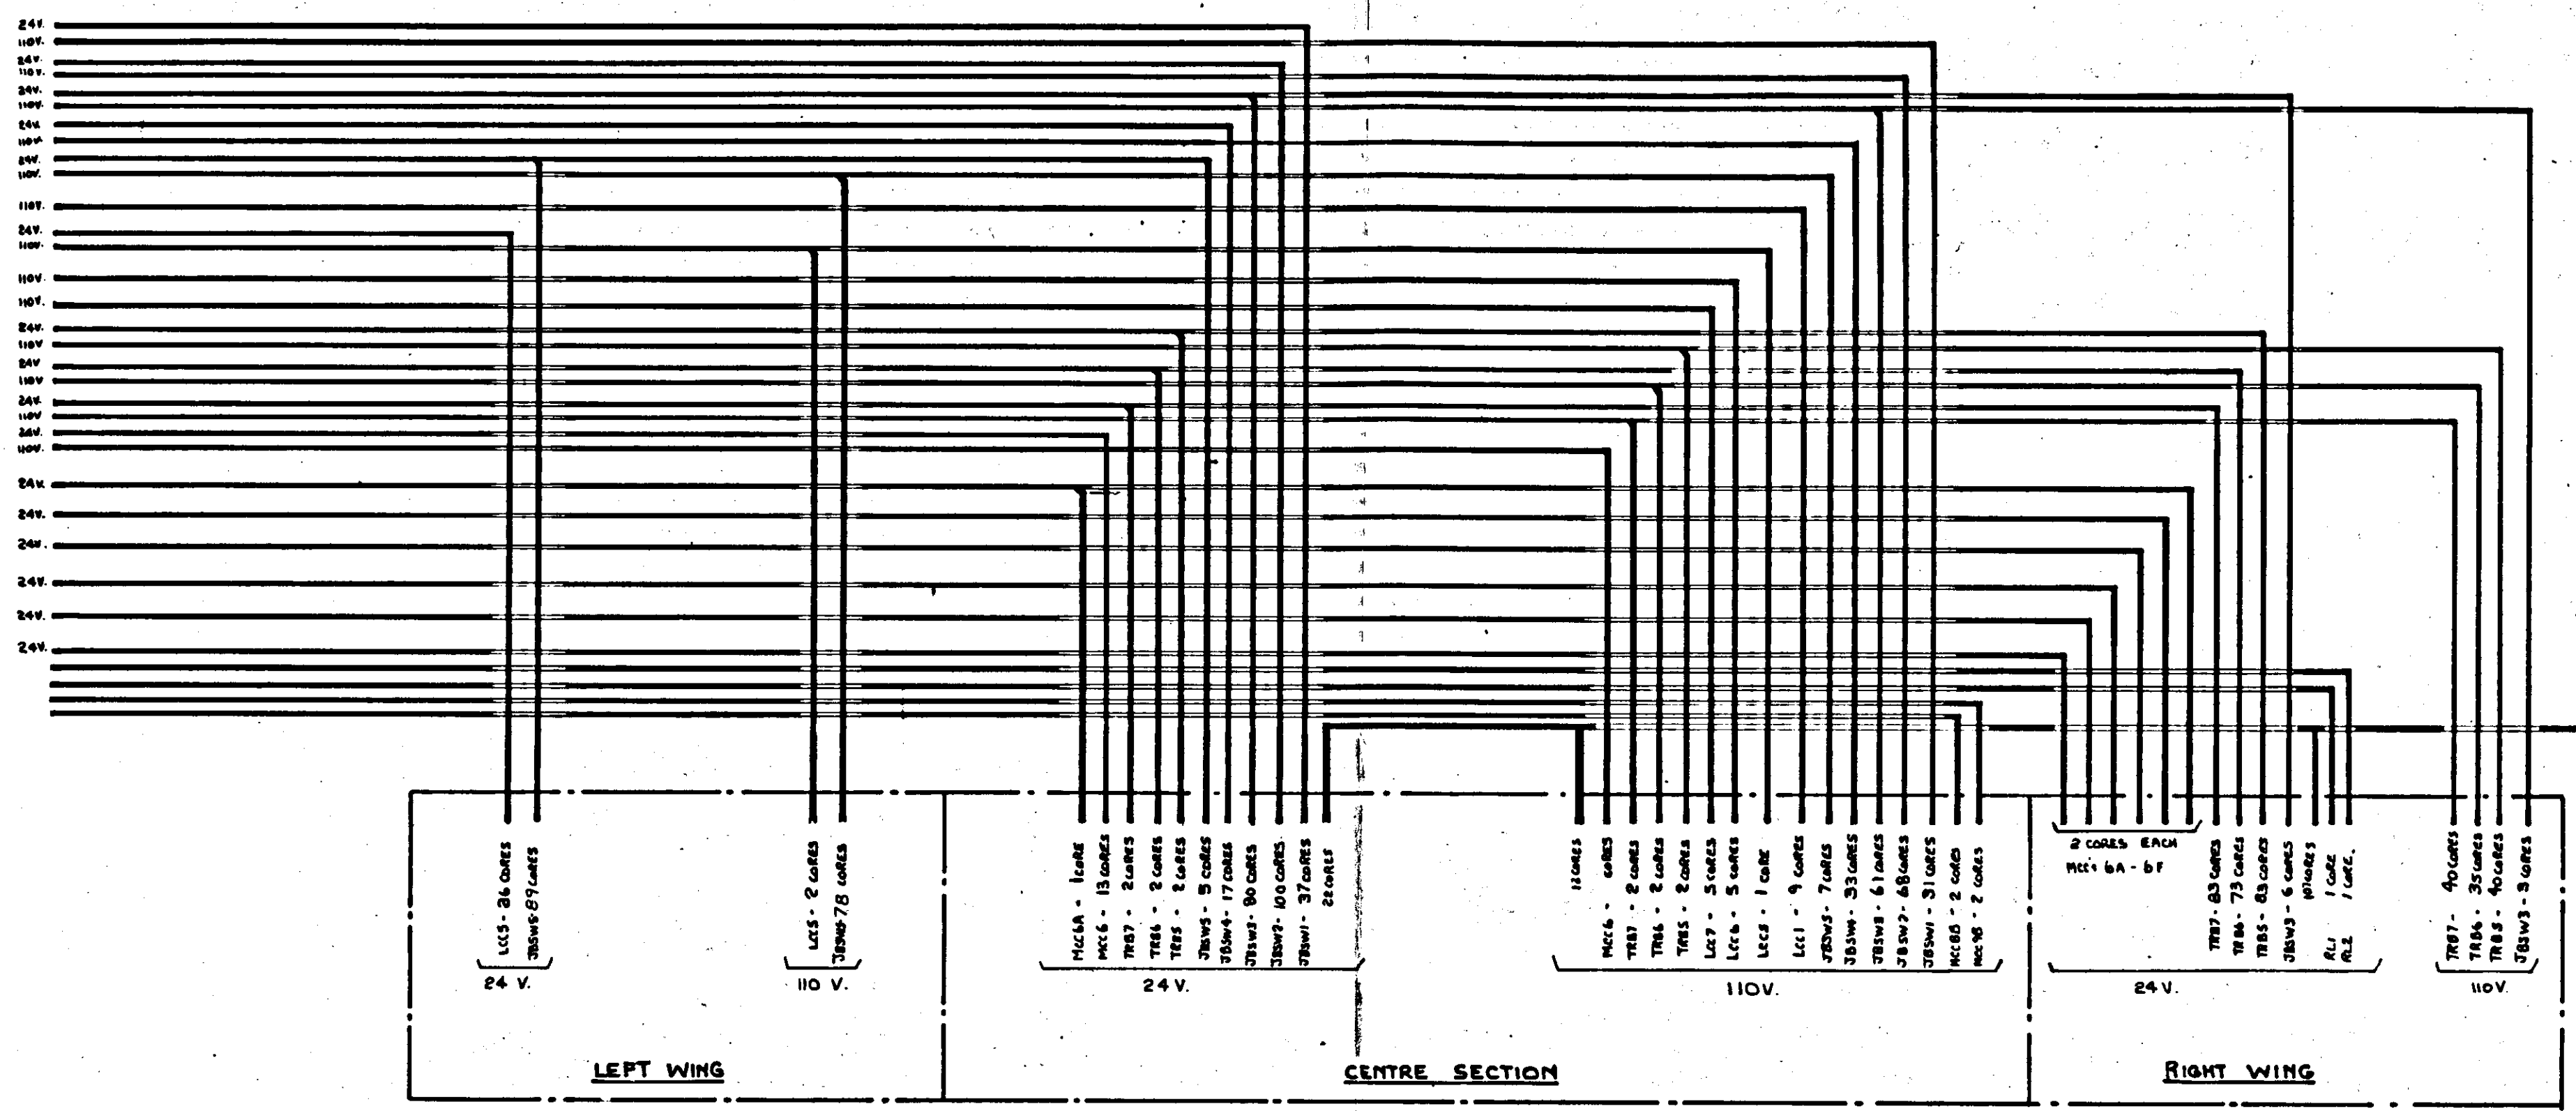

NUMBERS ADJACENT LOOMS INDICATE TERMINAL DESIGNATION ONLY - NOT WIRE NUMBERS

HANDWHEEL LIMITS SHOWN WITH VALVES FULLY CLOSED

DEWHURST & PARTNER LTD.
MELBOURNE WORKS HOUNSLOW

TITLE:
EXTERNAL WIRING DIAGRAM FOR SUPERVISORY CONTROL PANEL

REVISION 3
SECTION F HANDWHEEL LIMITS ADDED, MILL SYSTEM SWITCHES ADDED.
ORIGIN ICD
14/8/72 SGD. JX

REVISION 2
NO OF CORES CORRECTED.
SCALE ROOM CONTACTS ADDED.
ORIGIN ICD
14/3/72 SGD.

REVISION 1
GENERAL MODS
ORIGIN ICD
14/2/72 SGD. JS

DRAWN BY
DATE
CHECKED BY
APPROVED BY
DATE

KEY DIAG. No.
EXT. DIAG. No.
REL. DIAG. No.
PANEL LAYOUT No.

EXTERNAL WIRING DIAGRAM FOR SUPERVISORY CONTROL PANEL

THE DESIGN AND MANUFACTURING INFORMATION CONTAINED IN THIS DRAWING IS THE EXCLUSIVE RIGHT OF DEWHURST & PARTNER LTD. AND MUST NOT BE COPIED OR USED FOR MANUFACTURING PURPOSES.

ISSUE 1 2 4

RTX 361 AR

11140