


10728

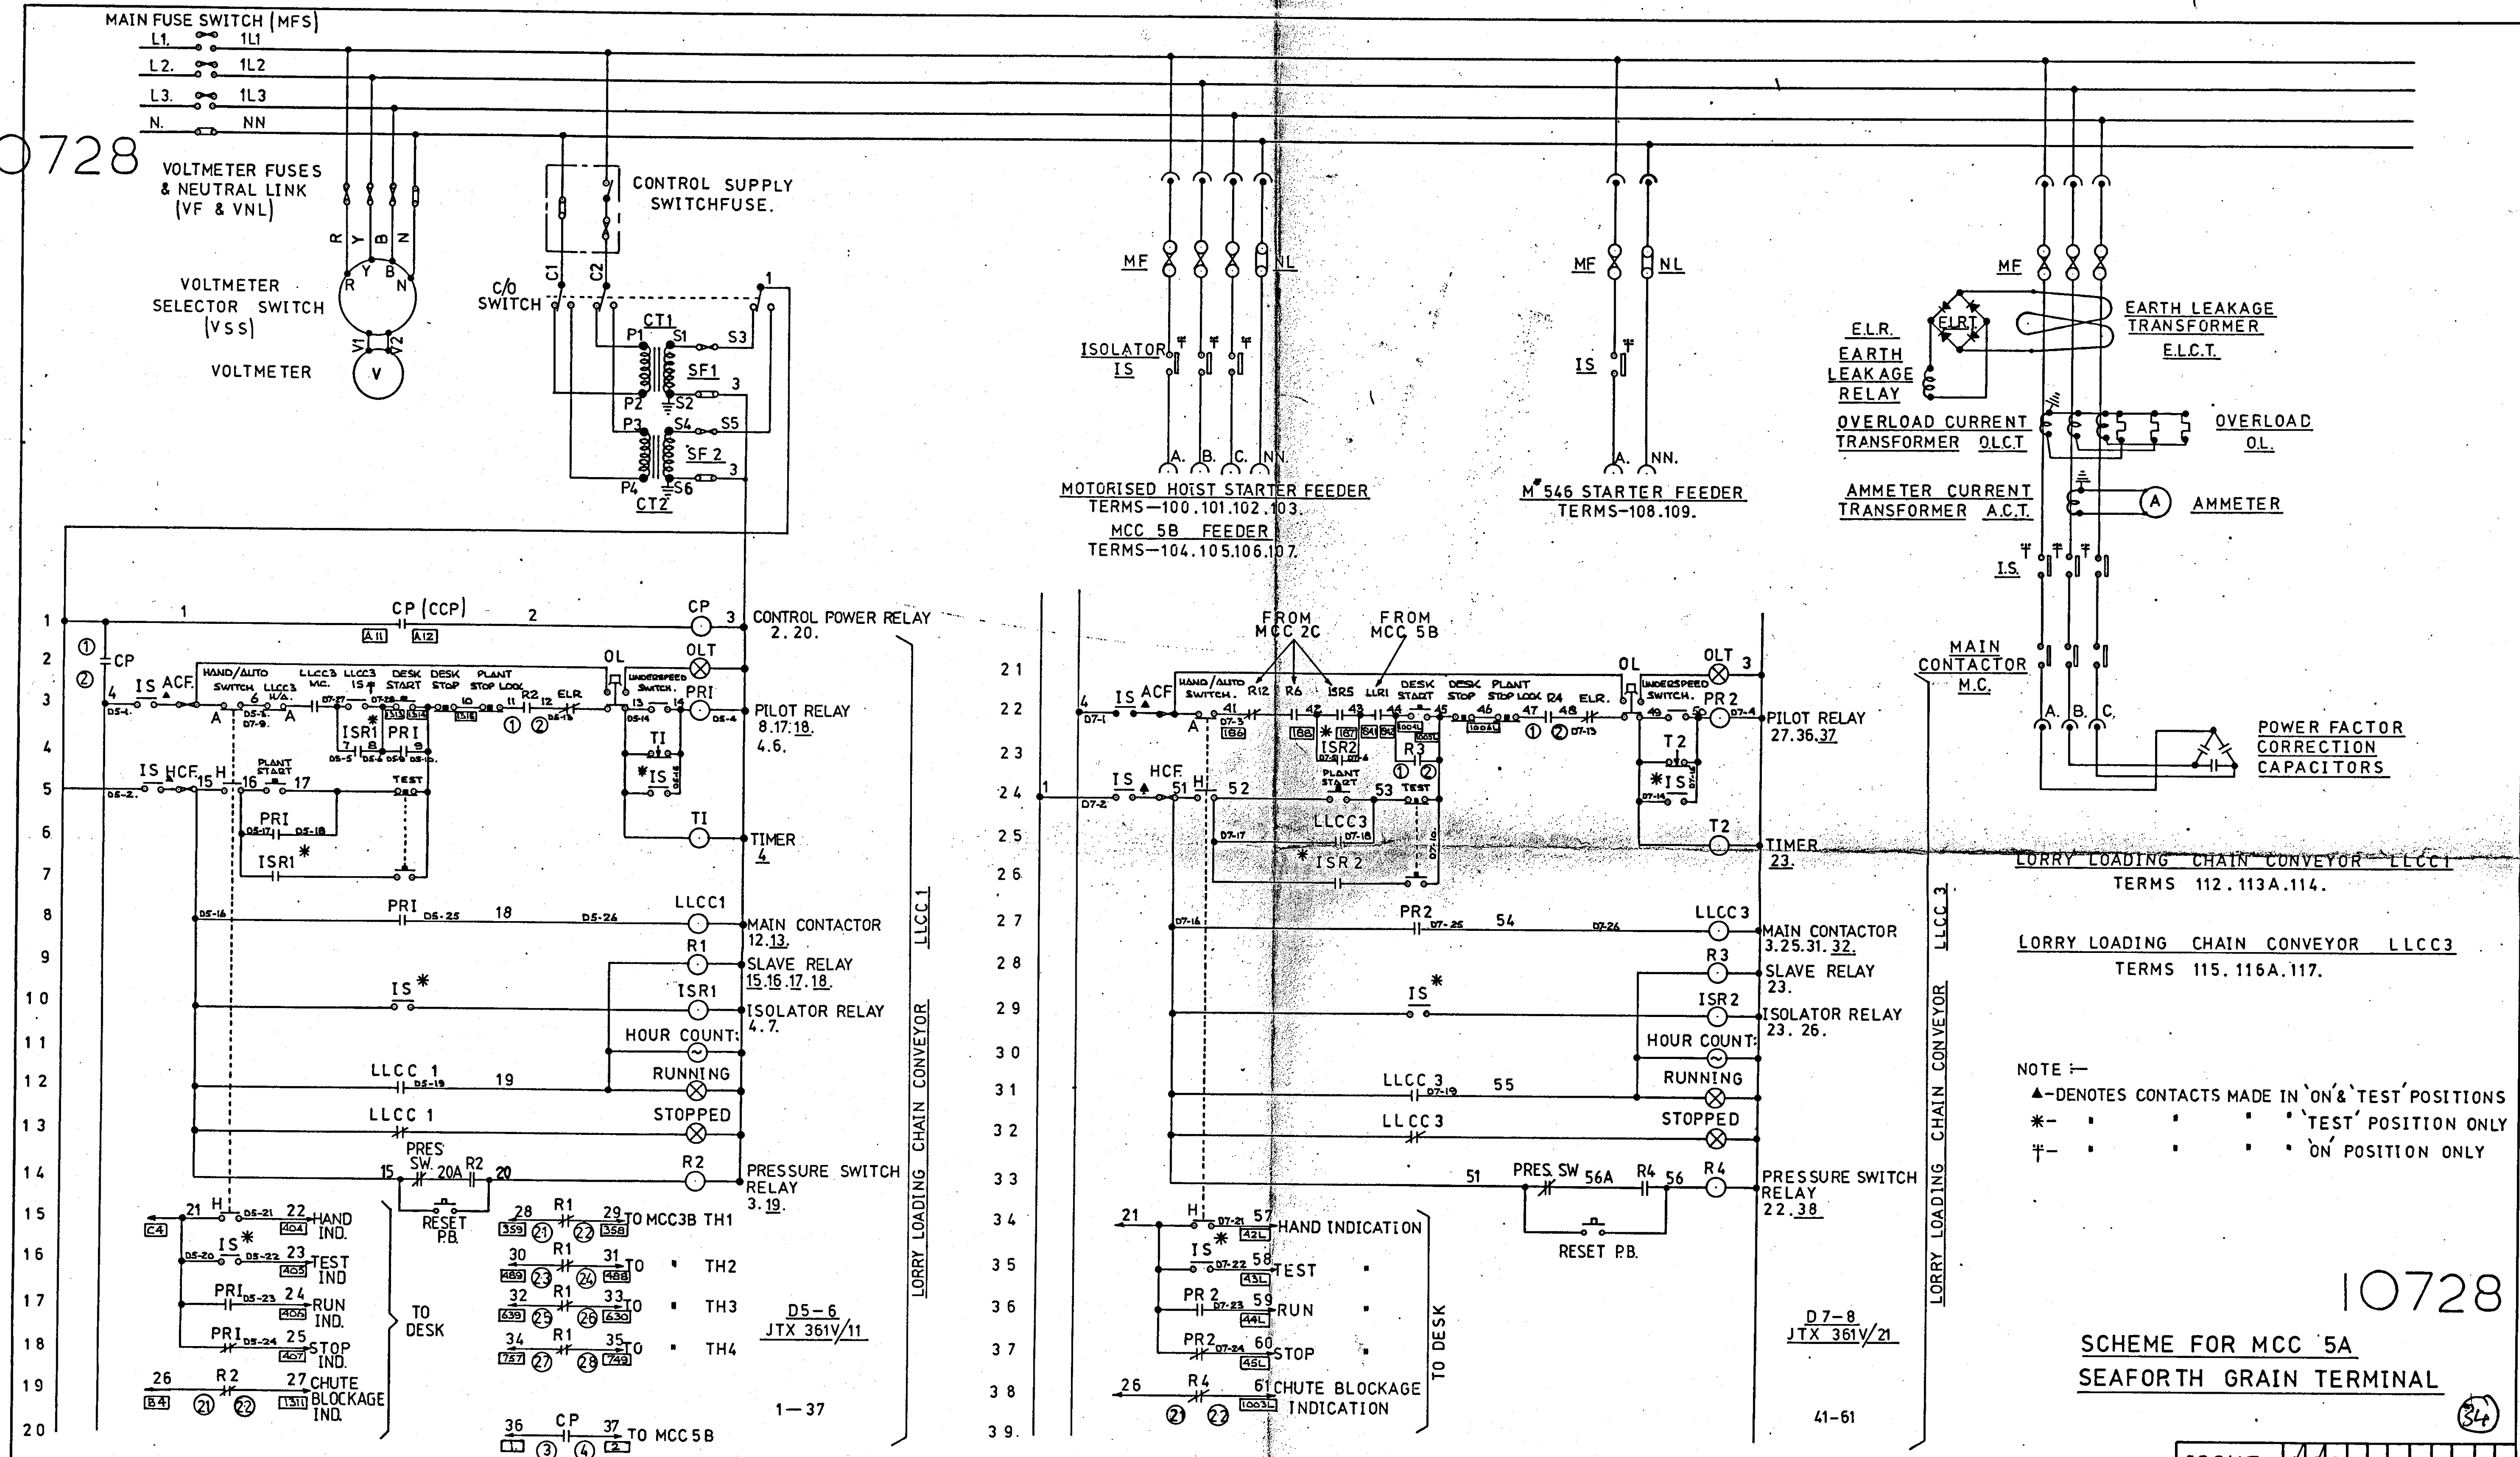

10728

SCHEME FOR MCC 5A
SEAFORTH GRAIN TERMINAL

ISSUE	1	2	3							
-------	---	---	---	--	--	--	--	--	--	--

CTX 361 AD

CTX 361 AD

DEWHURST & PARTNER LTD
MELBOURNE WORKS HOUNSLOW

TITLE —
SCHEME FOR MCC 5A — SEAFORTH GRAIN TERMINAL

REVISION 3	REVISION 2
Line 14: R2 contact	R1 & R2 WERE
& reset PB added	ACROSS MAIN
Line 33: R4 contact	CONT; COILS
& reset PB added	27-5-71
14-7-81 R.H.N.	

REVISION 1
LLCC.1. SUSTAINING
CONTACTS WERE
ON MC
20-4-71

	DRAWN BY
NG	DATE 16-3-71
E	CHECKED BY
	APPROVED BY
	DATE

KEY.DIA.N°
EXT.DIA.N° RTX 361 AD
REL.DIA.N°
PANEL LAYOUT. GTX 361AD

34