


10728

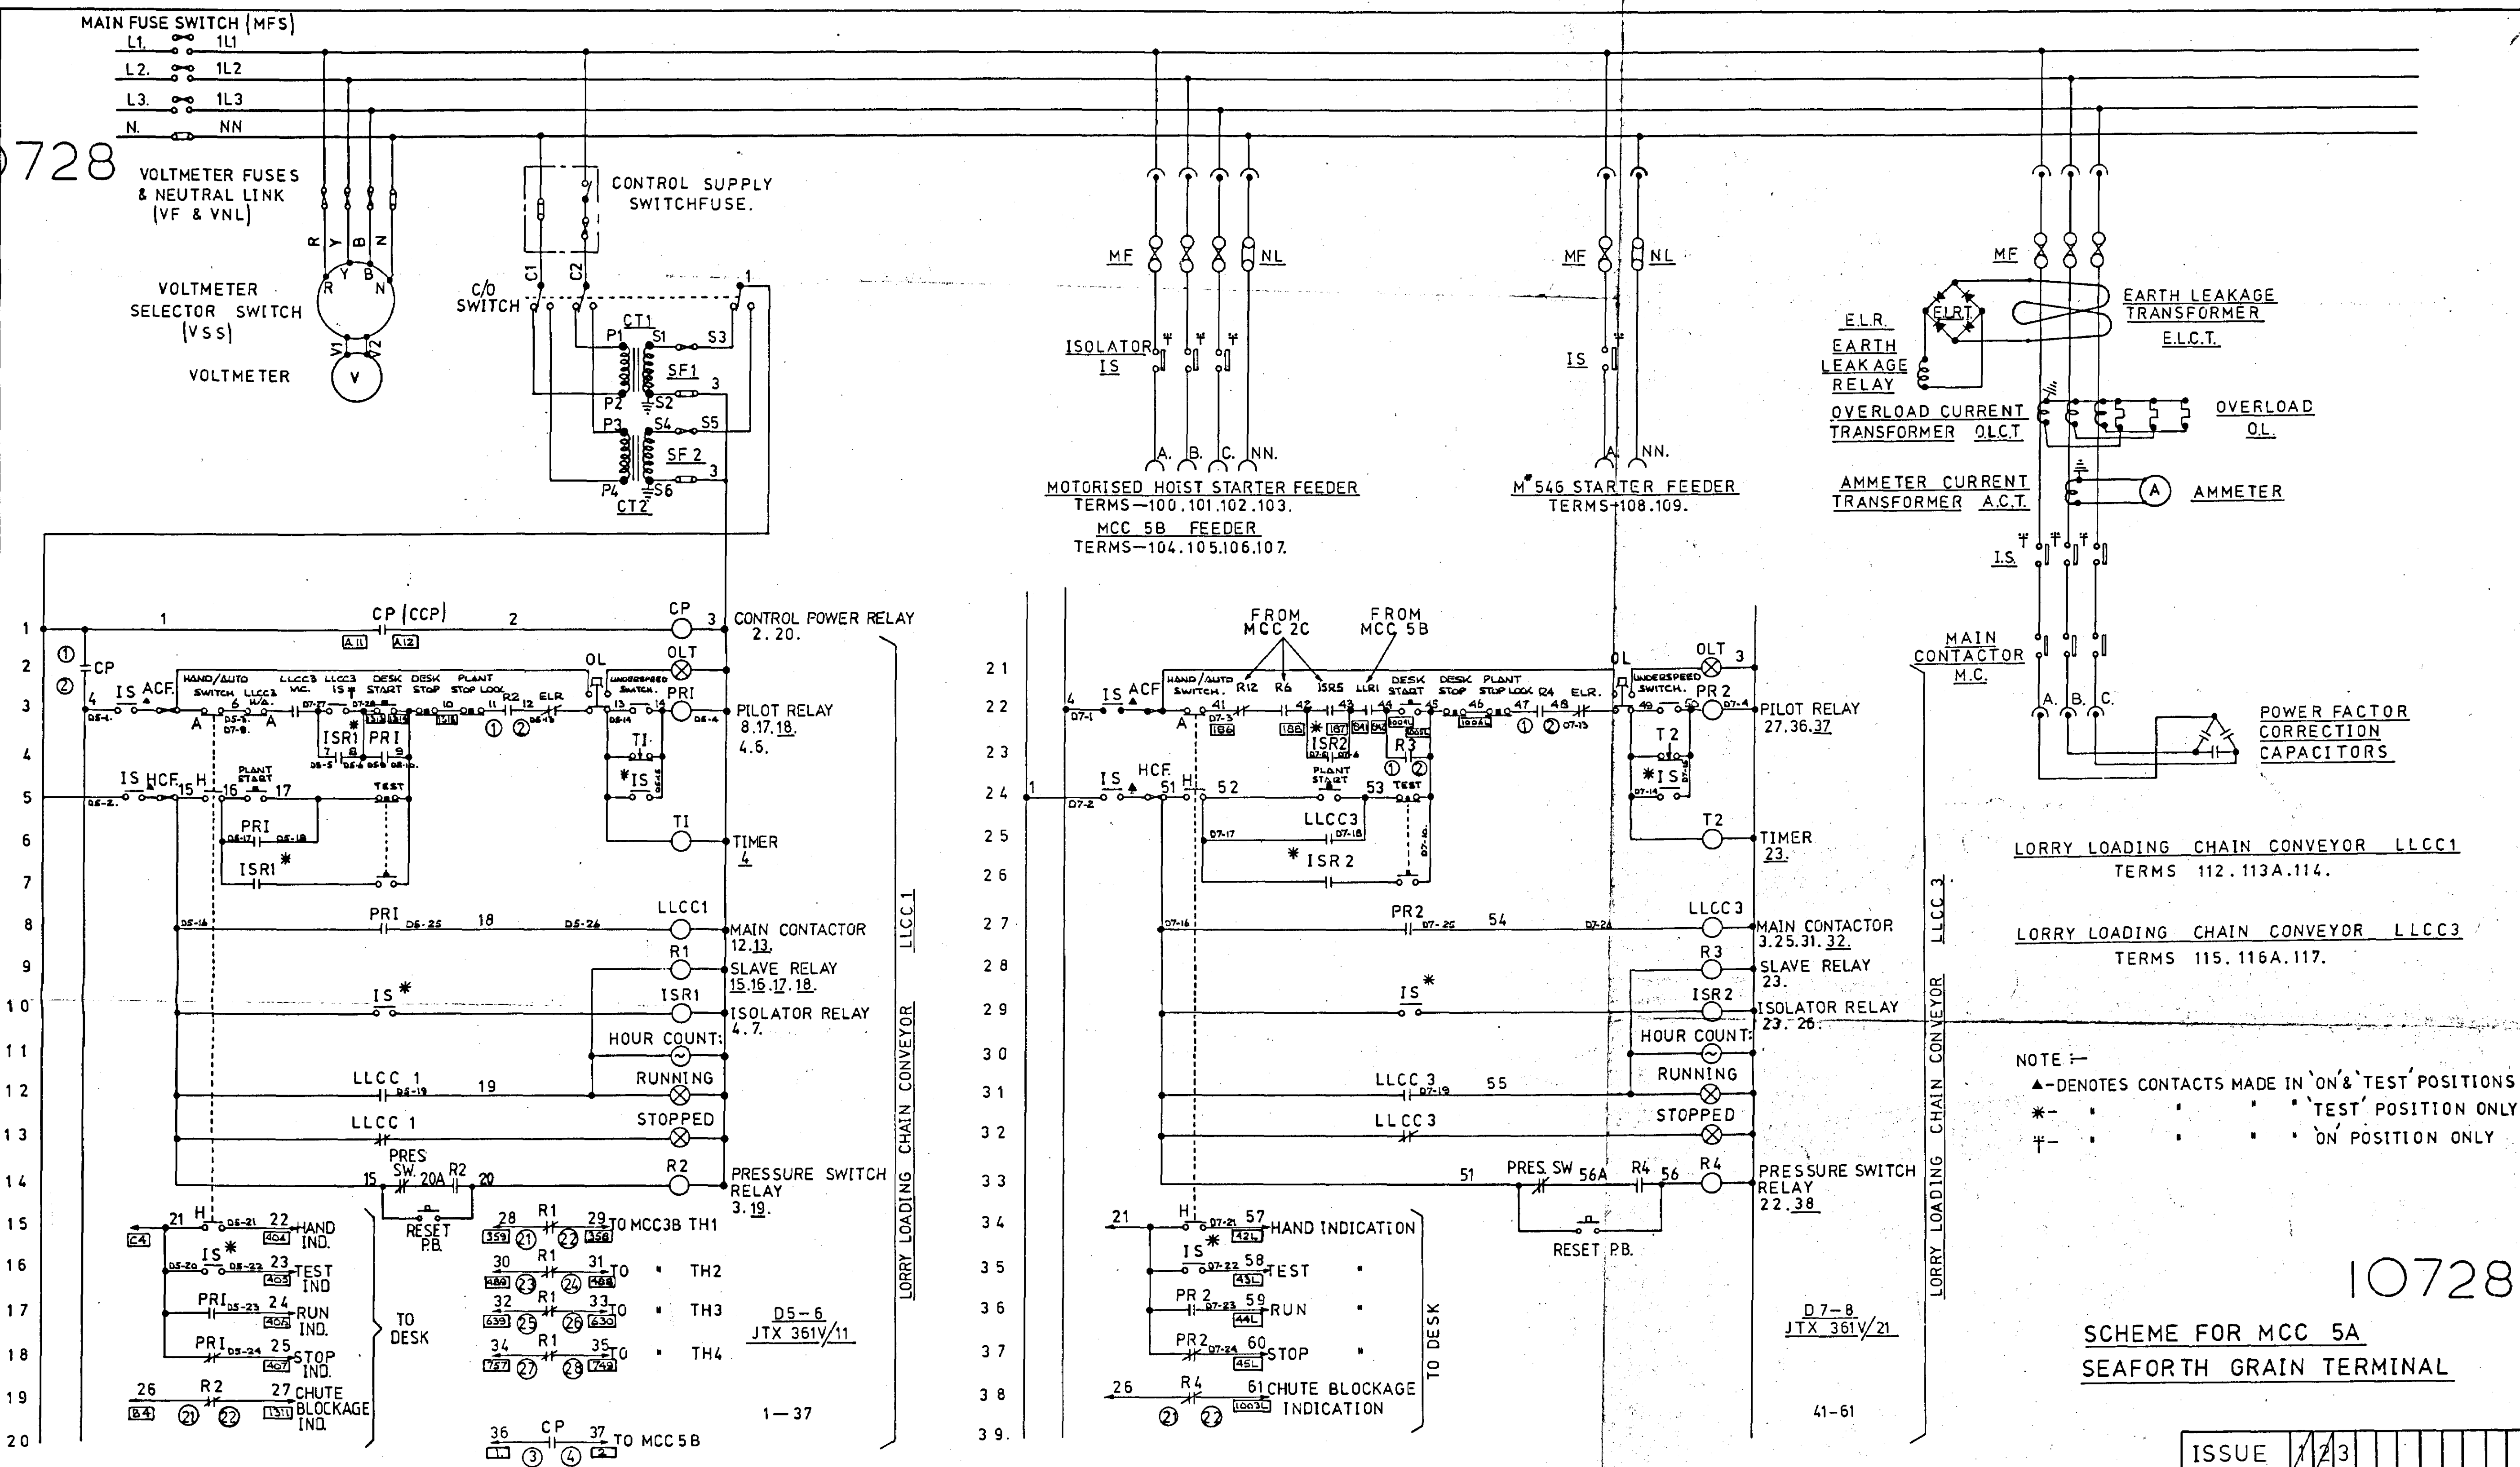

DEWHURST & PARTNER LTD
MELBOURNE WORKS HOUNSLOW

TITLE -
SCHEME FOR MCC 5A - SEAFORTH GRAIN TERMINAL

REVISION 3 Line 14: R2 contact & reset PB added Line 39: R4 contact & reset PB added 14-7-81 R.H.M.	REVISION 2 R1 & R2 WERE ACROSS MAIN CONT. COILS 27-5-71	REVISION 1 LLCC1 SUSTAINING CONTACTS WERE ON M.C. 20-4-71	DRAWN BY DATE 16-3-71 CHECKED BY APPROVED BY DATE	KEY: DIA. N° EXT. DIA. N° RTX 361 AD REL. DIA. N° PANEL LAYOUT. GTX 361 AD
--	---	---	---	---

ISSUE	1	2	3						
CTX 361 AD									
CTX 361 AD									