
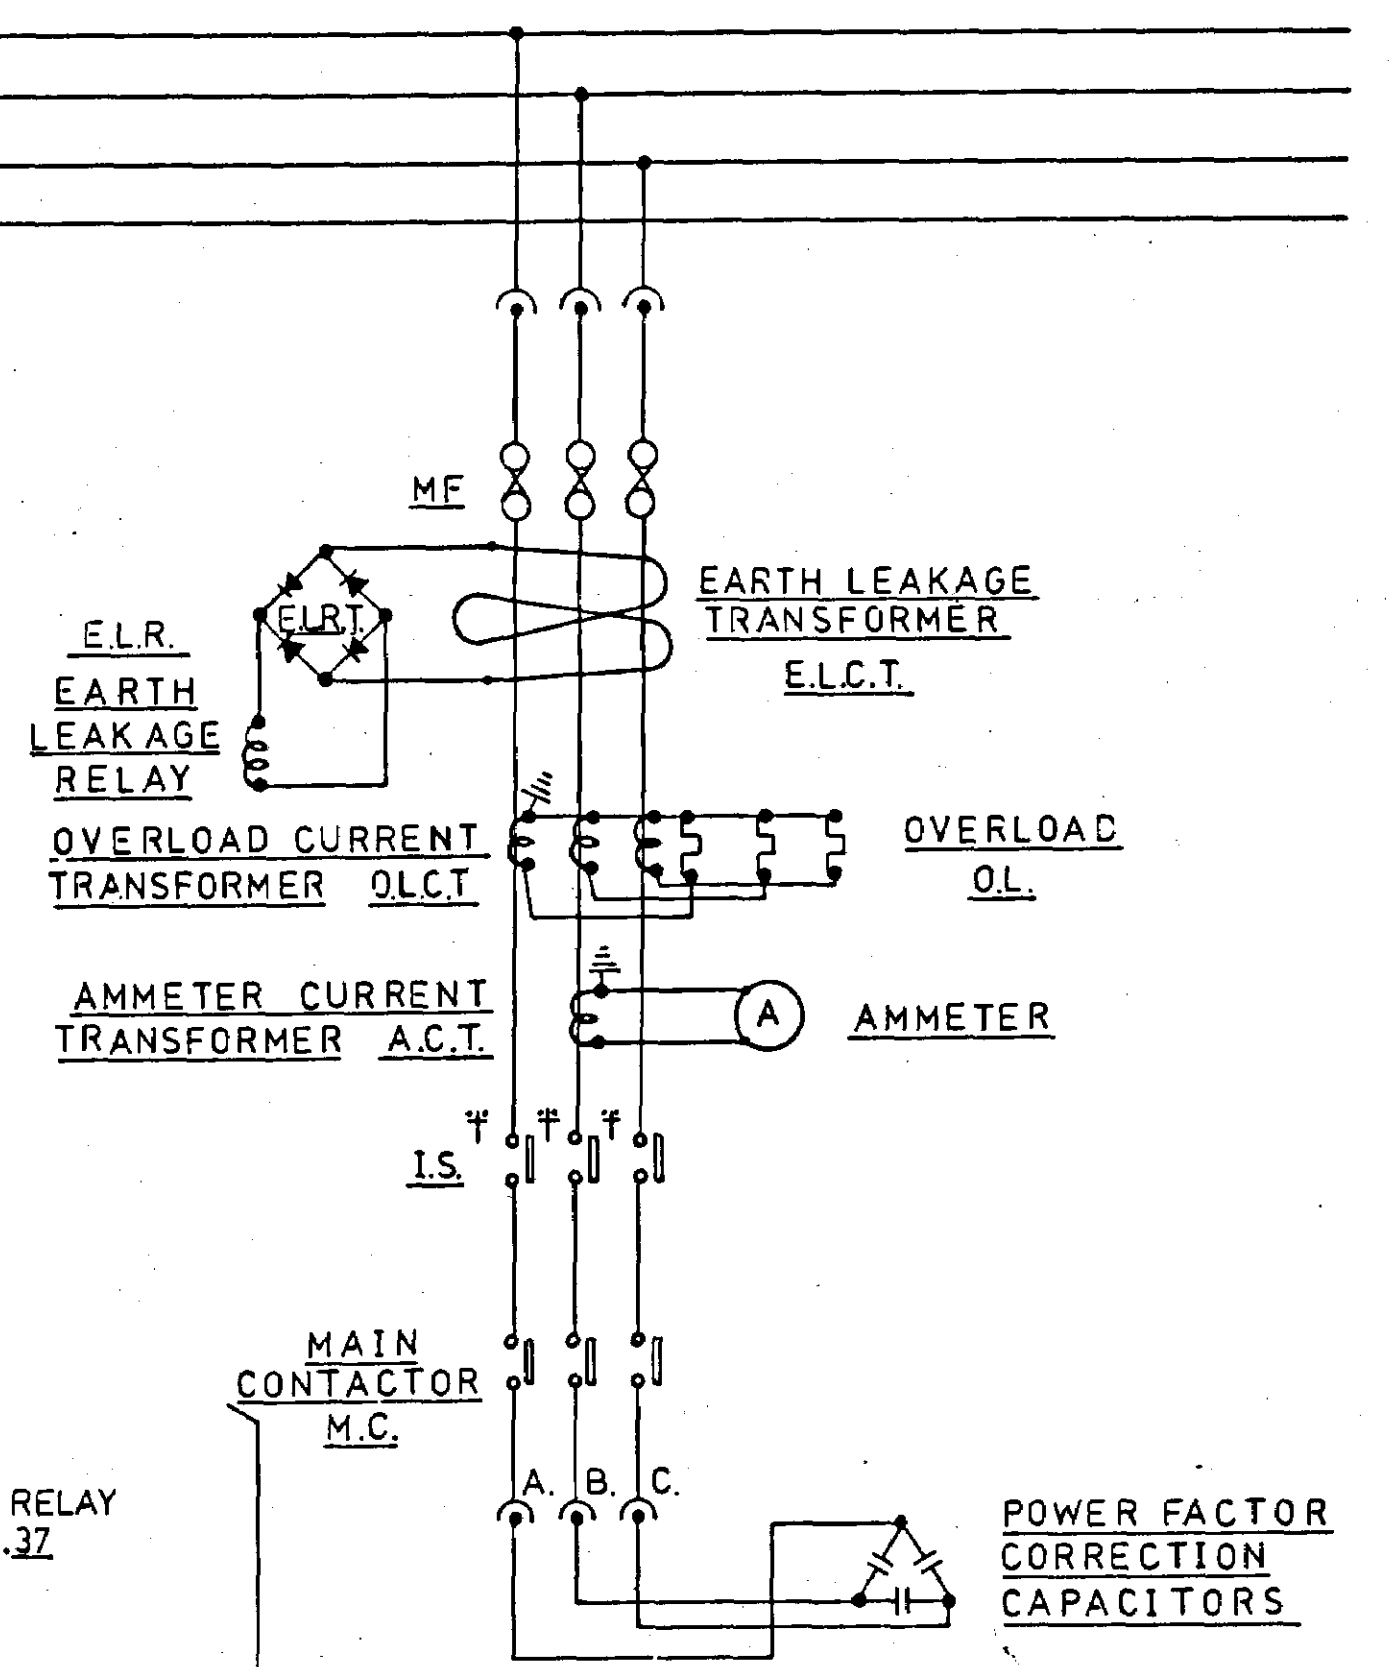
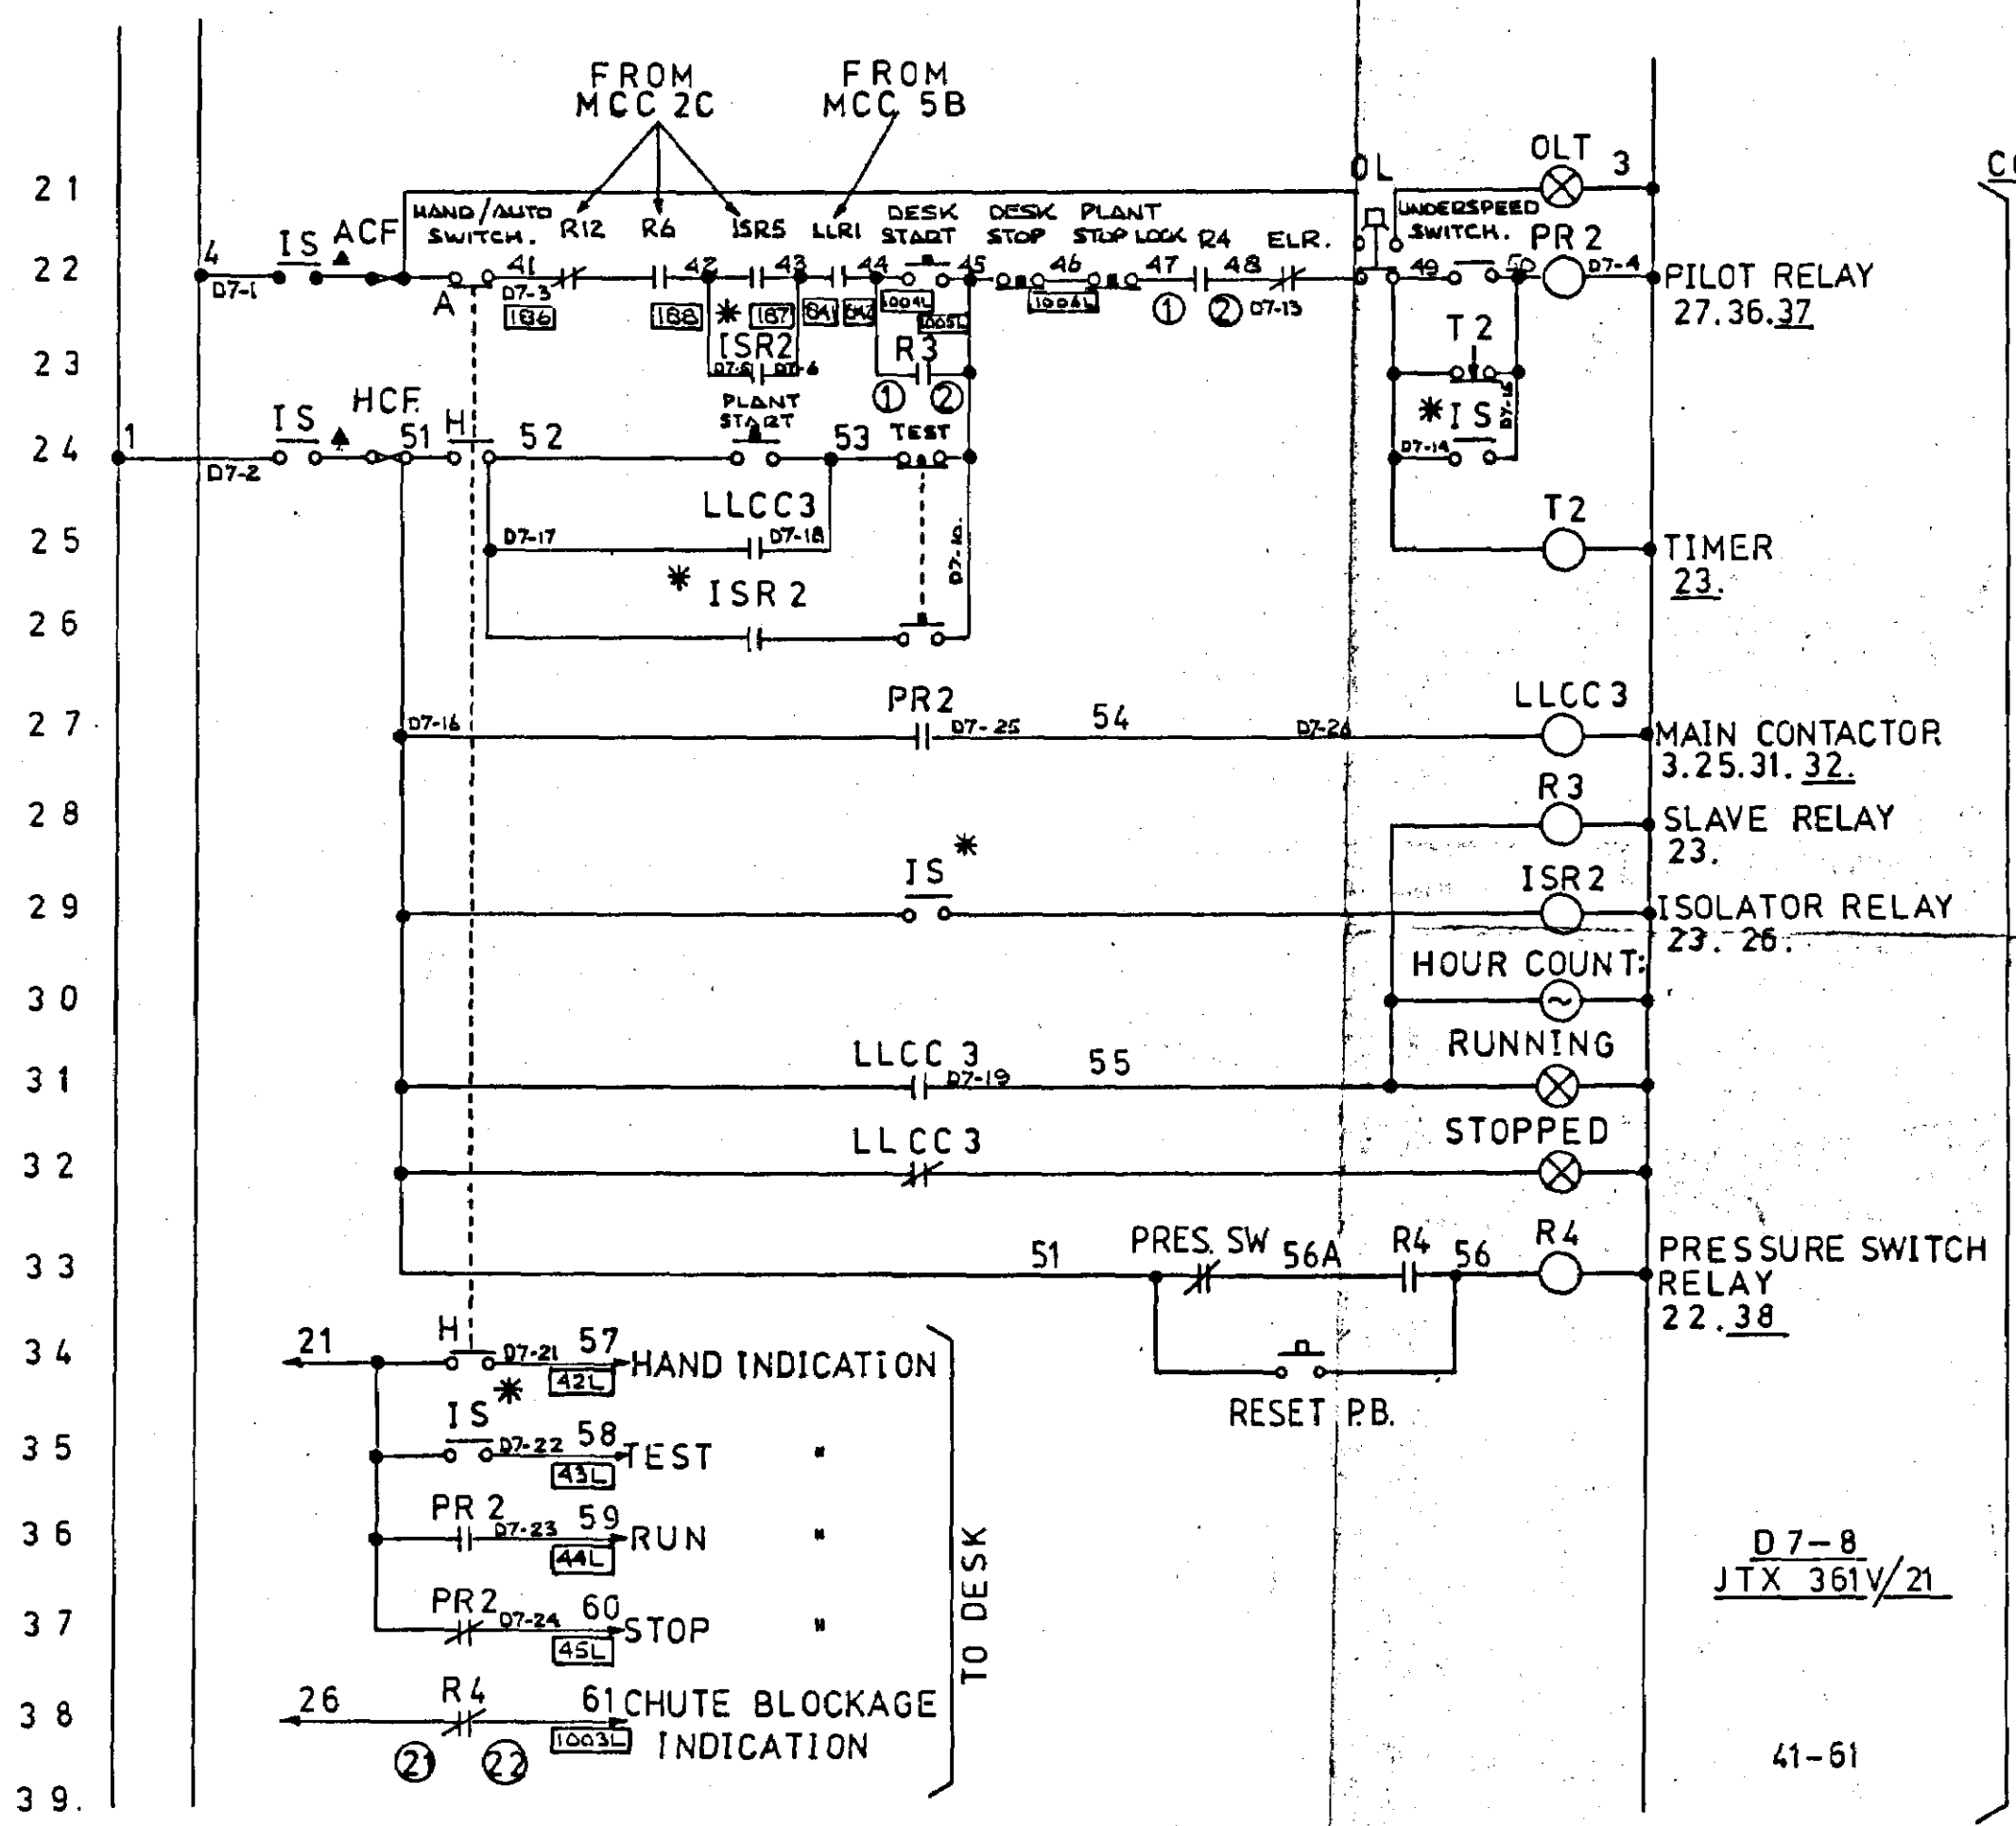
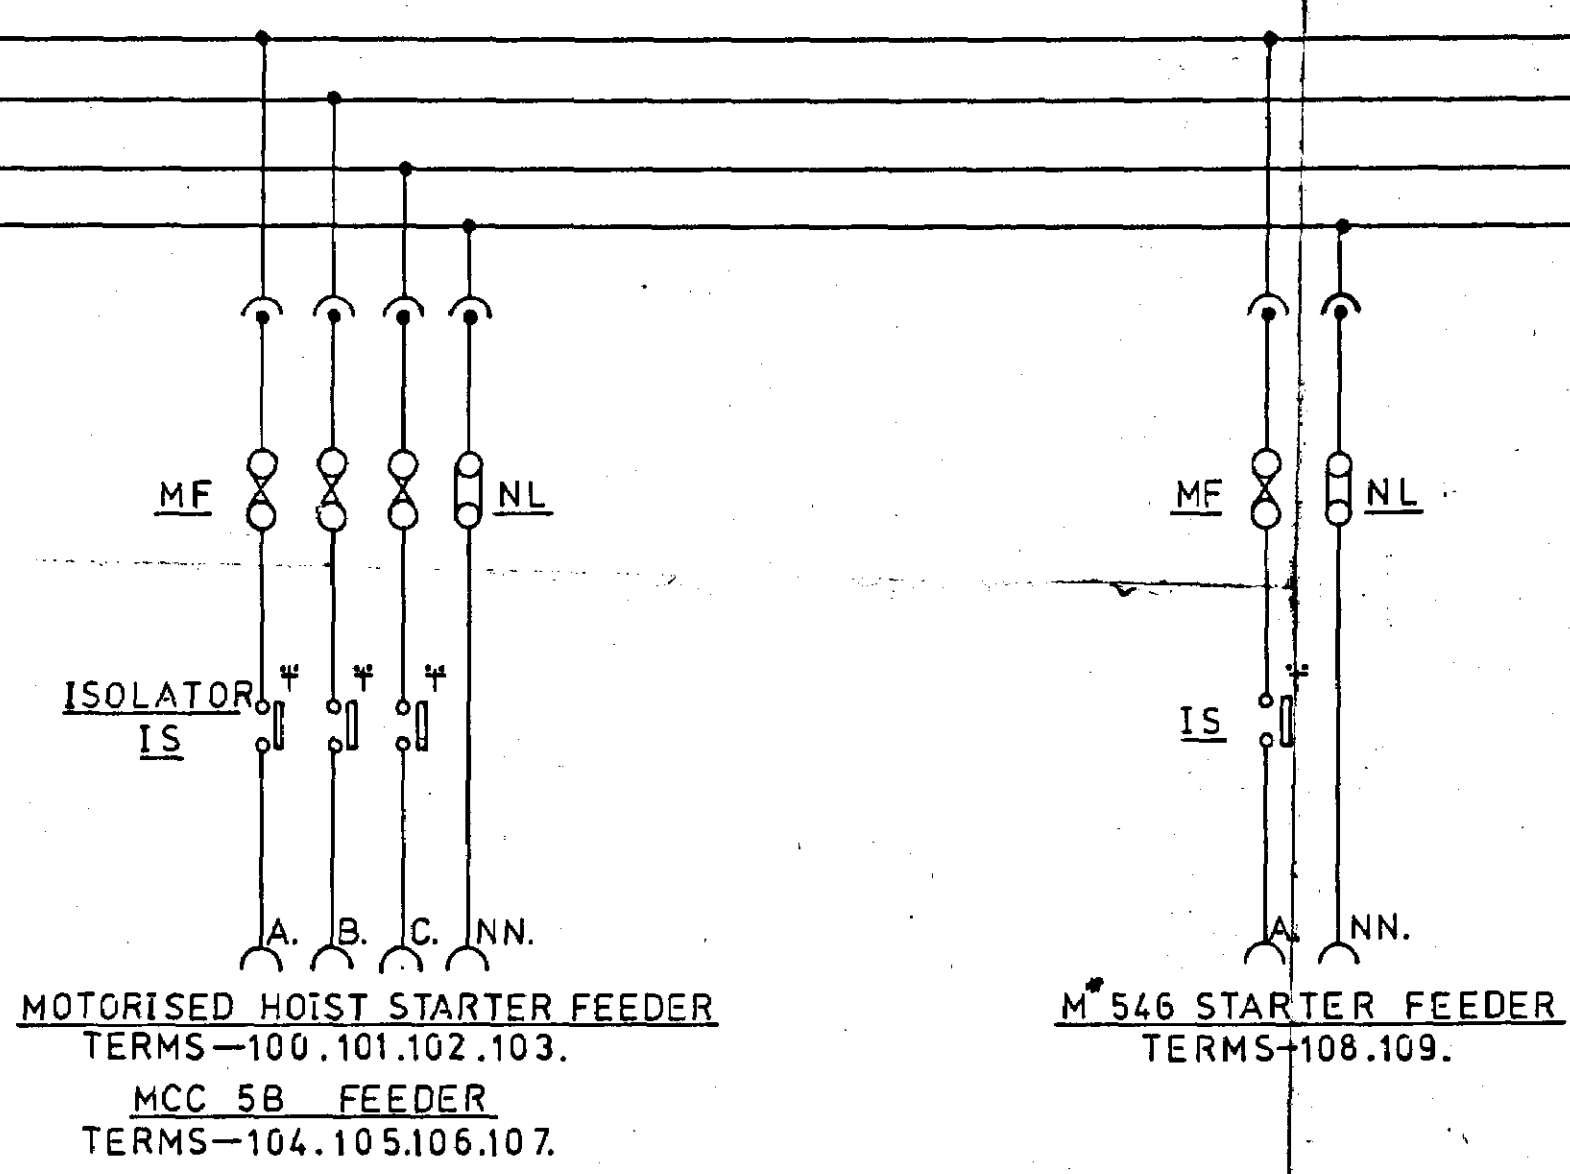
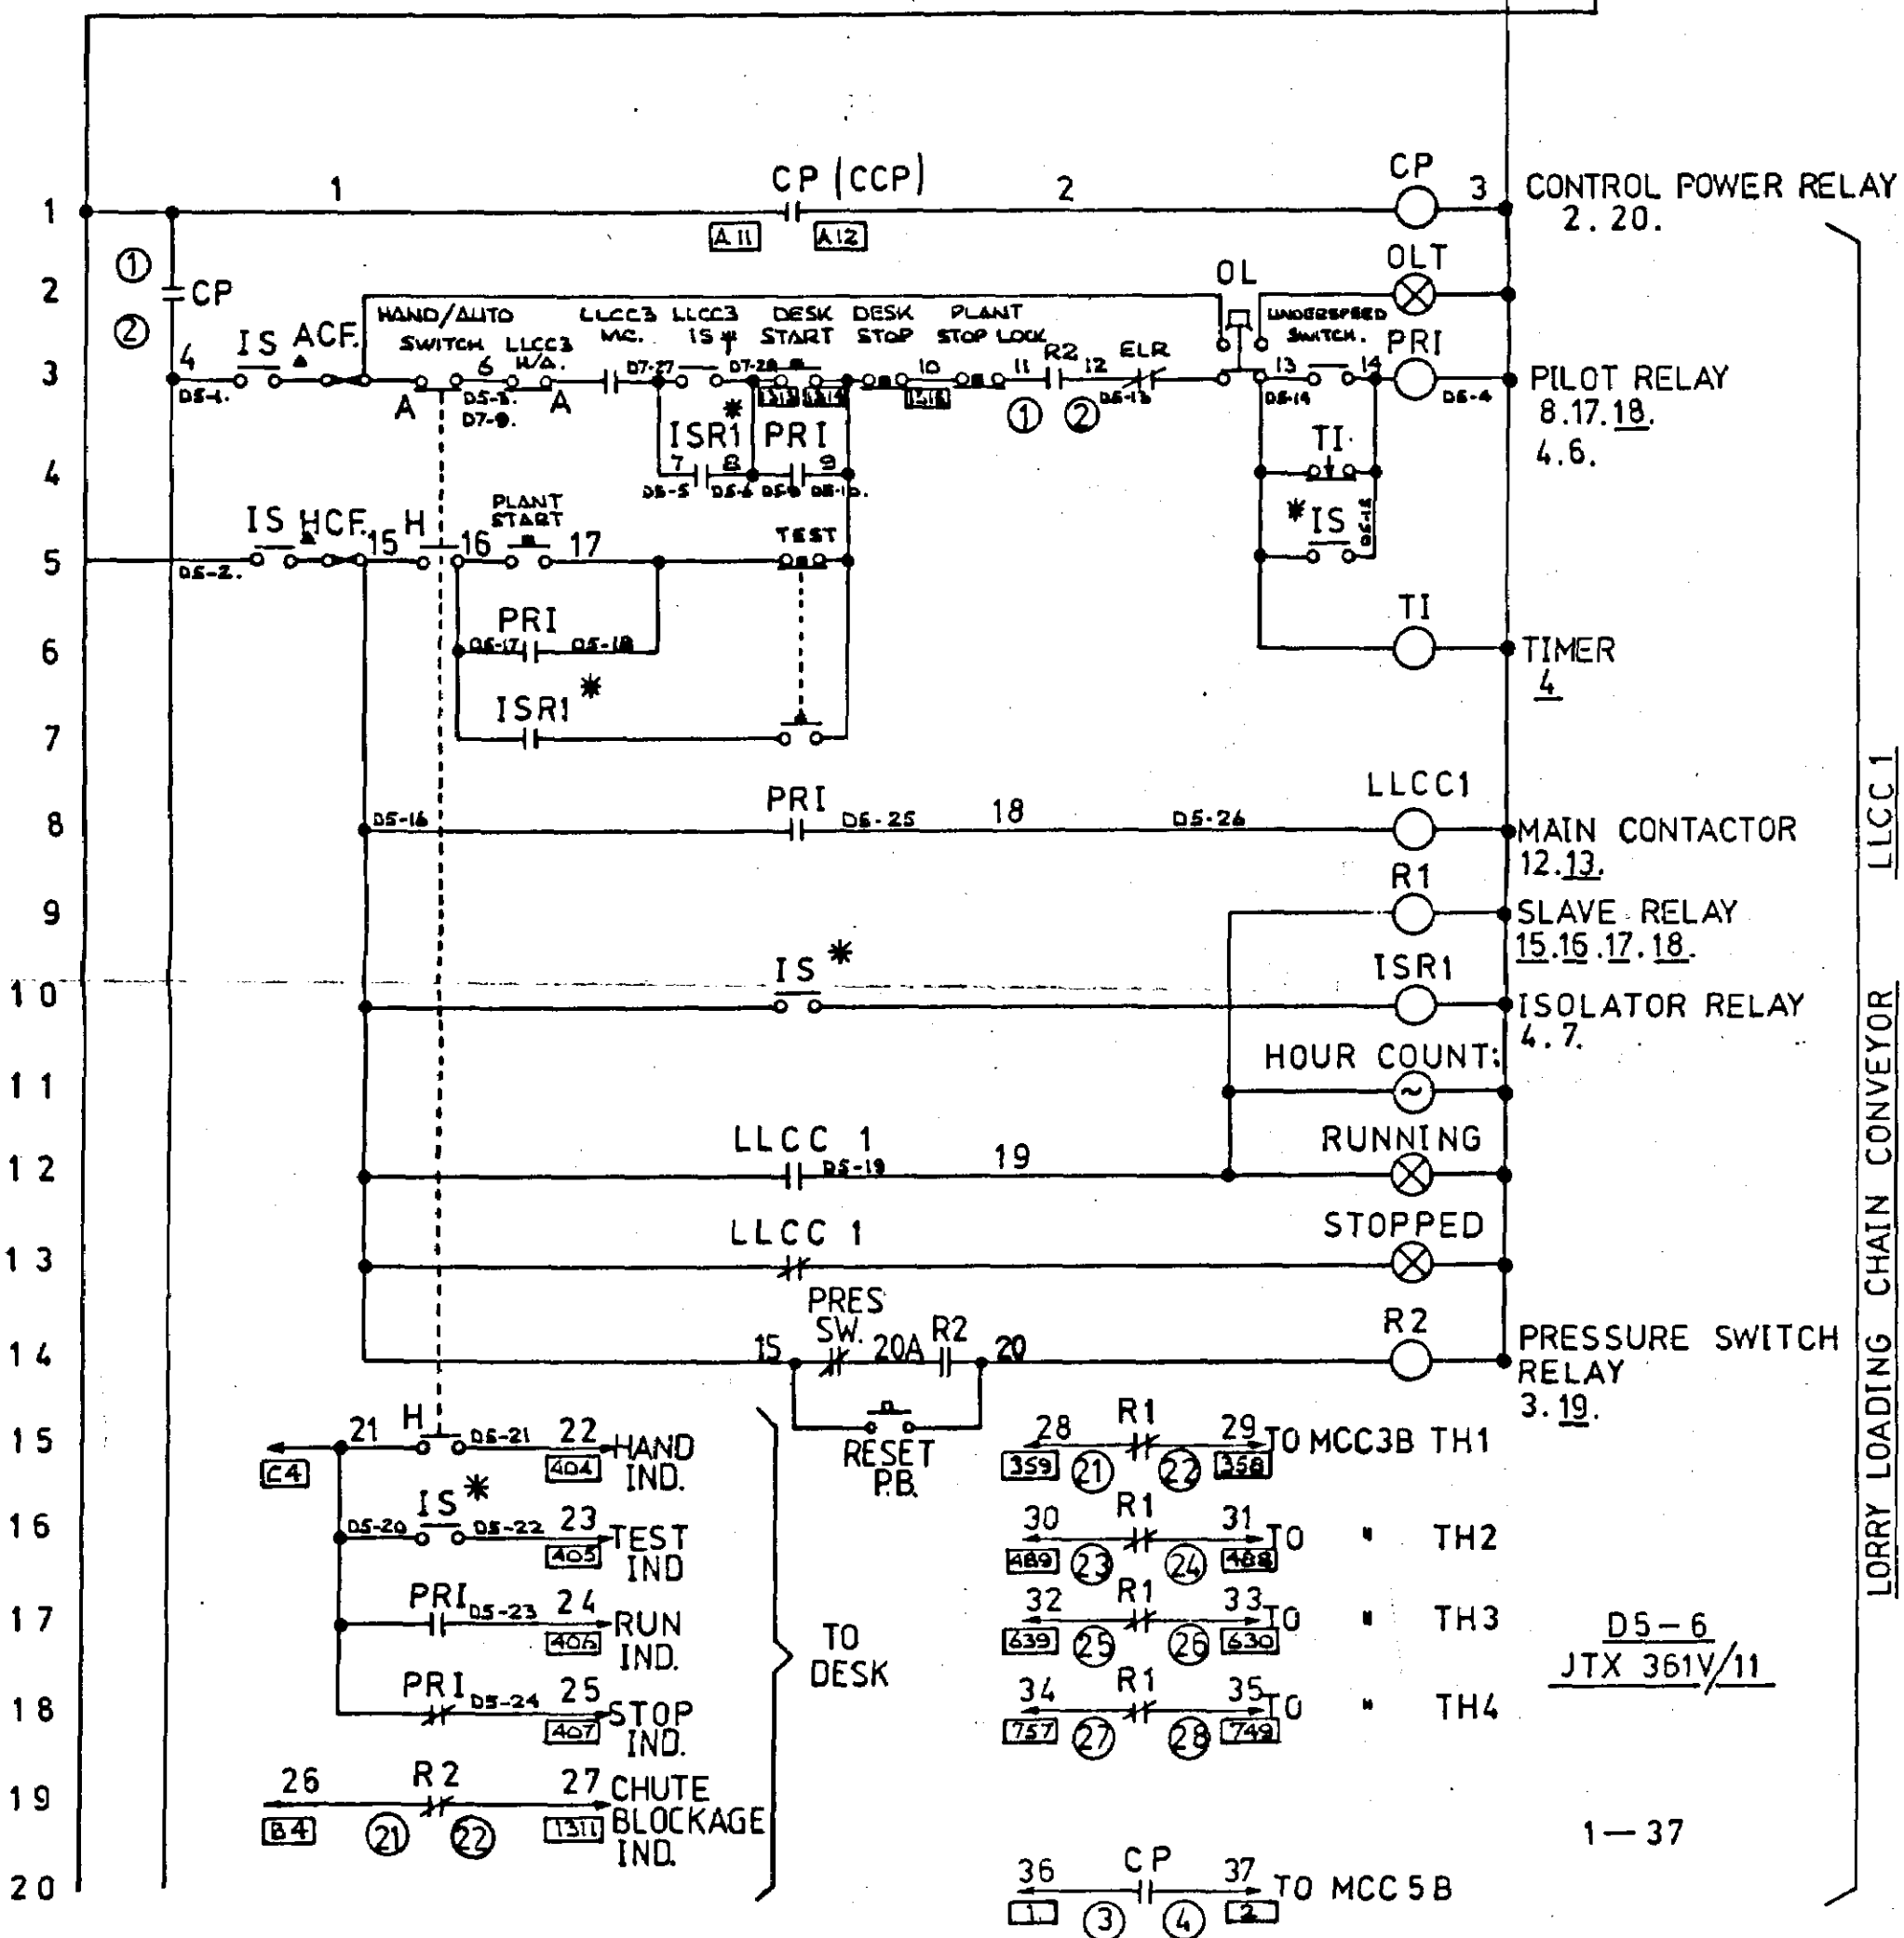


MAIN FUSE SWITCH (MFS)

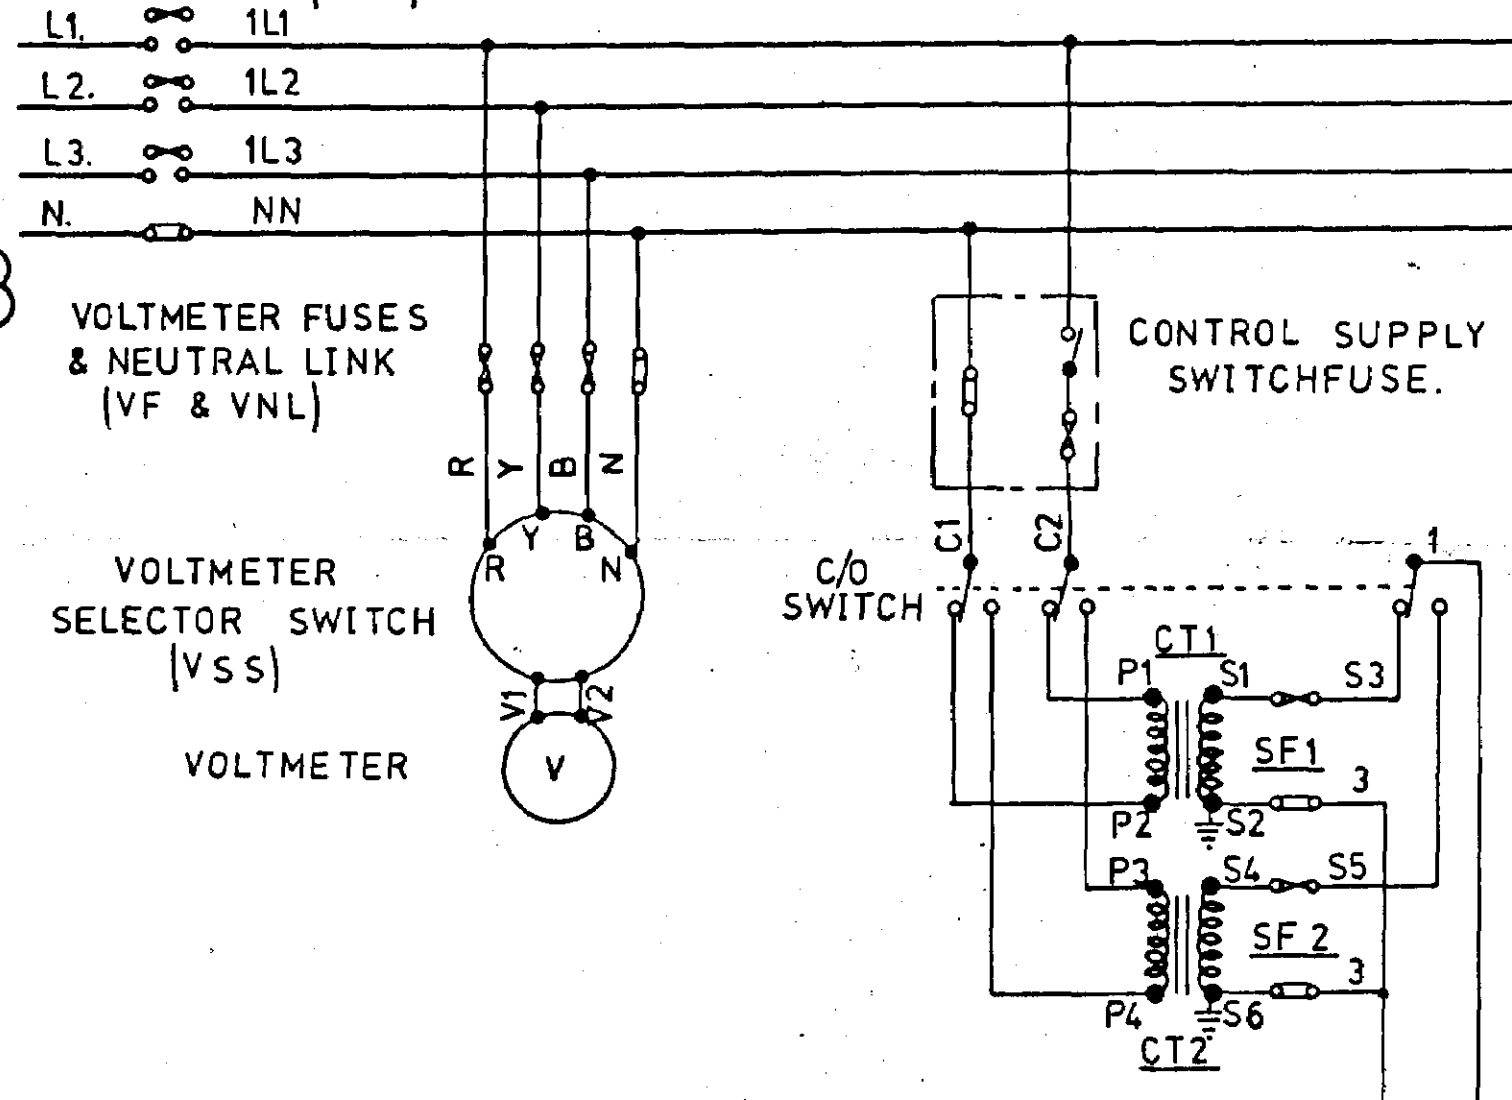

LORRY LOADING CHAIN CONVEYOR LLCC1
TERMS 112.113A.114.

LORRY LOADING CHAIN CONVEYOR LLCC3
TERMS 115.116A.117.

NOTE :-

▲-DENOTES CONTACTS MADE IN 'ON' & 'TEST' POSITIONS

*- " " " " 'TEST' POSITION ONLY

†- " " " " 'ON' POSITION ONLY

SCHEME FOR MCC 5A
SEAFORTH GRAIN TERMINAL

ISSUE	1	2	3																
CTX 361 AD																			
CTX 361 AD																			

DEWHURST & PARTNER LTD
MELBOURNE WORKS HOUNSLOW

TITLE—
SCHEME FOR MCC 5A - SEAFORTH GRAIN TERMINAL

REVISION 3 Line 14: R2 contact & reset PB added Line 33: R4 contact & reset PB added 16-7-81 R.M.N.	REVISION 2 R1 & R2 WERE ACROSS MAIN CONT: COILS 27-5-71	REVISION 1 LLCC1. SUSTAINING CONTACTS WERE ON MC. 20-4-71
--	---	---

DRAWN BY	KEY.DIA.N°
DATE 16-3-71	EXT.DIA.N° RTX 361 AD
CHECKED BY	REL.DIA.N°
APPROVED BY	PANEL LAYOUT. GTX 361AD
DATE	