


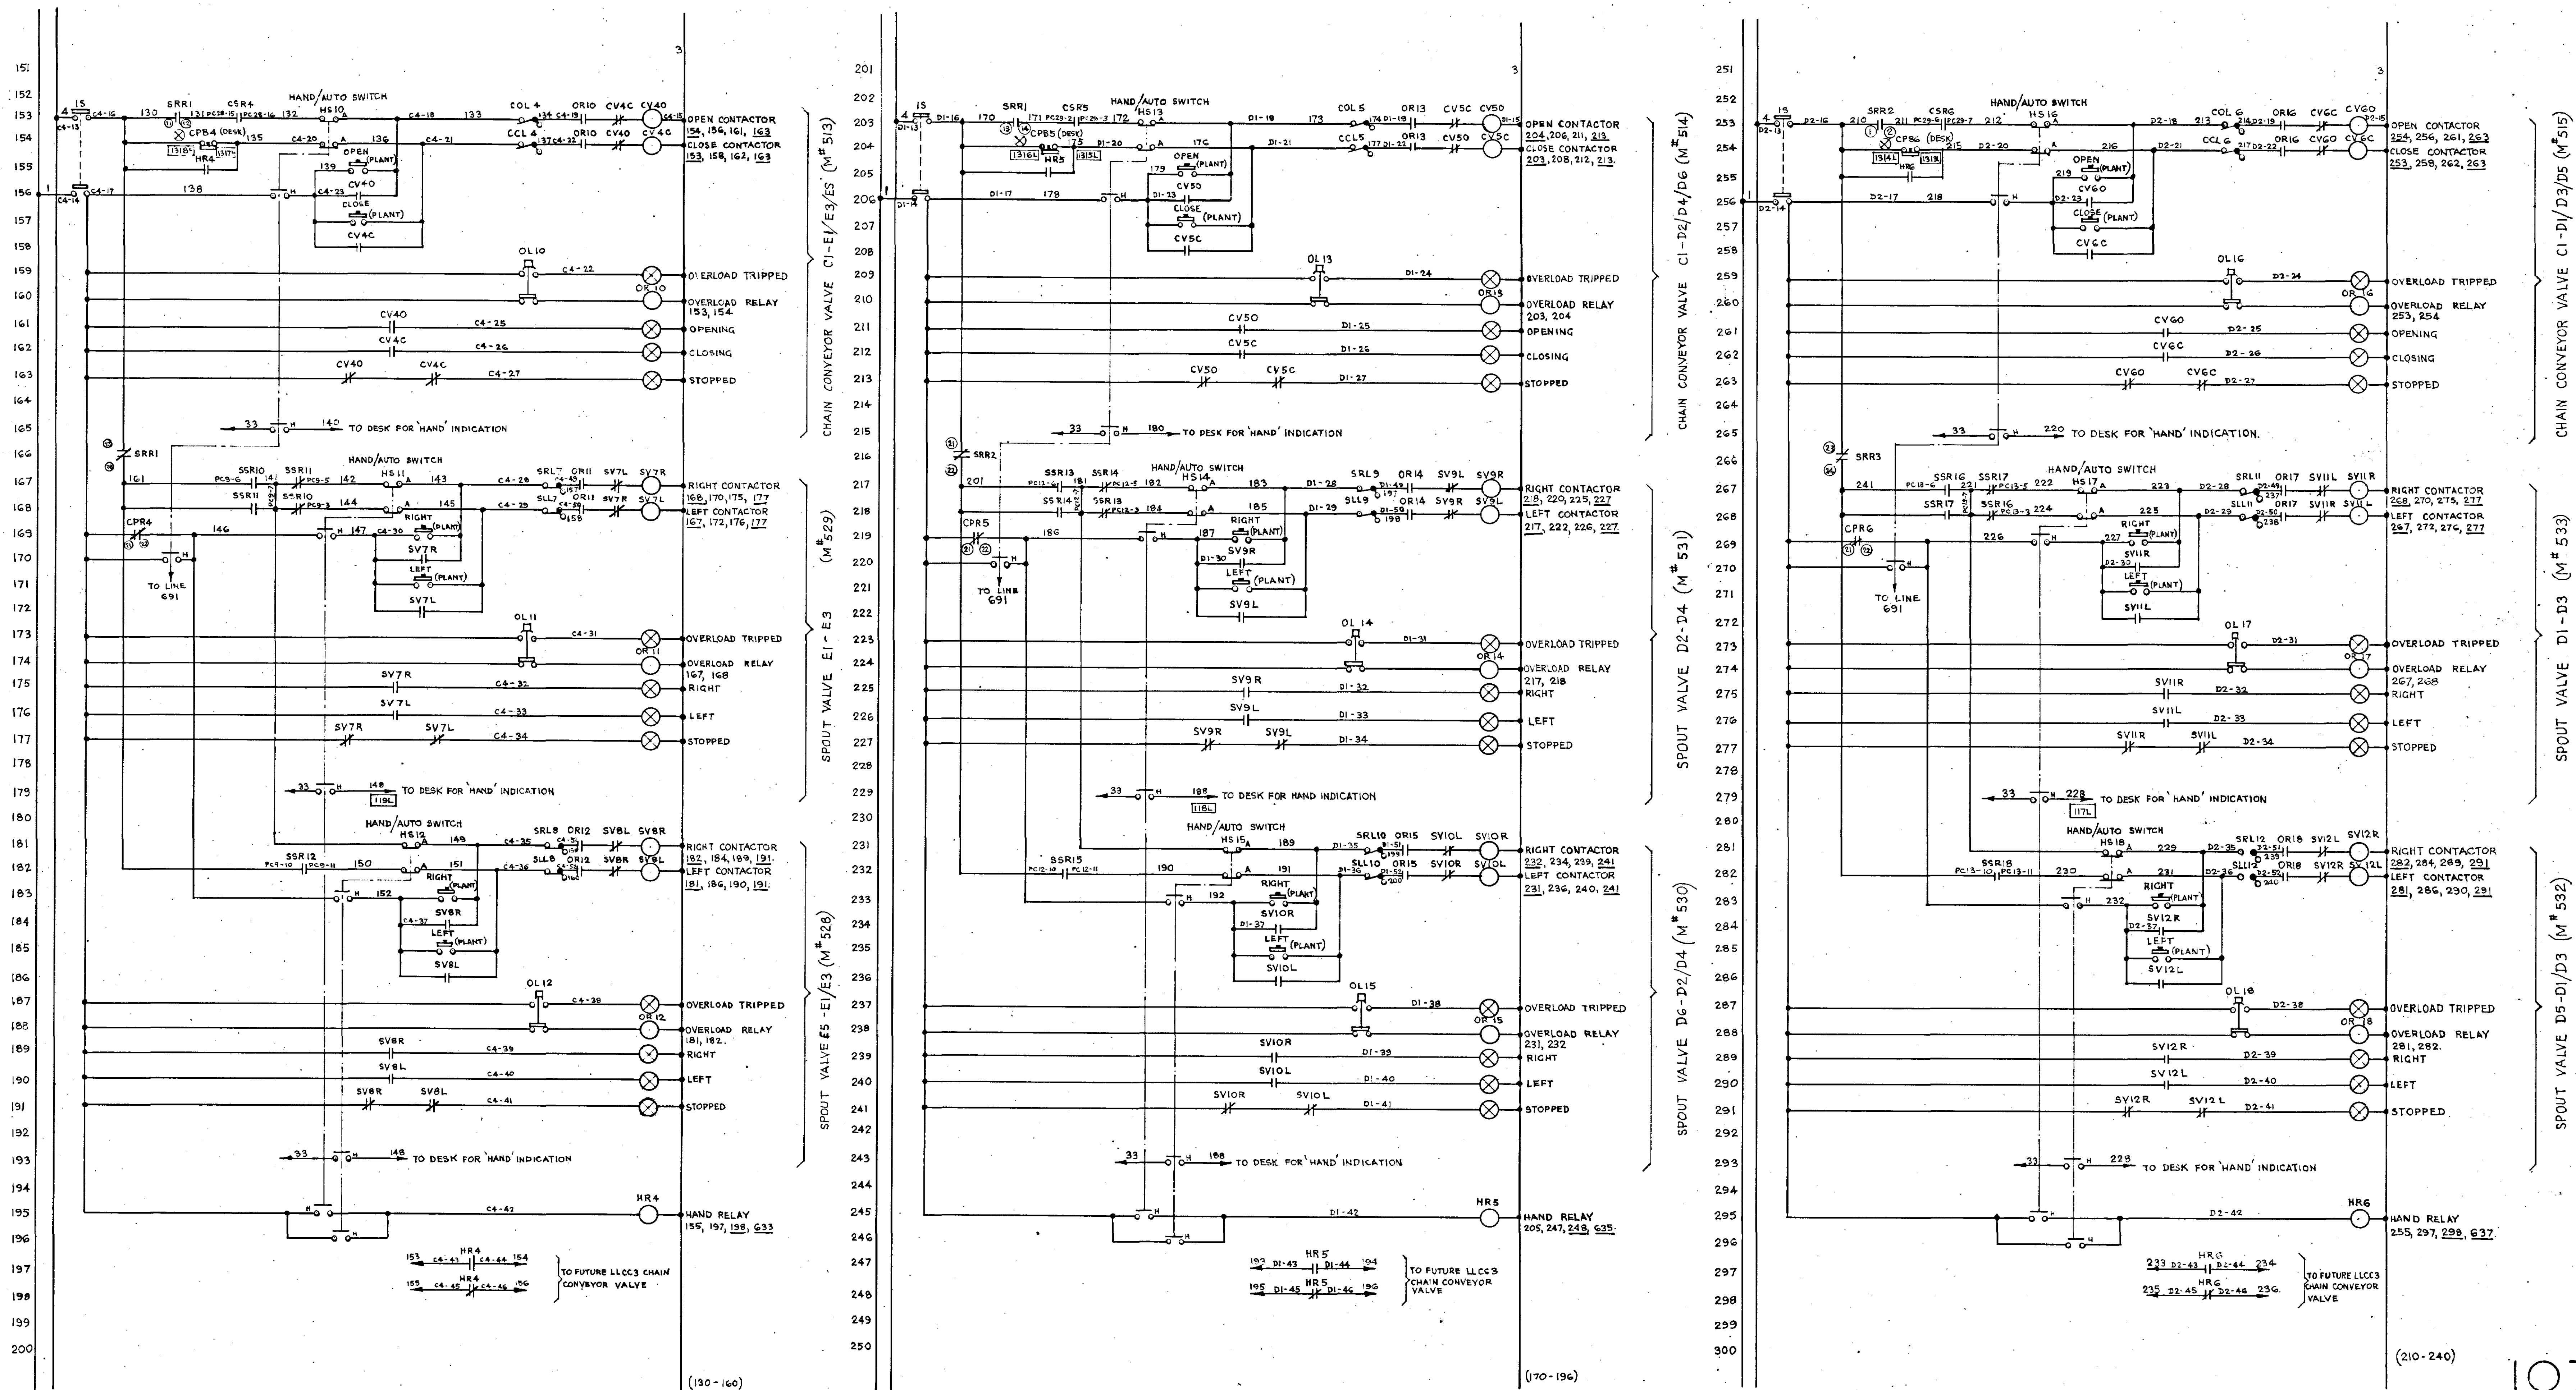

SCHEME FOR MCC5B - SEAFORTH GRAIN TERMINAL

THE DESIGN AND MANUFACTURING
 INFORMATION CONTAINED IN
 THIS DRAWING IS THE EXCLUSIVE
 RIGHT OF DEWHURST & PARTNER
 LTD. AND MUST NOT BE COPIED
 OR USED FOR MANUFACTURING
 PURPOSES.

DTX 361 AC/2

DTX 361 AC/2

DEWHURST & PARTNER LTD.
 MELBOURNE WORKS HOUNSLOW

TITLE
 SCHEME FOR MCC5B - SEAFORTH GRAIN TERMINAL

REVISION: 5
 DESK REVERSED
 ORIGIN: ICD
 11/7/72 SCD J.S.

REVISION: 4
 DESK TERMINALS
 ADDED
 ORIGIN: I.C.D
 1/2/72 SCD J.S.

REVISION: 3
 N/C'S ADDED ON
 SRR1 & SRR2.
 ORIGIN: EISP
 2/6/71 SCD J.T.

REVISION: 2
 SPOUT VALVE
 DESIGNATIONS
 INTERCHANGED
 NOTES ADDED
 ORIGIN: EISP
 3/5/71 SCD B.L.

REVISION: 1
 SRR1-12 & SRR1-12
 ADDED
 ORIGIN: EISP
 26/3/71 SCD J.T.

DRAWN BY B.J.C.
 DATE 2-3-71
 CHECKED BY
 APPROVED BY
 DATE

KEY DIAG No
 EXT DIAG No STX 361 AC
 REL DIAG No
 PANEL LAYOUT No HTX 361 AC