


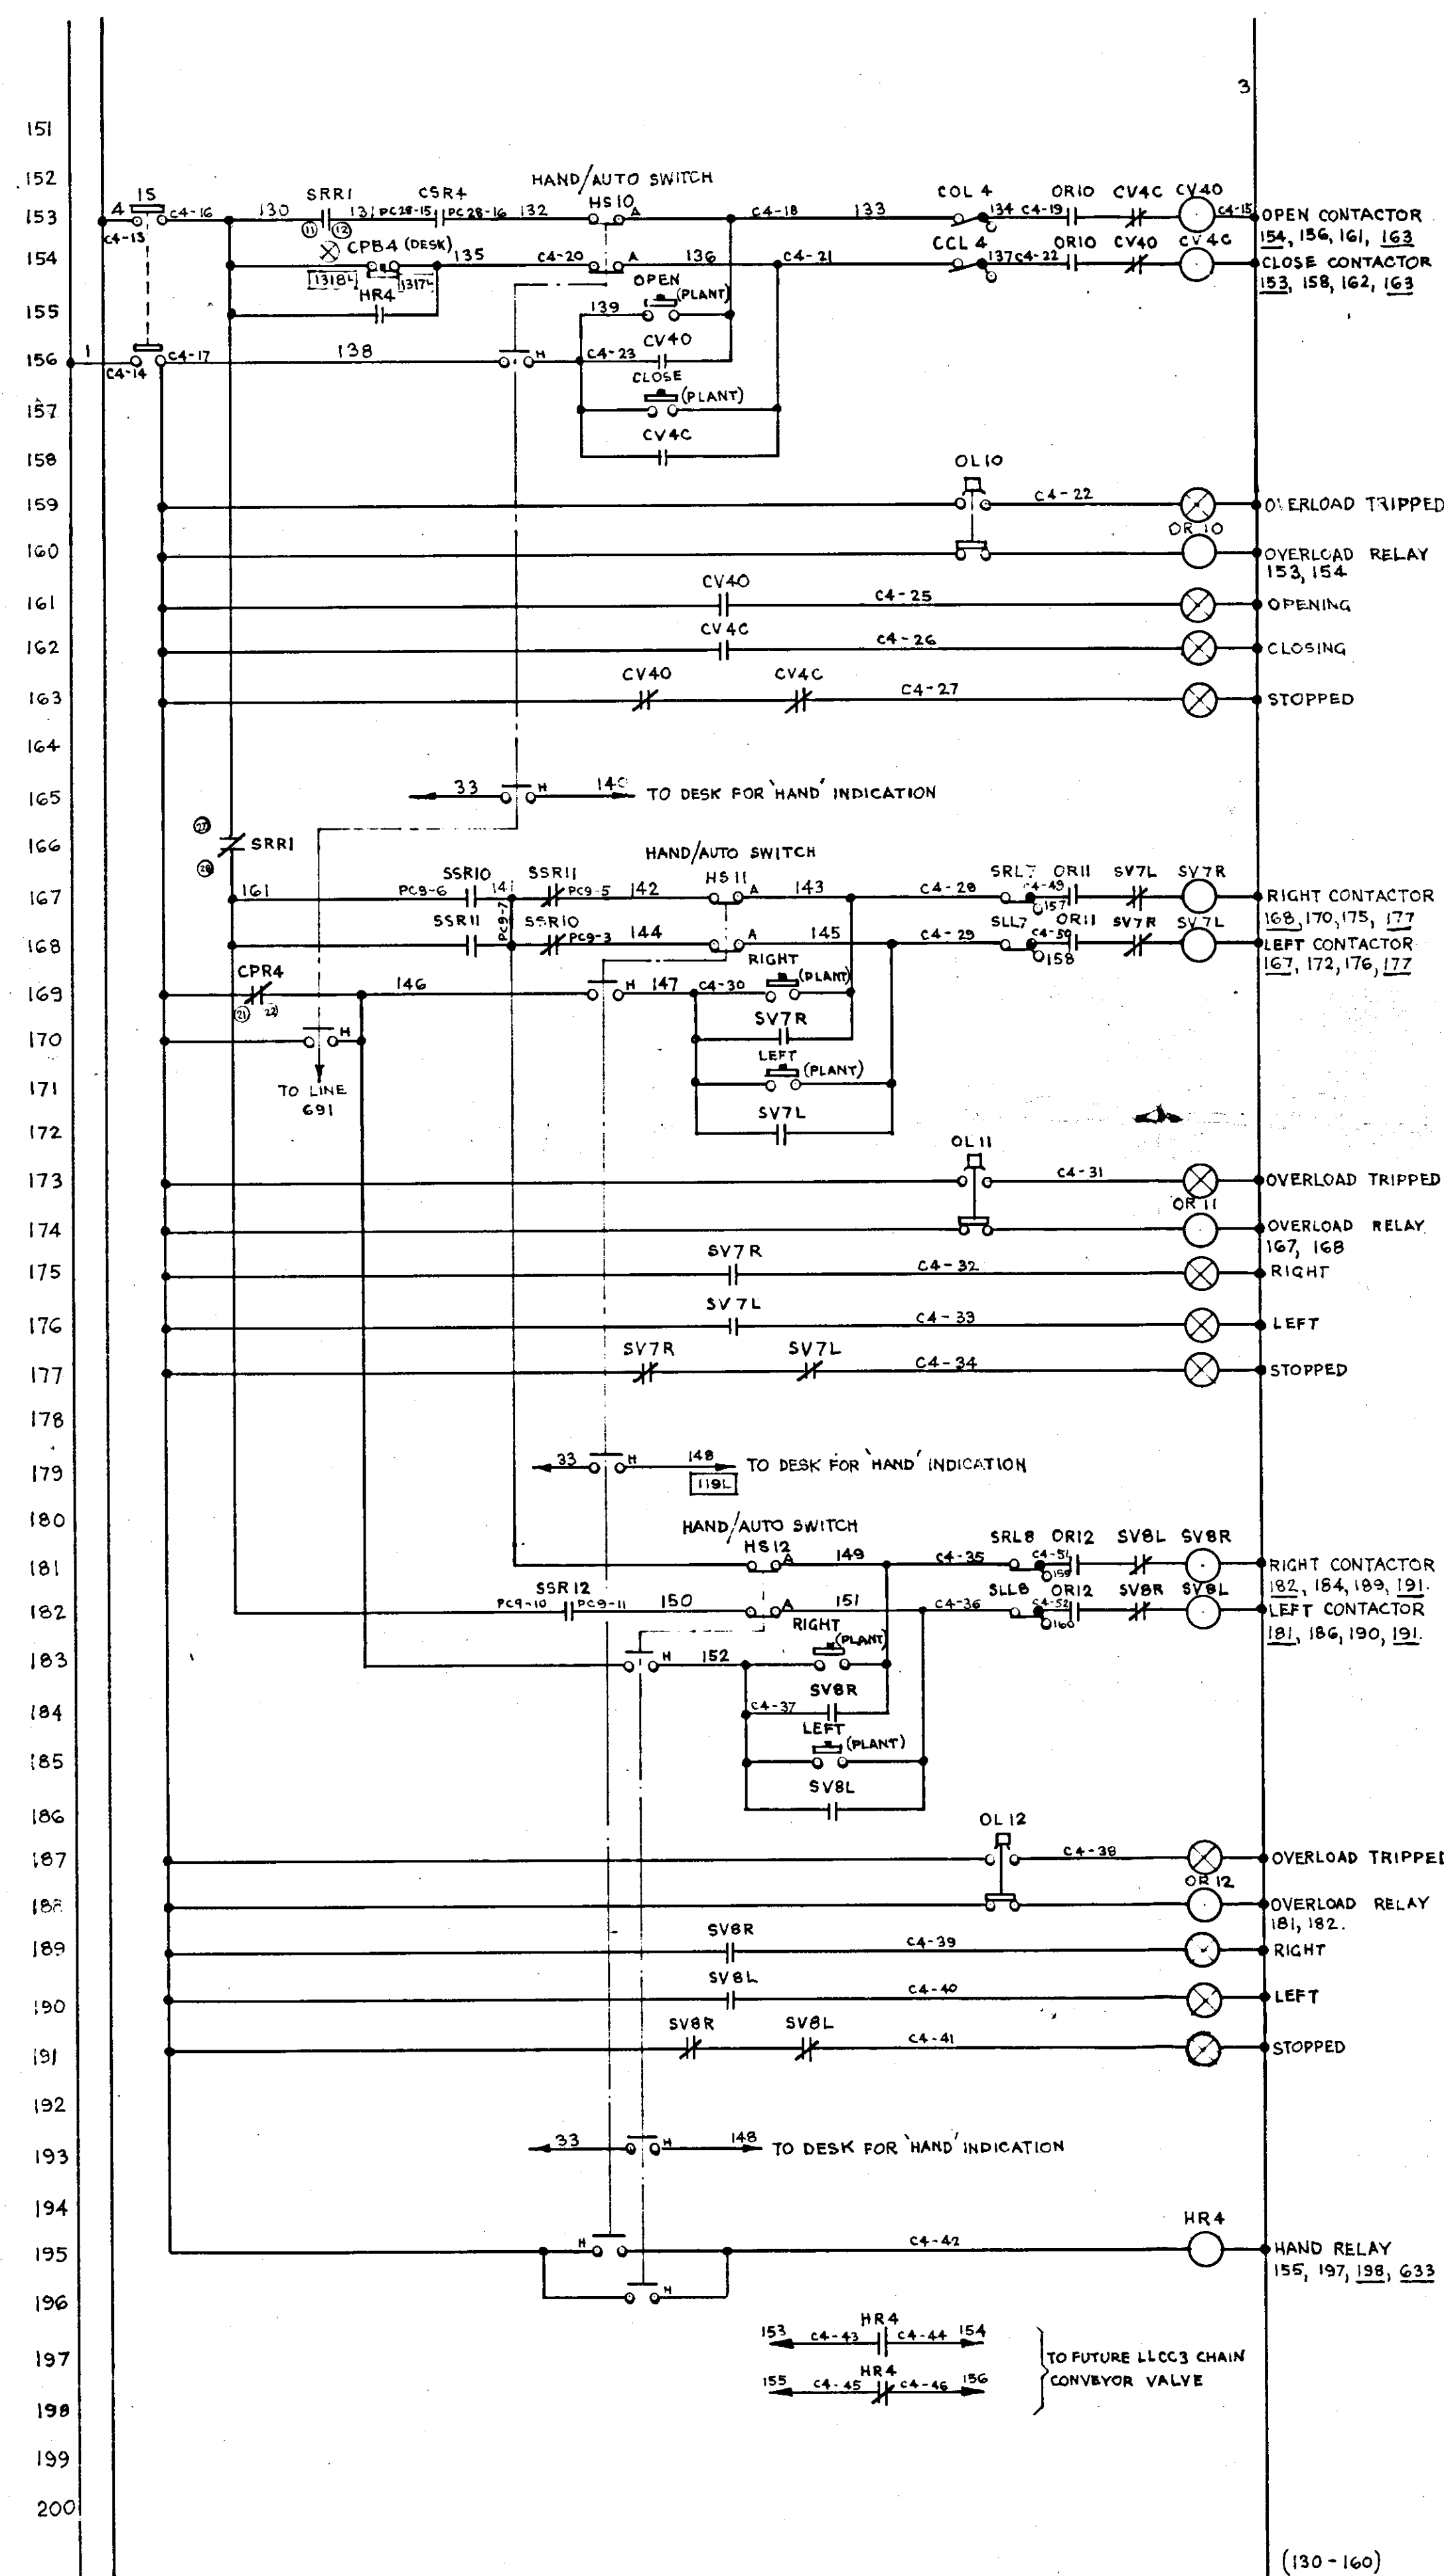

NOTES:-


⊙ STAYPUT TYPE PUSHBUTTON WITH
MUTUAL INTERLOCKING & BLOCKING.

IF RIGHT CONTACTOR IS ENERGISED
THIS INDICATES PLATE VALVE CLOSED
ON RIGHT SIDE, THUS GRAIN WILL
FLOW TO THE LEFT.


DEWHURST & PARTNER LTD.

MELBOURNE WORKS HOUNSLOW

TITLE	SCHEME FOR MCC5B - SEAFORTH GRAIN TERMINAL
-------	--

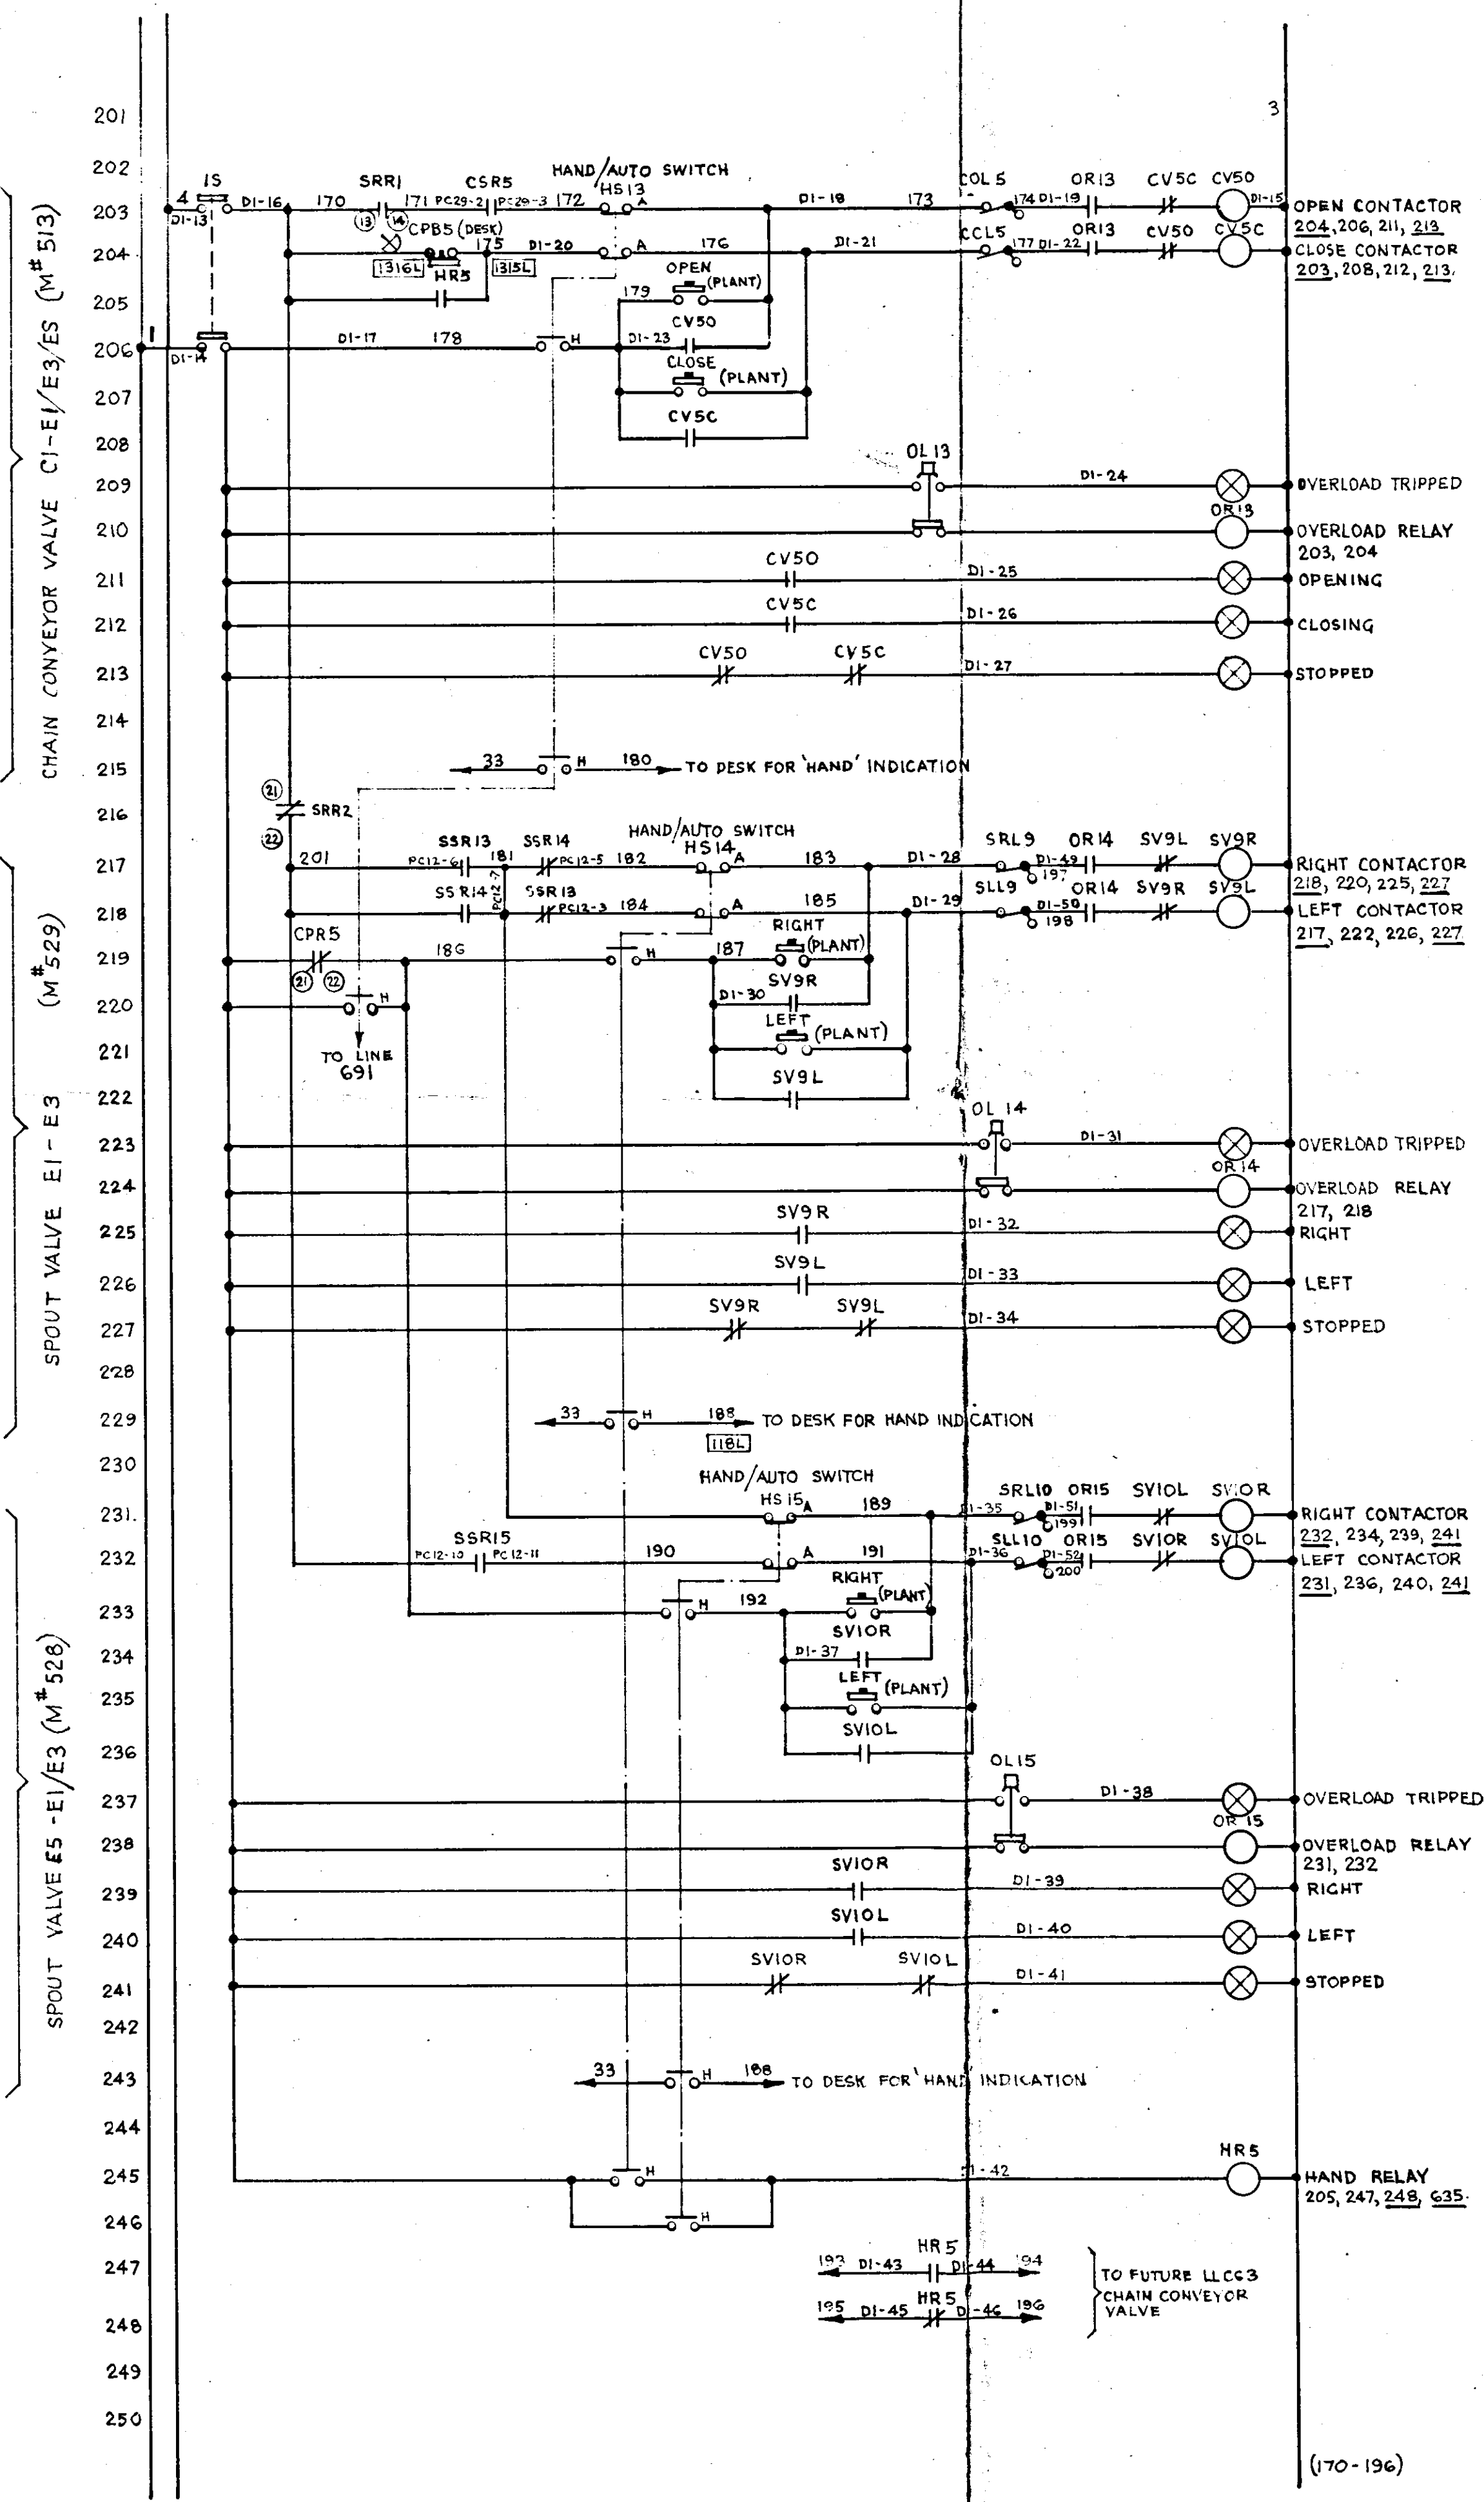

(170-196)

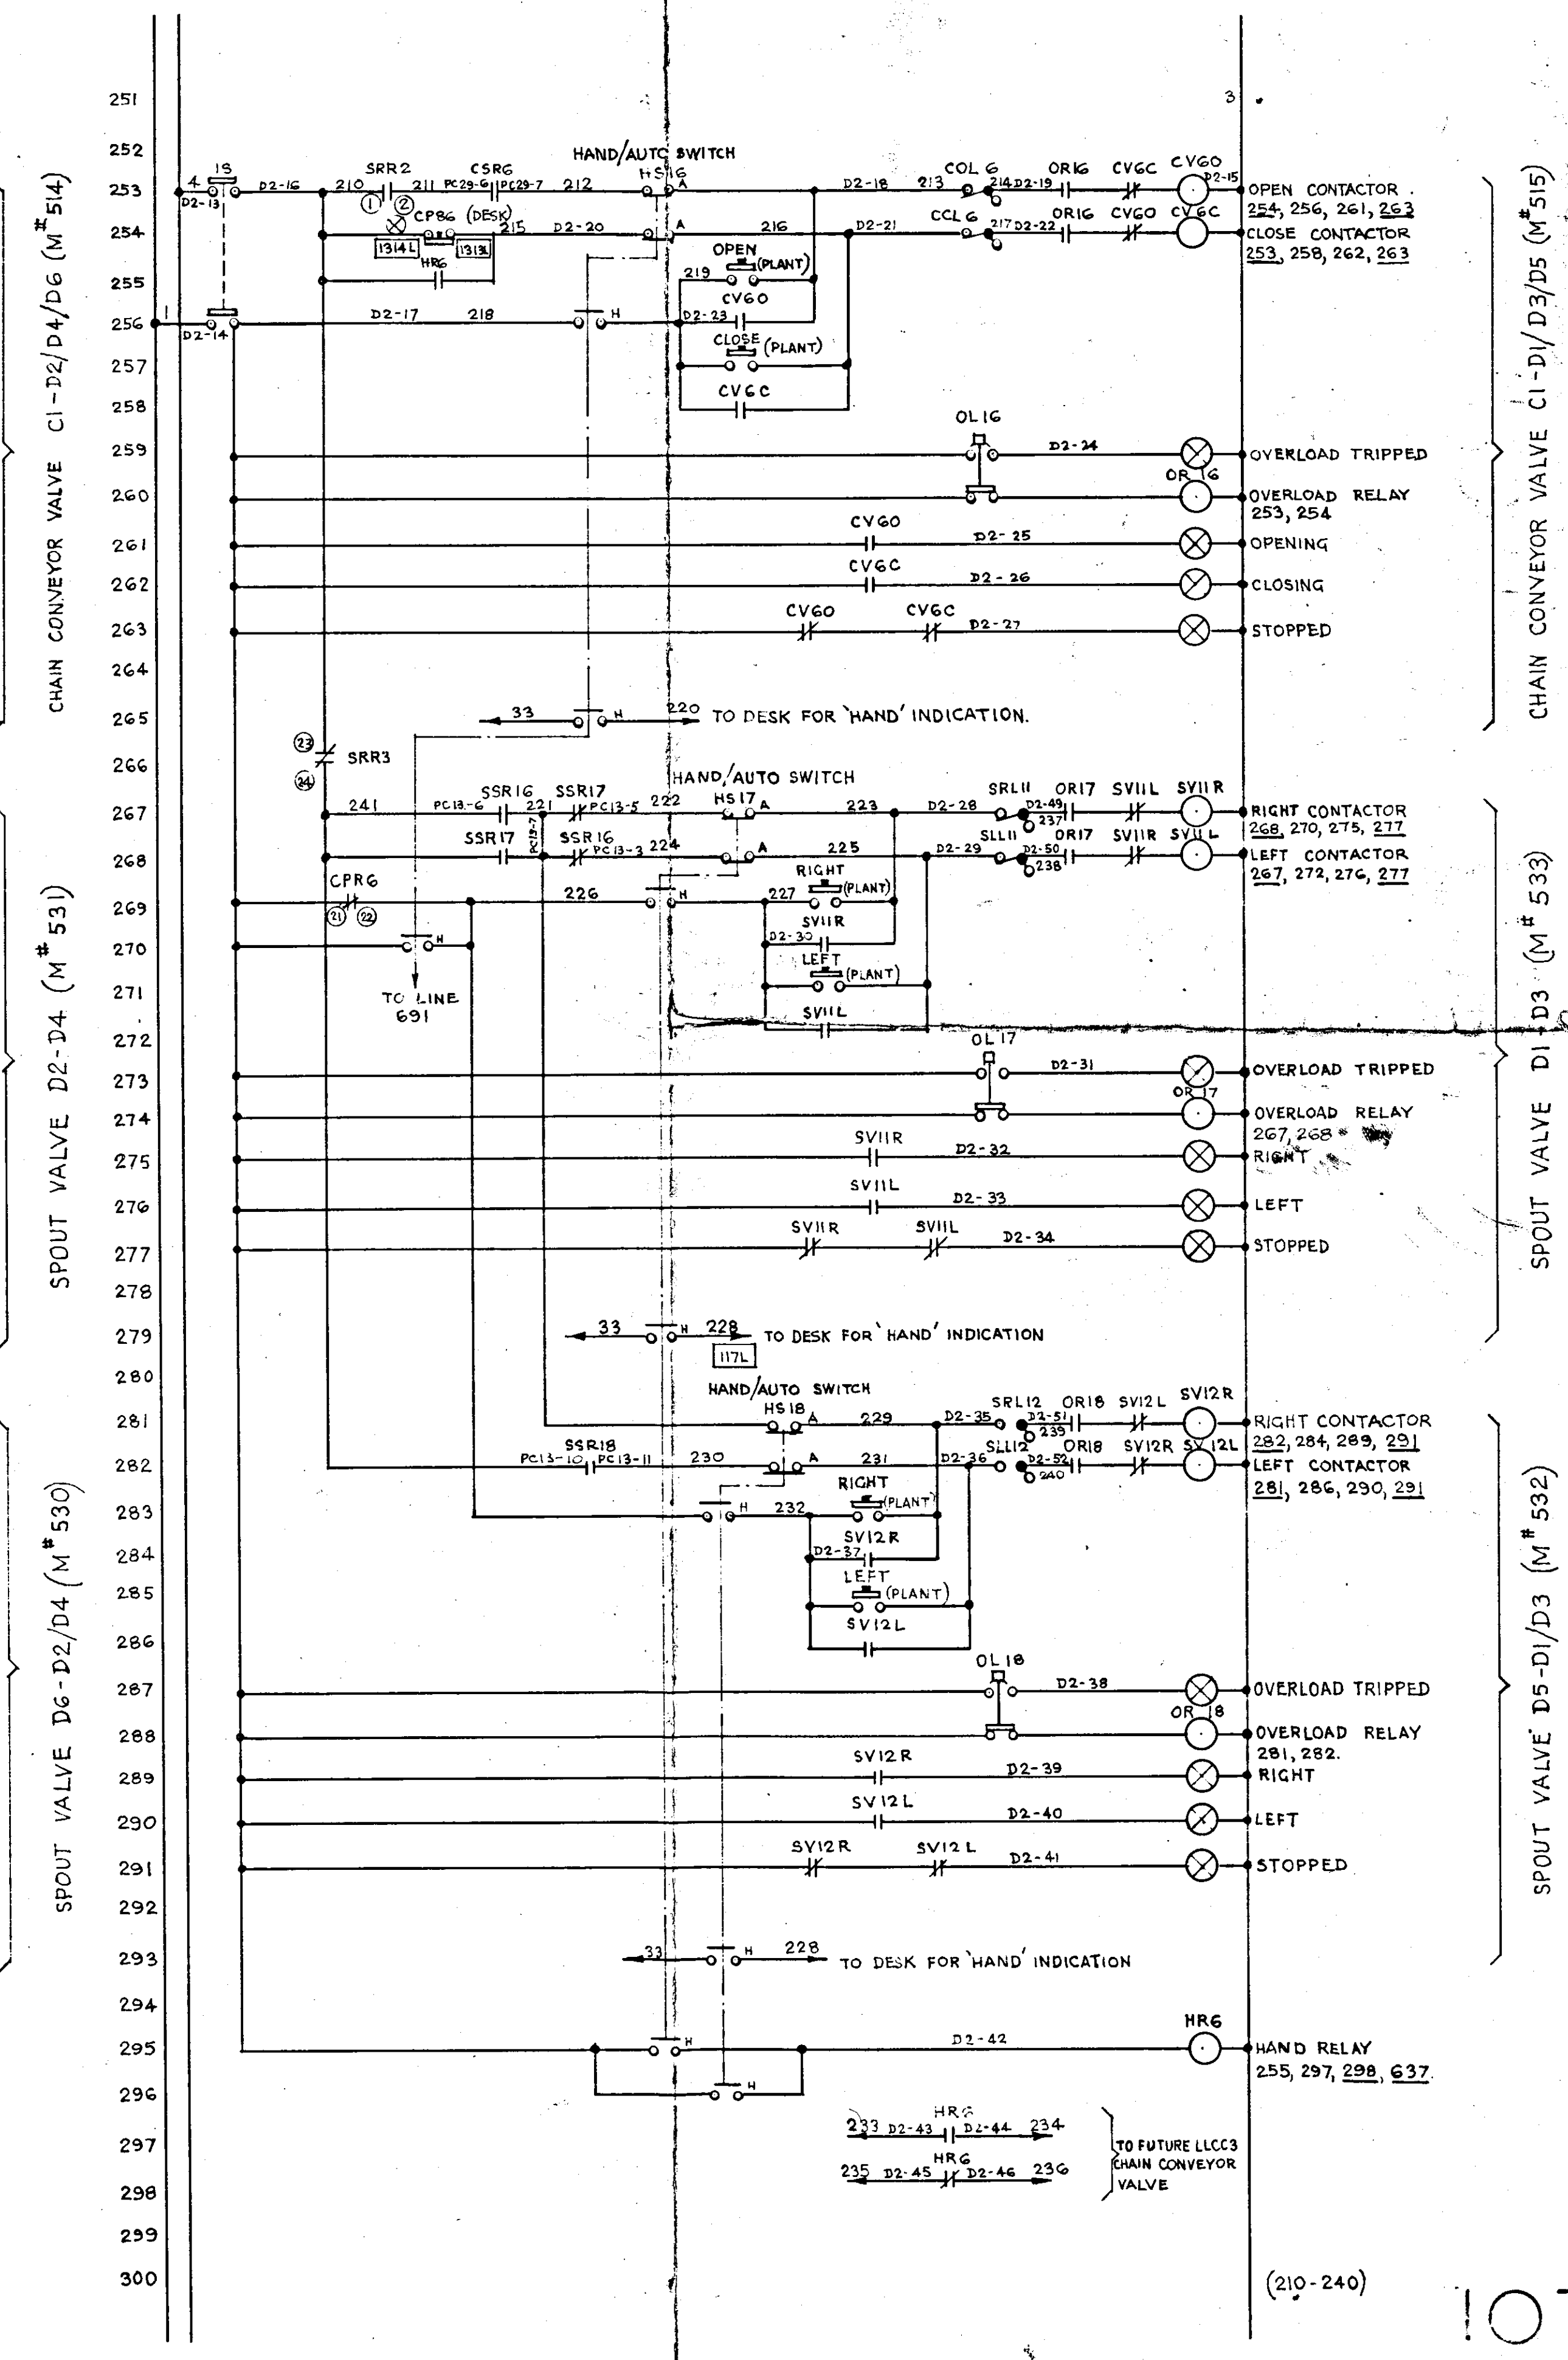

(210-240)

④

1072

SCHEME FOR MCC5 B - SEAFORTH GRAIN TERMINAL

THE DESIGN AND MANUFACTURING INFORMATION CONTAINED IN	ISSUE	1	2	3	4	5	6
--	-------	---	---	---	---	---	---

THIS DRAWING IS THE EXCLUSIVE
RIGHT OF DEWHURST & PARTNER

DTX 361 AC/2

OR USED FOR MANUFACTURING PURPOSES.	
-------------------------------------	--

KEY DIAG No	—
EXT DIAG No	STX 361 AC

DTX 361 AC/2

REL. DIAG. No	DTX 361 AC/2
PANEL LAYOUT No HTX 361 AC	

[illegible]

DTX 361 AC/2

DTX 361 AC/2