


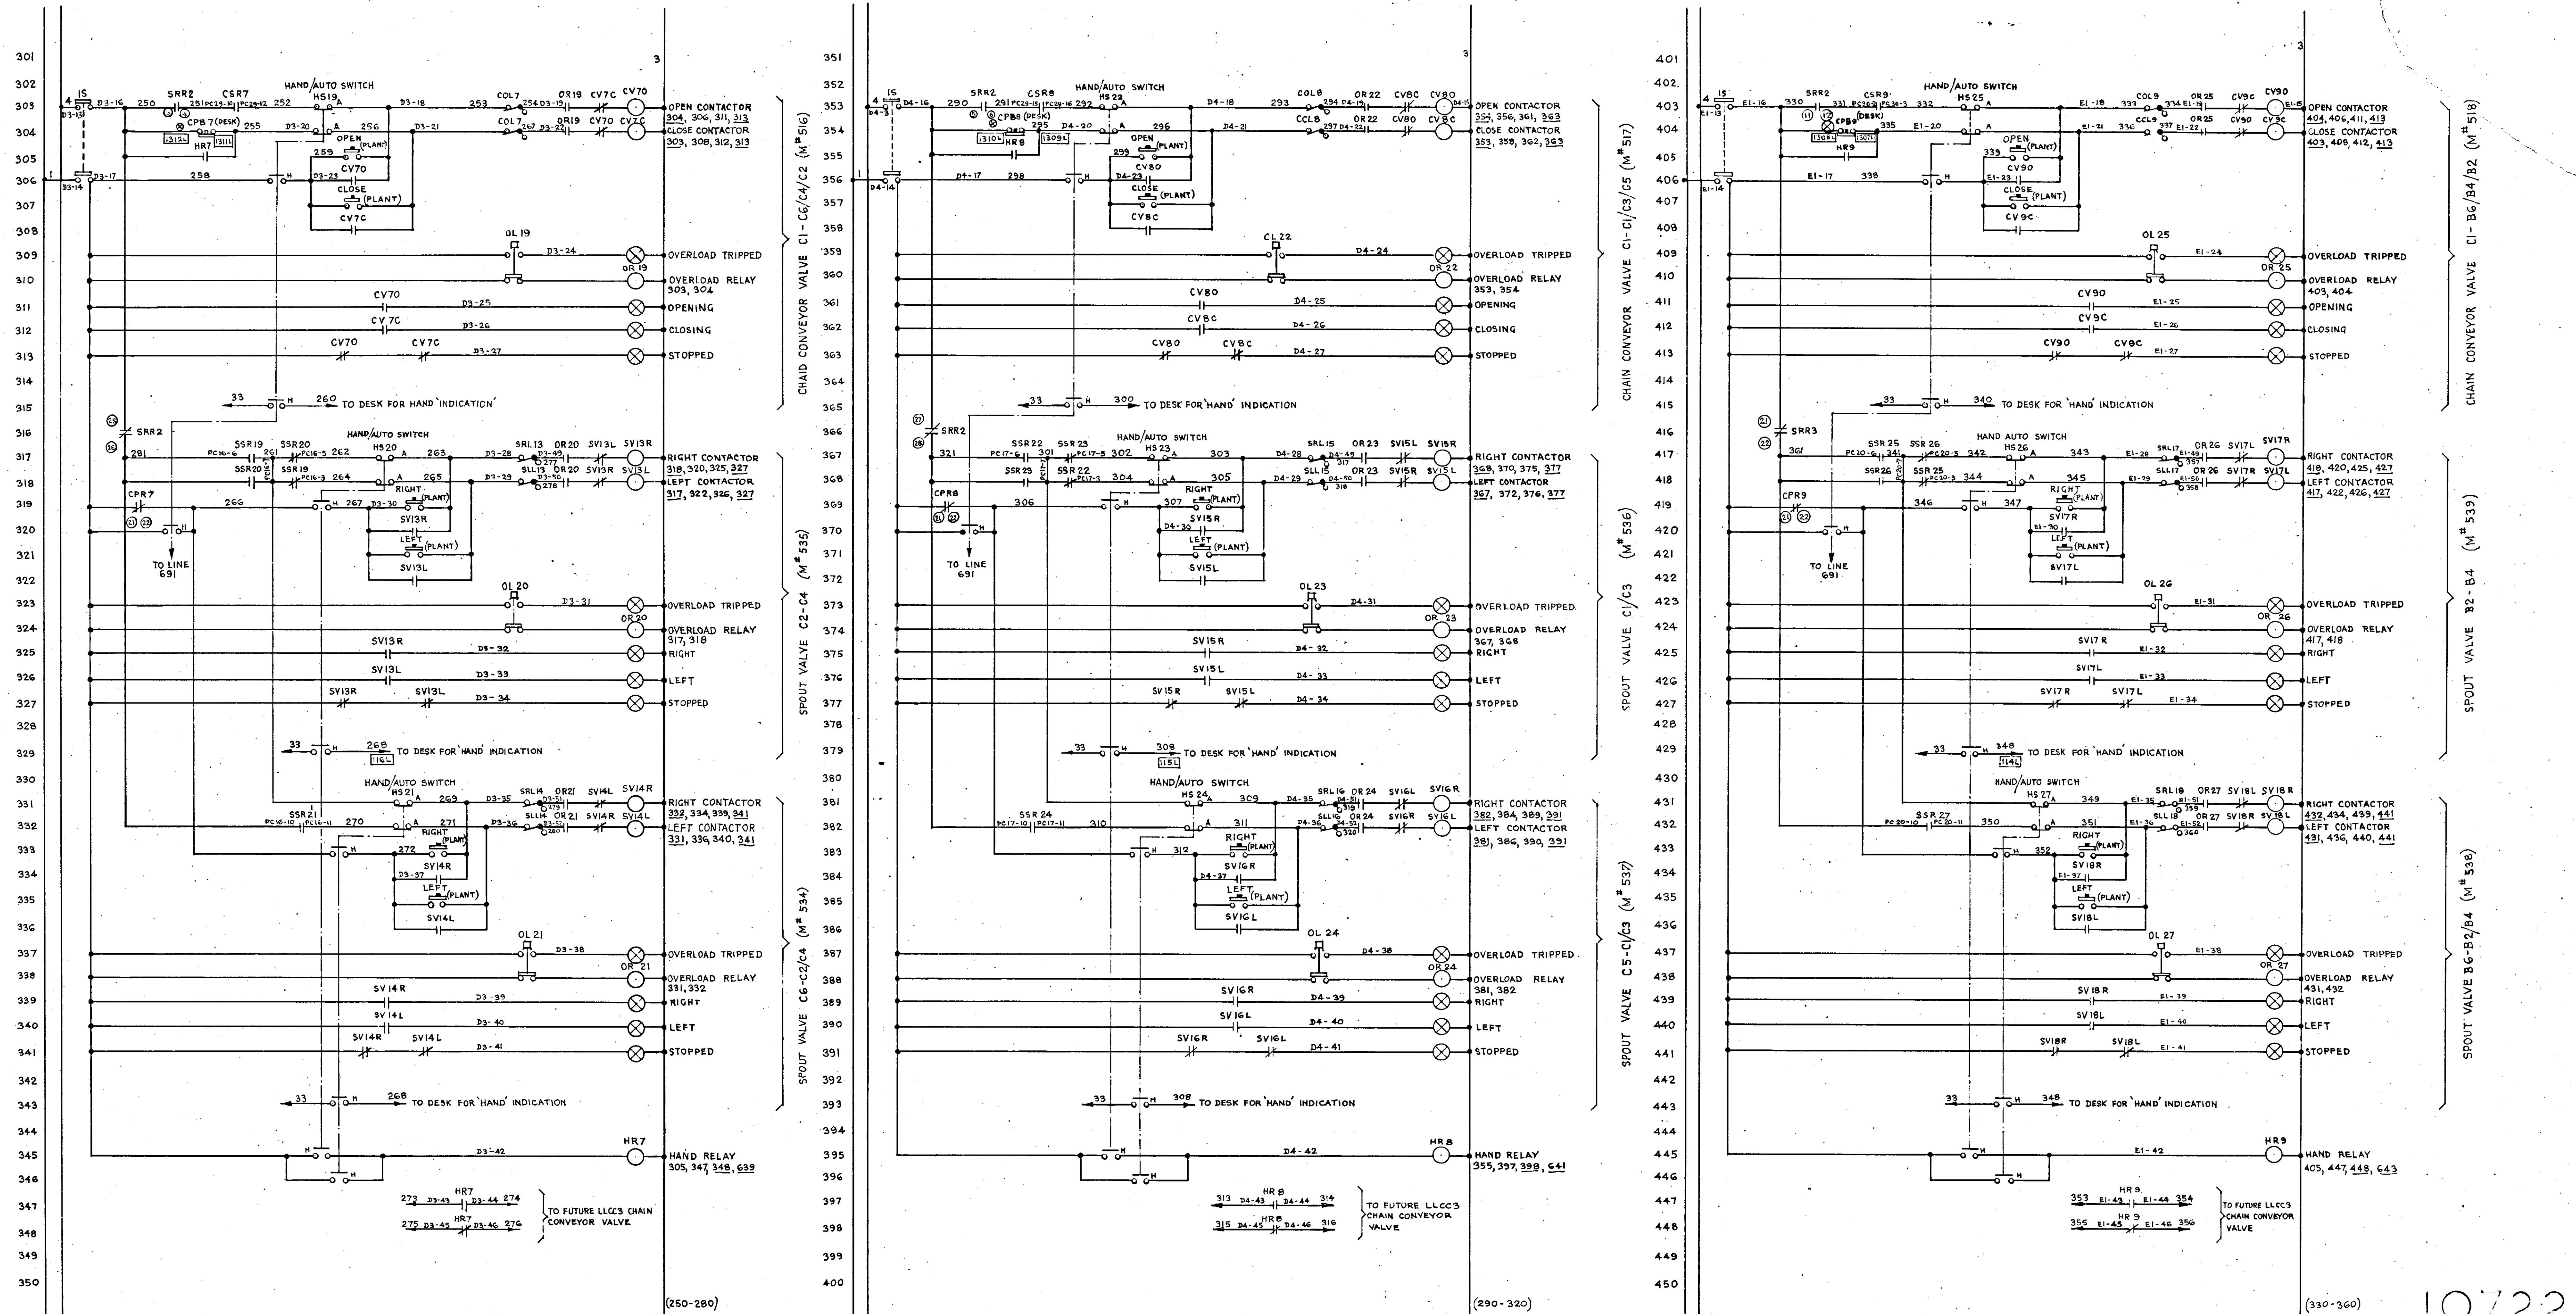

NOTES:-

⊗ STAYPUT TYPE PUSHBUTTON WITH
MANUAL INTERLOCKING & BLOCKING

IF RIGHT CONTACTOR IS ENERGISED
THIS INDICATES PLATE VALVE CLOSED
ON RIGHT SIDE. THUS GRAIN WILL
FLOW TO THE LEFT.

DEWHURST & PARTNER LTD.
MELBOURNE WORKS HOUNSLOW

TITLE	SCHEME FOR MCC 5 B - SEAFORTH GRAIN TERMINAL
-------	--

REVISION: 5 BINS REVERSED	REVISION: 4 DESK TERMINALS ADDED	REVISION: 3 N/C'S ON SR2 & SR3'S ADDED	REVISION: 2 SPOUT VALVE DESIGNATIONS INTERCHANGED. FIBERS ADDED.	REVISION: 1 SRL 13-8 & SRL 13-18 ADDED	DRAWN BY B.J.C. DATE 2 - 3 - 71 CHECKED BY APPROVED BY DATE
ORIGIN: ICD 1/4/71Z SCD. JS.	ORIGIN: ICD 1/2/72 SCD. JS.	ORIGIN: SCD. 2/6/71 SCD. J.T.	ORIGIN: EISP 3/5/71 SCD. B.J.L.	ORIGIN: EISP 26/3/71 SCD. J.T.	

SCHEME FOR MCC 5B — SEAFORTH GRAIN TERMINAL												
THE DESIGN AND MANUFACTURING INFORMATION CONTAINED IN THIS DRAWING IS THE EXCLUSIVE RIGHT OF DEWHURST & PARTNER LTD. AND MUST NOT BE COPIED OR USED FOR MANUFACTURING PURPOSES					ISSUE 1/2/3/4/5							
					DTX 361AC/3							
KEY DIAG N°												
EXT. DIAG N° STX 361 AC												
REL DIAG N°												
PANEL LAYOUT N° HTX 361 AC					DTX 361AC/3							