


10722

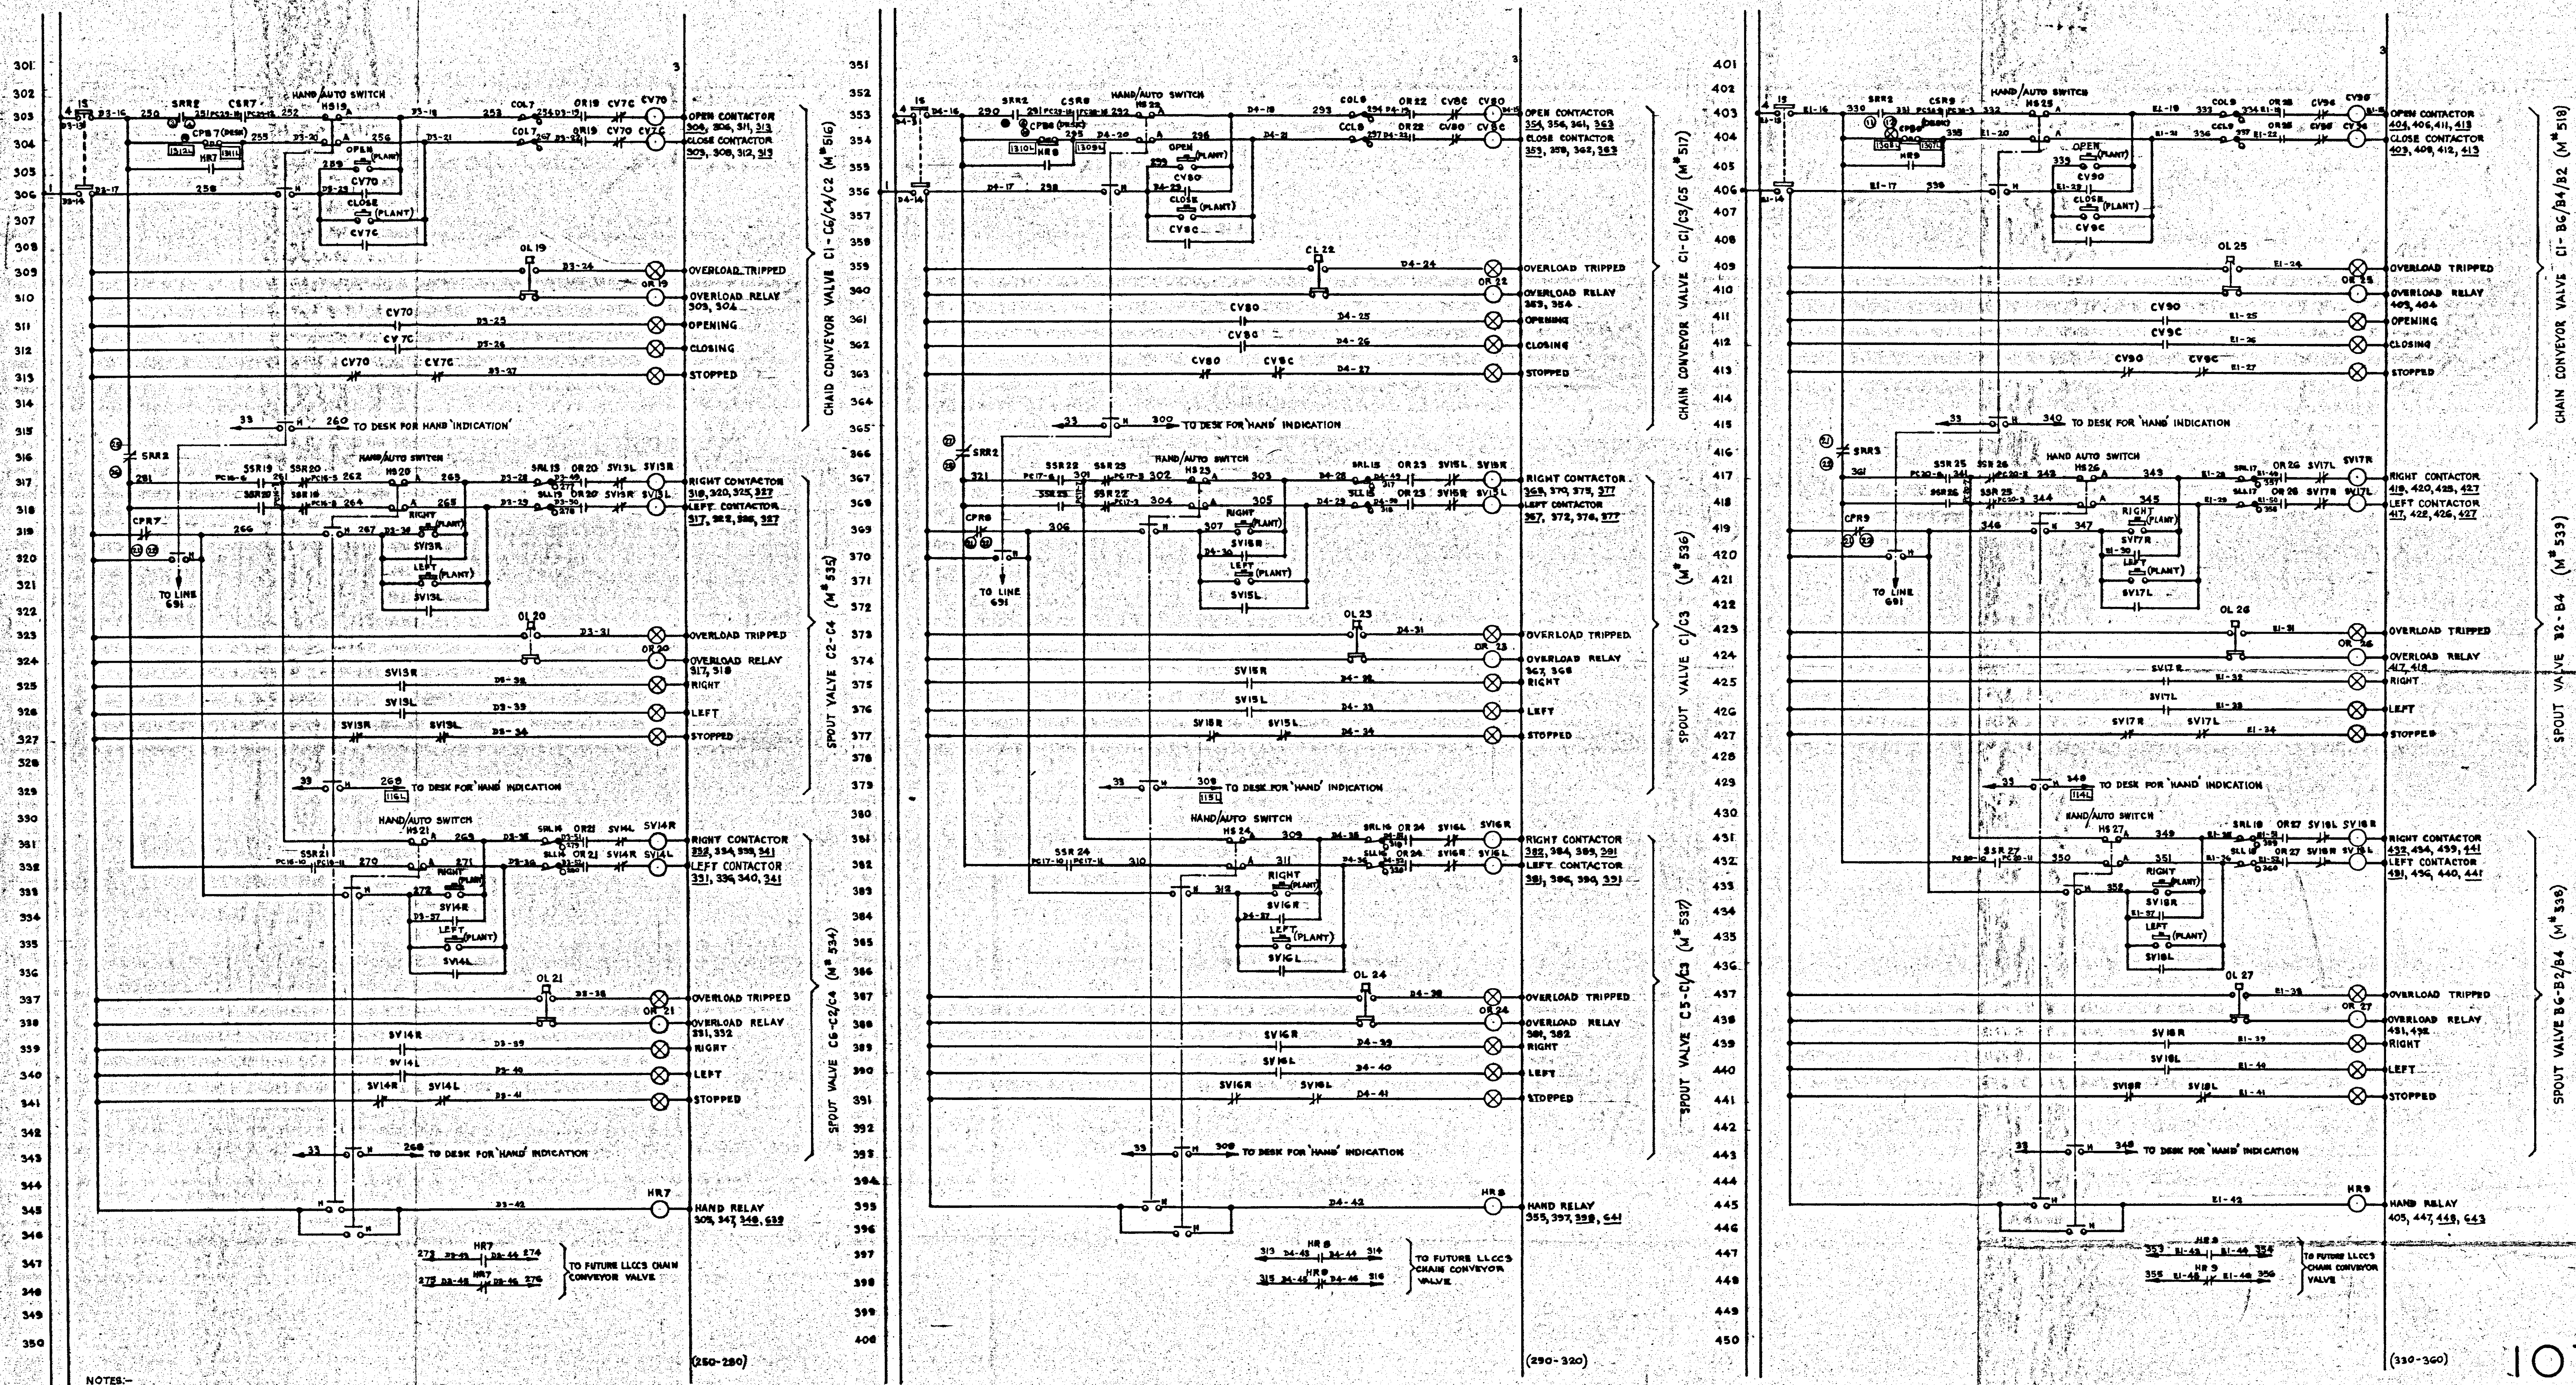

NOTES:-

⊗ STAYPUT TYPE PUSHBUTTON WITH
MANUAL INTERLOCKING & BLOCKING

IF RIGHT CONTACTOR IS ENERGISED
THIS INDICATES PLATE VALVE CLOSED
ON RIGHT SIDE. THUS GRAIN WILL
FLOW TO THE LEFT

(250-280)

(290-320)

(330-360)

10722

DEWHURST & PARTNER LTD.
MELBOURNE WORKS HOUNSLOW.

TITLE SCHEME FOR MCC 5 B - SEAFORTH GRAIN TERMINAL

REVISION: 5
BINS REVERSED

ORIGIN: ICD
14/7/78 SGP. J

REVISION: 4
DESK TERMINALS
ADDED
ORIGIN: ICD
1/2/73 SCD

REVISION: 3
N/C'S ON SRR2 &
SRR3 ADDED
ORIGINAL E19R.
21/6/71 SCD IT

REVISION: 2
SPOUT VALVE
DESIGNATIONS
INTERCHANGED -
NOTES ADDED.
ORIGIN: EISP.
3/5/71 SGP BJA

REVISION: 1
SWL 13-10 & SLL 13-10
ADDED
ORIGIN: BISR
26/3/71 SCD LT

DRAWN BY	B.J.C.
DATE	2-3-71
CHECKED BY	
APPROVED BY	
DATE	

KEY DIAG N
EXT. DIAG N
REL. DIAG N
PANEL LAYO

STX 361 AC
UT N° WTX 361 AC

SCHEME FOR MCC5B - SEAFORTH GRAIN TERMINAL

THE DESIGN AND MANUFACTURING
INFORMATION CONTAINED IN
THIS DRAWING IS THE EXCLUSIVE
RIGHT OF DEWHURST & PARTNER
LTD. AND MUST NOT BE COPIED
OR USED FOR MANUFACTURING
PURPOSES

ISSUE 12345

DTX 361AC/3

DTX 361AC/3