


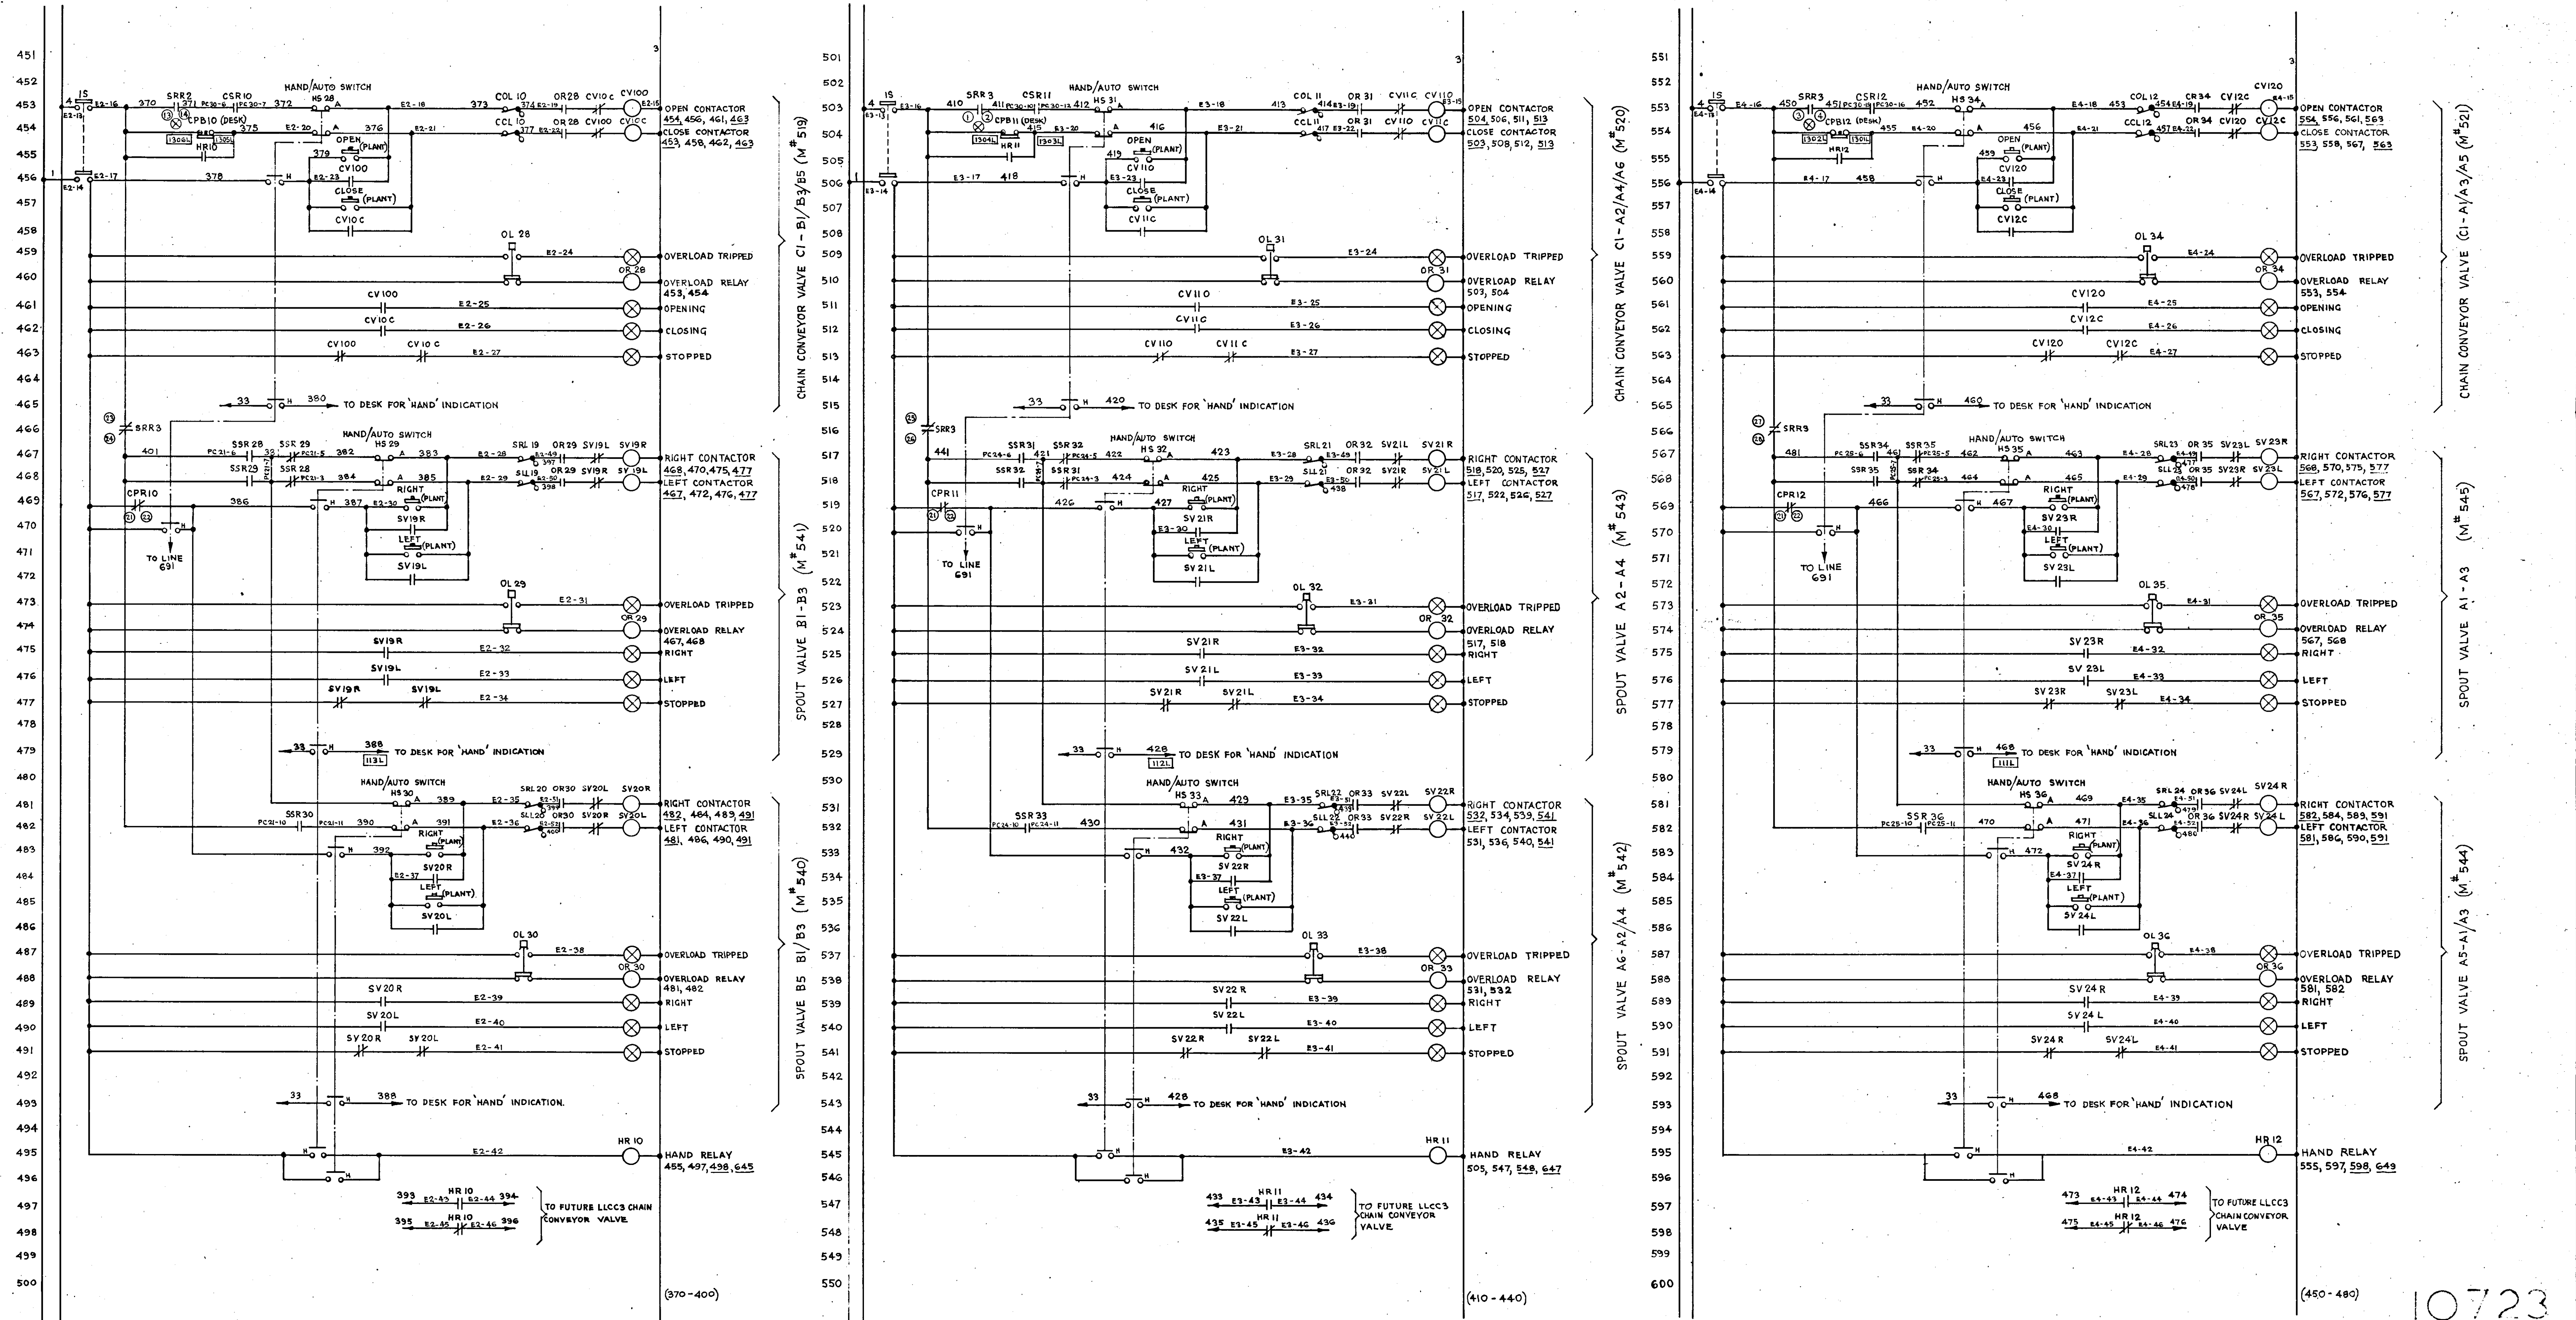

NOTES:-
 ⓧ STAYPUT TYPE PUSHBUTTON WITH
 MANUAL INTERLOCKING & BLOCKING

IF RIGHT CONTACTOR IS ENERGISED
 THIS INDICATES PLATE VALVE CLOSED
 ON RIGHT SIDE, THUS GRAIN WILL
 FLOW TO THE LEFT.

DEWHURST & PARTNER LTD.
 MELBOURNE WORKS HOUNSLOW

TITLE: SCHEME FOR MCC5B - SEAFORTH GRAIN TERMINAL

REVISION: 5
 BINS REVERSED
 ORIGIN: ICD
 14/7/72 SGD. J.S.

REVISION: 4
 M/C3 ON SRR3 ADDED
 ORIGIN: E.I.S.P.
 21/6/71 SGD. J.T.

REVISION: 3
 SPOUT VALVE
 DESIGNATIONS
 INTERCHANGED.
 NOTES ADDED
 ORIGIN: E.I.S.P.
 3/5/71 SGD. B.J.C.

REVISION: 2
 M540 & M541
 TITLES MODIFIED
 ORIGIN: E.I.S.P.
 14/4/71 SGD. J.T.

REVISION: 1
 SRR19-24 &
 SLL19-24 ADDED
 ORIGIN: E.I.S.P.
 26/3/71 SGD. J.T.

DRAWN BY B.J.C.
 DATE 2-3-71
 CHECKED BY
 APPROVED BY
 DATE

SCHEME FOR MCC5B - SEAFORTH GRAIN TERMINAL	
THE DESIGN AND MANUFACTURING INFORMATION CONTAINED IN THIS DRAWING IS THE EXCLUSIVE RIGHT OF DEWHURST & PARTNER LTD. AND MUST NOT BE COPIED OR USED FOR MANUFACTURING PURPOSES	ISSUE 123456
KEY DIAG No EXT. DIAG No STX 361 AC REL. DIAG. No PANEL LAYOUT No RTX 361 AC	DTX 361 AC/4
	DTX 361 AC/4