


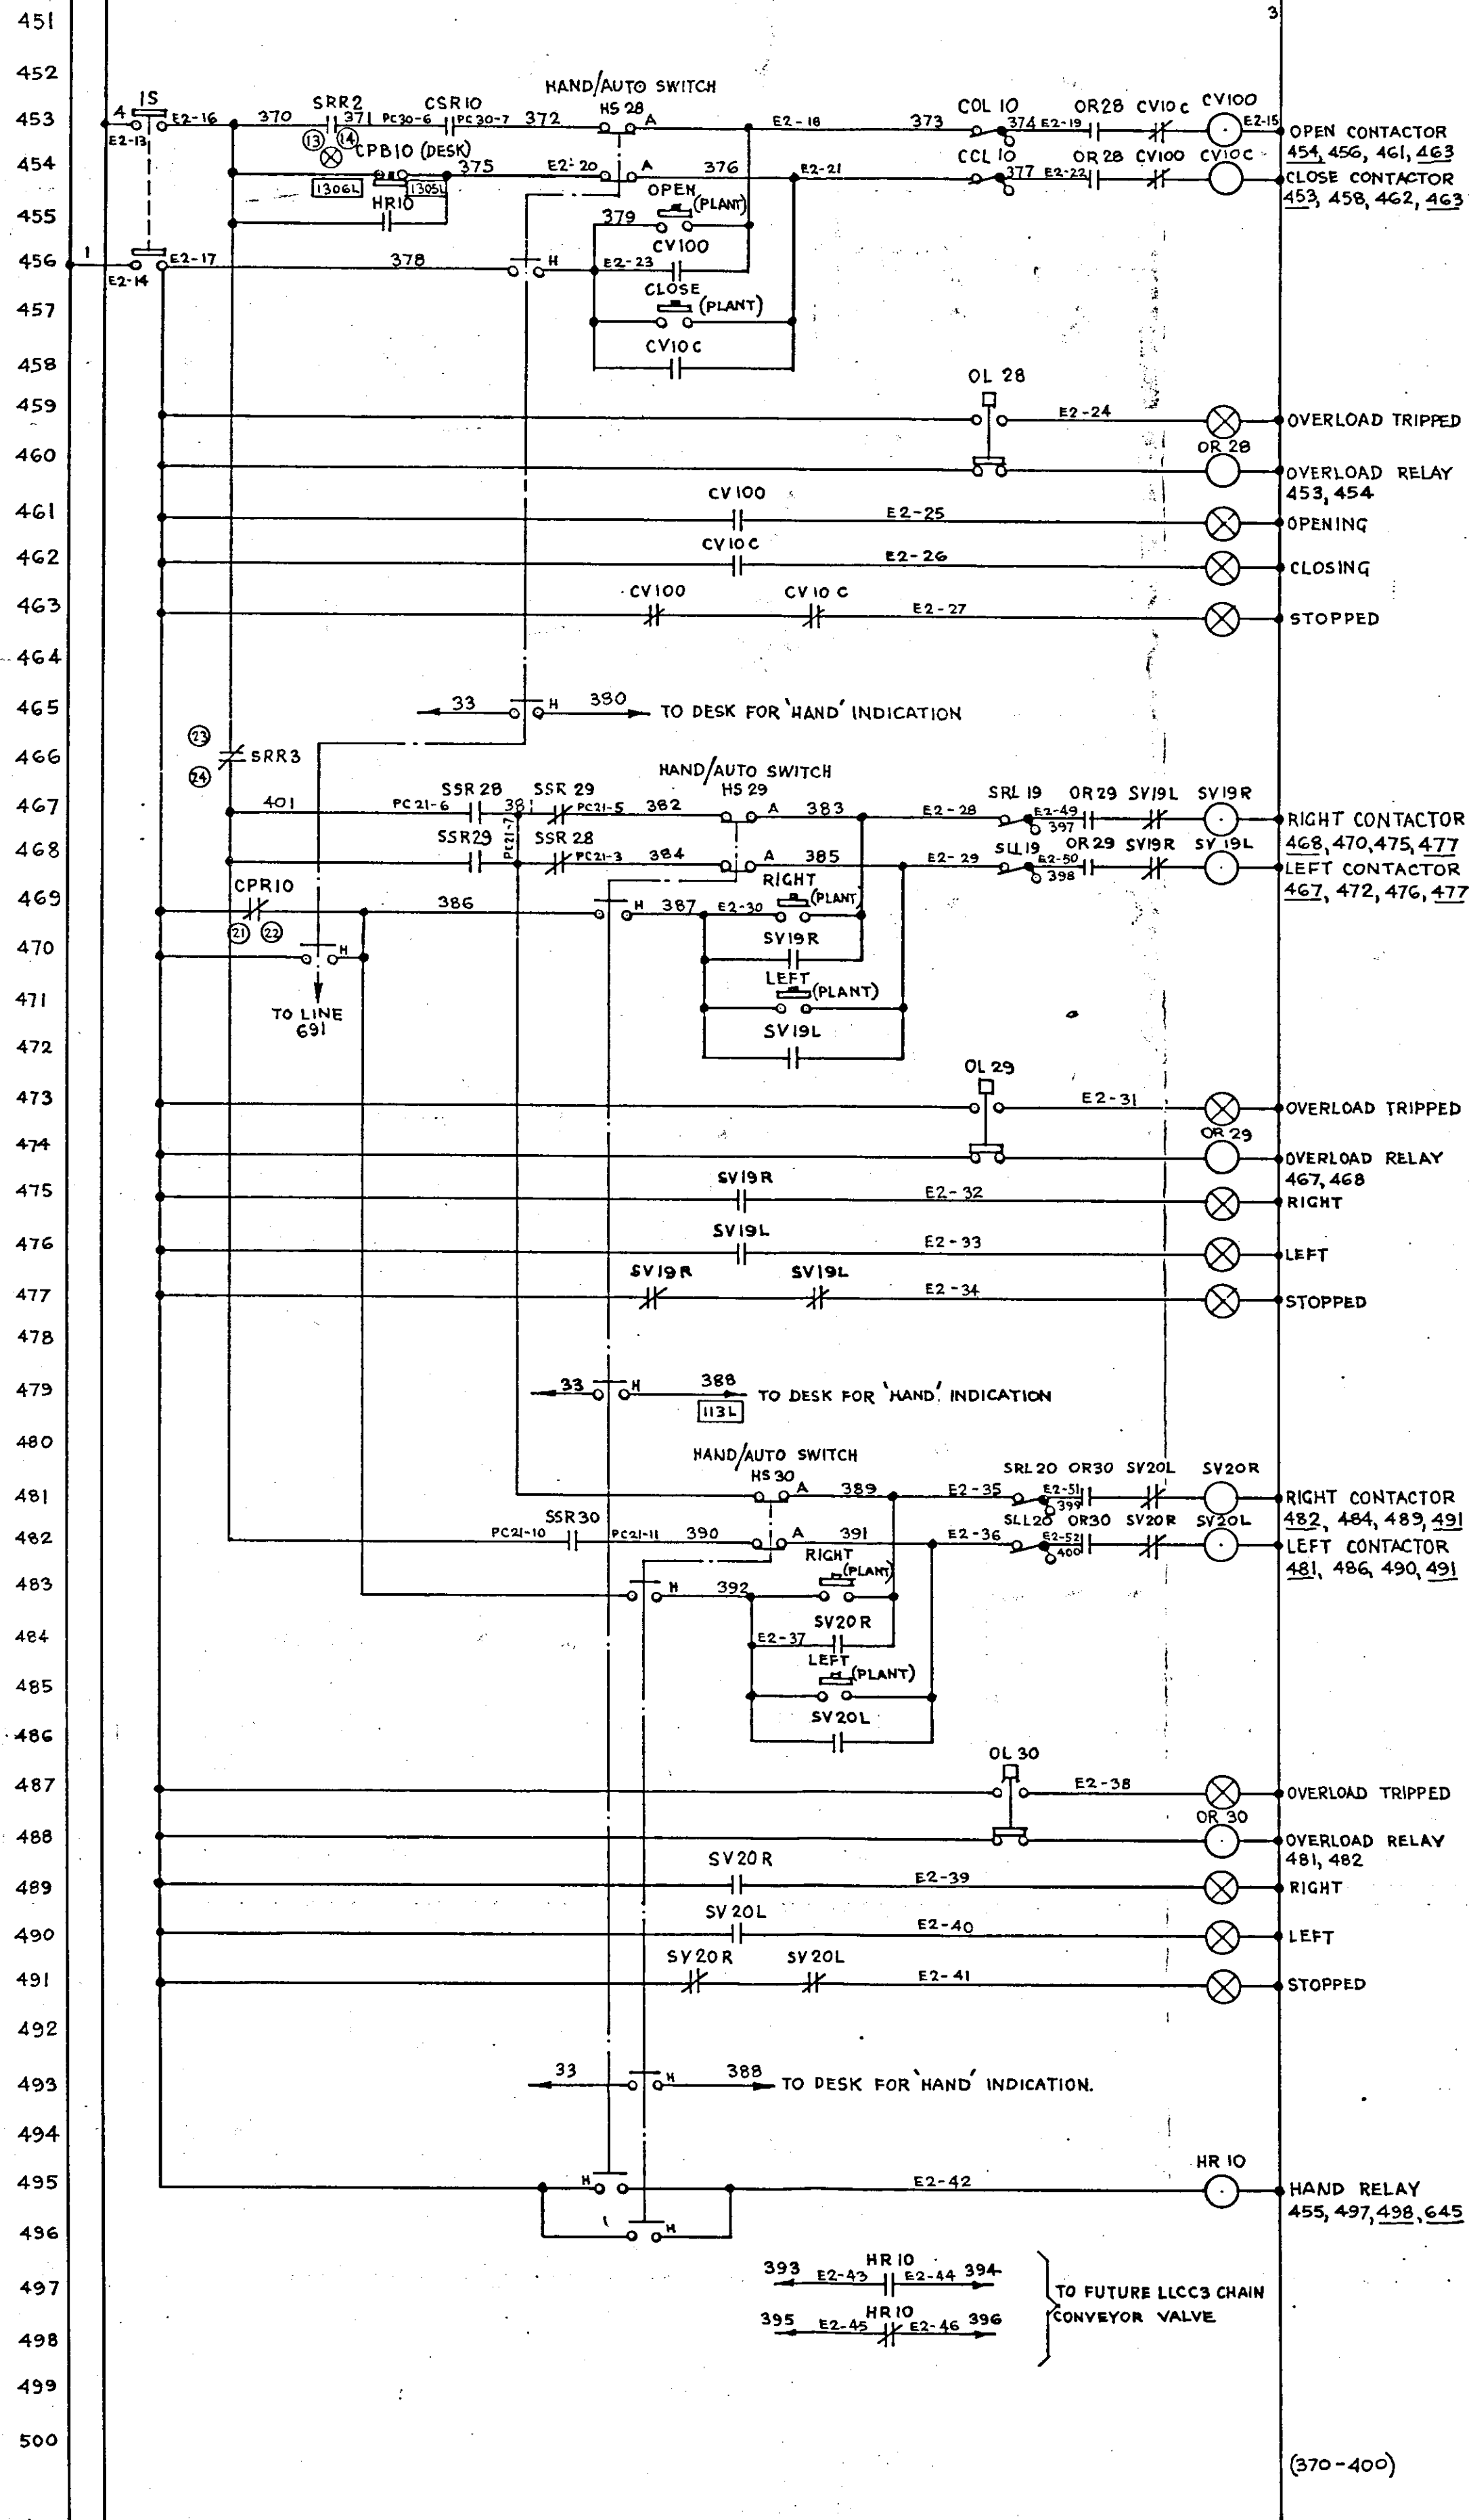

NOTES:-
⊗ STAYPUT TYPE PUSH-BUTTON WITH
MANUAL INTERLOCKING & BLOCKING

IF RIGHT CONTACTOR IS ENERGISED
THIS INDICATES PLATE VALVE CLOSED
ON RIGHT SIDE, THUS GRAIN WILL
FLOW TO THE LEFT.

DEWHURST & PARTNER LTD.
MELBOURNE WORKS HOUNSLOW

TITLE: SCHEME FOR MCC 5 B - SEAFORTH GRAIN TERMINAL

REVISION: 5
BINS REVERSED
ORIGIN: 1CD
14/7/72 SGD. J

REVISION: 4
N/C3 ON SRR3 ADD

ORIGIN: E.I.S.P.
21/6/71 SQD. J

REVISION: 3
SPOUT VALVE
DESIGNATIONS
INTERCHANGED.
NOTES ADDED
ORIGIN: E.I.S.F.
3/5/71 SGD B

REVISION: 2 M [#] 540 & M [#] 5 TITLES MODIFIED	ORIGIN: EISF 14/4/71 SGD.
---	------------------------------

REVISION: 1
SRL 19-24 &
SLL 19-24 ADD
ORIGIN: E.L.S.
26/3/71 SGD

DRAWN BY	DATE 2-3-
	CHECKED BY
	APPROVED BY
	DATE

SCHEME FOR MCC5B - SEAFORTH GRAIN TERMINAL

THE DESIGN AND MANUFACTURING
INFORMATION CONTAINED IN
THIS DRAWING IS THE EXCLUSIVE
RIGHT OF DEWHURST & PARTNER
LTD. AND MUST NOT BE COPIED
OR USED FOR MANUFACTURING
PURPOSES

ISSUE	1	2	3	4	5	6						
-------	---	---	---	---	---	---	--	--	--	--	--	--

DTX 361 AC/4

DTX 361 AC/4

2

10723