

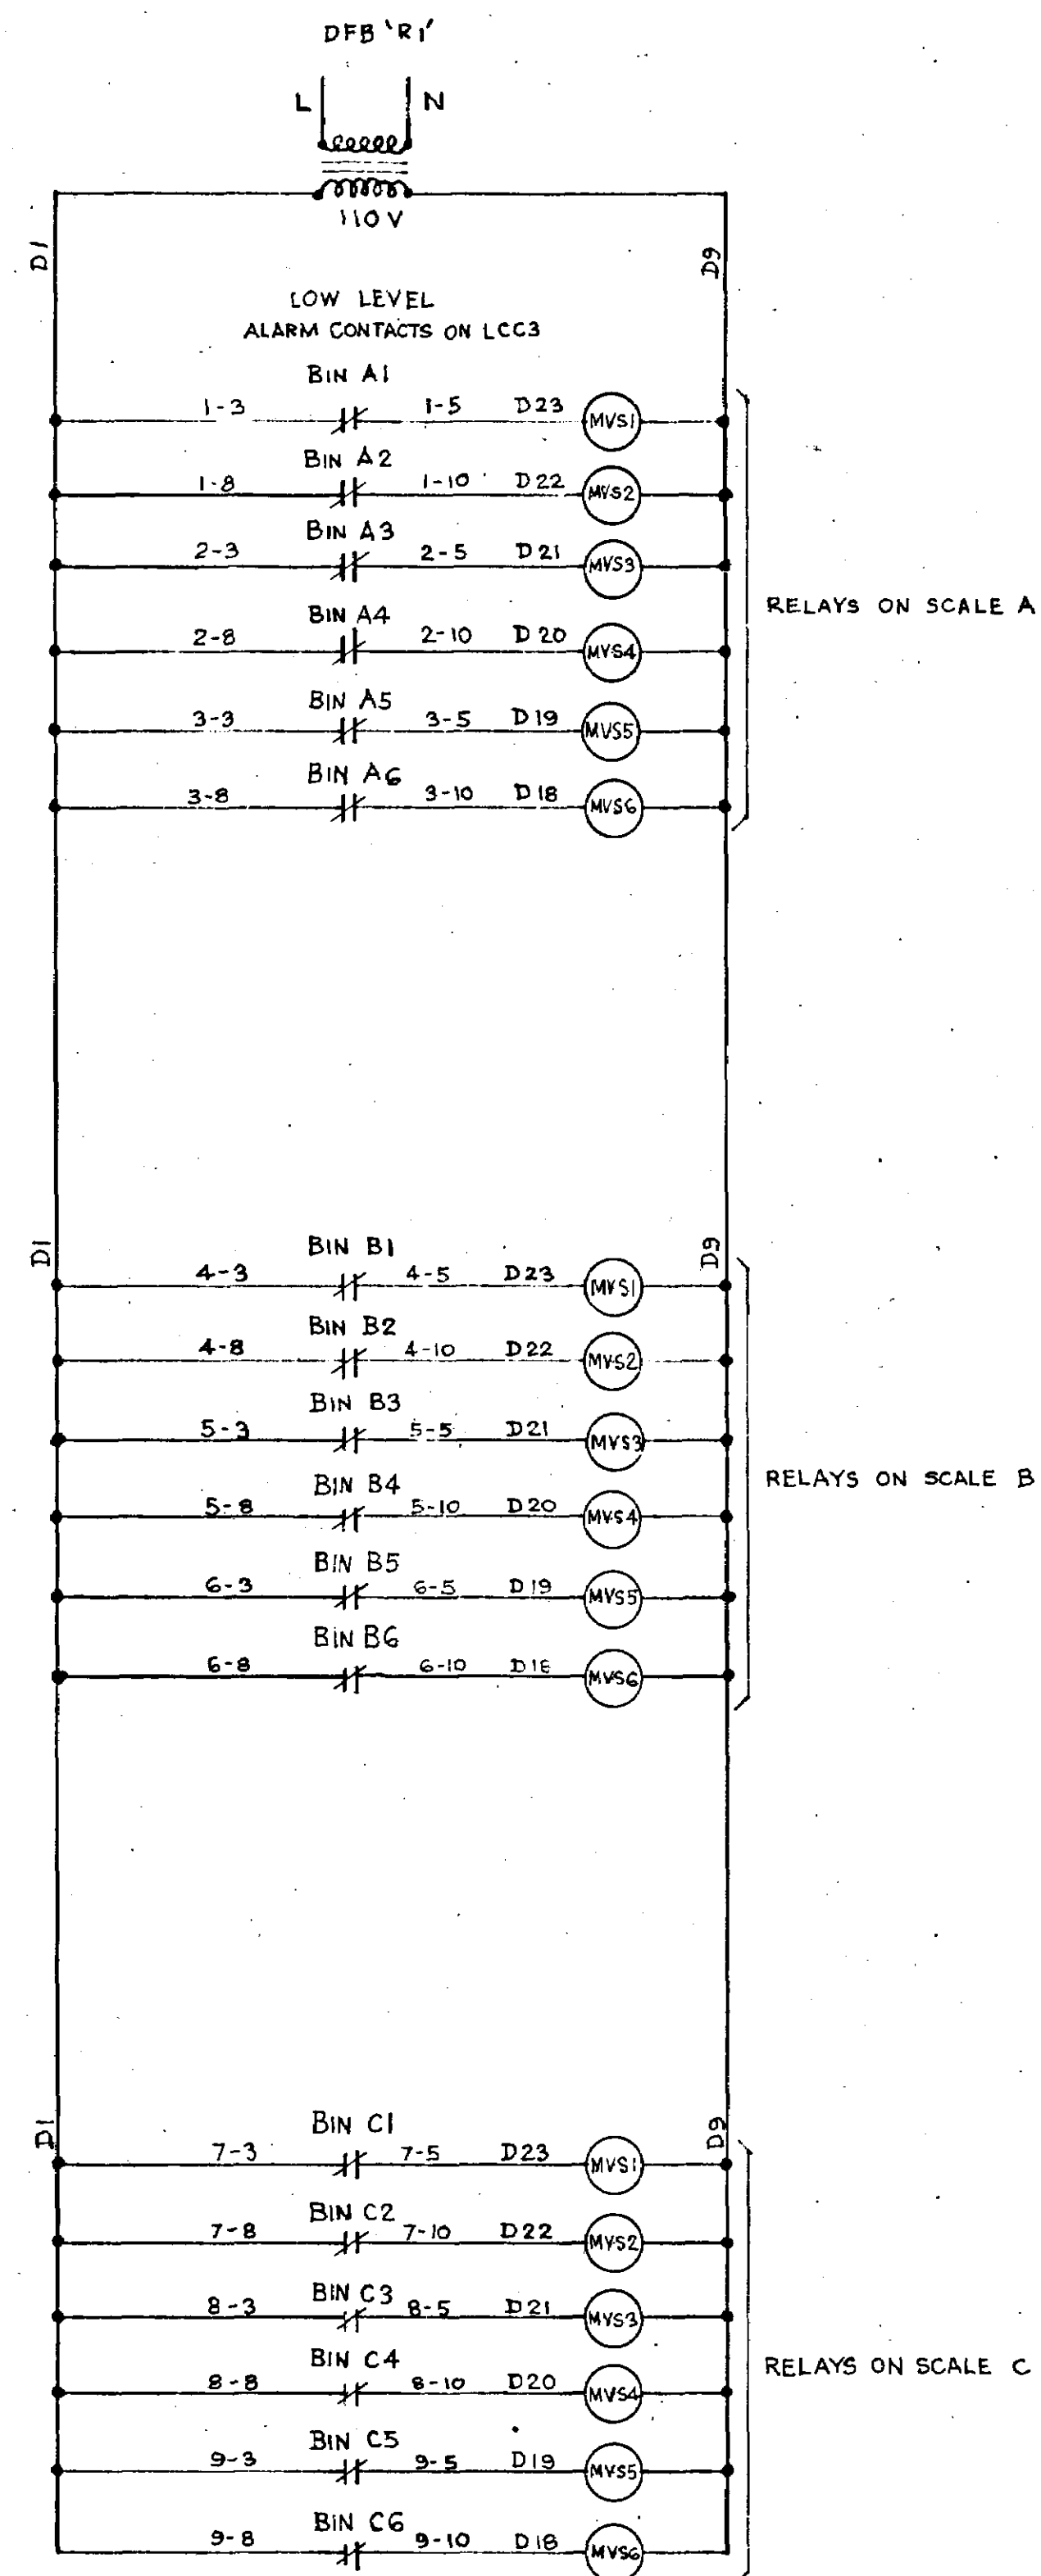
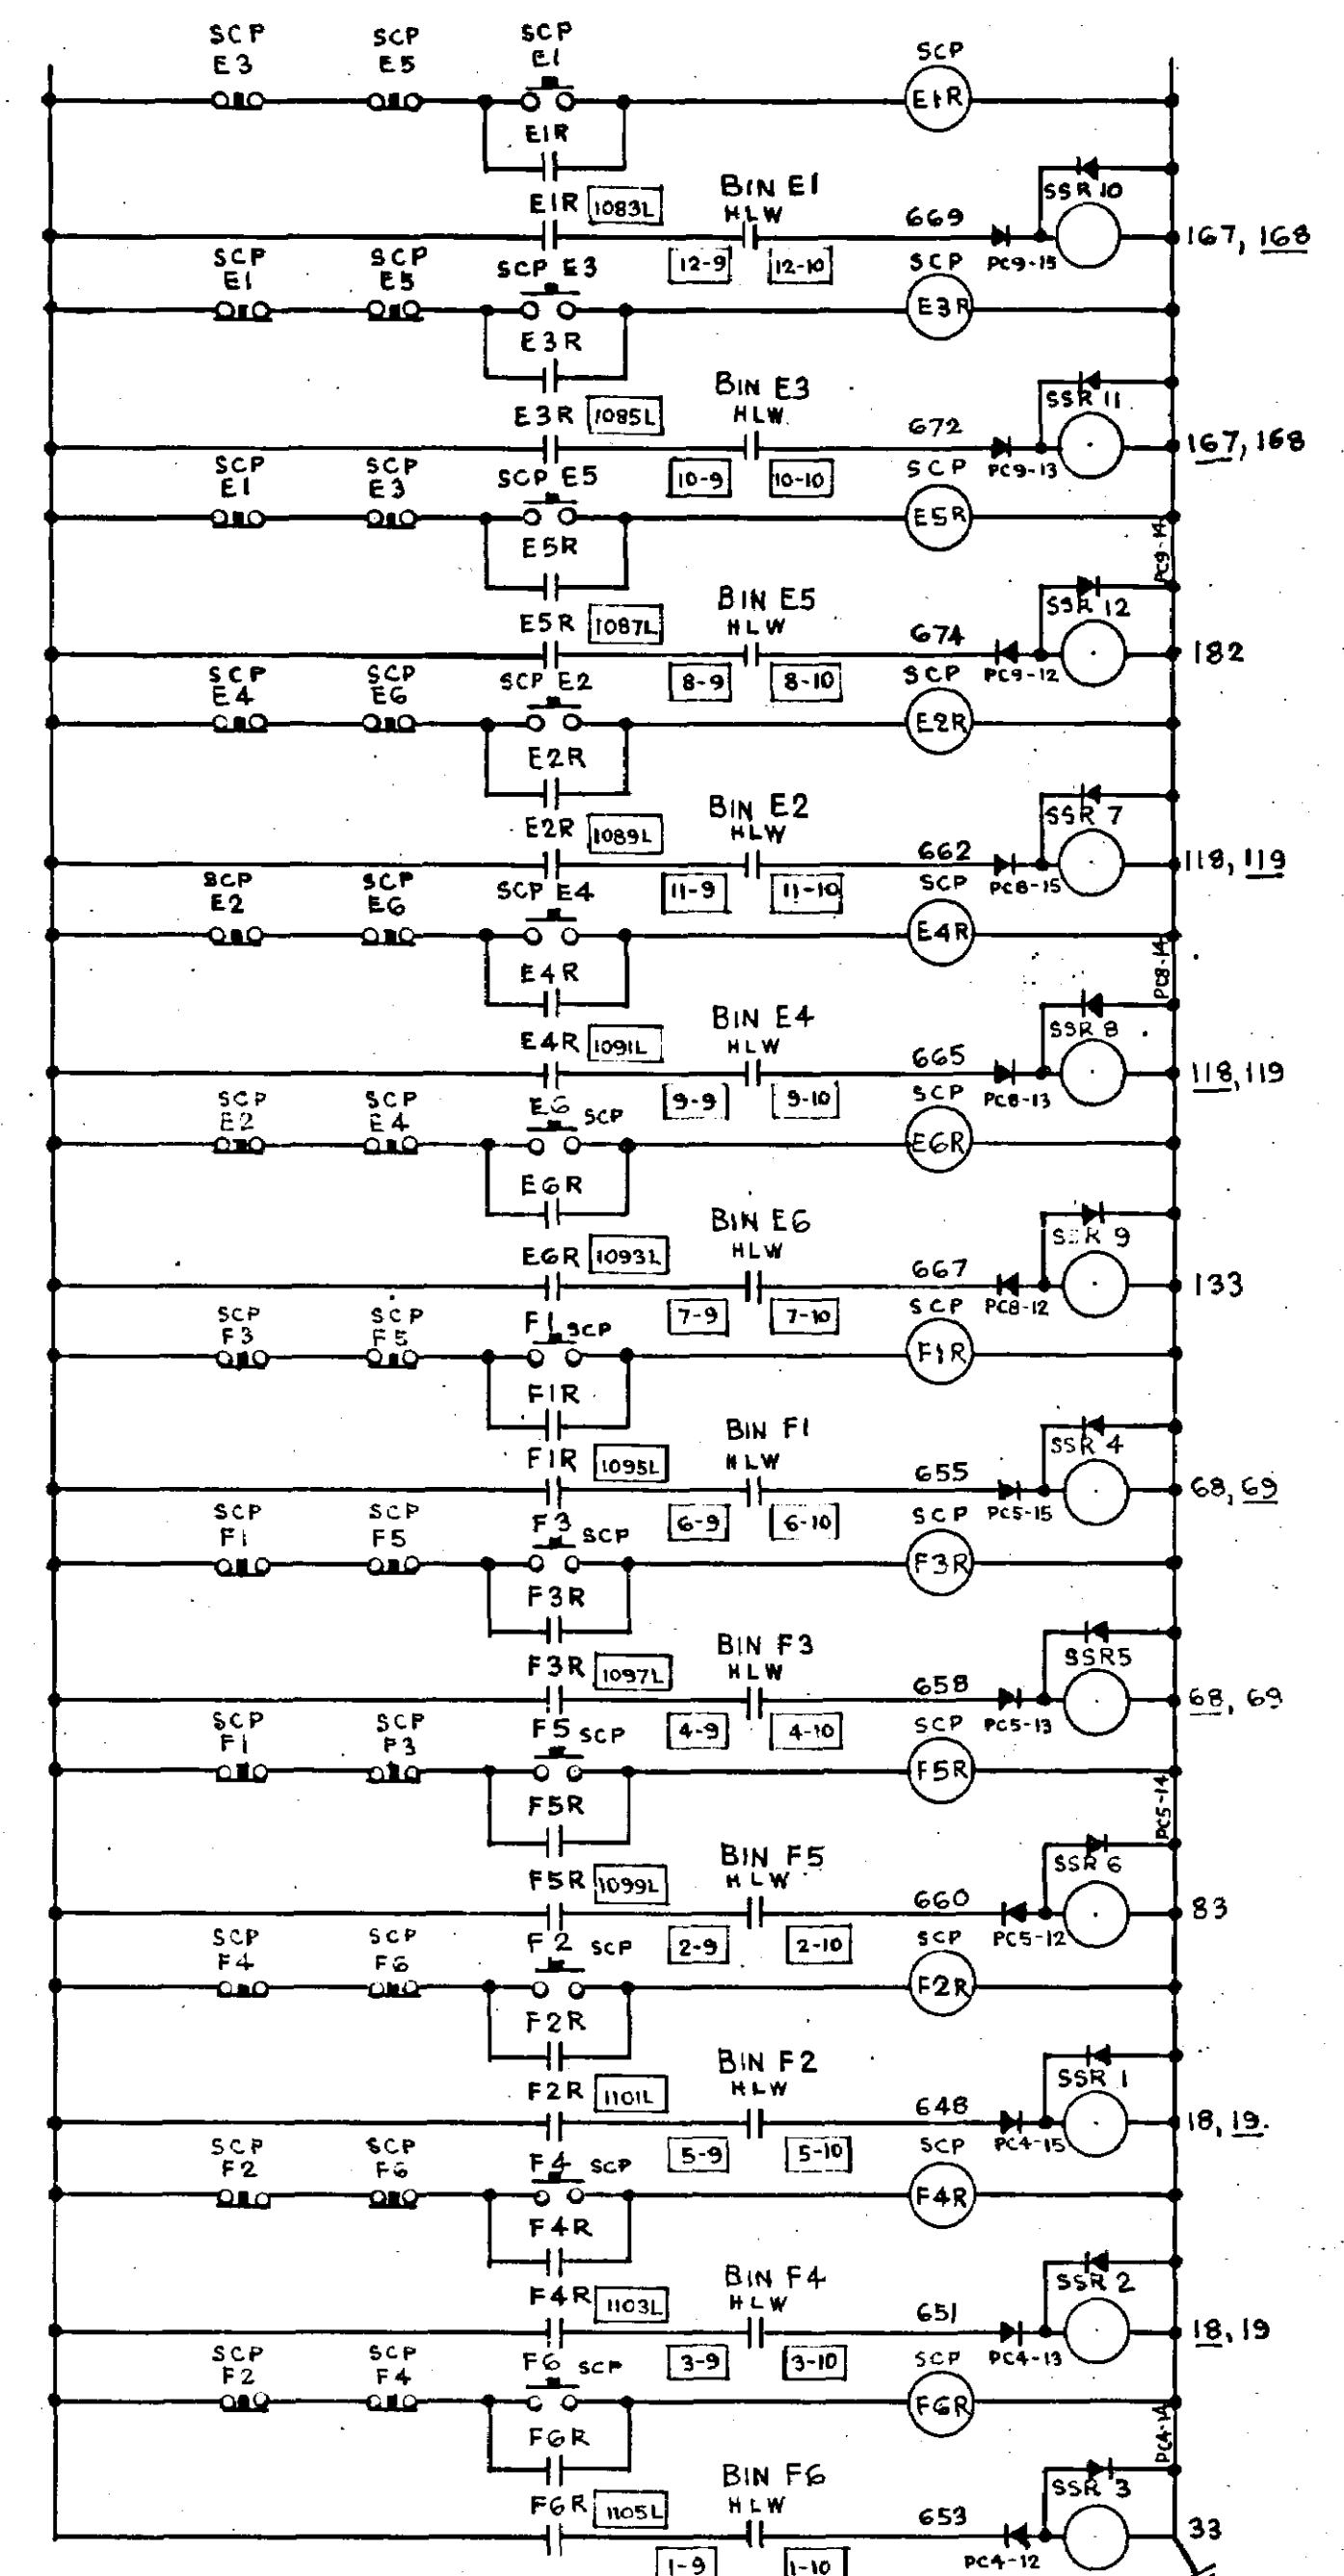


10725

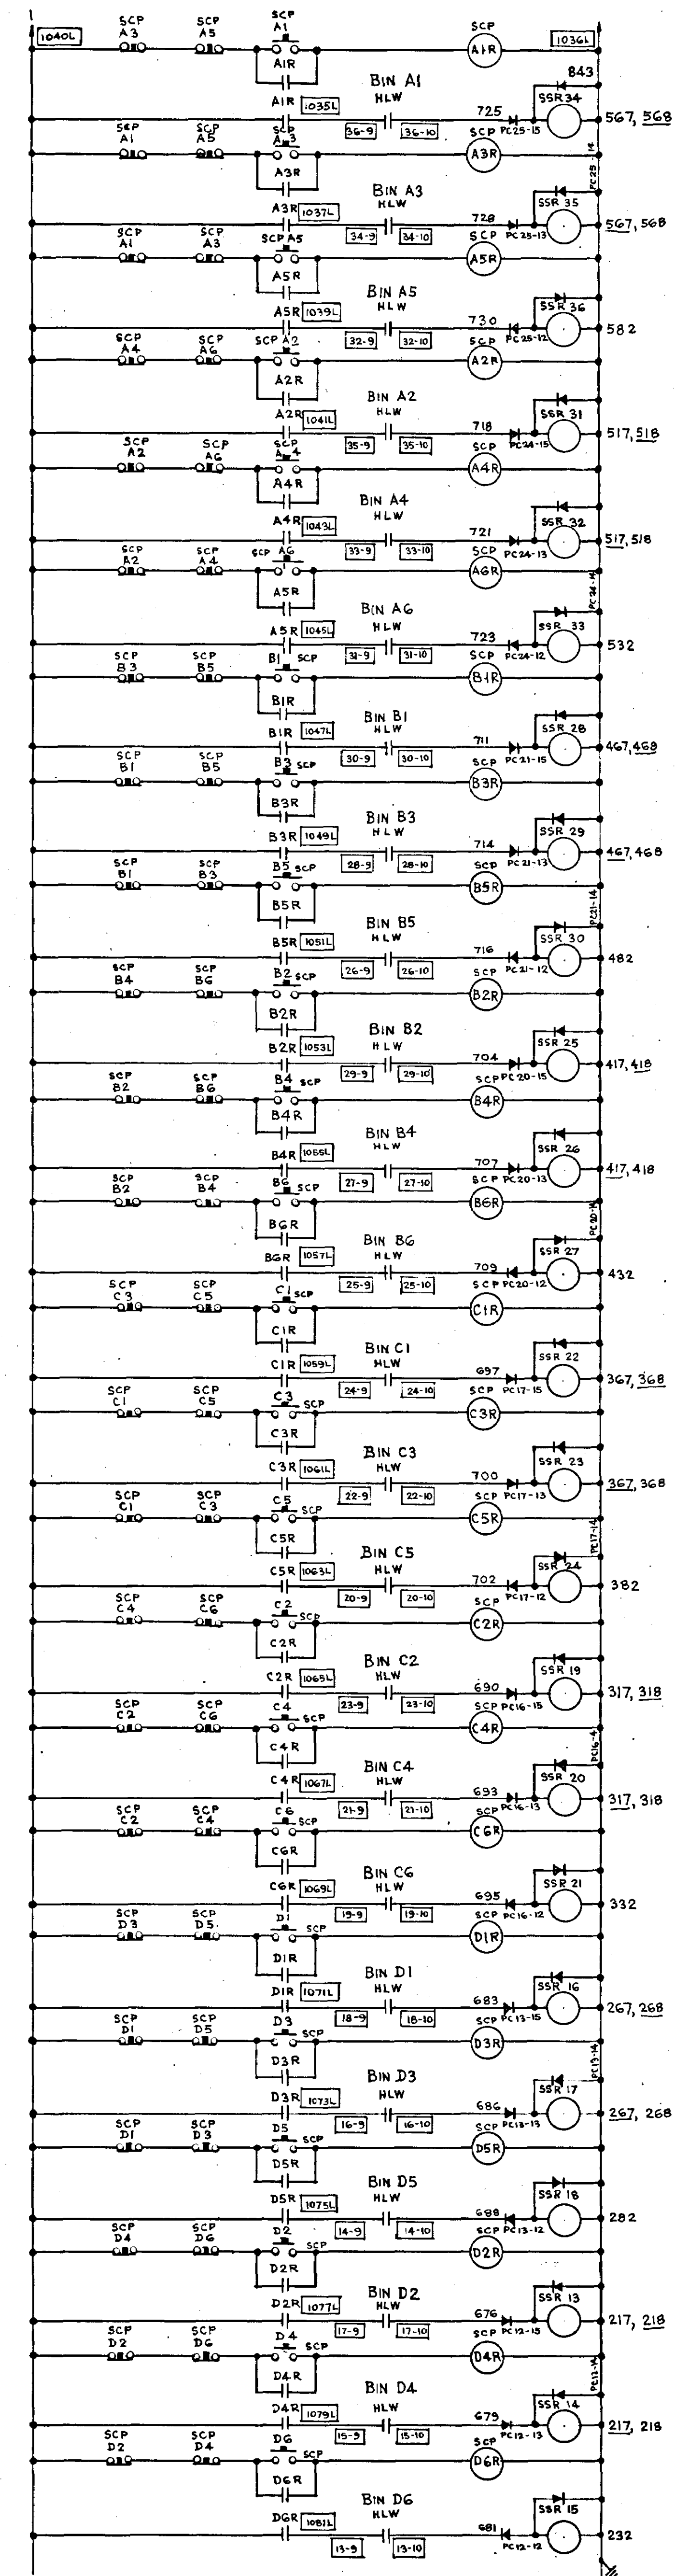

TERMINALS SHOWN THUS '9-8' ARE IN 'LCC's
" " " D18 " ON SCALES

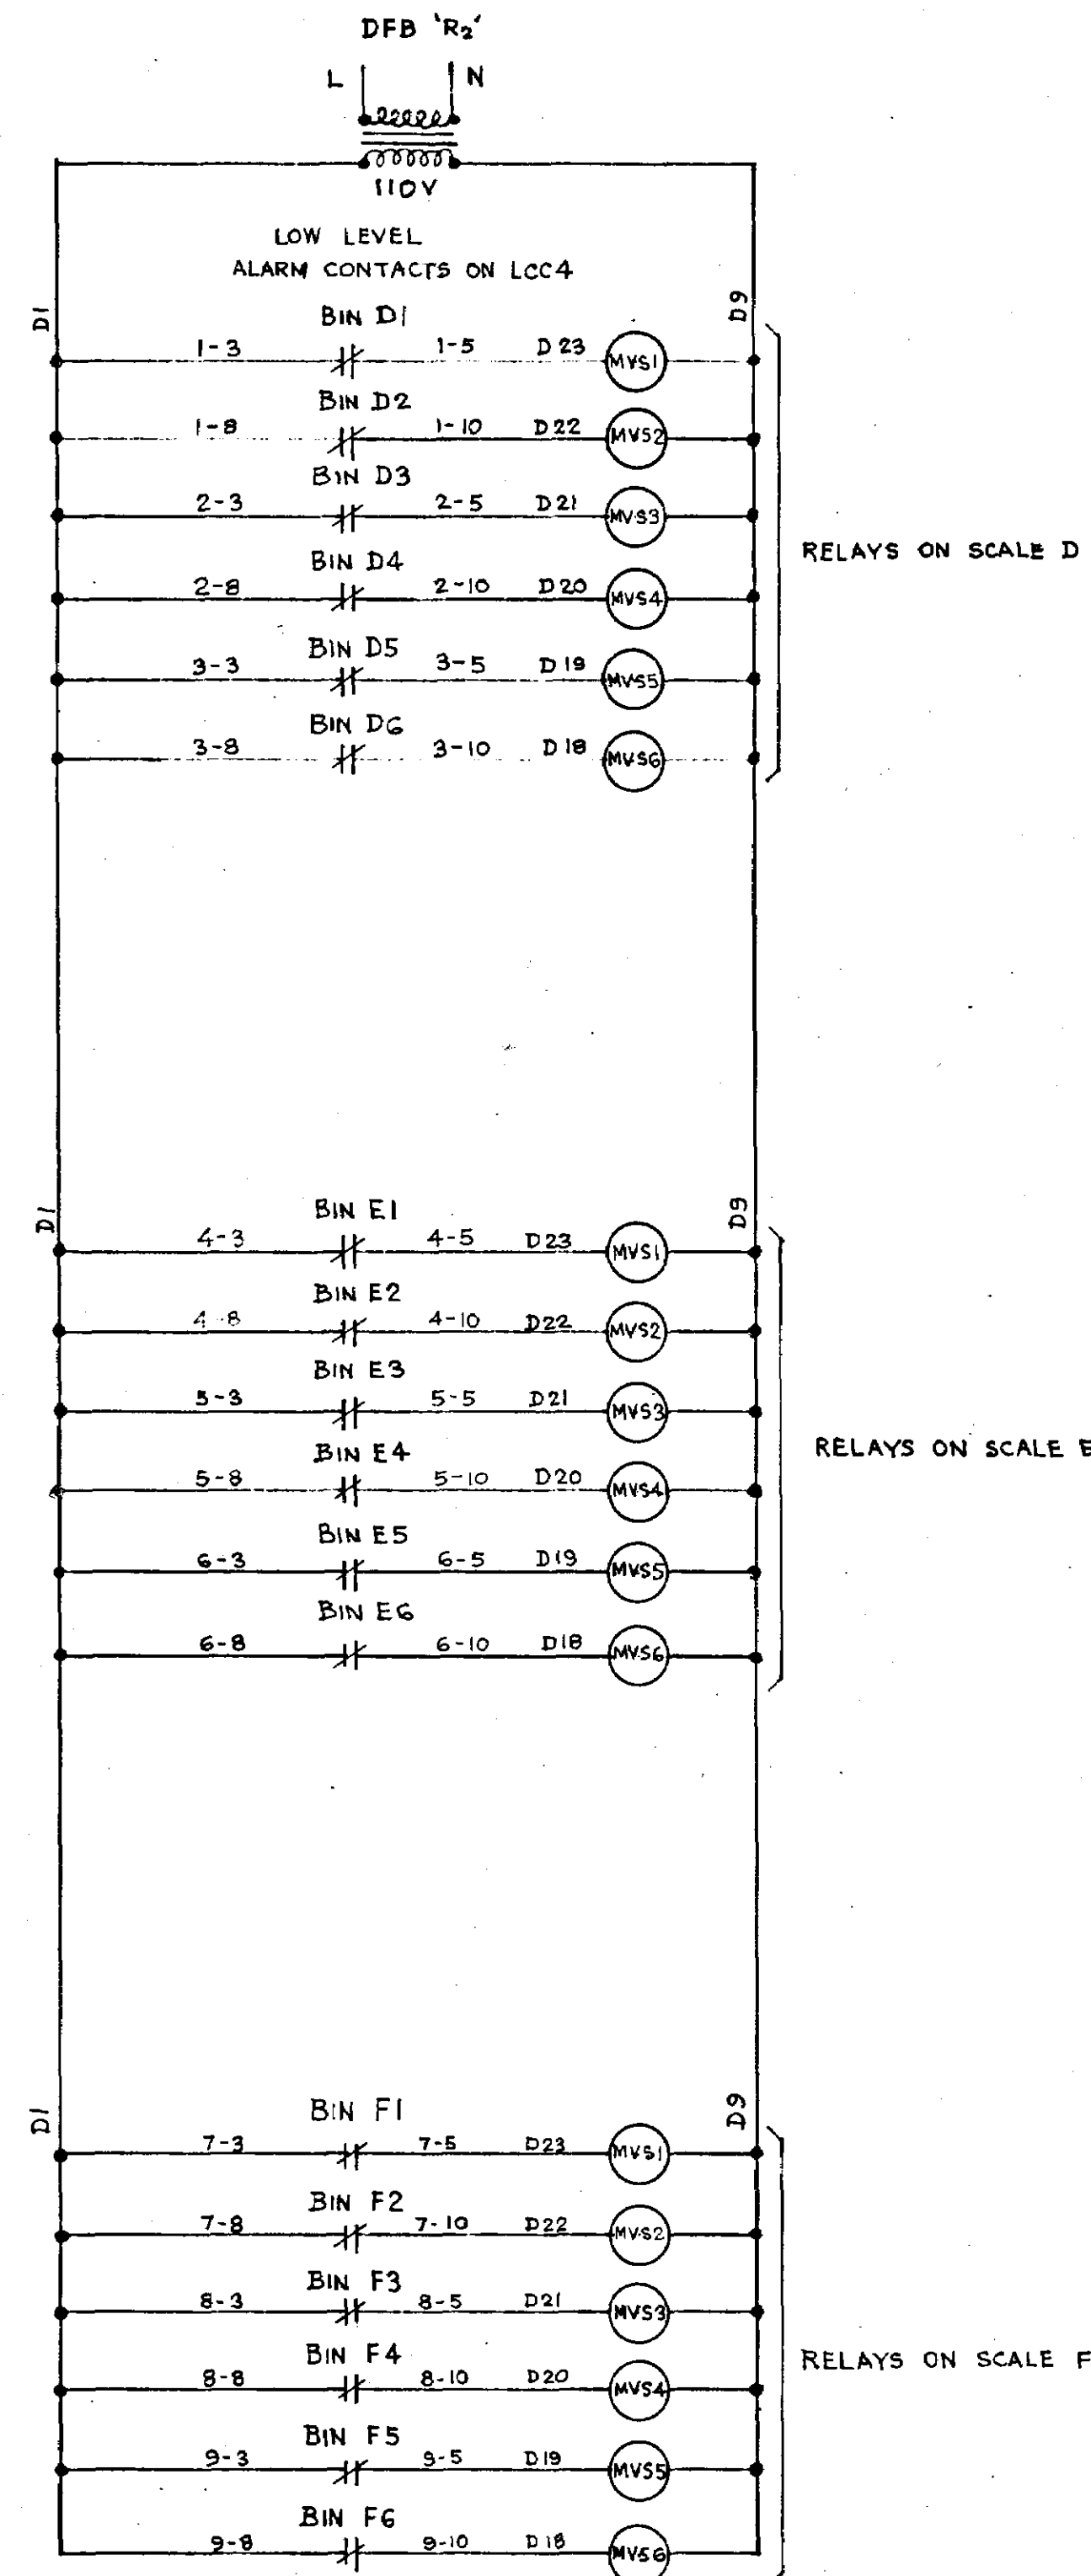

10725

SCHEME FOR MCC 5B -SEAFORTH GRAIN TERMINAL

THE DESIGN AND MANUFACTURING INFORMATION CONTAINED IN THIS DRAWING IS THE EXCLUSIVE RIGHT OF DEWHURST & PARTNER LTD. AND MUST NOT BE COPIED OR USED FOR MANUFACTURING PURPOSES.	ISSUE	<u>7</u>	3																
	DTX 361 AC/6																		

DTX 361 AC/6

DEWHURST & PARTNER LTD.

MELBOURNE WORKS

HOUNSLOW

TITLE

SCHEME FOR MCC 5B - SEAFORTH GRAIN TERMINAL

REVISION:

ORIGIN:

REVISION:

ORIGIN:

REVISION: 3
LEVEL CONTROL CONTACTS
WERE SHOWN N/C &
BETWEEN TERMS 11 & 12
ORIGIN: I.C.D.
20/11/72 SGD J.S.

REVISION: 2
DESK SELECTION
WIRING ADDED
(FROM SHEET 5)
ORIGIN: I.C.D.
14/7/77. SGD JS.

REVISION: 1	DRAWN
REDRAWN	DATE
	CHECK
ORIGIN: I.C.D.	APPROV
6/4/72 SCD. JS.	DATE

KEY DIAG. No.	—
EXT. DIAG. No.	STX 361 AC
REL. DIAG. No.	—
PANEL LAYOUT No.	HTX 361 AC