

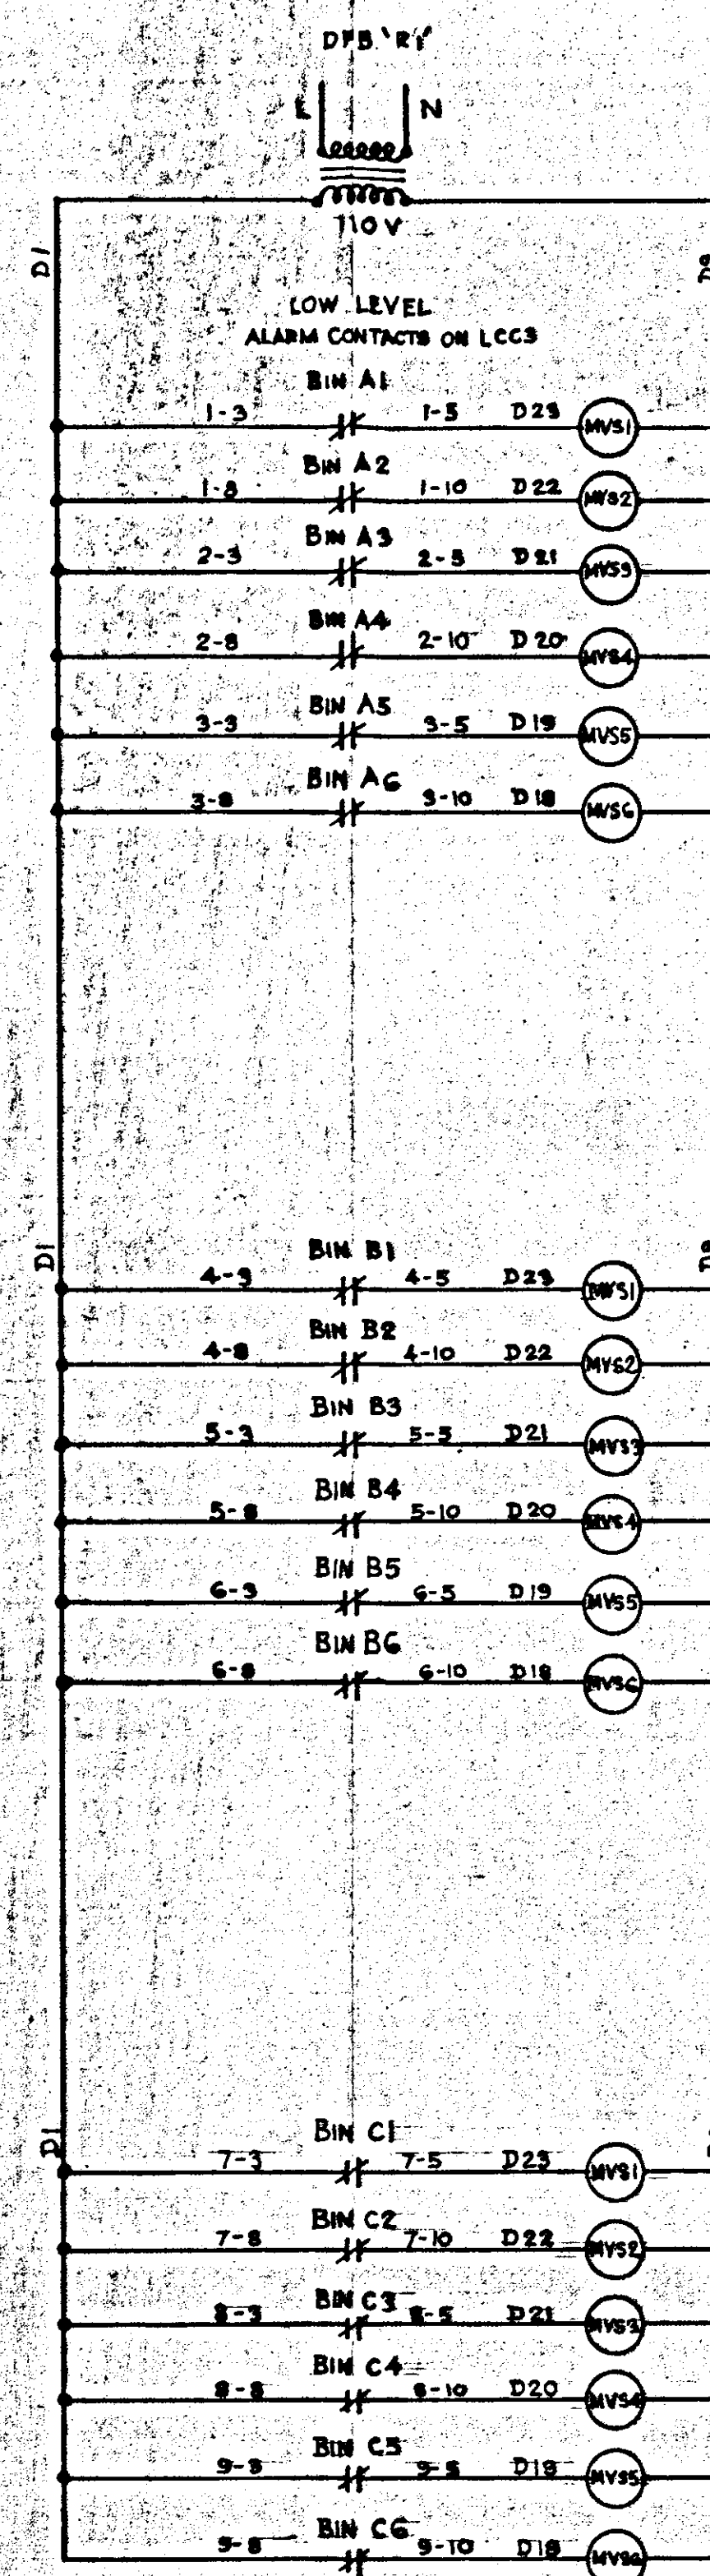
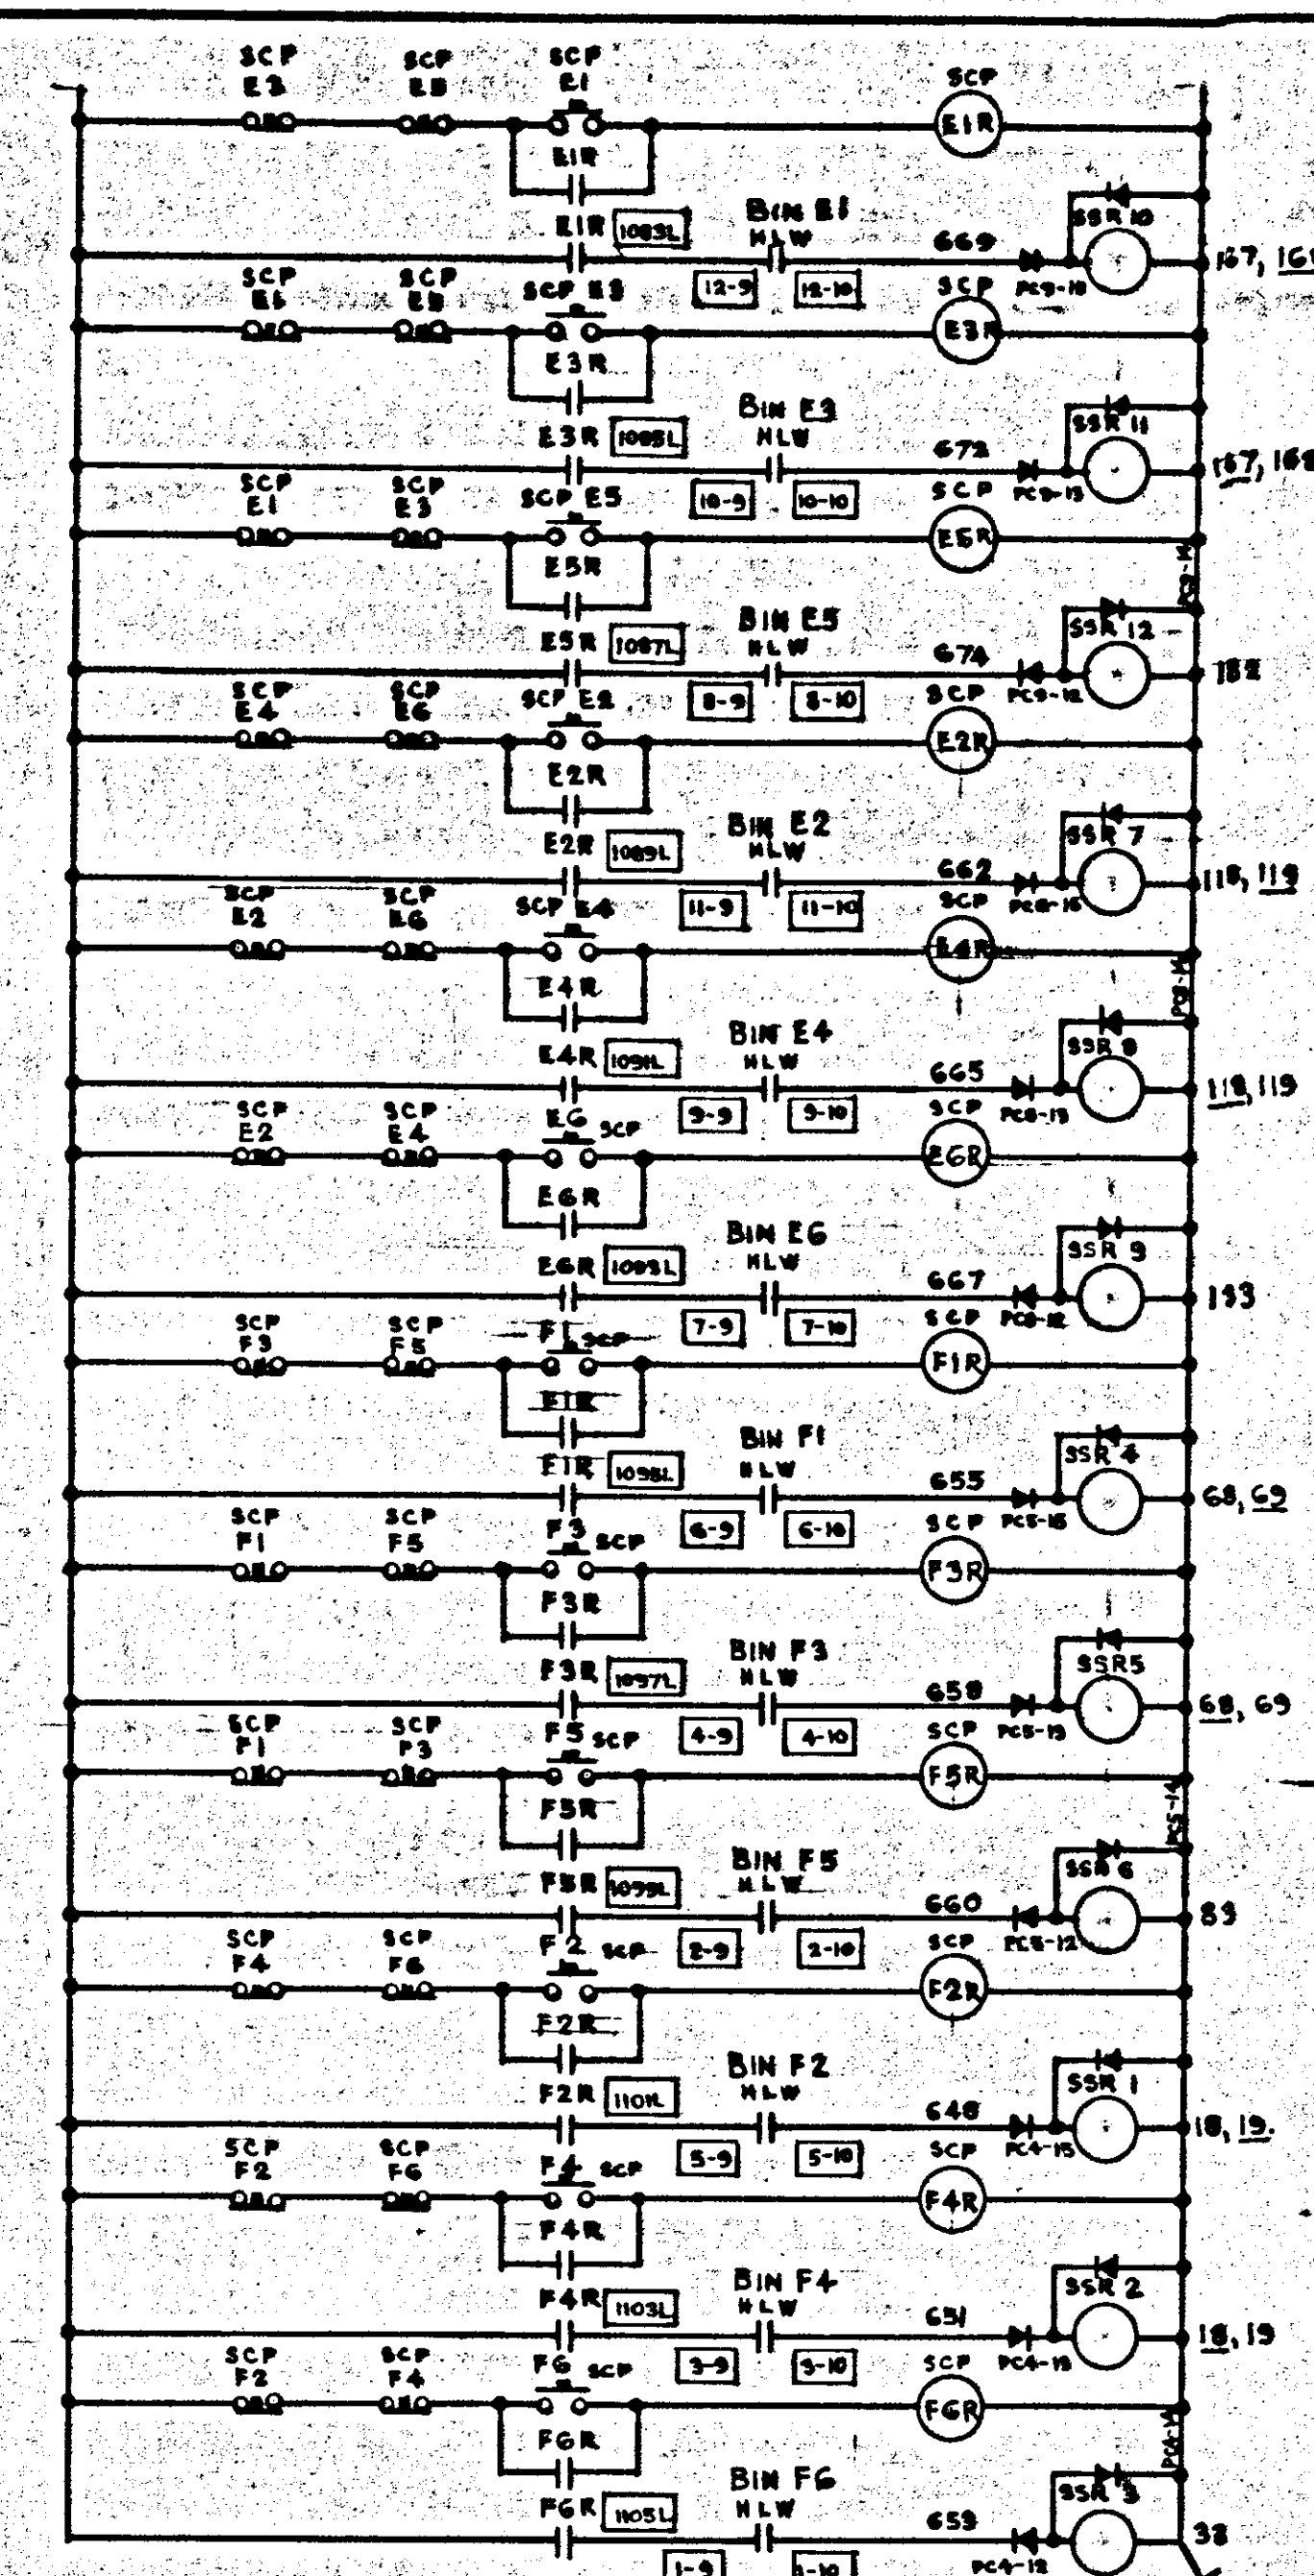


10725

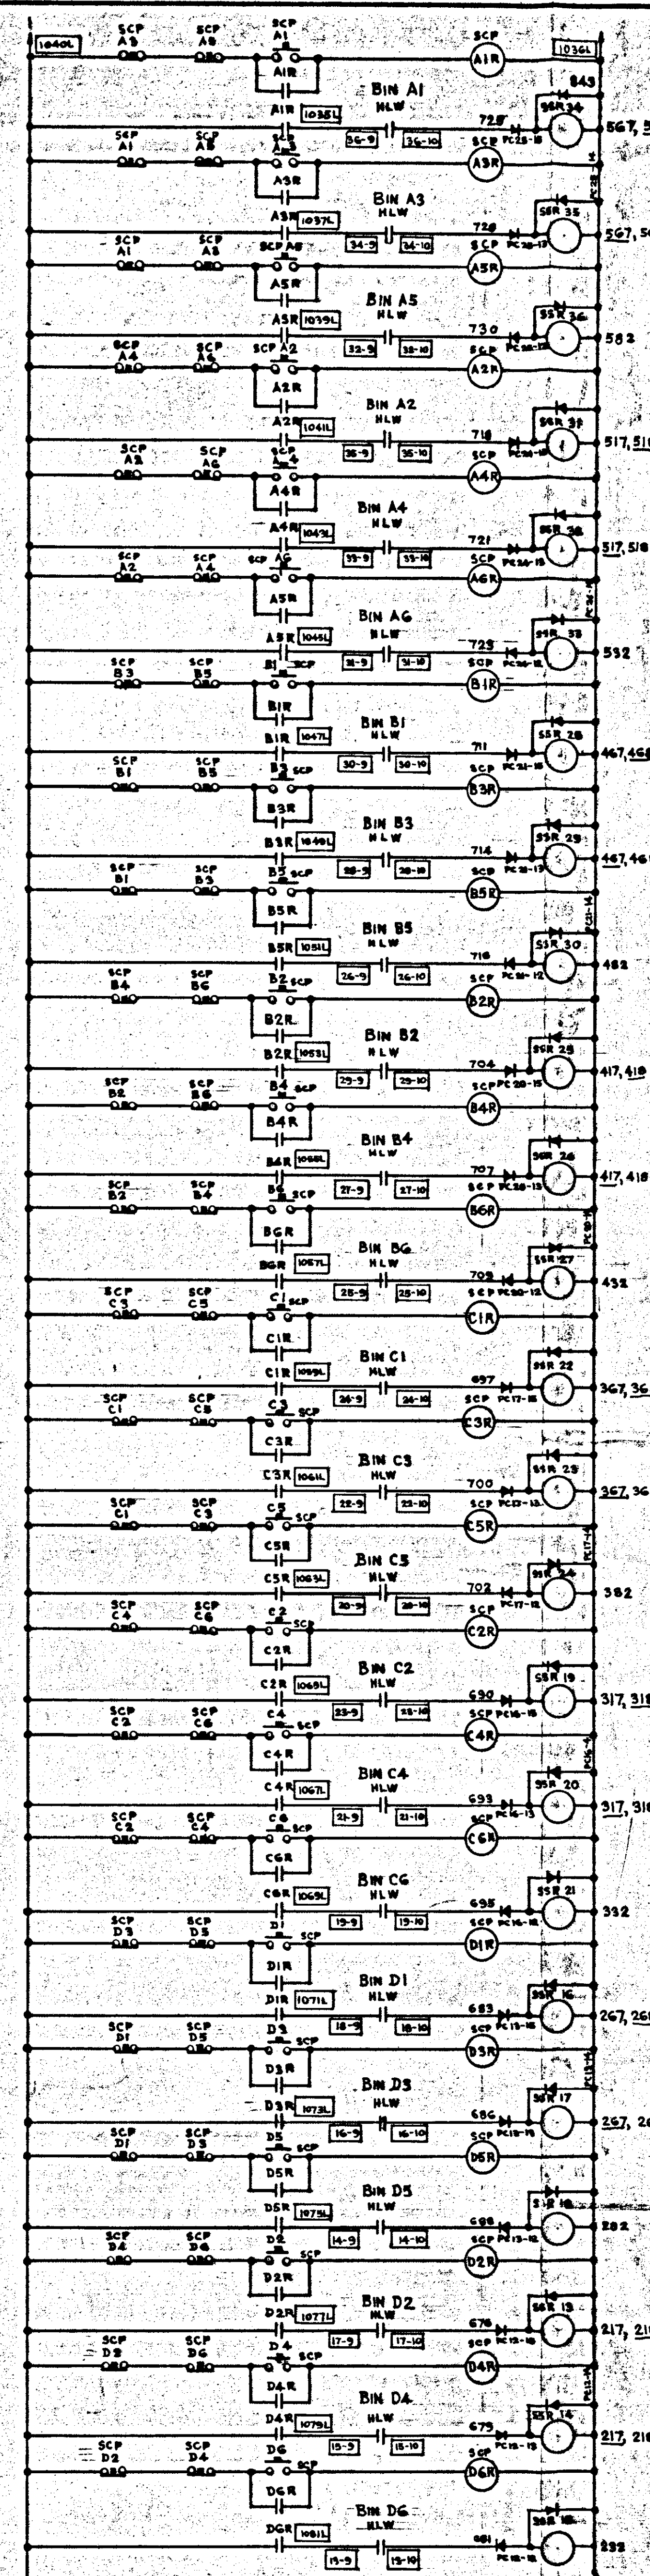

TERMINALS SHOWN THUS '9-8' ARE IN 'LCC's
" " " DIS " ON SCALES

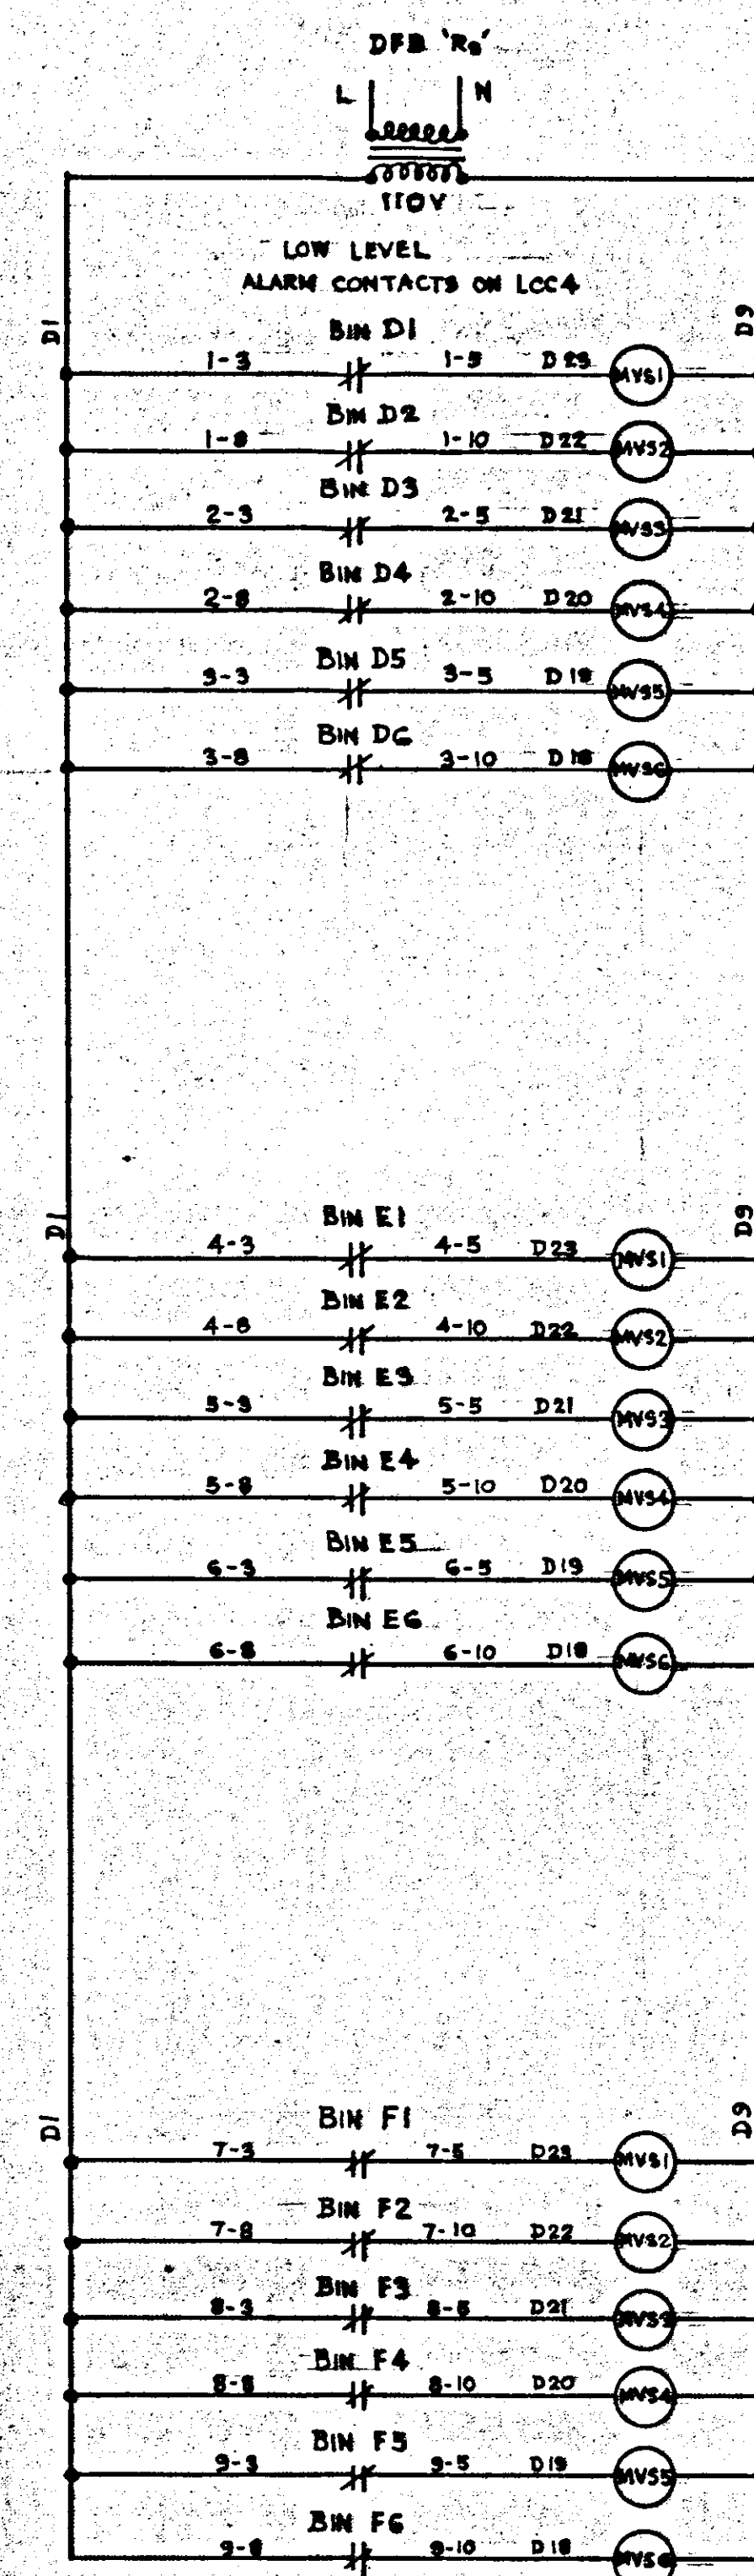

10725

DEWHURST & PARTNER LTD.

MELBOURNE WORKS HOUNSLOW

TITLE

SCHEME FOR MCC 5B - SEAFORTH GRAIN TERMINAL

REVISION:

ORIGIN:

REVISION

ORIGIN:

REVISION: 3
LEVEL CONTROL CONTACT
WERE SHOWN N/C &
BETWEEN TERMS 11 &
ORIGIN: I. C. D.
20/11/72 SGD J.S.

REVISION: 2
DESK SELECTION
WIRING ADDED
(FROM SHEETS)
ORIGIN: E.C.D.
14/7/77 SGD

REVISION: 1
REDRAWN: 4

ORIGIN: I.C.I.
6/4/72 SGD. JS

DRAWN BY	BJC
DATE	2.3
CHECKED BY	
APPROVED BY	
DATE	

SCHEME FOR MCC 5B - SEAFORTH GRAIN TERMINAL

[illegible]

DTX 361 AC/6

DTX 361 AC/6