
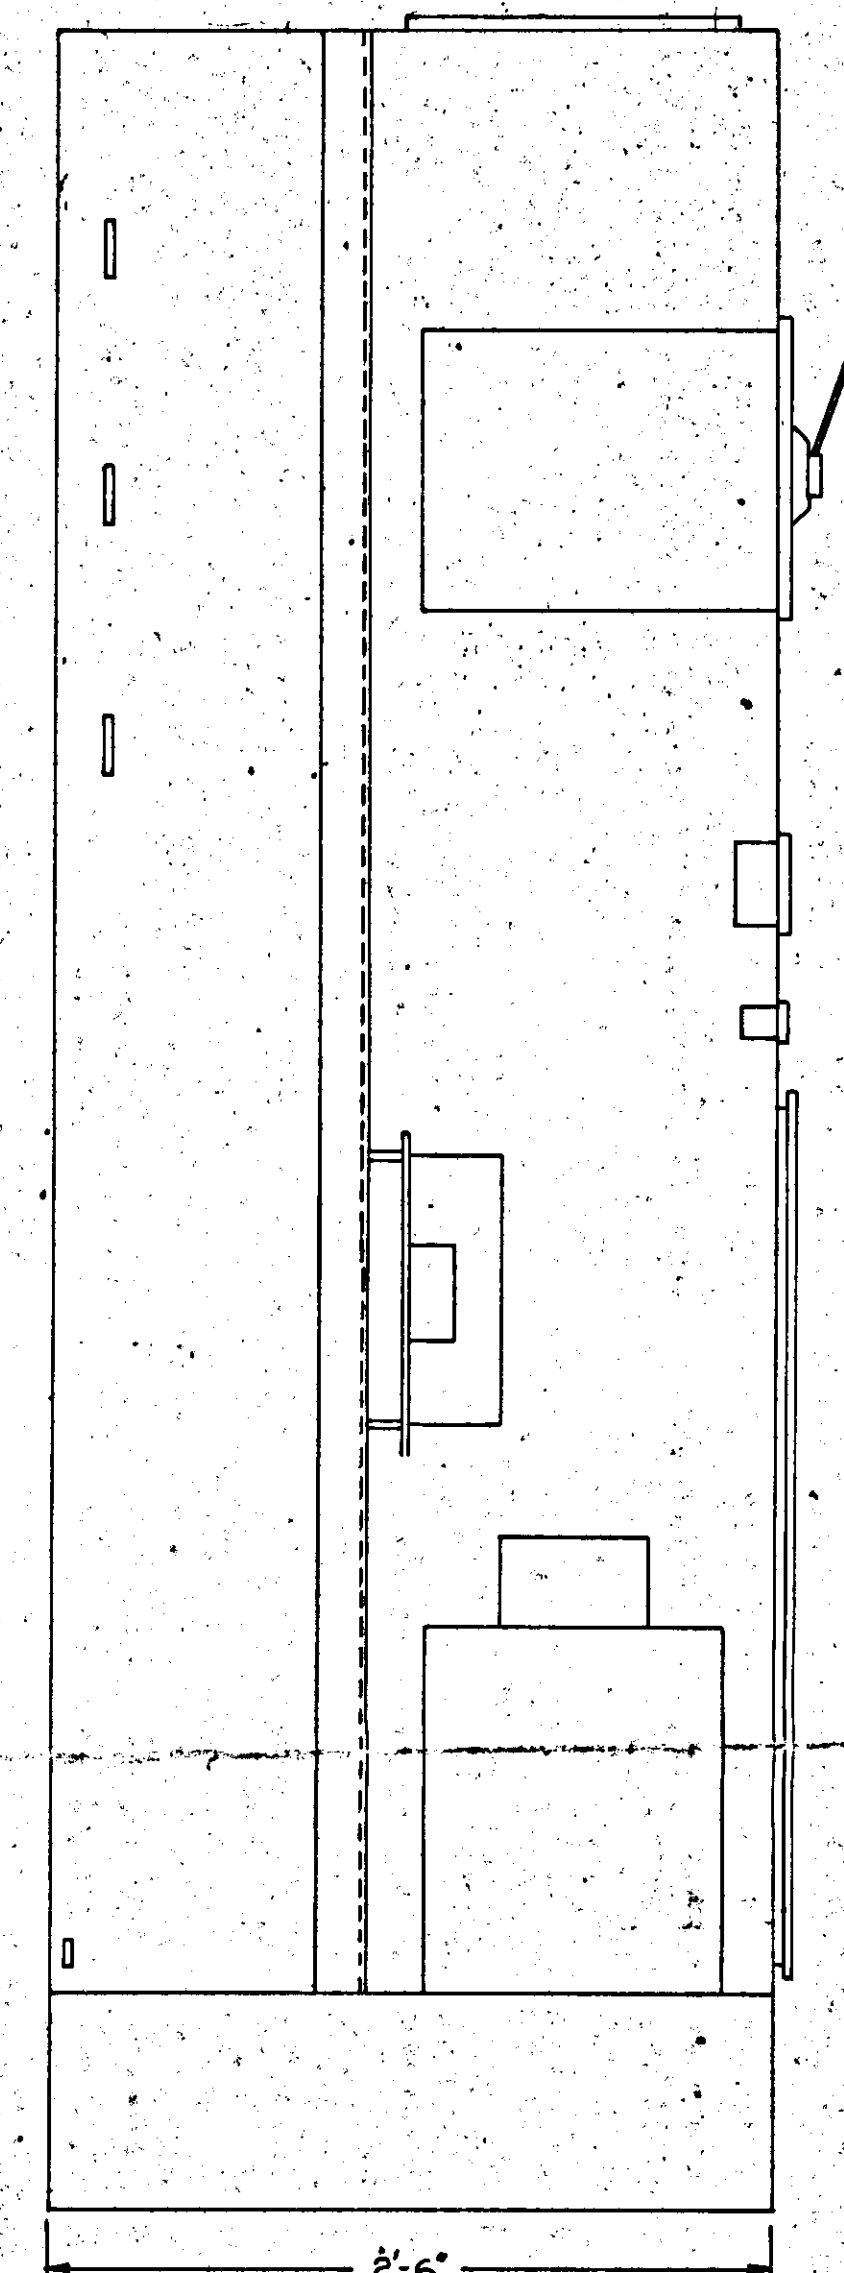
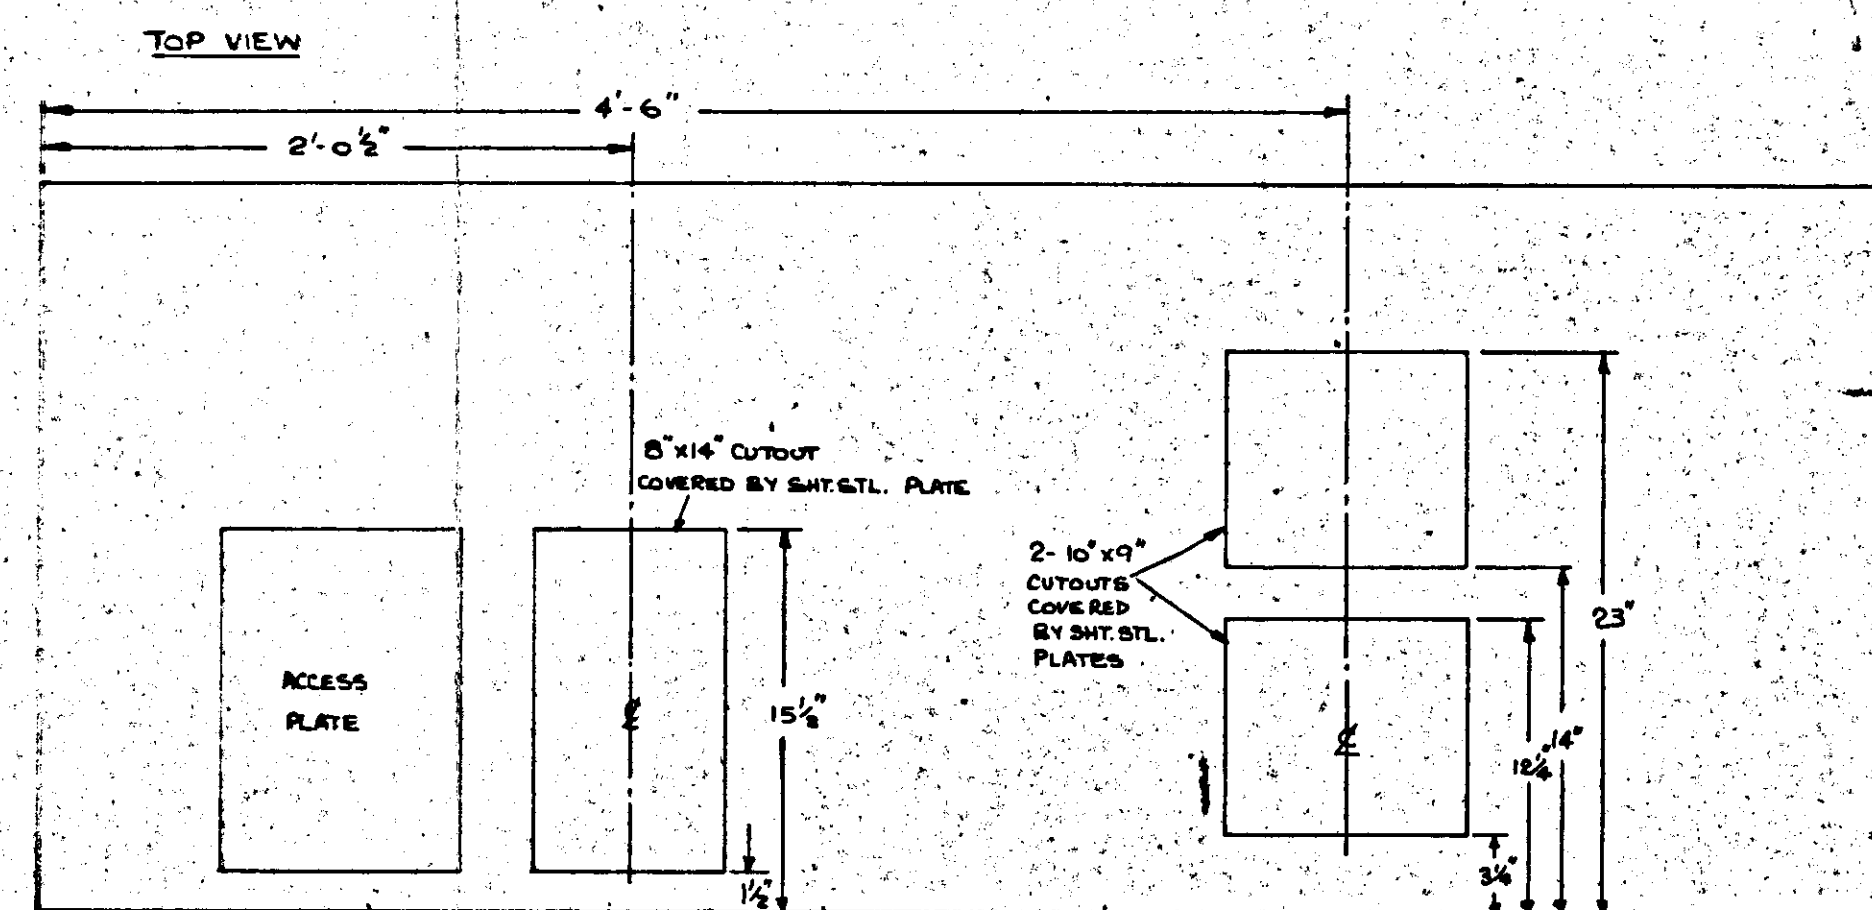
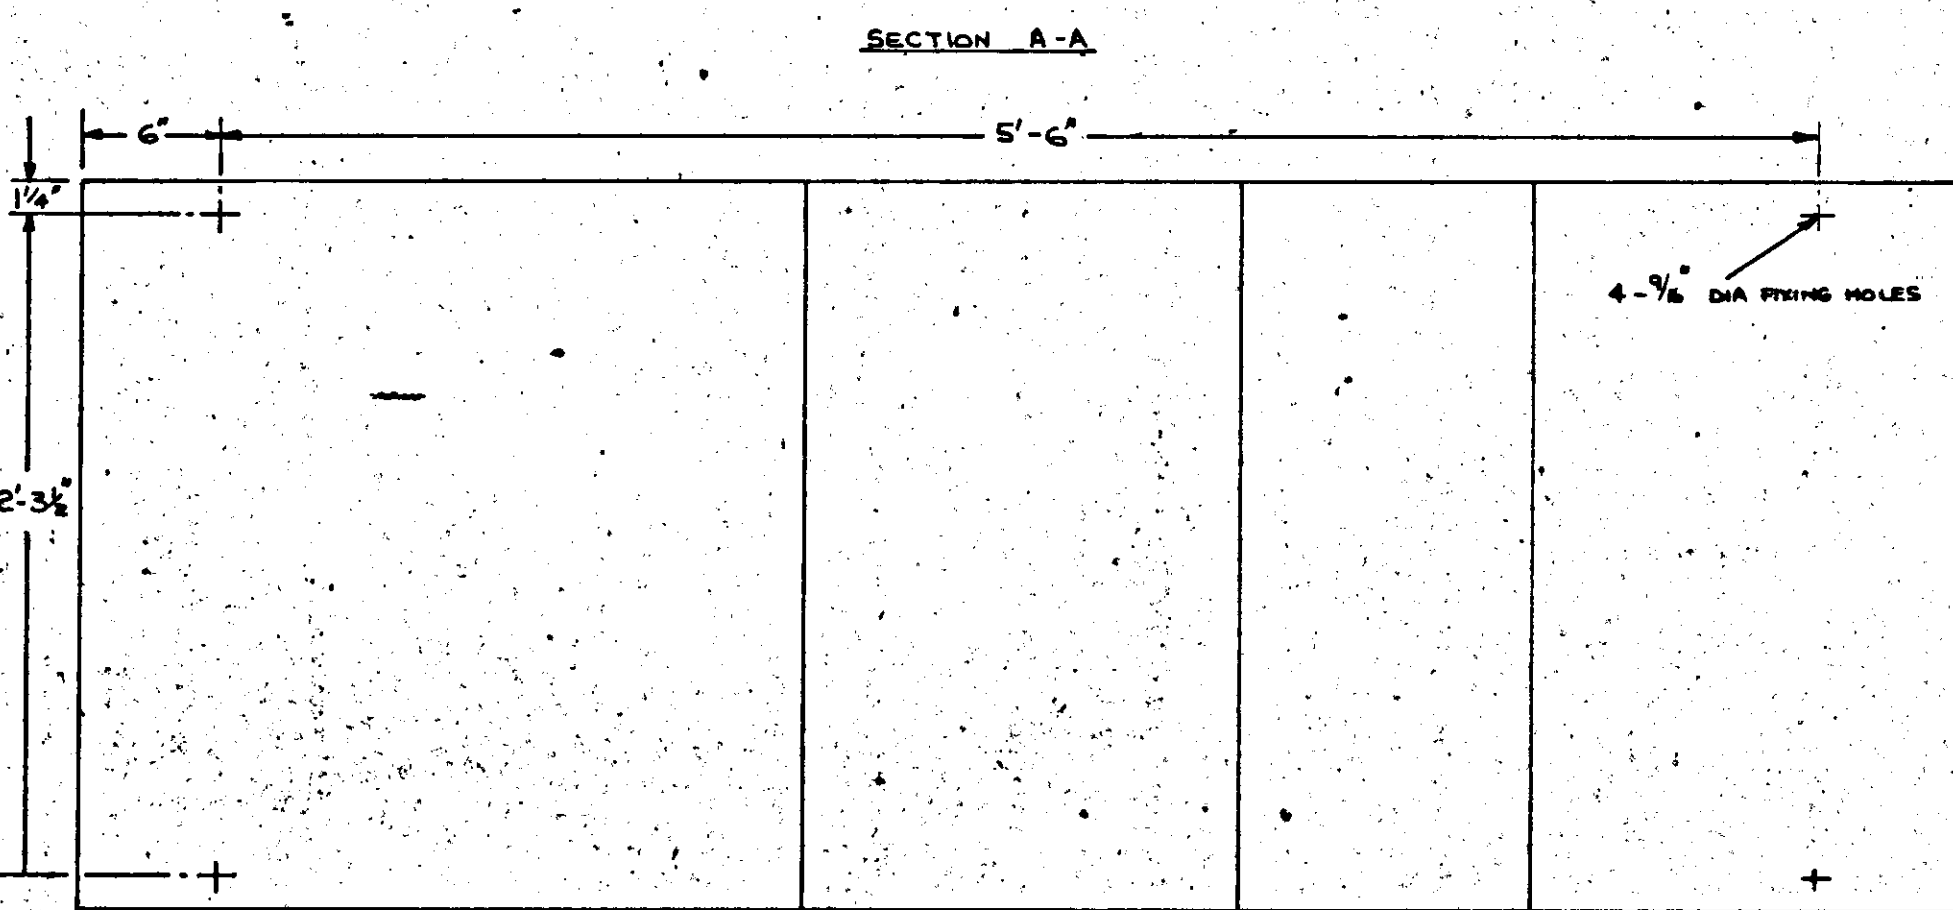


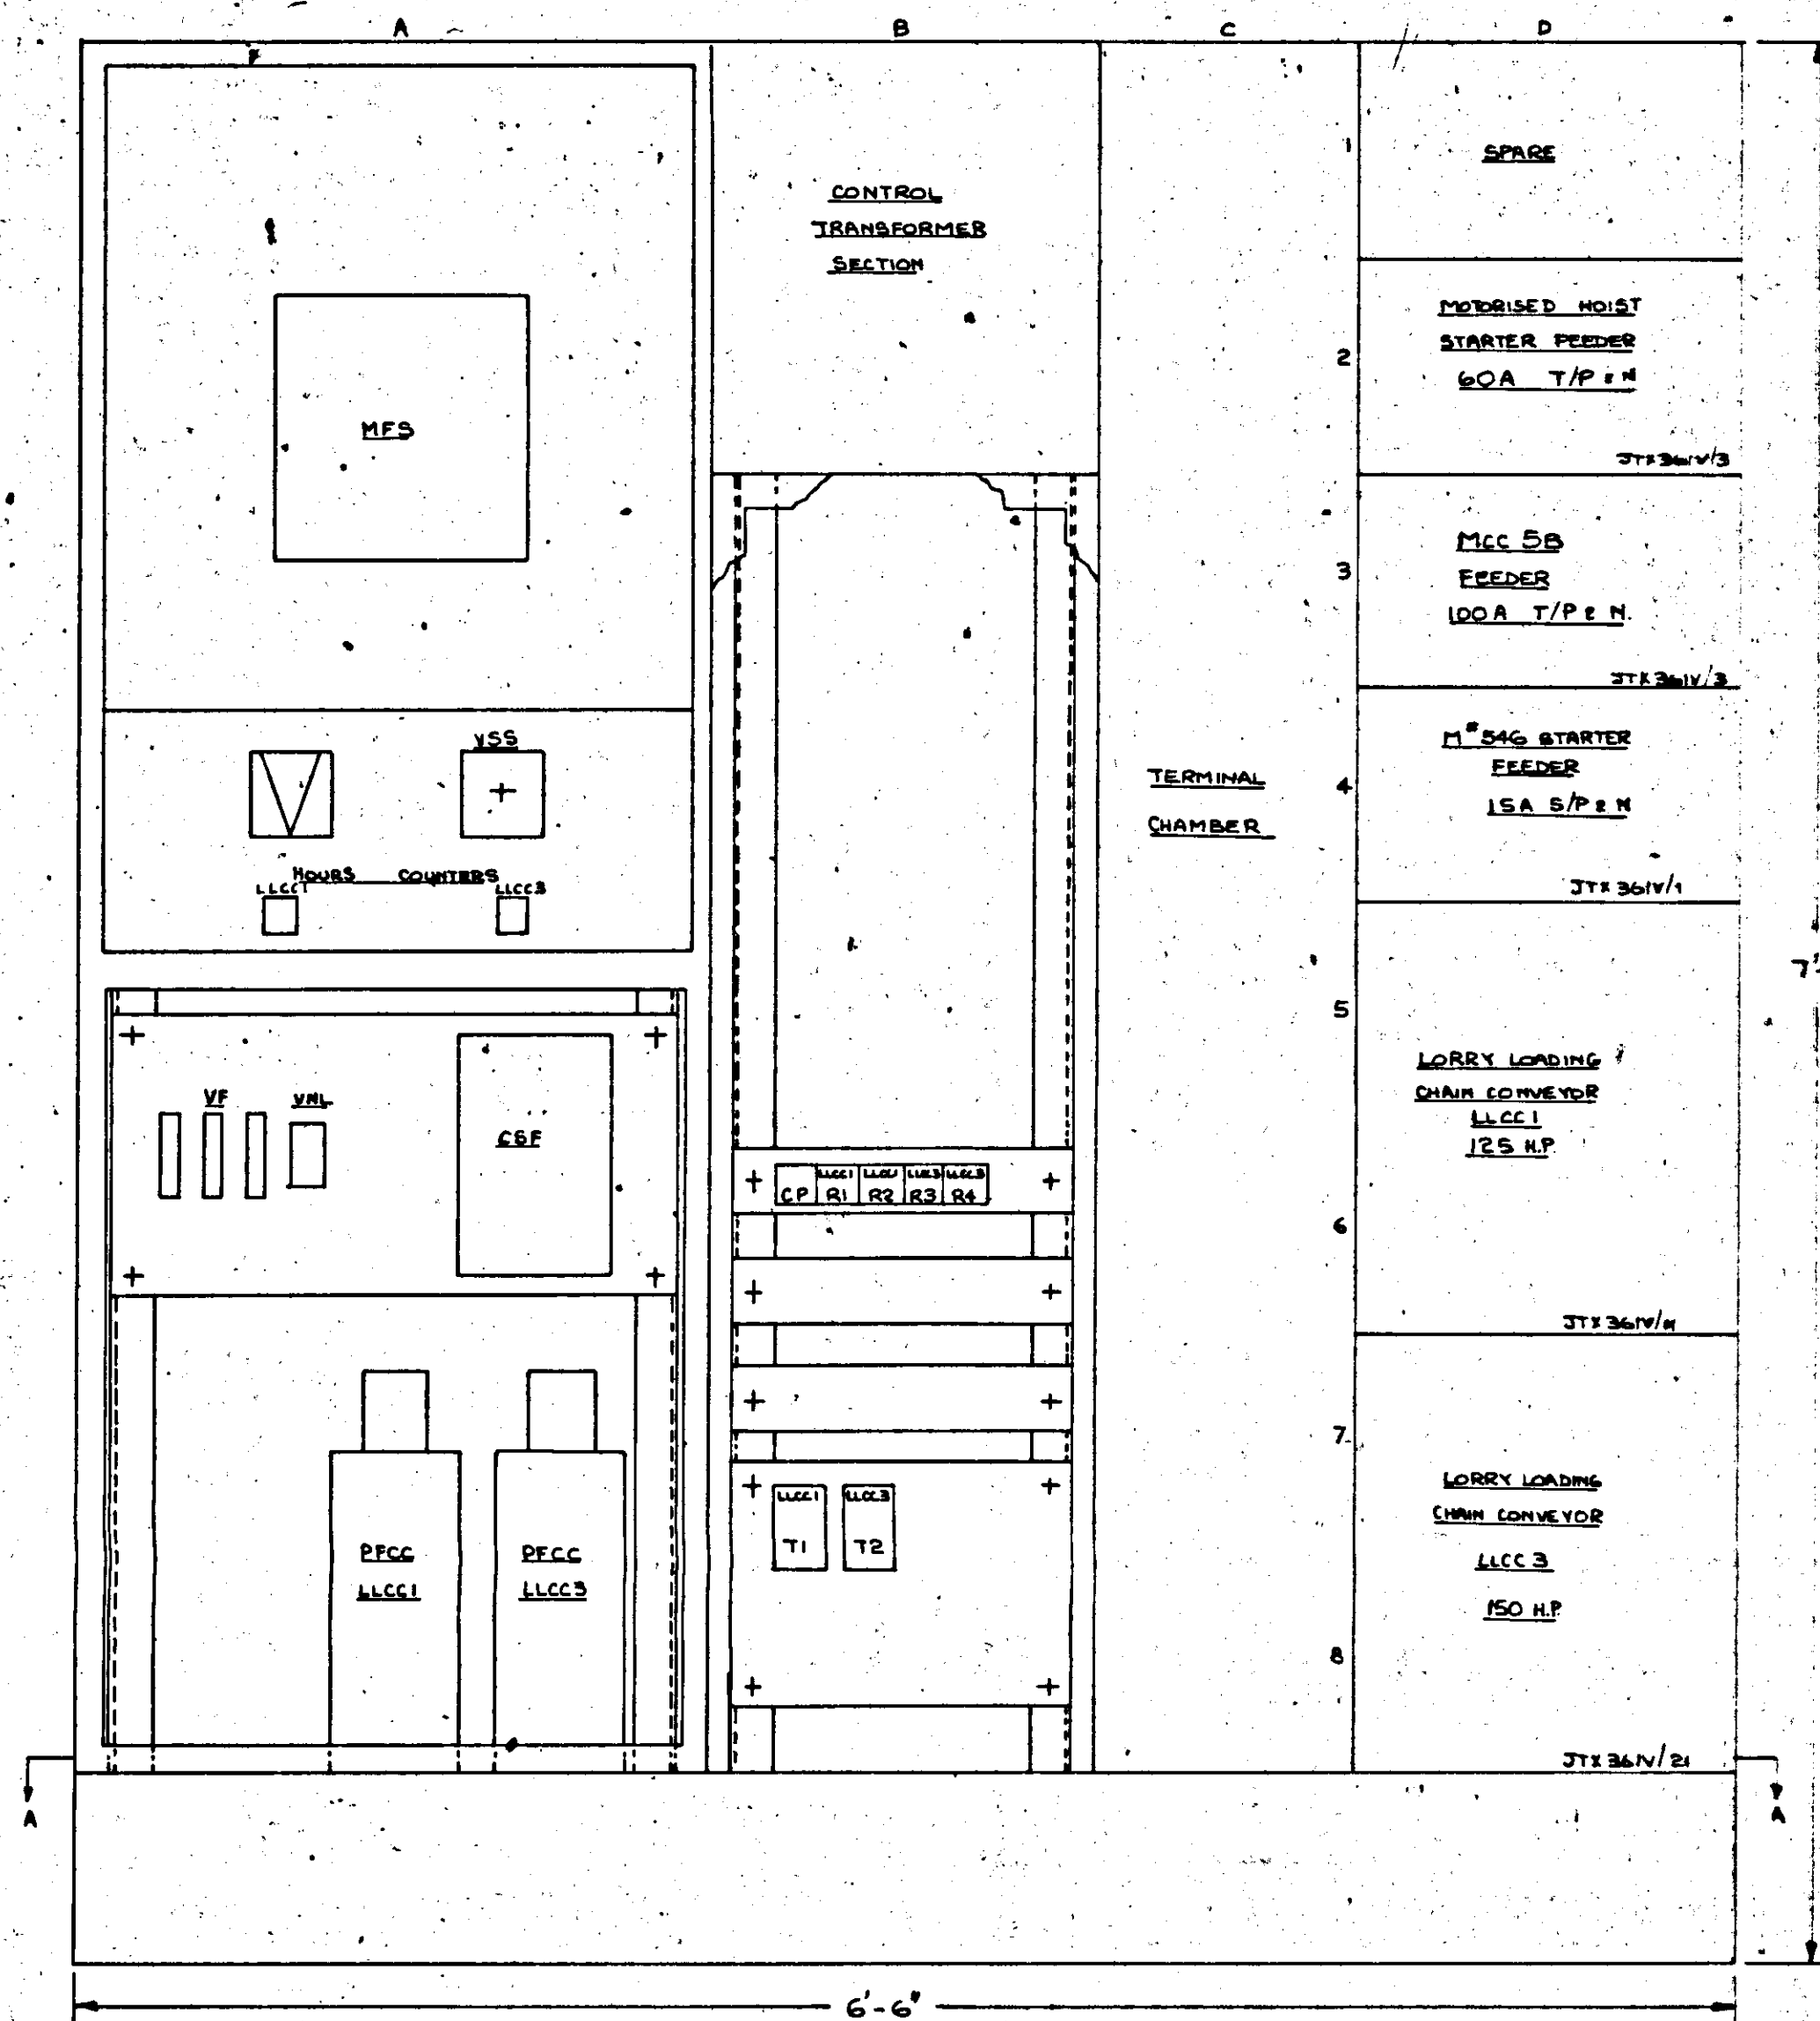

LAYOUT FOR MCC 5A
SEAFORTH GRAIN TERMINAL

THE DESIGN AND MANUFACTURING INFORMATION CONTAINED IN THIS DRAWING IS THE EXCLUSIVE RIGHT OF DEWHURST & PARTNER LTD. AND MUST NOT BE COPIED OR USED FOR MANUFACTURING PURPOSES.

ISSUE 12

GTX 361 AD

GTX 361 AD

DEWHURST & PARTNER LTD.
MELBOURNE WORKS - HOUNSLOW

TITLE
LAYOUT FOR MCC 5A - SEAFORTH GRAIN TERMINAL

REVISION
ORIGIN / / SGD

REVISION
ORIGIN / / SGD

REVISION 1
DATE 19/2/71
DIA. NOS. ADDED
ORIGIN R.M.P.
W/S / 71 SGD J.T.

DRAWN BY J. Thomas
DATE 19/2/71
CHECKED BY
APPROVED BY
DATE

KEY DIAG. No. GTX 361 AD
EXT. DIAG. No. GTX 361 AD
REL. DIAG. No.
PANEL LAYOUT No.

35

35

35