

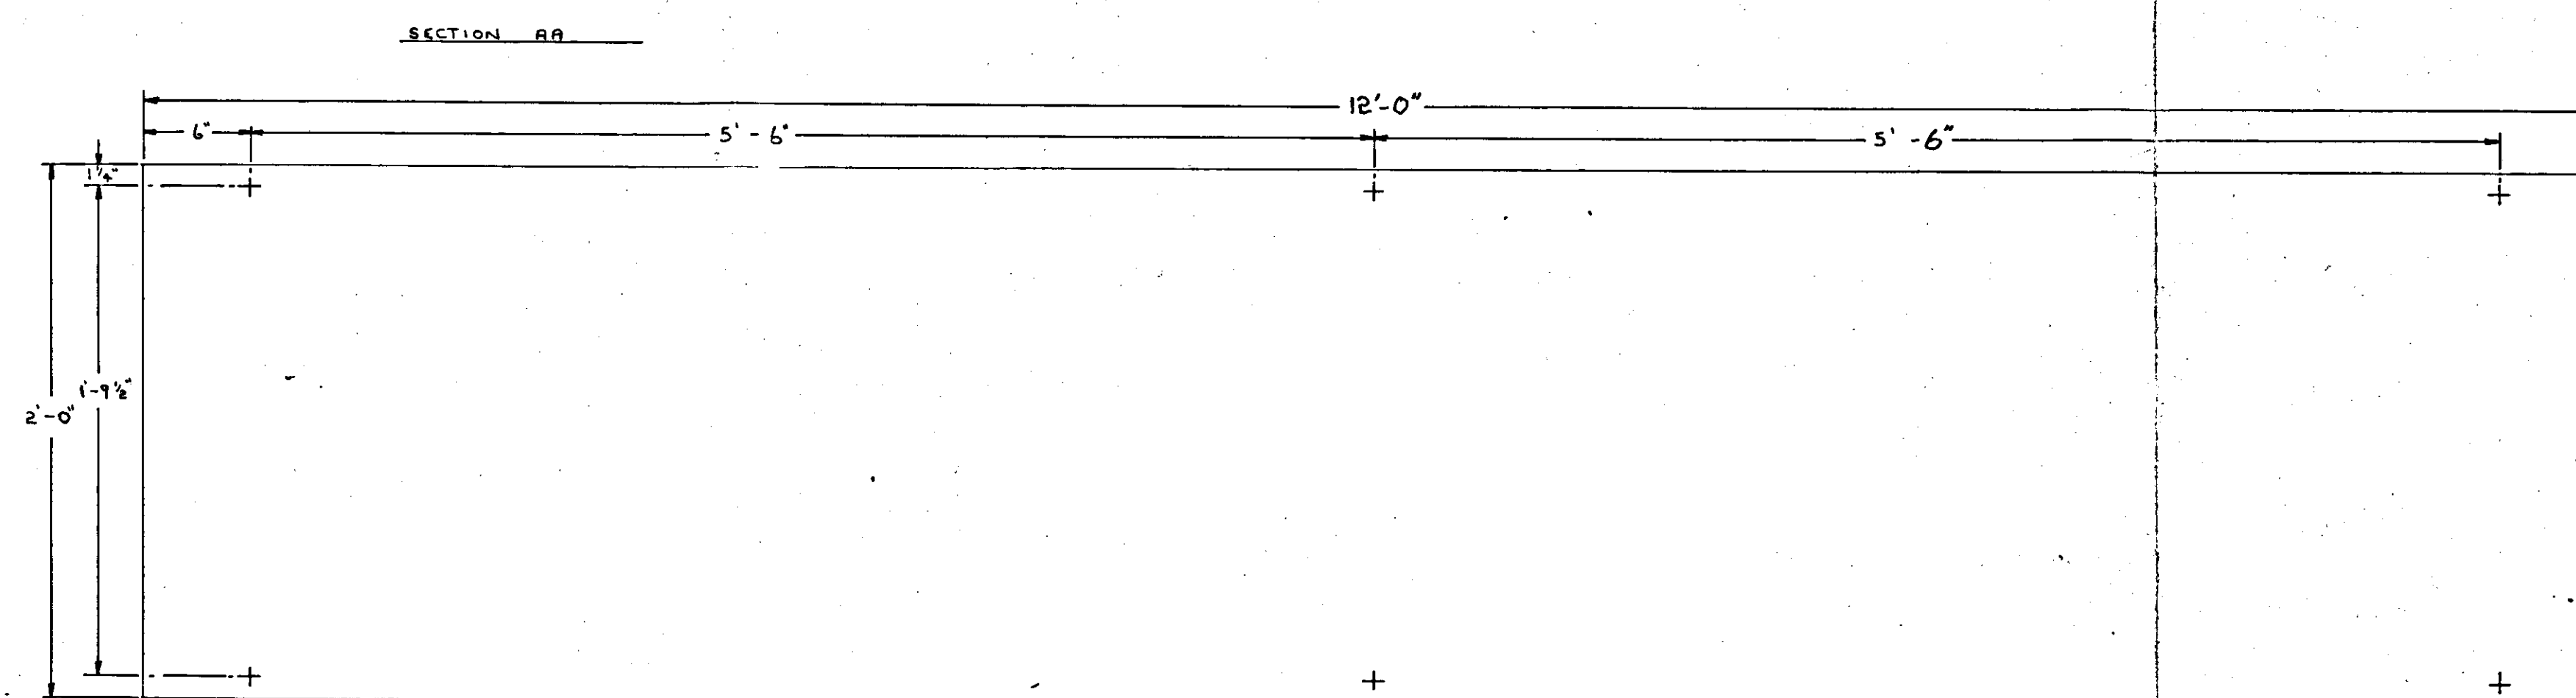
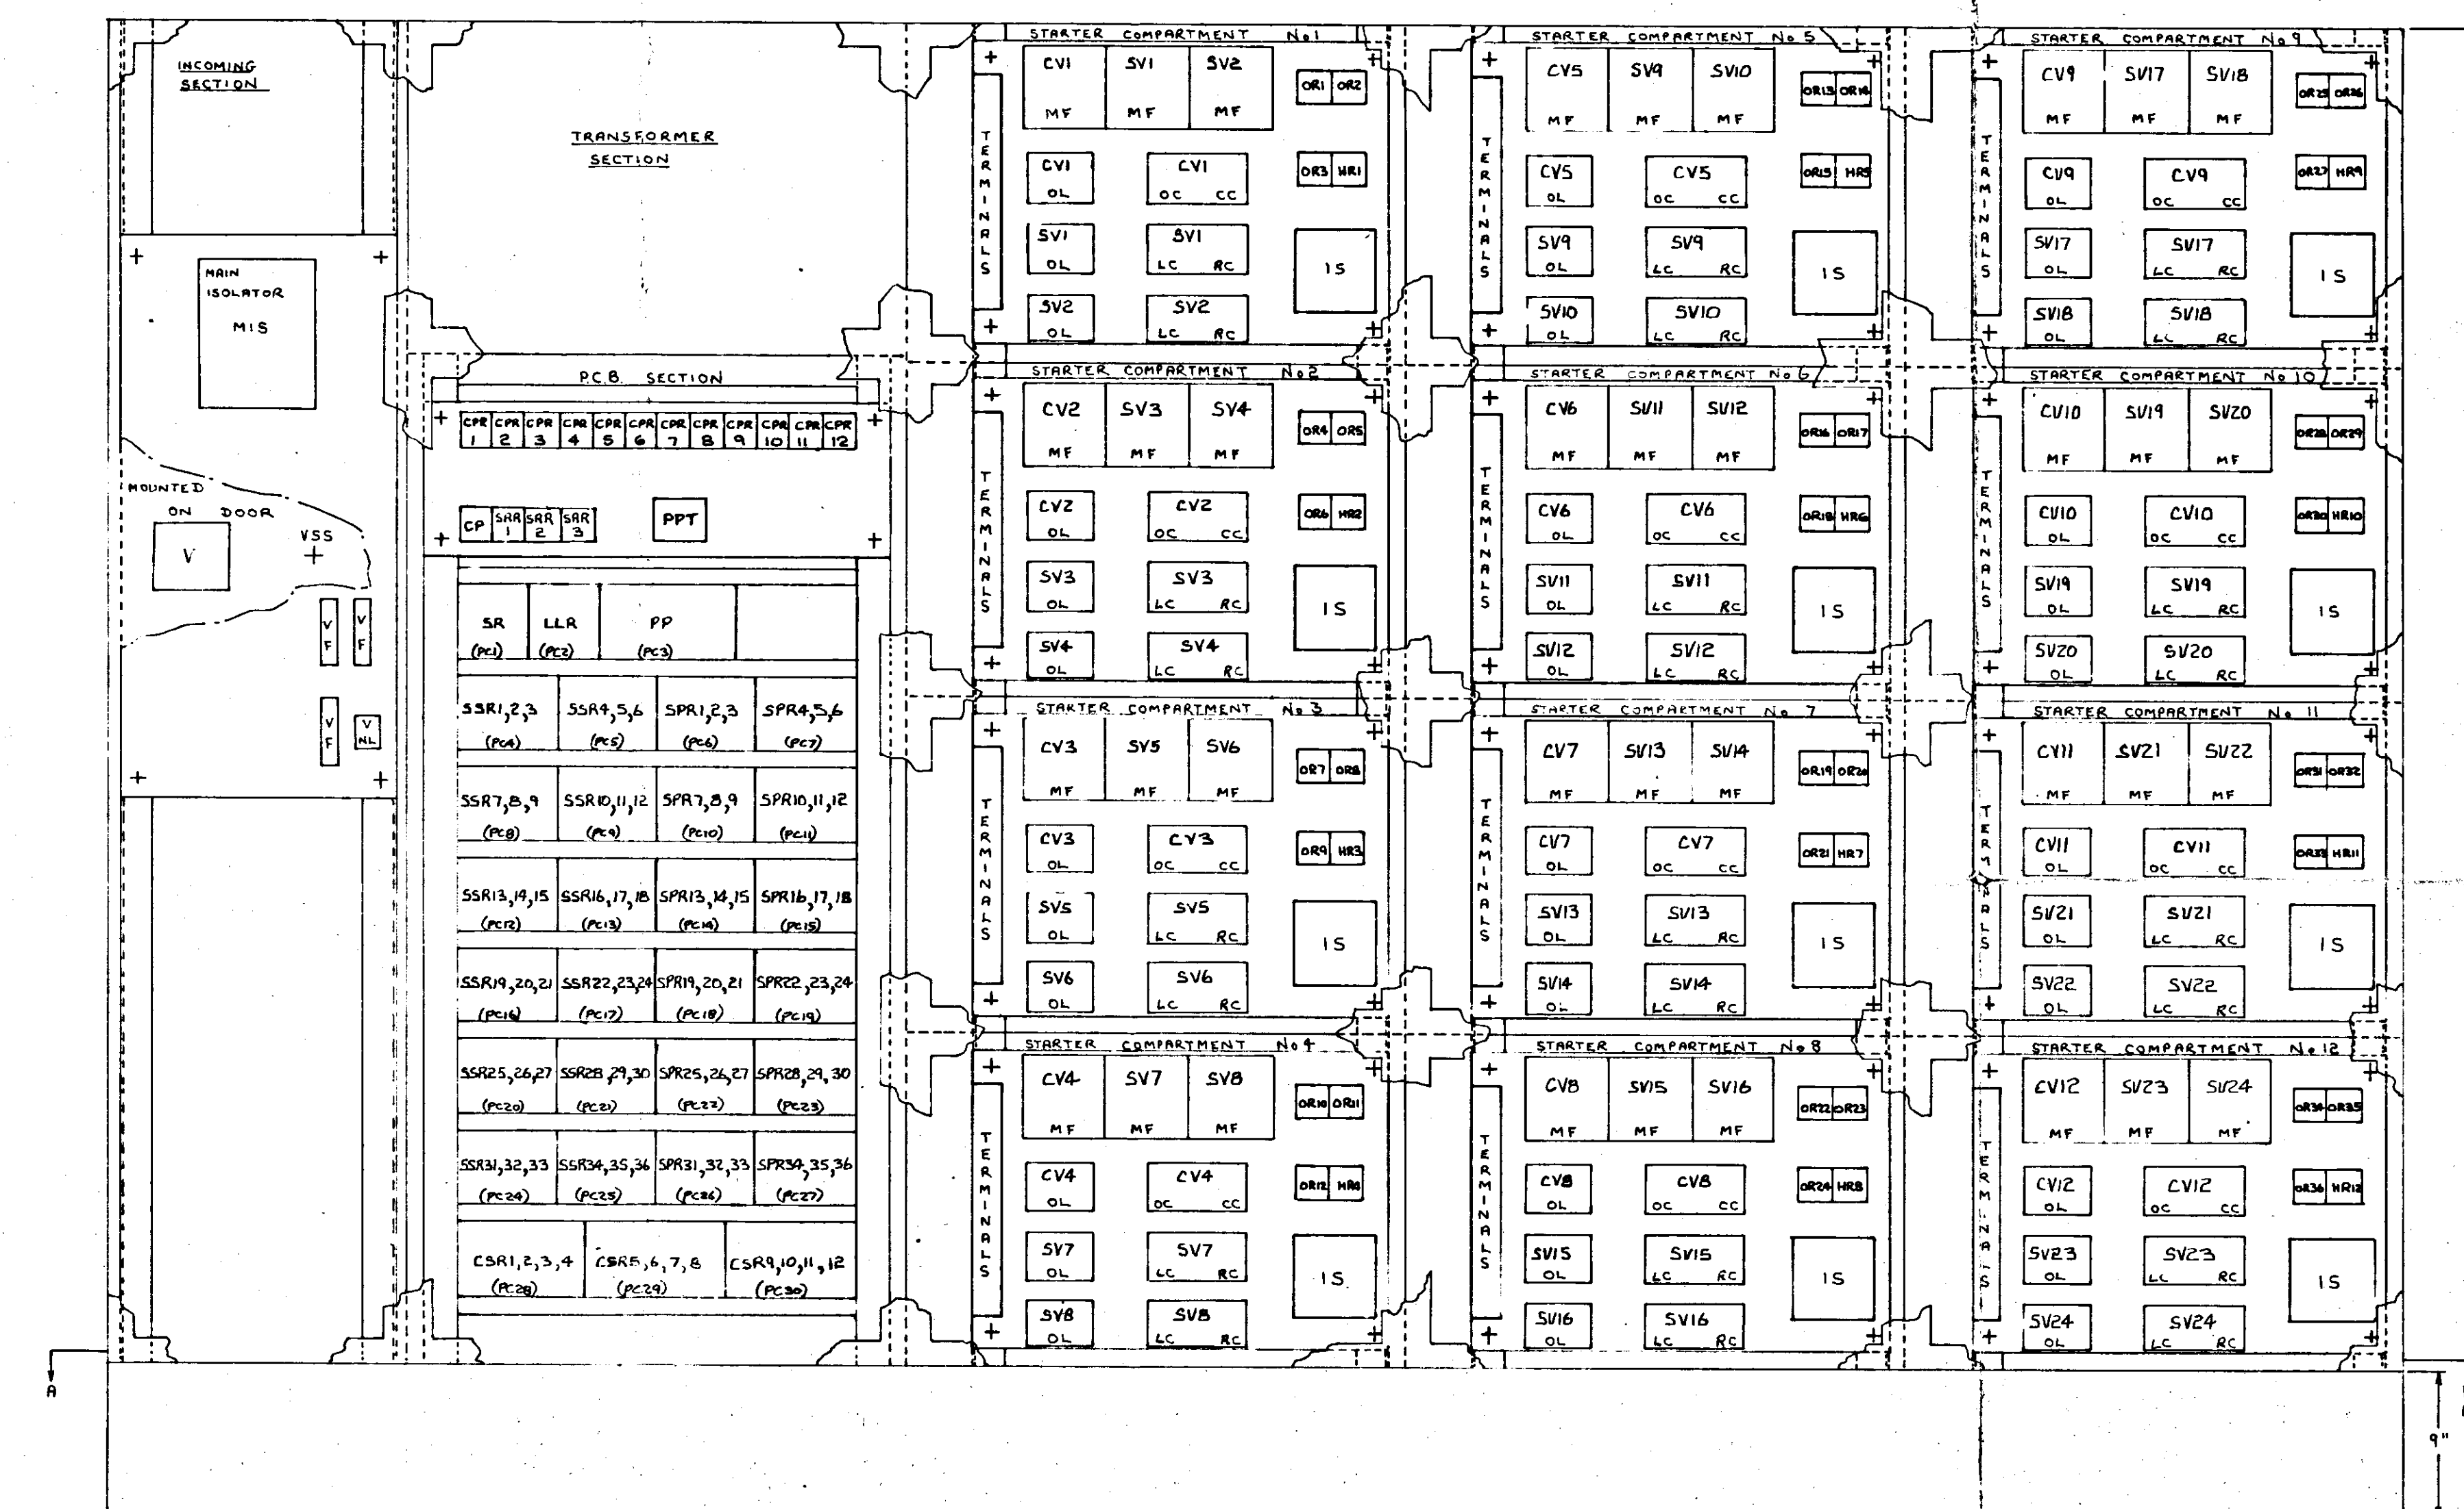


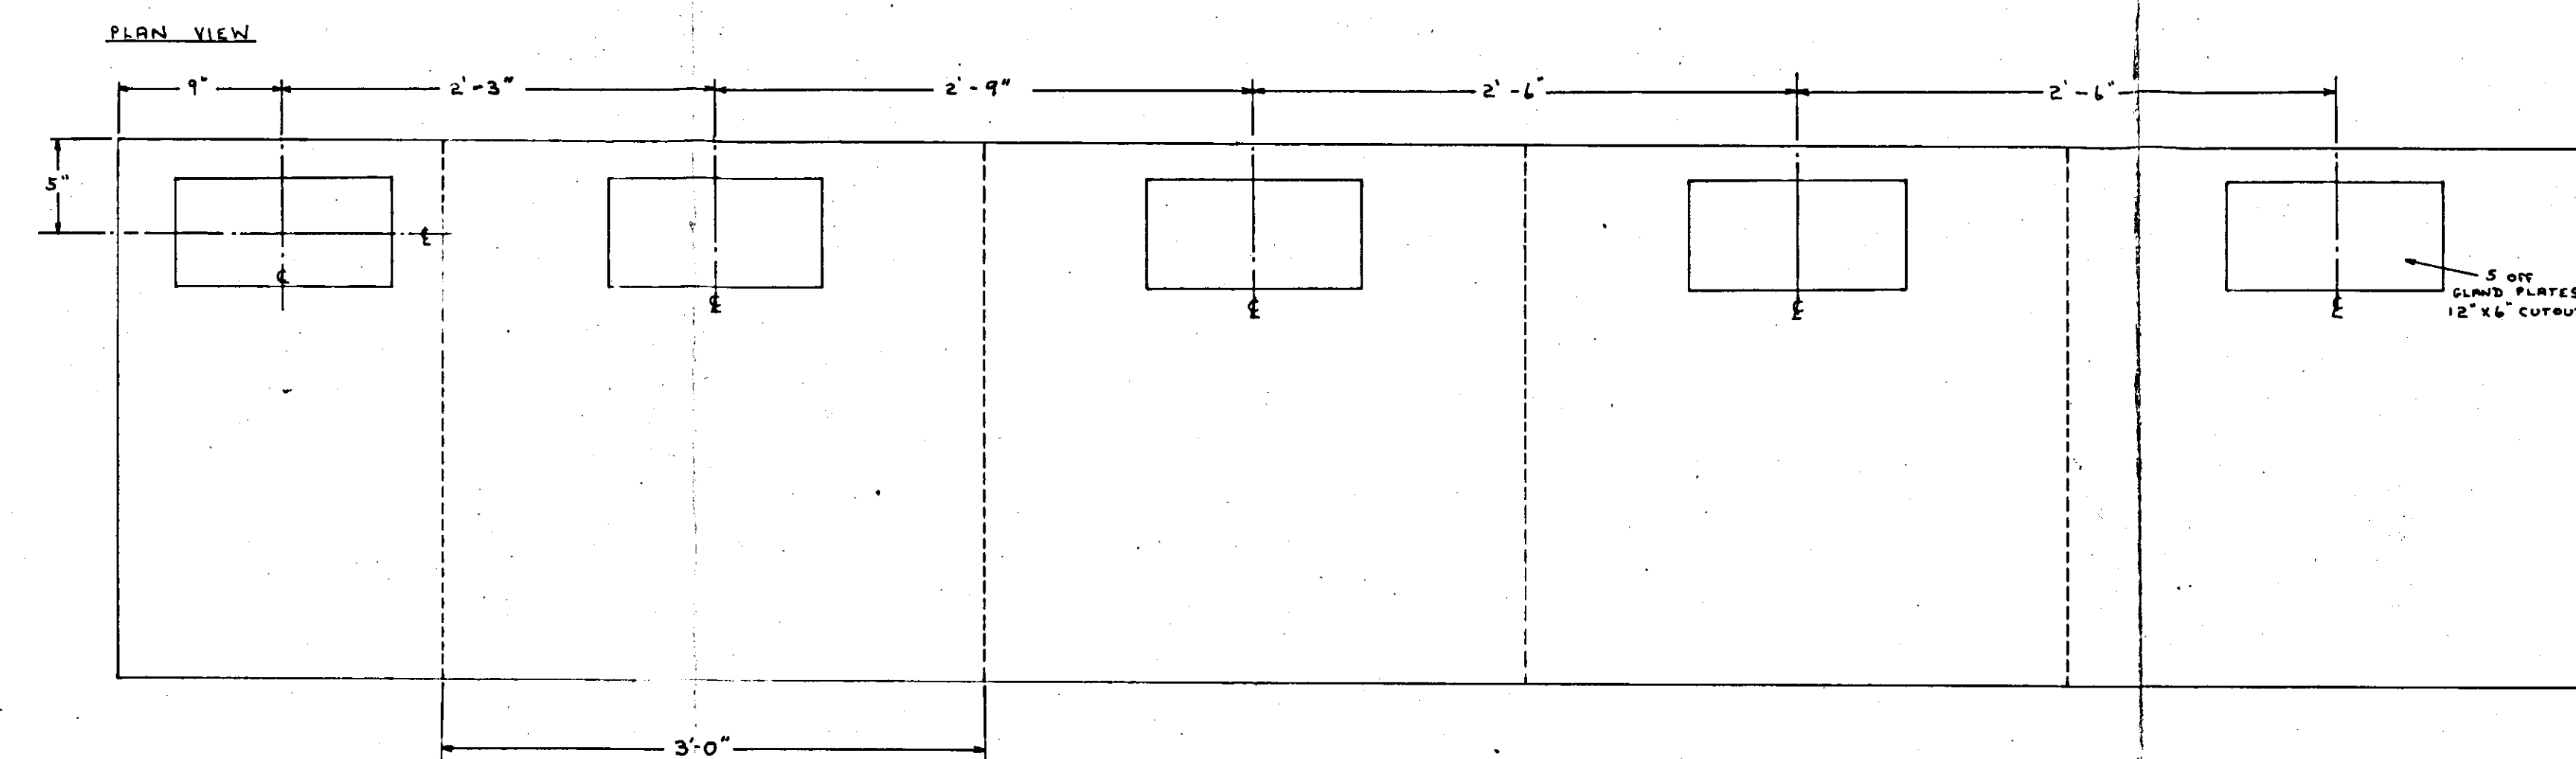

TYPICAL ROOM LAYOUT

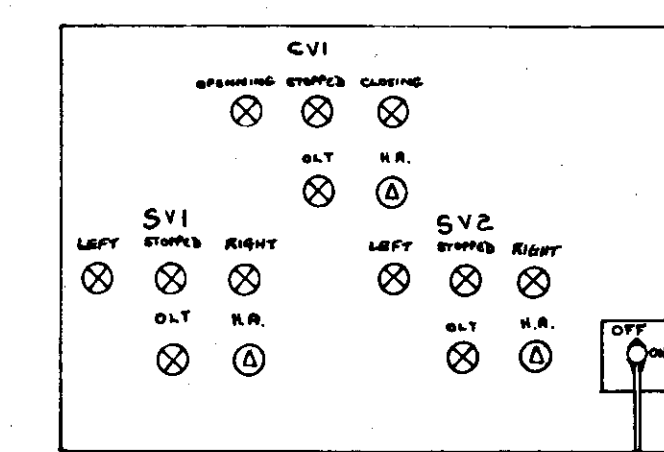

OUTGOING AND INTERCONNECTION TERMINALS AT REAR

To BE REVISED
PLC MODS.

38

DEWHURST & PARTNER LTD.
MELBOURNE WORKS HOUNSLOW

TITLE: LAYOUT FOR MCC 5B - SEAFORTH GRAIN TERMINAL

REVISION: 1
ORIGIN: 1 / 1 SGD.

REVISION: 1
ORIGIN: 1 / 1 SGD.

REVISION: 1
ORIGIN: 1 / 1 SGD.

REVISION: 1
ORIGIN: 1 / 1 SGD.

LAYOUT FOR MCC 5B - SEAFORTH GRAIN TERMINAL

THE DESIGN AND MANUFACTURING INFORMATION CONTAINED IN THIS DRAWING IS THE EXCLUSIVE RIGHT OF DEWHURST & PARTNER LTD. AND MUST NOT BE COPIED OR USED FOR MANUFACTURING PURPOSES.	ISSUE 12
HTX361AC	38
HTX361AC	