


10727

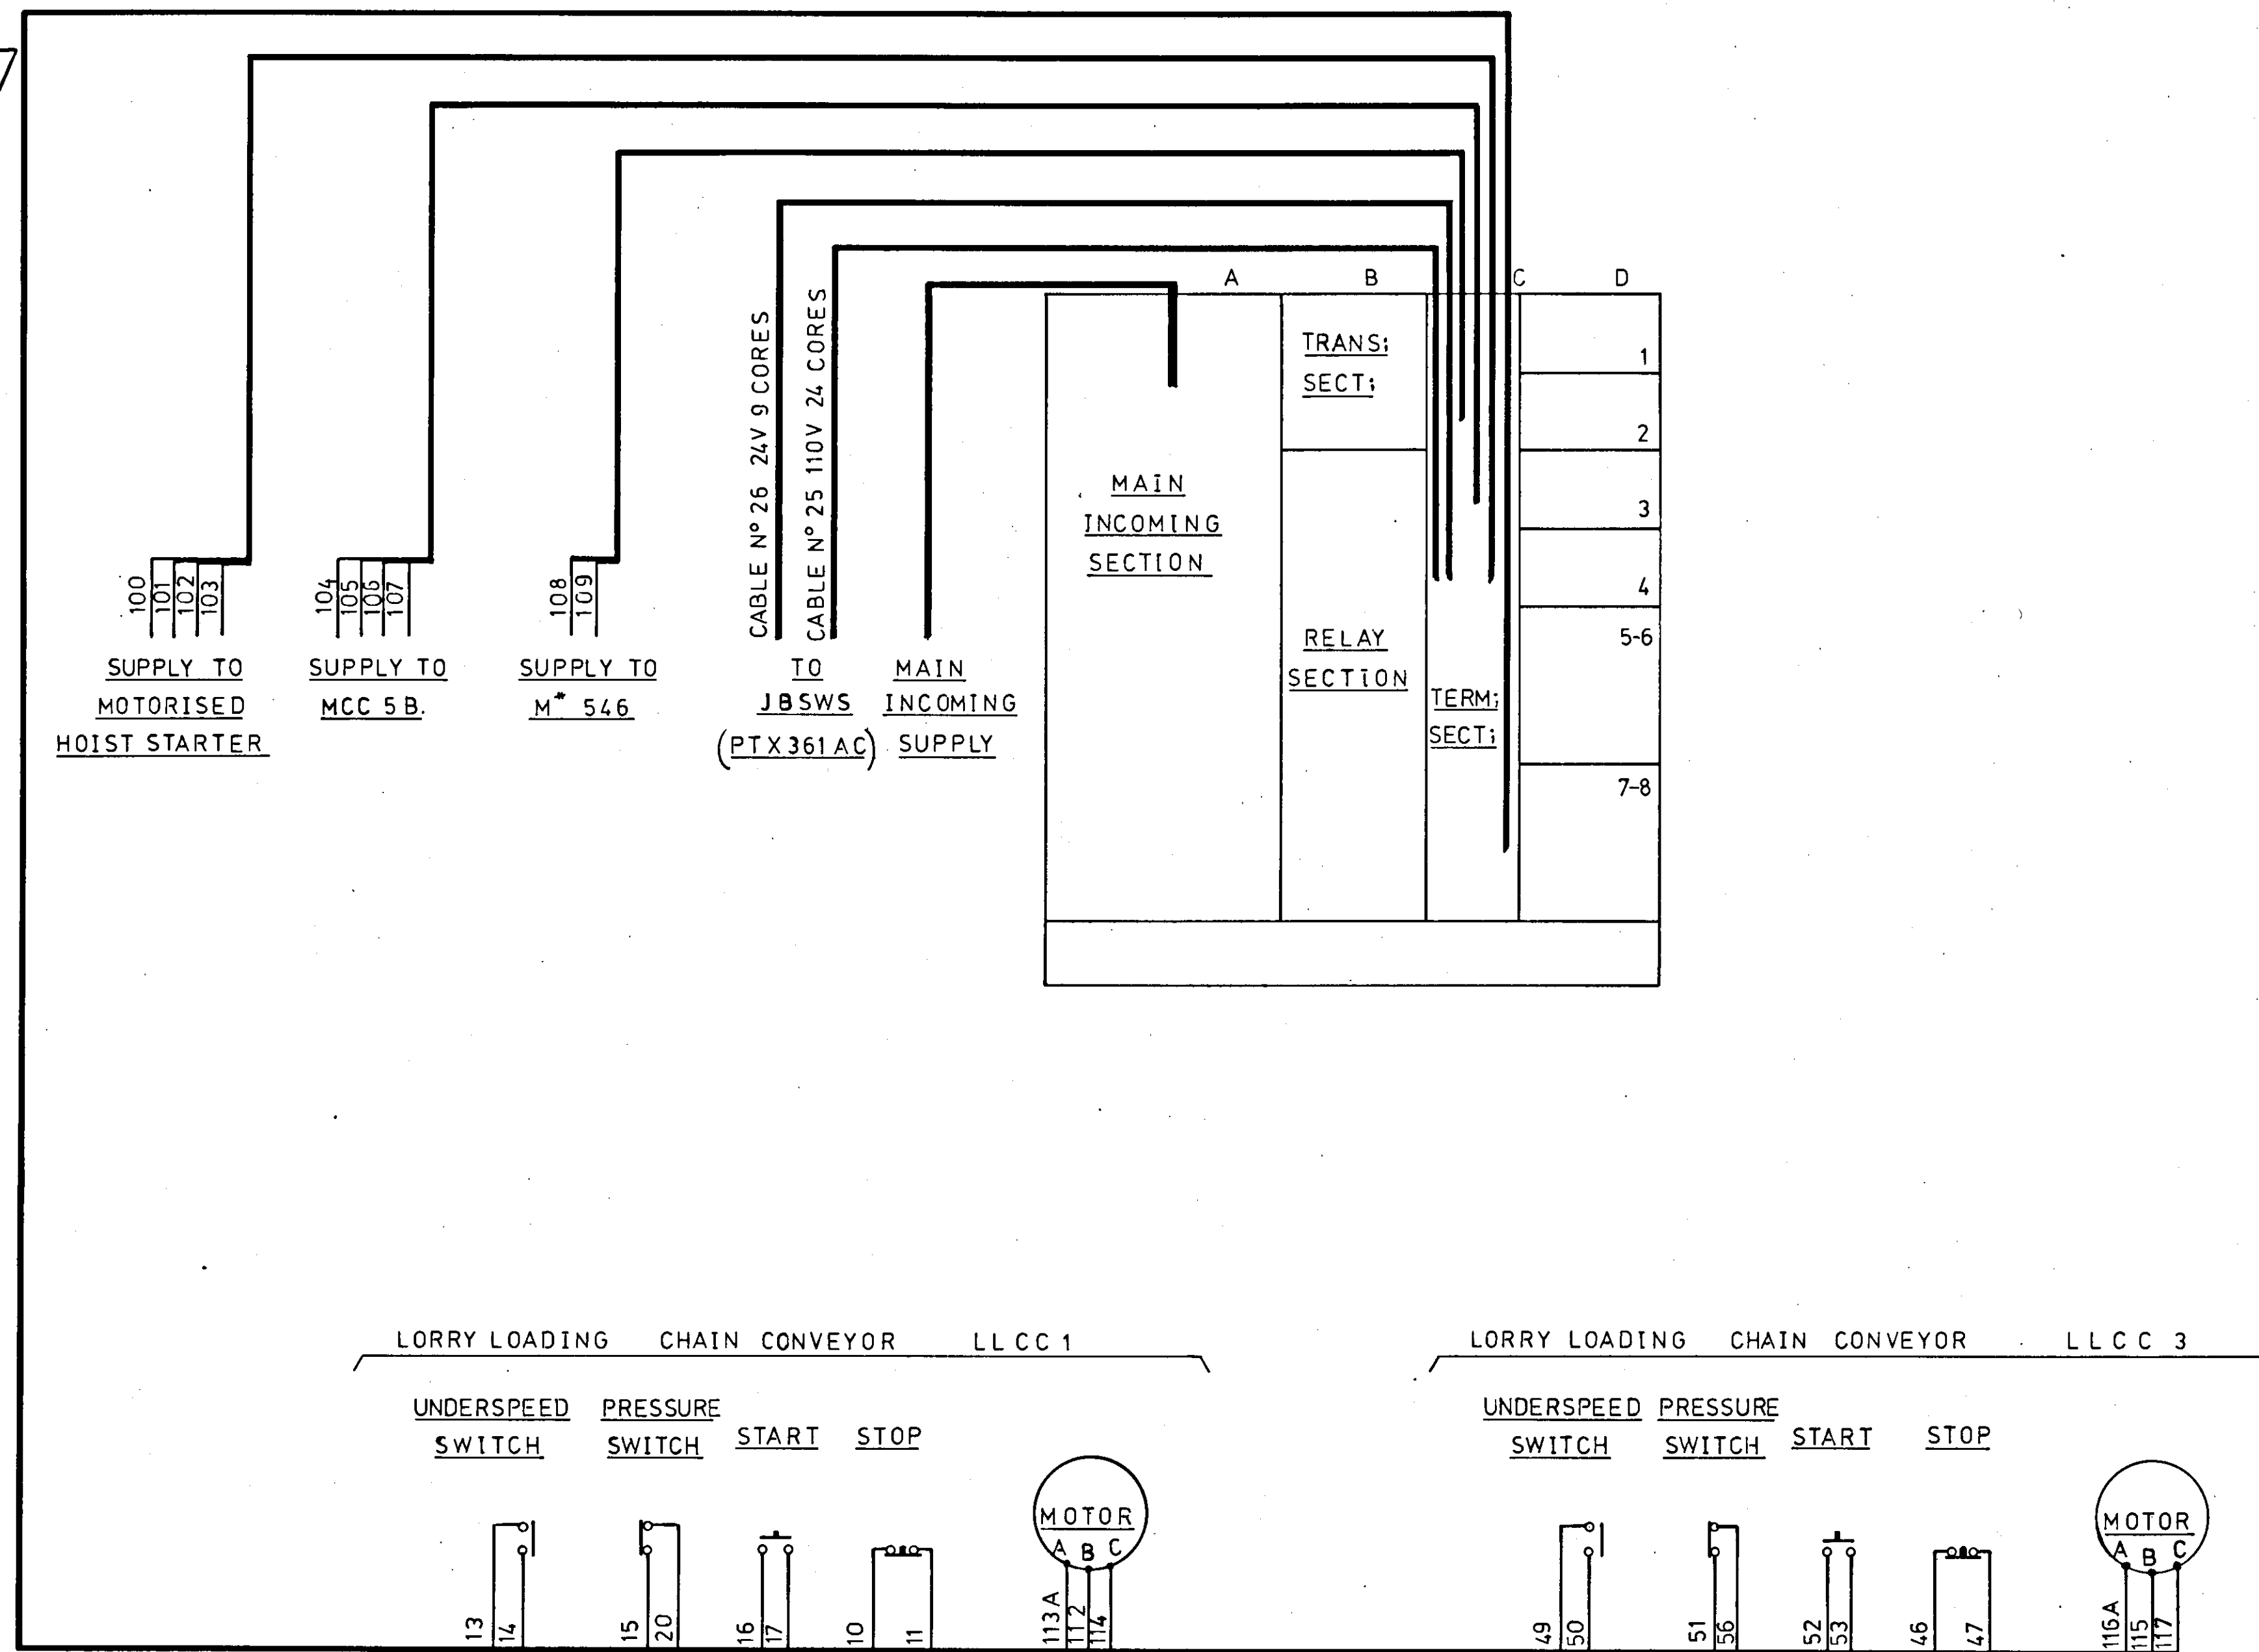

EXTERNAL WIRING DIAGRAM FOR MCC 5A—  
SEAFORTH GRAIN TERMINAL

10727

ISSUE 1

RTX 361 AD

RTX 361 AD

DEWHURST & PARTNER LTD  
MELBOURNE WORKS HOUNSLOW

TITLE  
EXTERNAL WIRING DIAGRAM FOR MCC 5A SEAFORTH GRAIN TERMINAL

REVISION—

REVISION—

REVISION—

DRAWN BY  
DATE — 5-4-71  
CHECKED BY  
APPROVED BY  
DATE  
KEY DIA — CTX 361 AD  
EXT DIA —  
REL DIA —  
PANEL LAYOUT—GTX 361 AD