
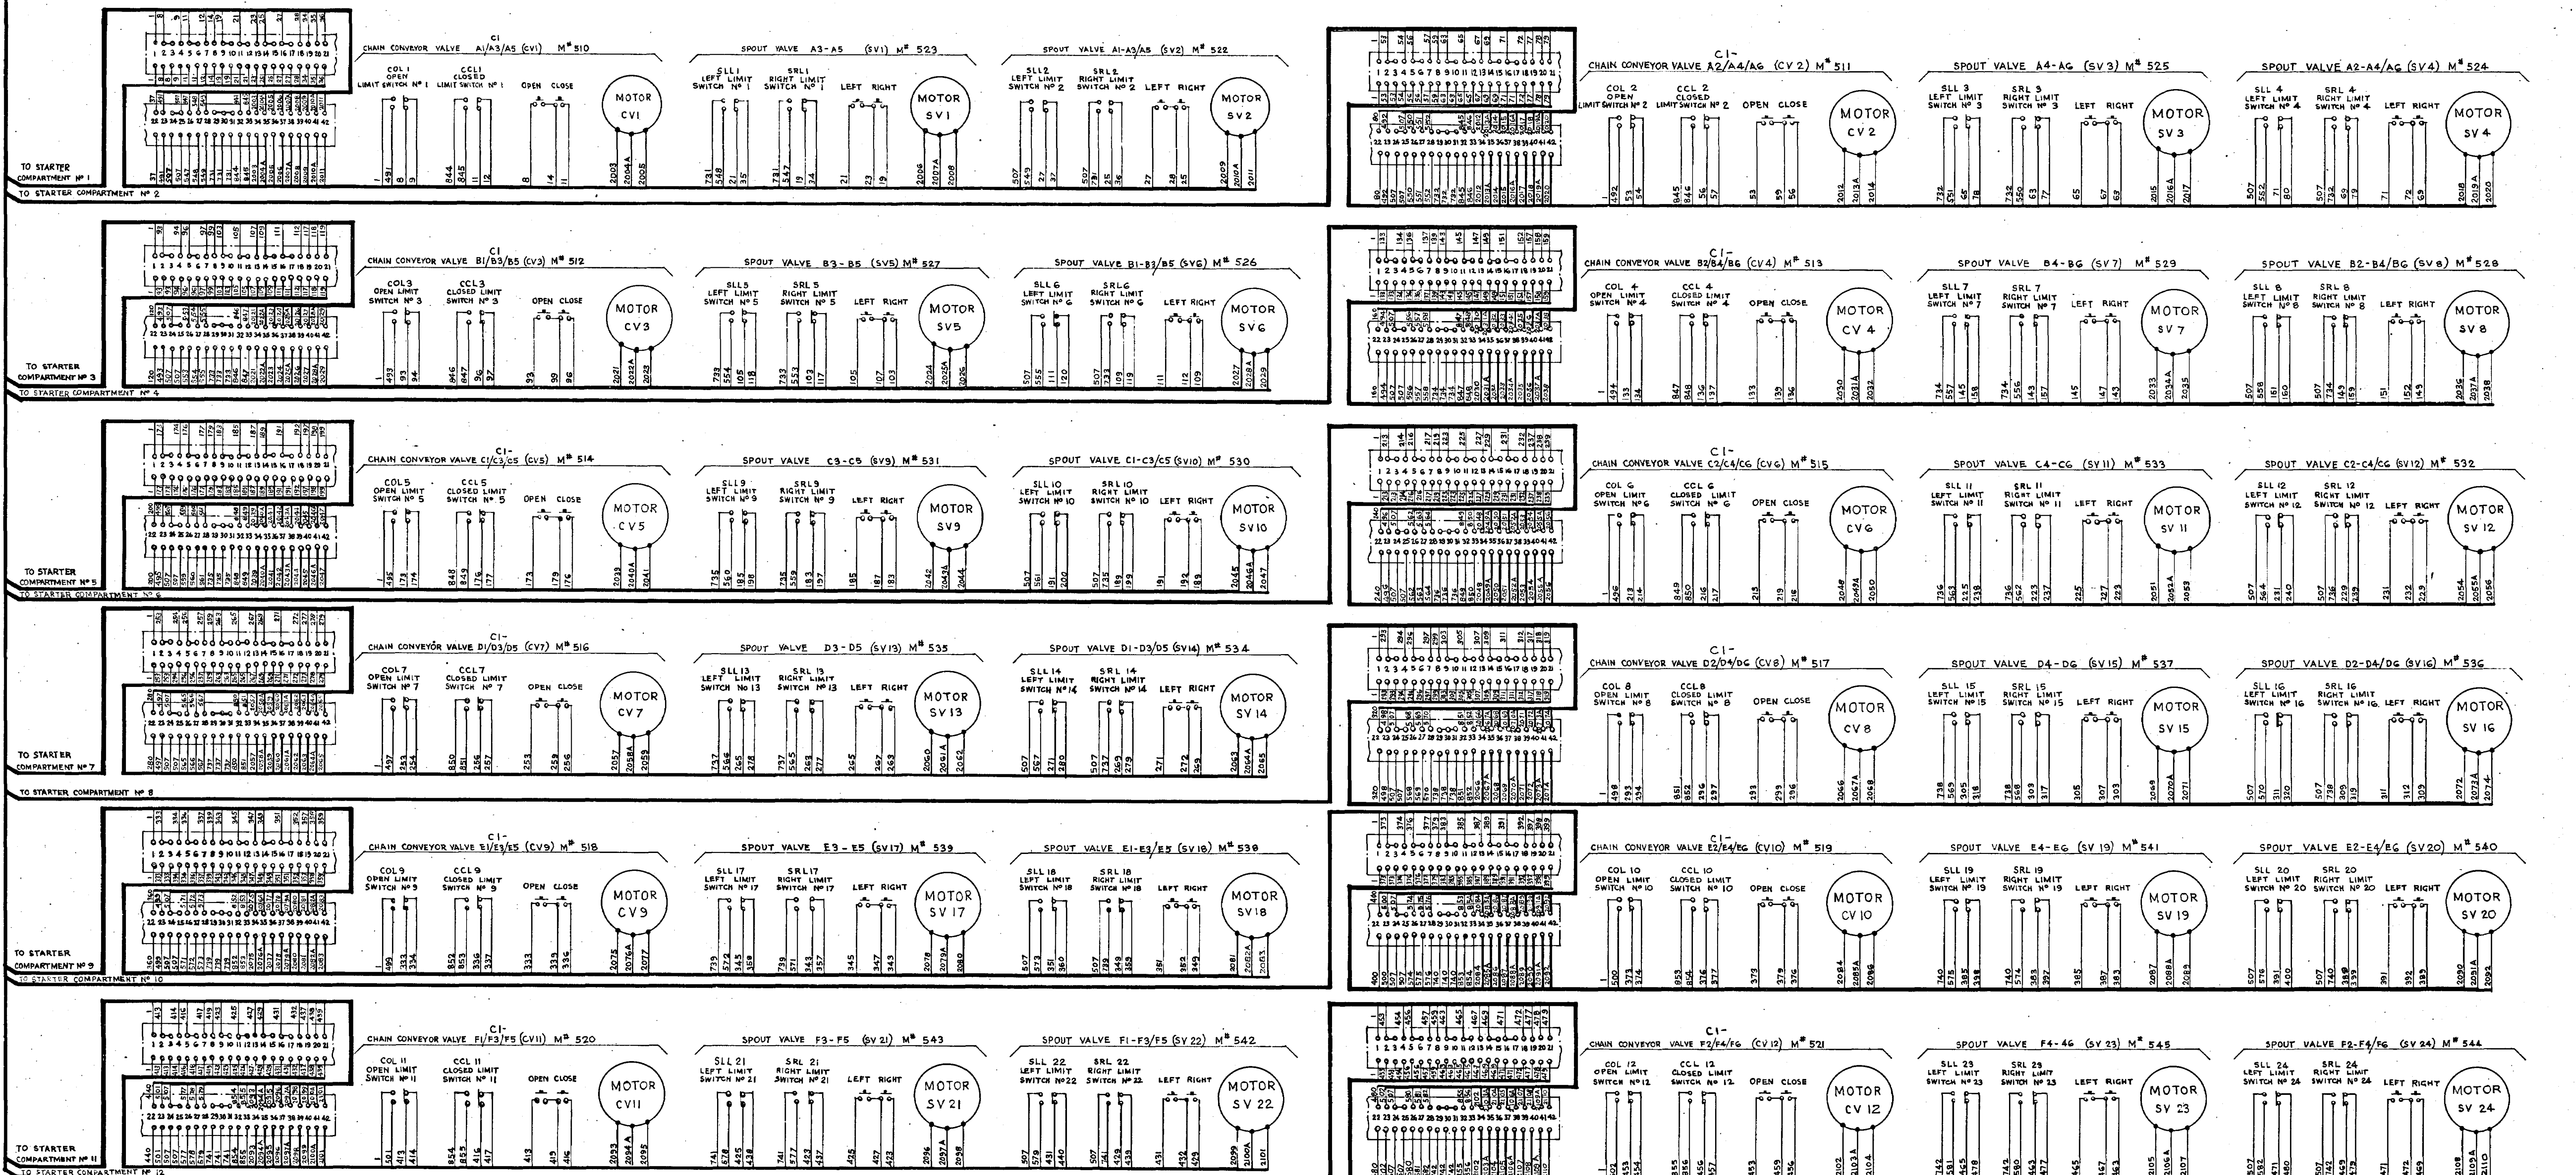


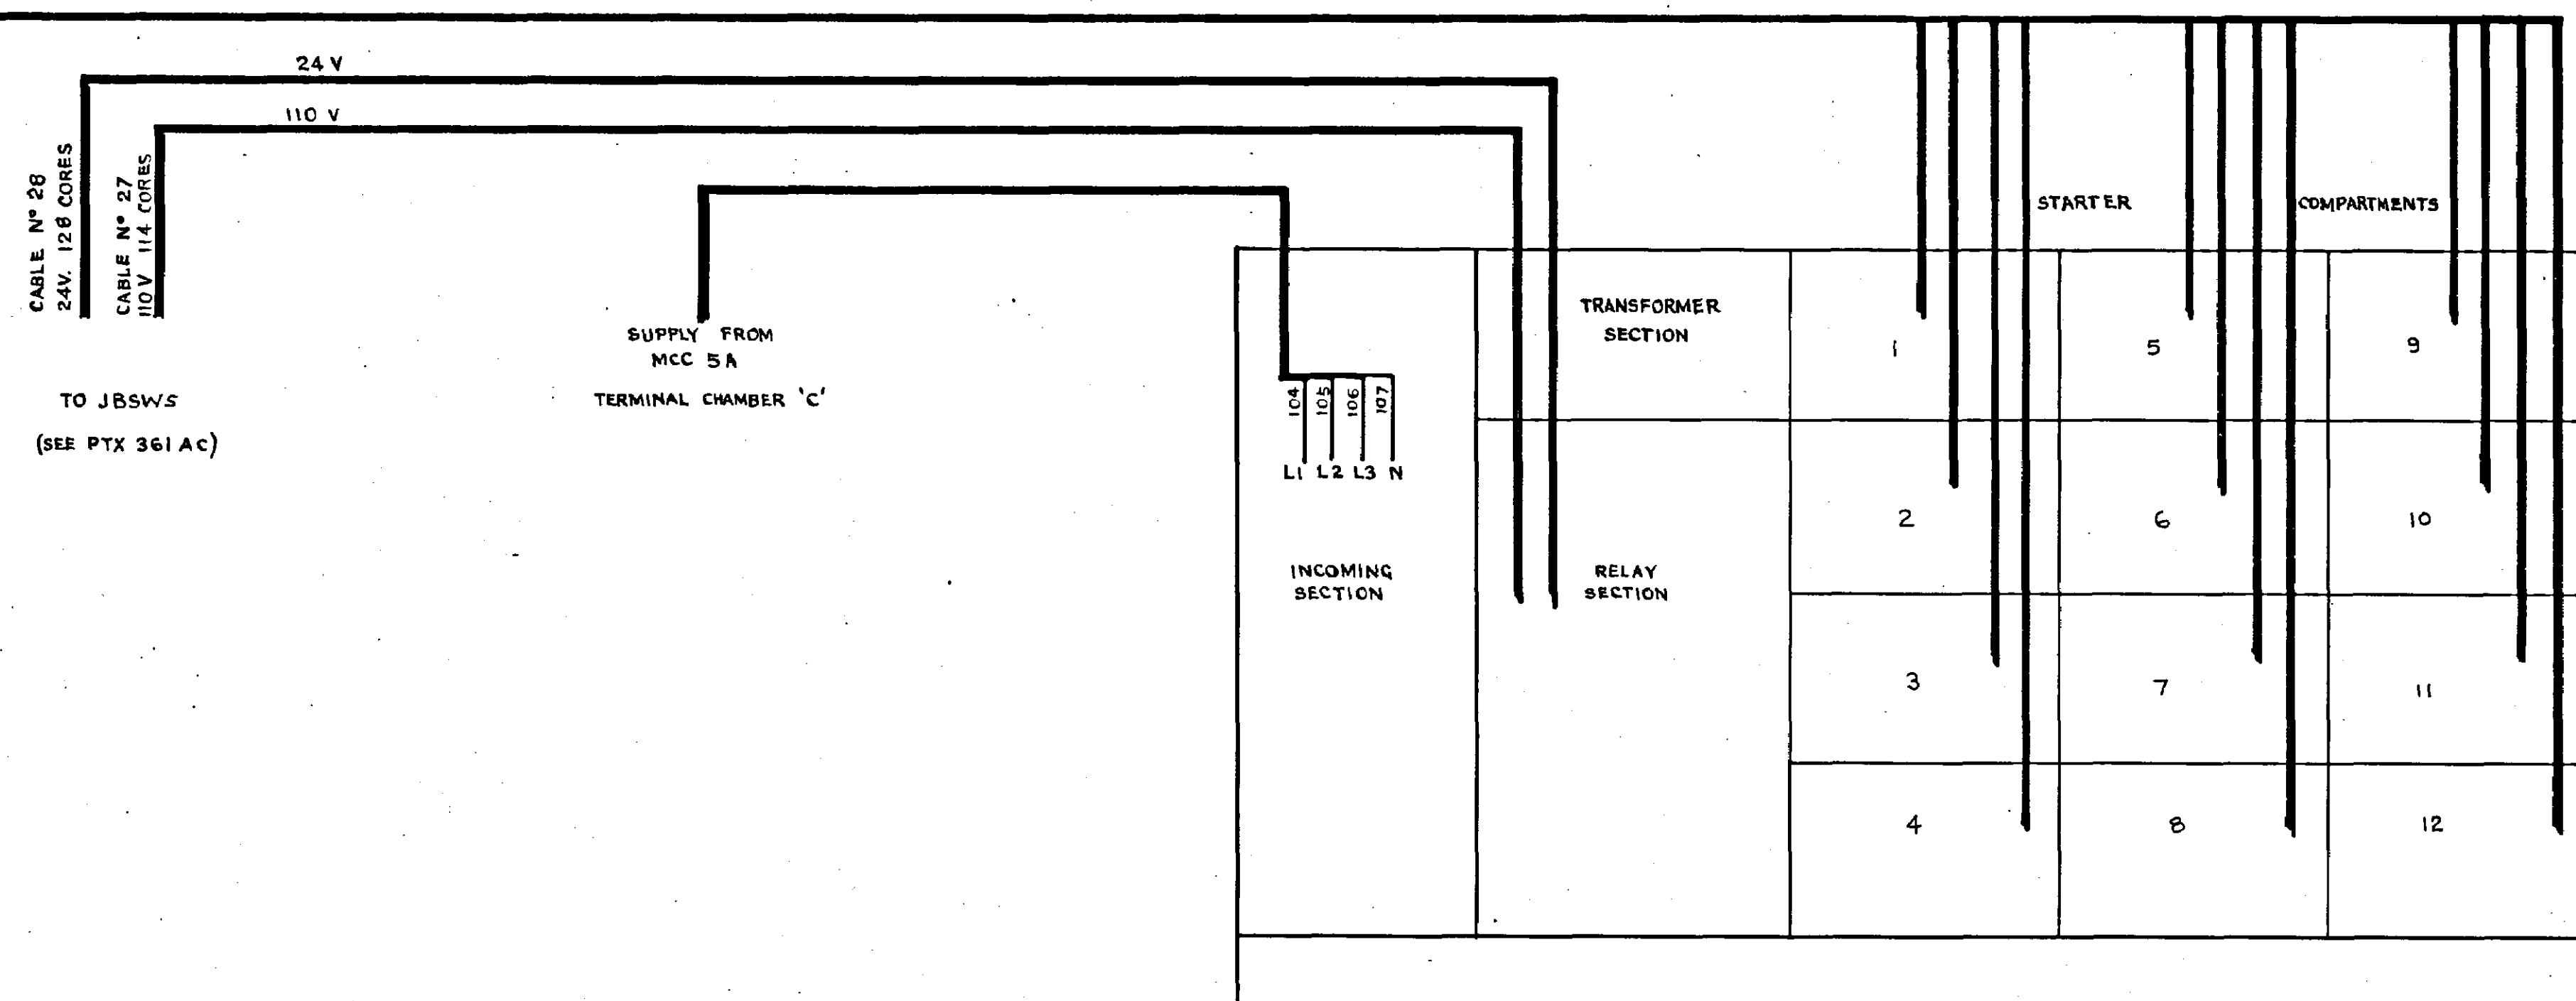

DEWHURST &amp; PARTNER LTD

MELBOURNE WORKS HOUNSLOW

TITLE  
EXTERNAL WIRING DIAGRAM FOR MCC 5B-SEAFORTH GRAIN TERMINAL

REVISION:

ORIGIN: / / SGD

REVISION:

ORIGIN: / / SGD

REVISION:

ORIGIN: / / SGD

REVISION: 2  
WIRES 731-742  
DID GO BACK TO THE  
PANEL  
ORIGIN: EISP  
18/6/71 JOD J.T.REVISION: 1  
SPOUT VALVE  
DESIGNATIONS  
INTERCHANGED  
ORIGIN: EISP  
3/8/71 SGD BJCEXTERNAL WIRING  
DIAGRAM FOR  
MCC 5B  
SEAFORTH GRAIN TERMINALDRAWN BY J. THOMAS  
DATE 5/4/71  
CHECKED BY  
APPROVED BY  
DATETHE DESIGN AND MANUFACTURING  
INFORMATION CONTAINED IN  
THIS DRAWING IS THE EXCLUSIVE  
RIGHT OF DEWHURST & PARTNER  
LTD. AND MUST NOT BE COPIED  
OR USED FOR MANUFACTURING  
PURPOSES

ISSUE 1/2/3

STX 361 AC

STX 361 AC