


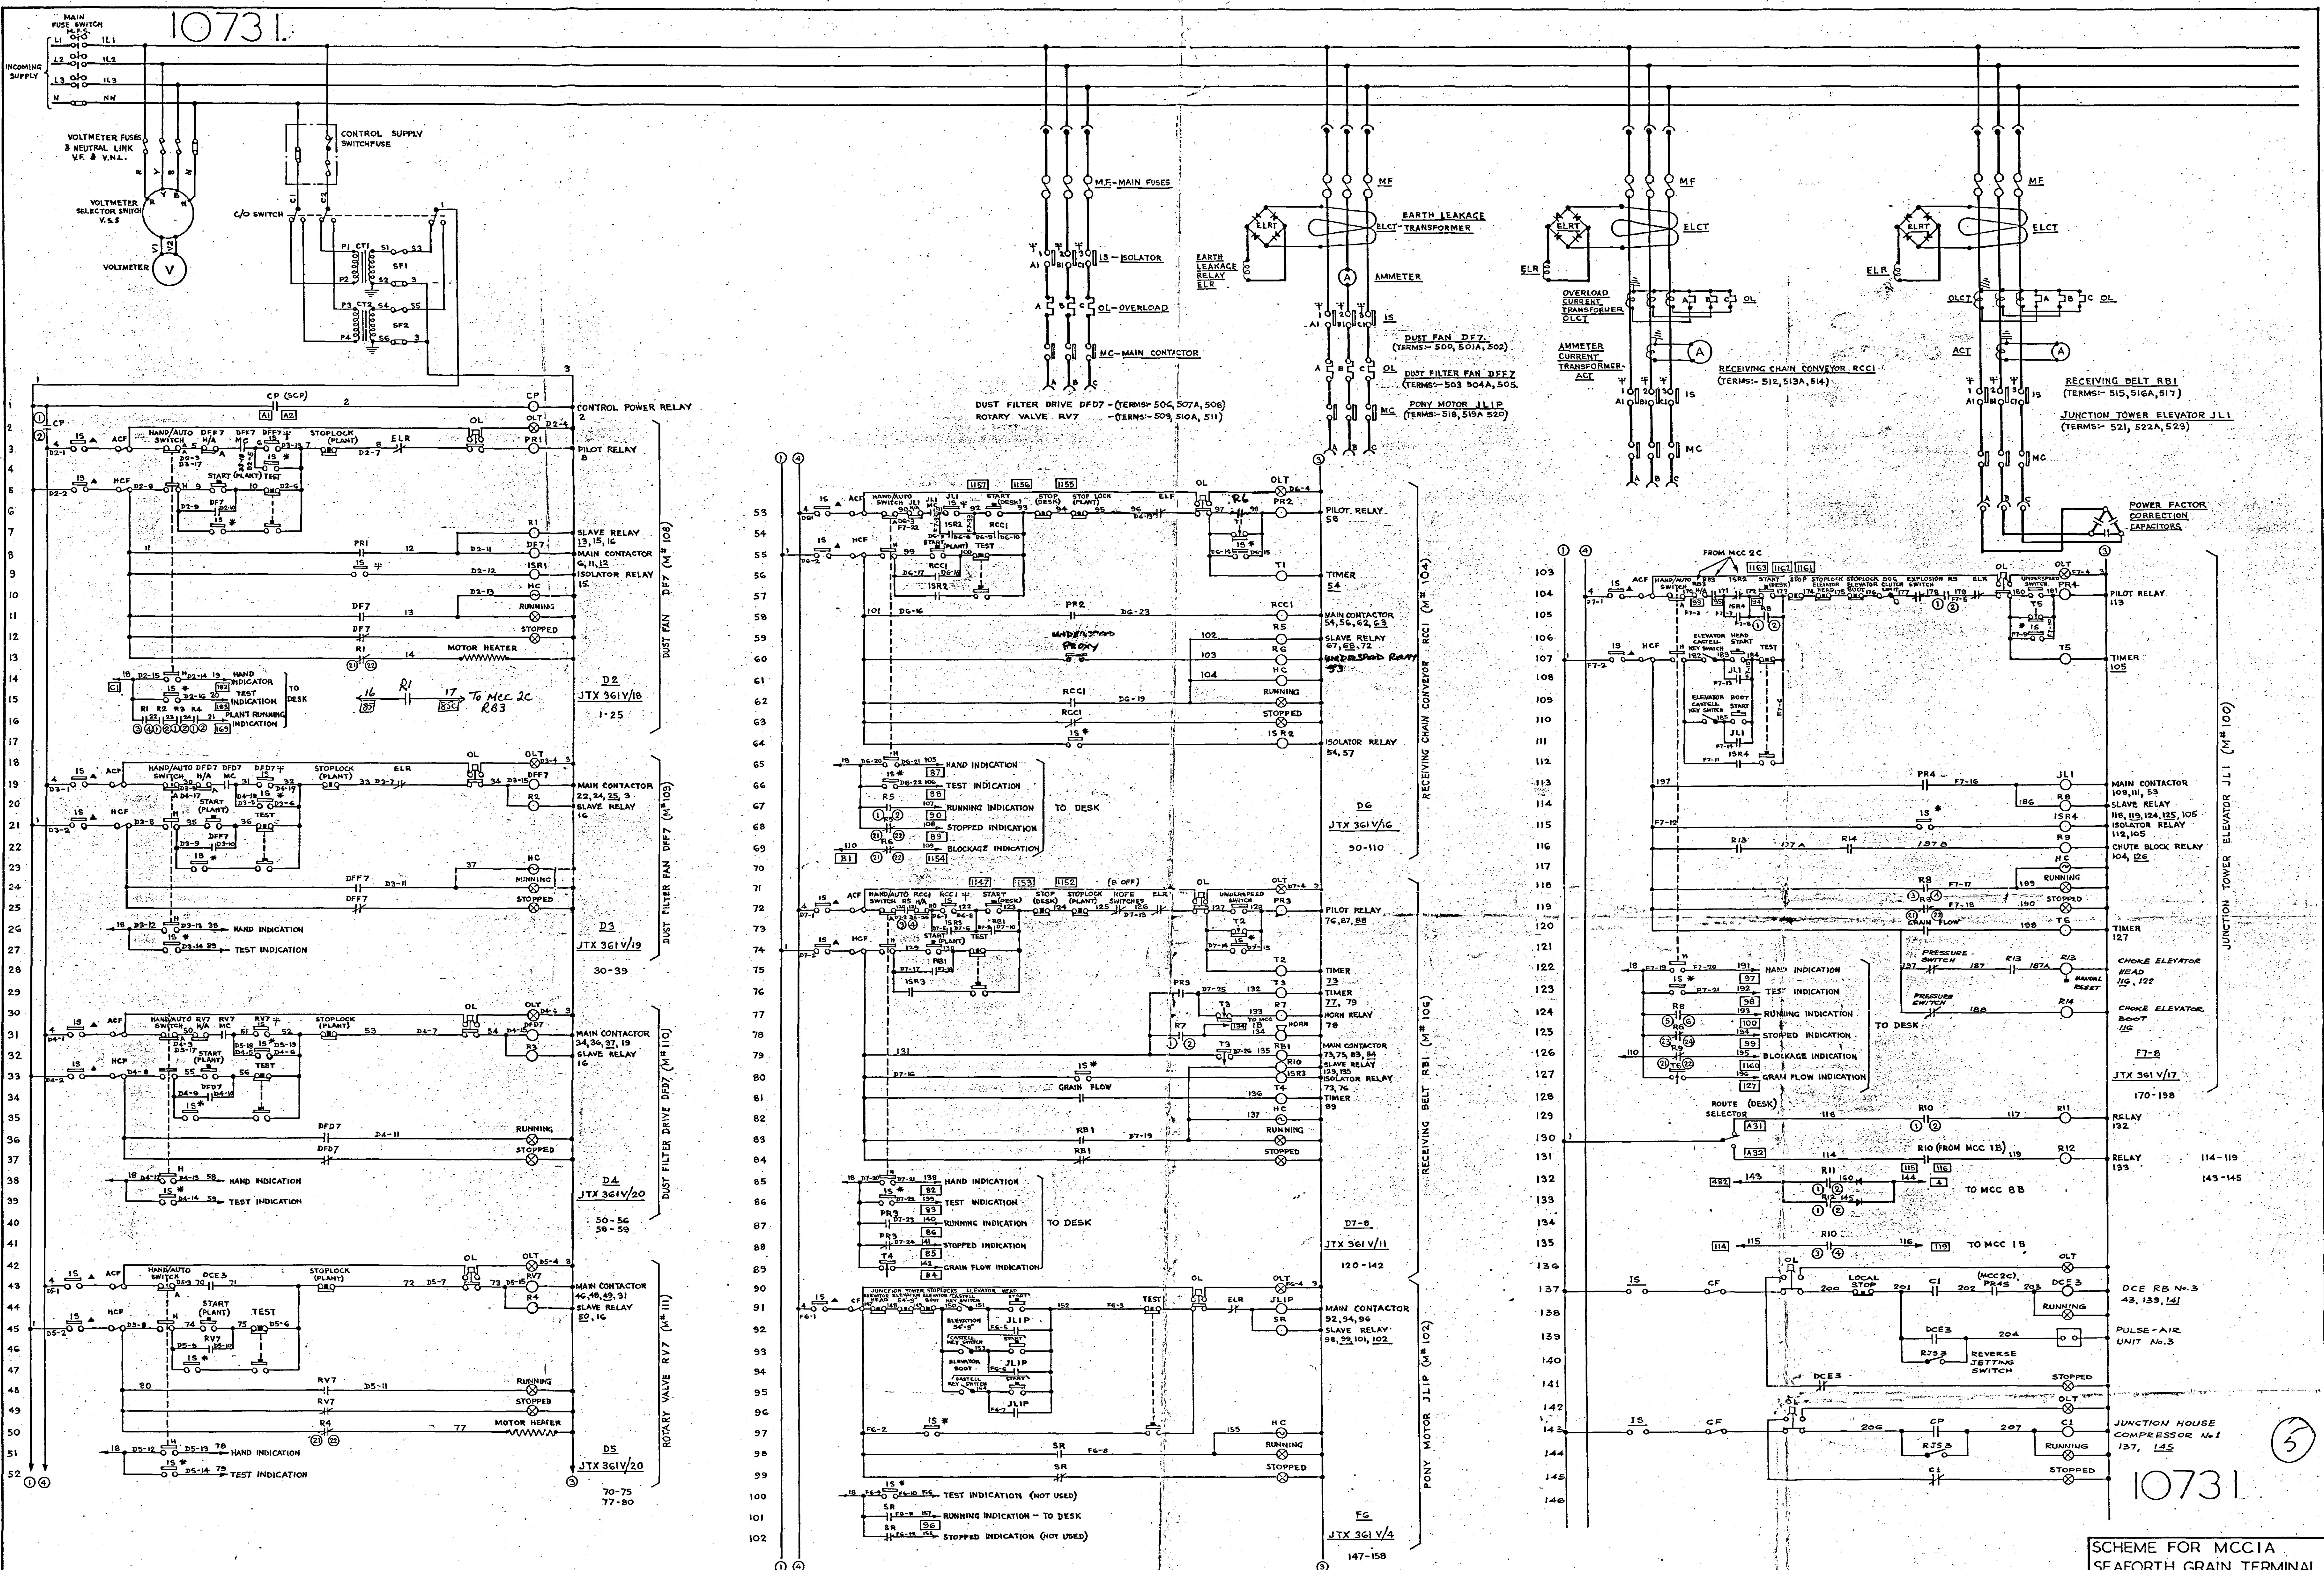

DEWHURST & PARTNER LTD MELBOURNE WORKS. HOUNSLOW.		TITLE SCHEME FOR MCC1A - SEAFORTH GRAIN TERMINAL		REVISION: 11 WIRING MODS TO CHUTE BLOCK REM. ADDED. 31-9-77.		REVISION: 10 NEW COMPRESSOR FITTED IN JUNCTION HOUSE FOR DCE/INTERLOCKS DELTA. E.B. NO.3. MOD. COL. LINES 15 & 19. 22-4-84 E.P.		REVISION: 9 MCC 2B & MCC2C HITTED IN 3/HOUSE FOR RB NO.3 E.E. PRICE		REVISION: 8 NEW DUST PLANT (DCE) HITTED IN 3/HOUSE FOR RB NO.3 E.E. PRICE		REVISION: 7 ON RBT SUSTAINING FEED MODIFIED. MINOR MODS. 20/4/71 SGB. J.T.		REVISION: 6 DCEK CONNECTIONS ADDED. 24/1/72 SGB. J.S.		REVISION: 5 DCEK CONNECTIONS ADDED. 24/1/72 SGB. J.S.		REVISION: 4 MODS TO RCC1, RB1 AND JL1. 1/6/71 SGB. B.J.C.		REVISION: 3 CONNECTIONS TO MCC2B MODIFIED. 14/2/72 J.S.		REVISION: 2 BLOCKAGE INDICATION FEED MODIFIED. MINOR MODS. 11/5/71 SGB. J.T.		REVISION: 1 HORR CONNECTION TO RB ADDED. 26/5/71 SGB. J.T.		THE DESIGN AND MANUFACTURING INFORMATION CONTAINED IN THIS DRAWING IS THE EXCLUSIVE RIGHT OF DEWHURST & PARTNER LTD. AND MUST NOT BE COPIED OR USED FOR MANUFACTURING PURPOSES.		KEY DIAG NO. EXT. DIAG NO. 5TX 361 AA REL. DIAG NO. JTX 361 AA PANEL LAYOUT NO. HTX 361 AA		SCHEME FOR MCC1A SEAFORTH GRAIN TERMINAL ISSUE 123456789101112 DTX 361 AA DTX 361 AA	
--	--	---	--	--	--	--	--	--	--	--	--	---	--	--	--	--	--	--	--	--	--	---	--	---	--	---	--	---	--	--	--