


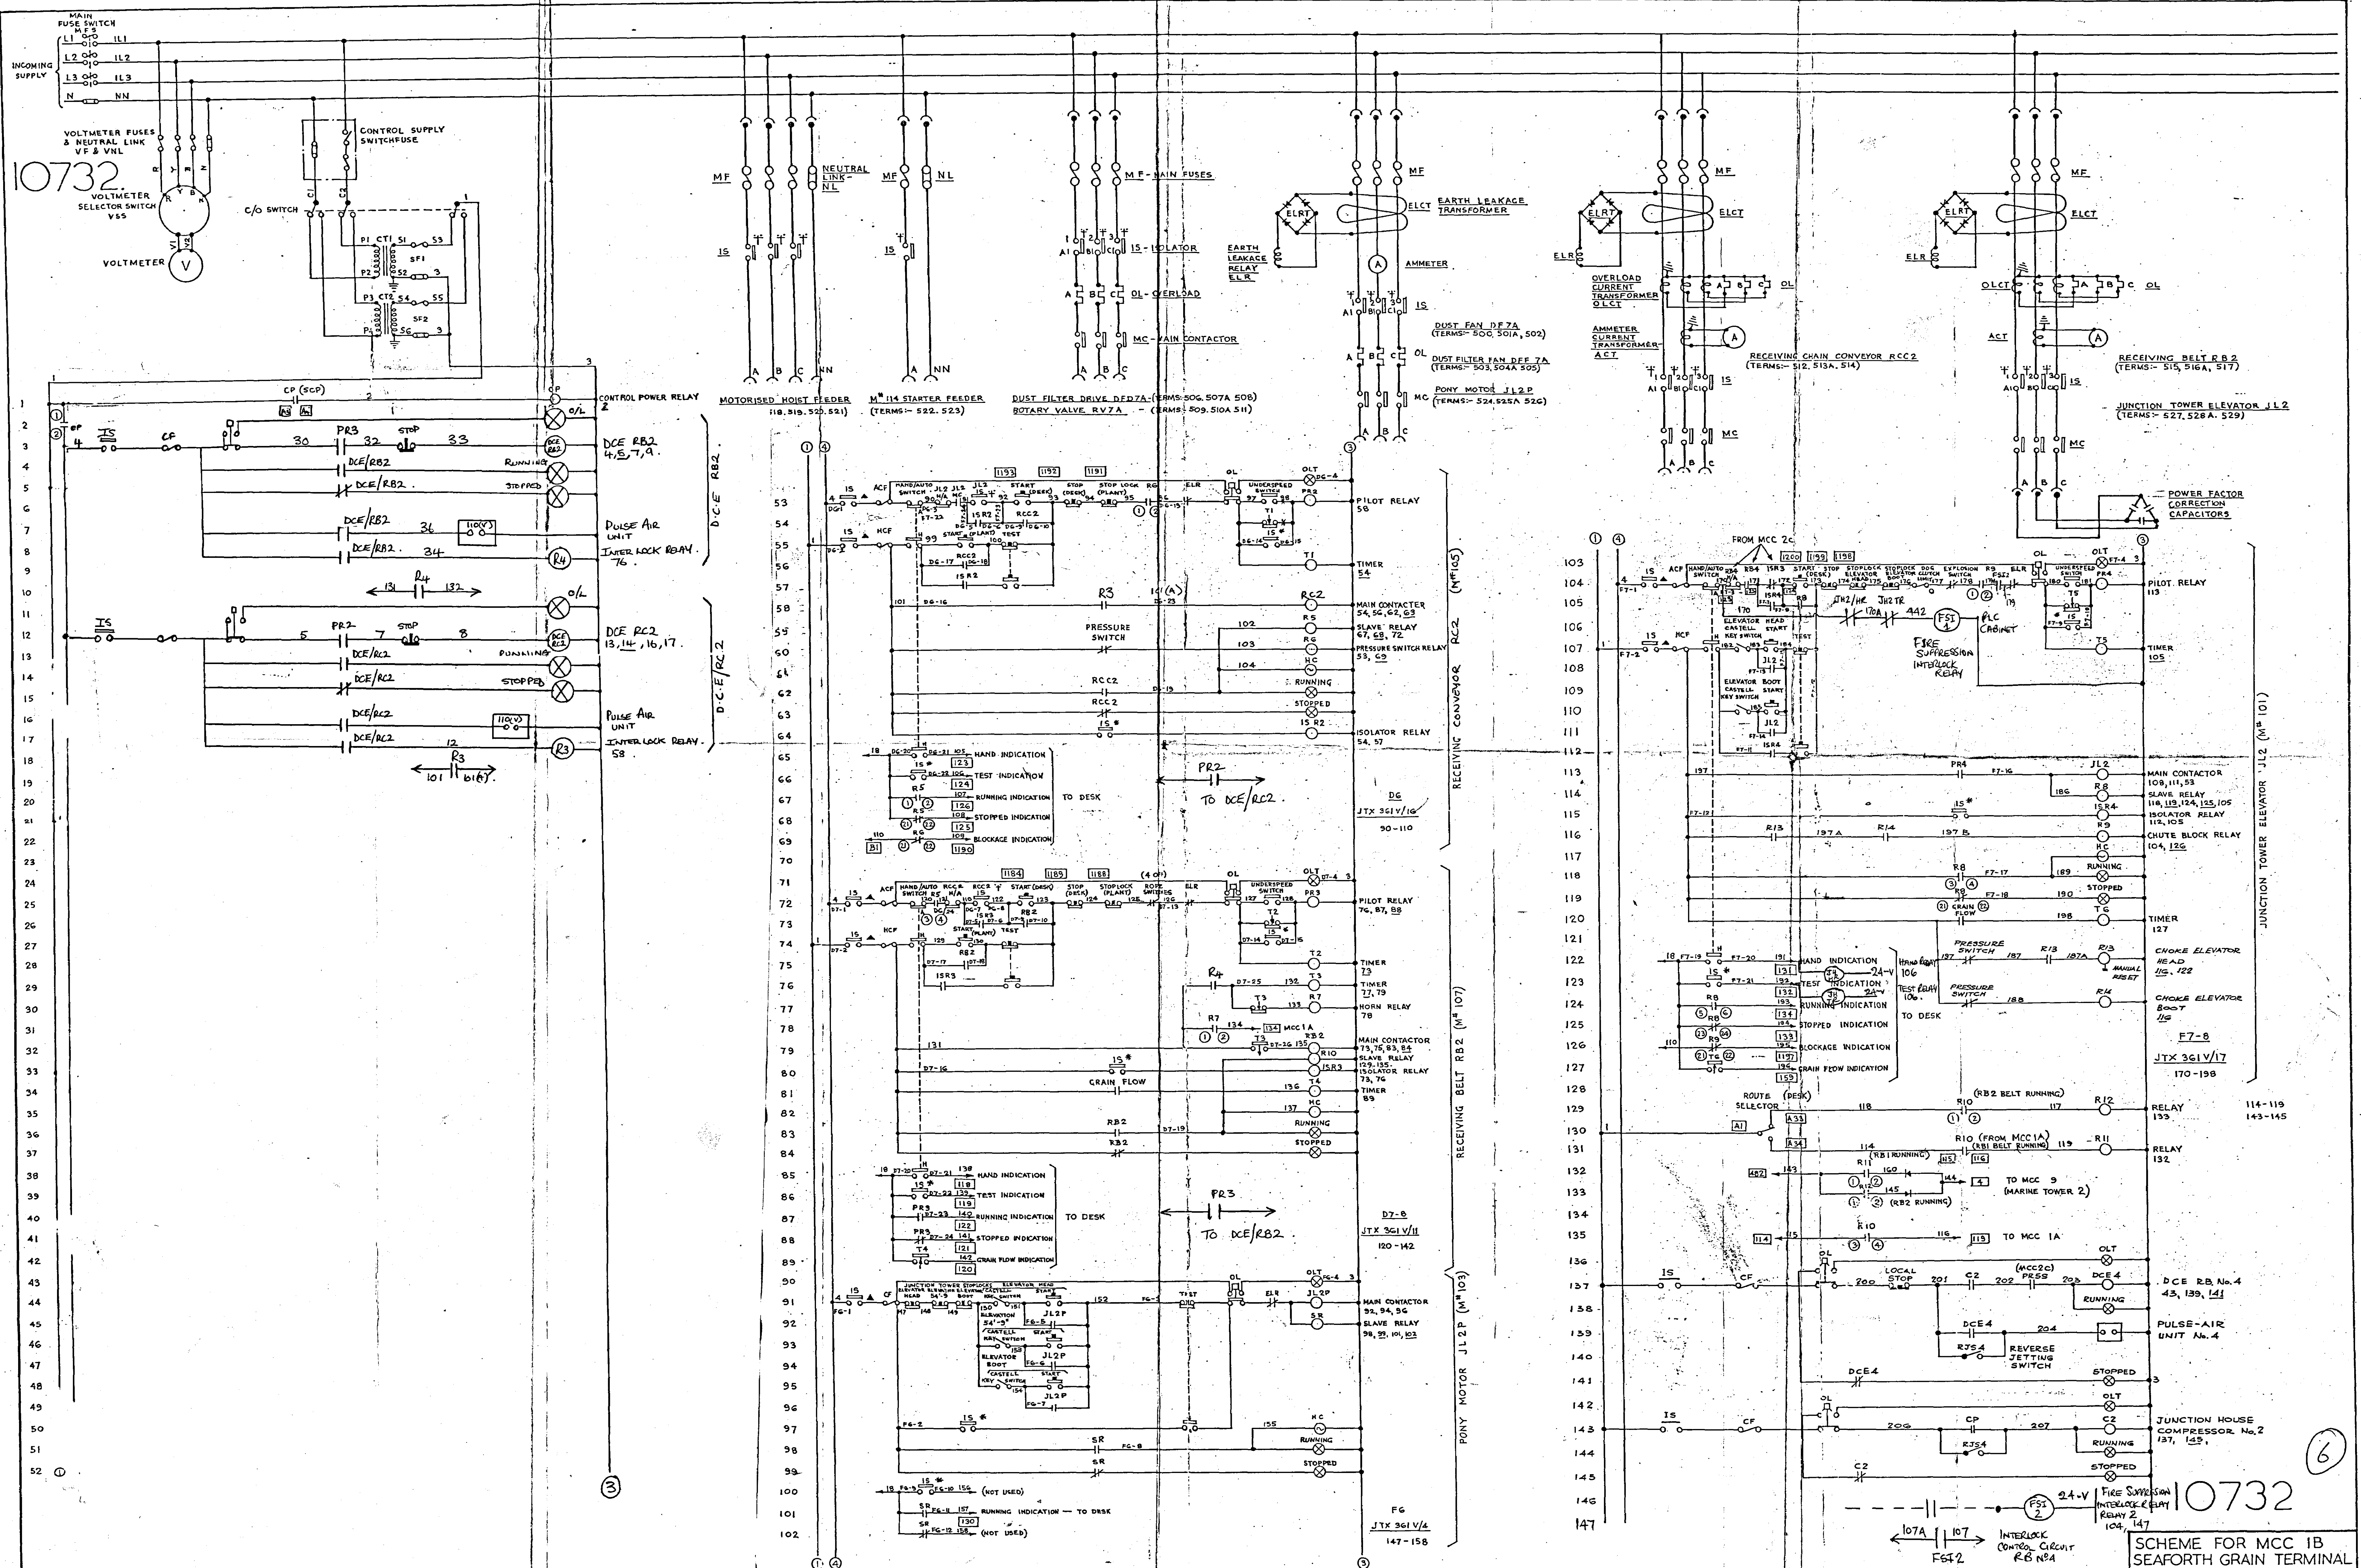

DEWHURST & PARTNER LTD.
MELBOURNE WORKS HOUNSLOW

SCHEME FOR MCCIB - SEAFORTH GRAIN TERMINAL

▲ DENOTES CONTACTS MADE IN 'ON' AND 'TEST' POSITIONS. ◆ DENOTES CONTACTS MADE IN 'TEST' POSITION ONLY * DENOTES CONTACTS MADE IN 'ON' POSITION ONLY										INFORMATION CONTAINED IN THIS DRAWING IS THE EXCLUSIVE RIGHT OF DEWHURST & PARTNER LTD. AND MUST NOT BE COPIED OR USED FOR MANUFACTURING PURPOSES										15302 1 2 3 4 5 6 7 8 9 10 11 12 13 DTX 361 AB	
REVISION: 12 WINDING 13 FROM DUST PLUMB TO D.C.E. UNITS MOD: 13 191013 27-9 99 00										REVISION: 11 WINDING MODS. TO CHUTE BLOCK RELAY RELAYS R13 & R14 MOD: 11 191013 55-1-134 6P										REVISION: 10 NEW COMPRESSOR FITTED IN JUNCTION OF R24 & R25 EXTRA COMPRESSOR FITTED: 28-1-59										REVISION: 9 NEW DUST PLANT (CCE) COMPRESSOR IN J1/JOKE OF R24 & R25 MOD: 9 191013 5-5-59 6P										DTX 361 AB	
REVISION: 8 CONTACT R1102 ADDED ON LINE 1 0-3-77										REVISION: 7 RELAYS R11 & R12 REVERSED MODIFIED ORIGIN: SITE 08/12/73 H.S.										REVISION: 6 CONNECTIONS TO MCC 98 MODIFIED ORIGIN: CUST. 24/1/73 H.S.										REVISION: 5 R22 TERMINALS ADDED ORIGIN: I.C.R. 24/1/73 SGB, J.S.										REVISION: 4 MODS R22, R23, R28 & J12. ORIGIN: E.J.S.P. 08/11/59 B.G.C.										REVISION: 3 ON R23 SUSTAINING CONTACT WAS ON M.C.C. TERMINAL MODIFIED ORIGIN: E.J.S.P. 17/11/59 S.G.D.										REVISION: 2 BLOCKAGE INDICATION FEED MODIFIED. MINOR MODS. TERMINAL MODIFIED ORIGIN: E.J.S.P. 25/2/71 SGT, J.T.										REVISION: 1 NOT REMOVED ORIGIN: E.J.S.P. 25/2/71 SGT, J.T.										DRAWN BY THOMAS DATE 18/2/71 CHECKED BY APPROVED BY DATE										KEY DIAG. NO EXT. LAY. NO JTX 361 A.B. REL. DIAG. NO JTX 361 A.B. PANEL LAYOUT NO HTX 361 A.B.										DTX 361 AB									