


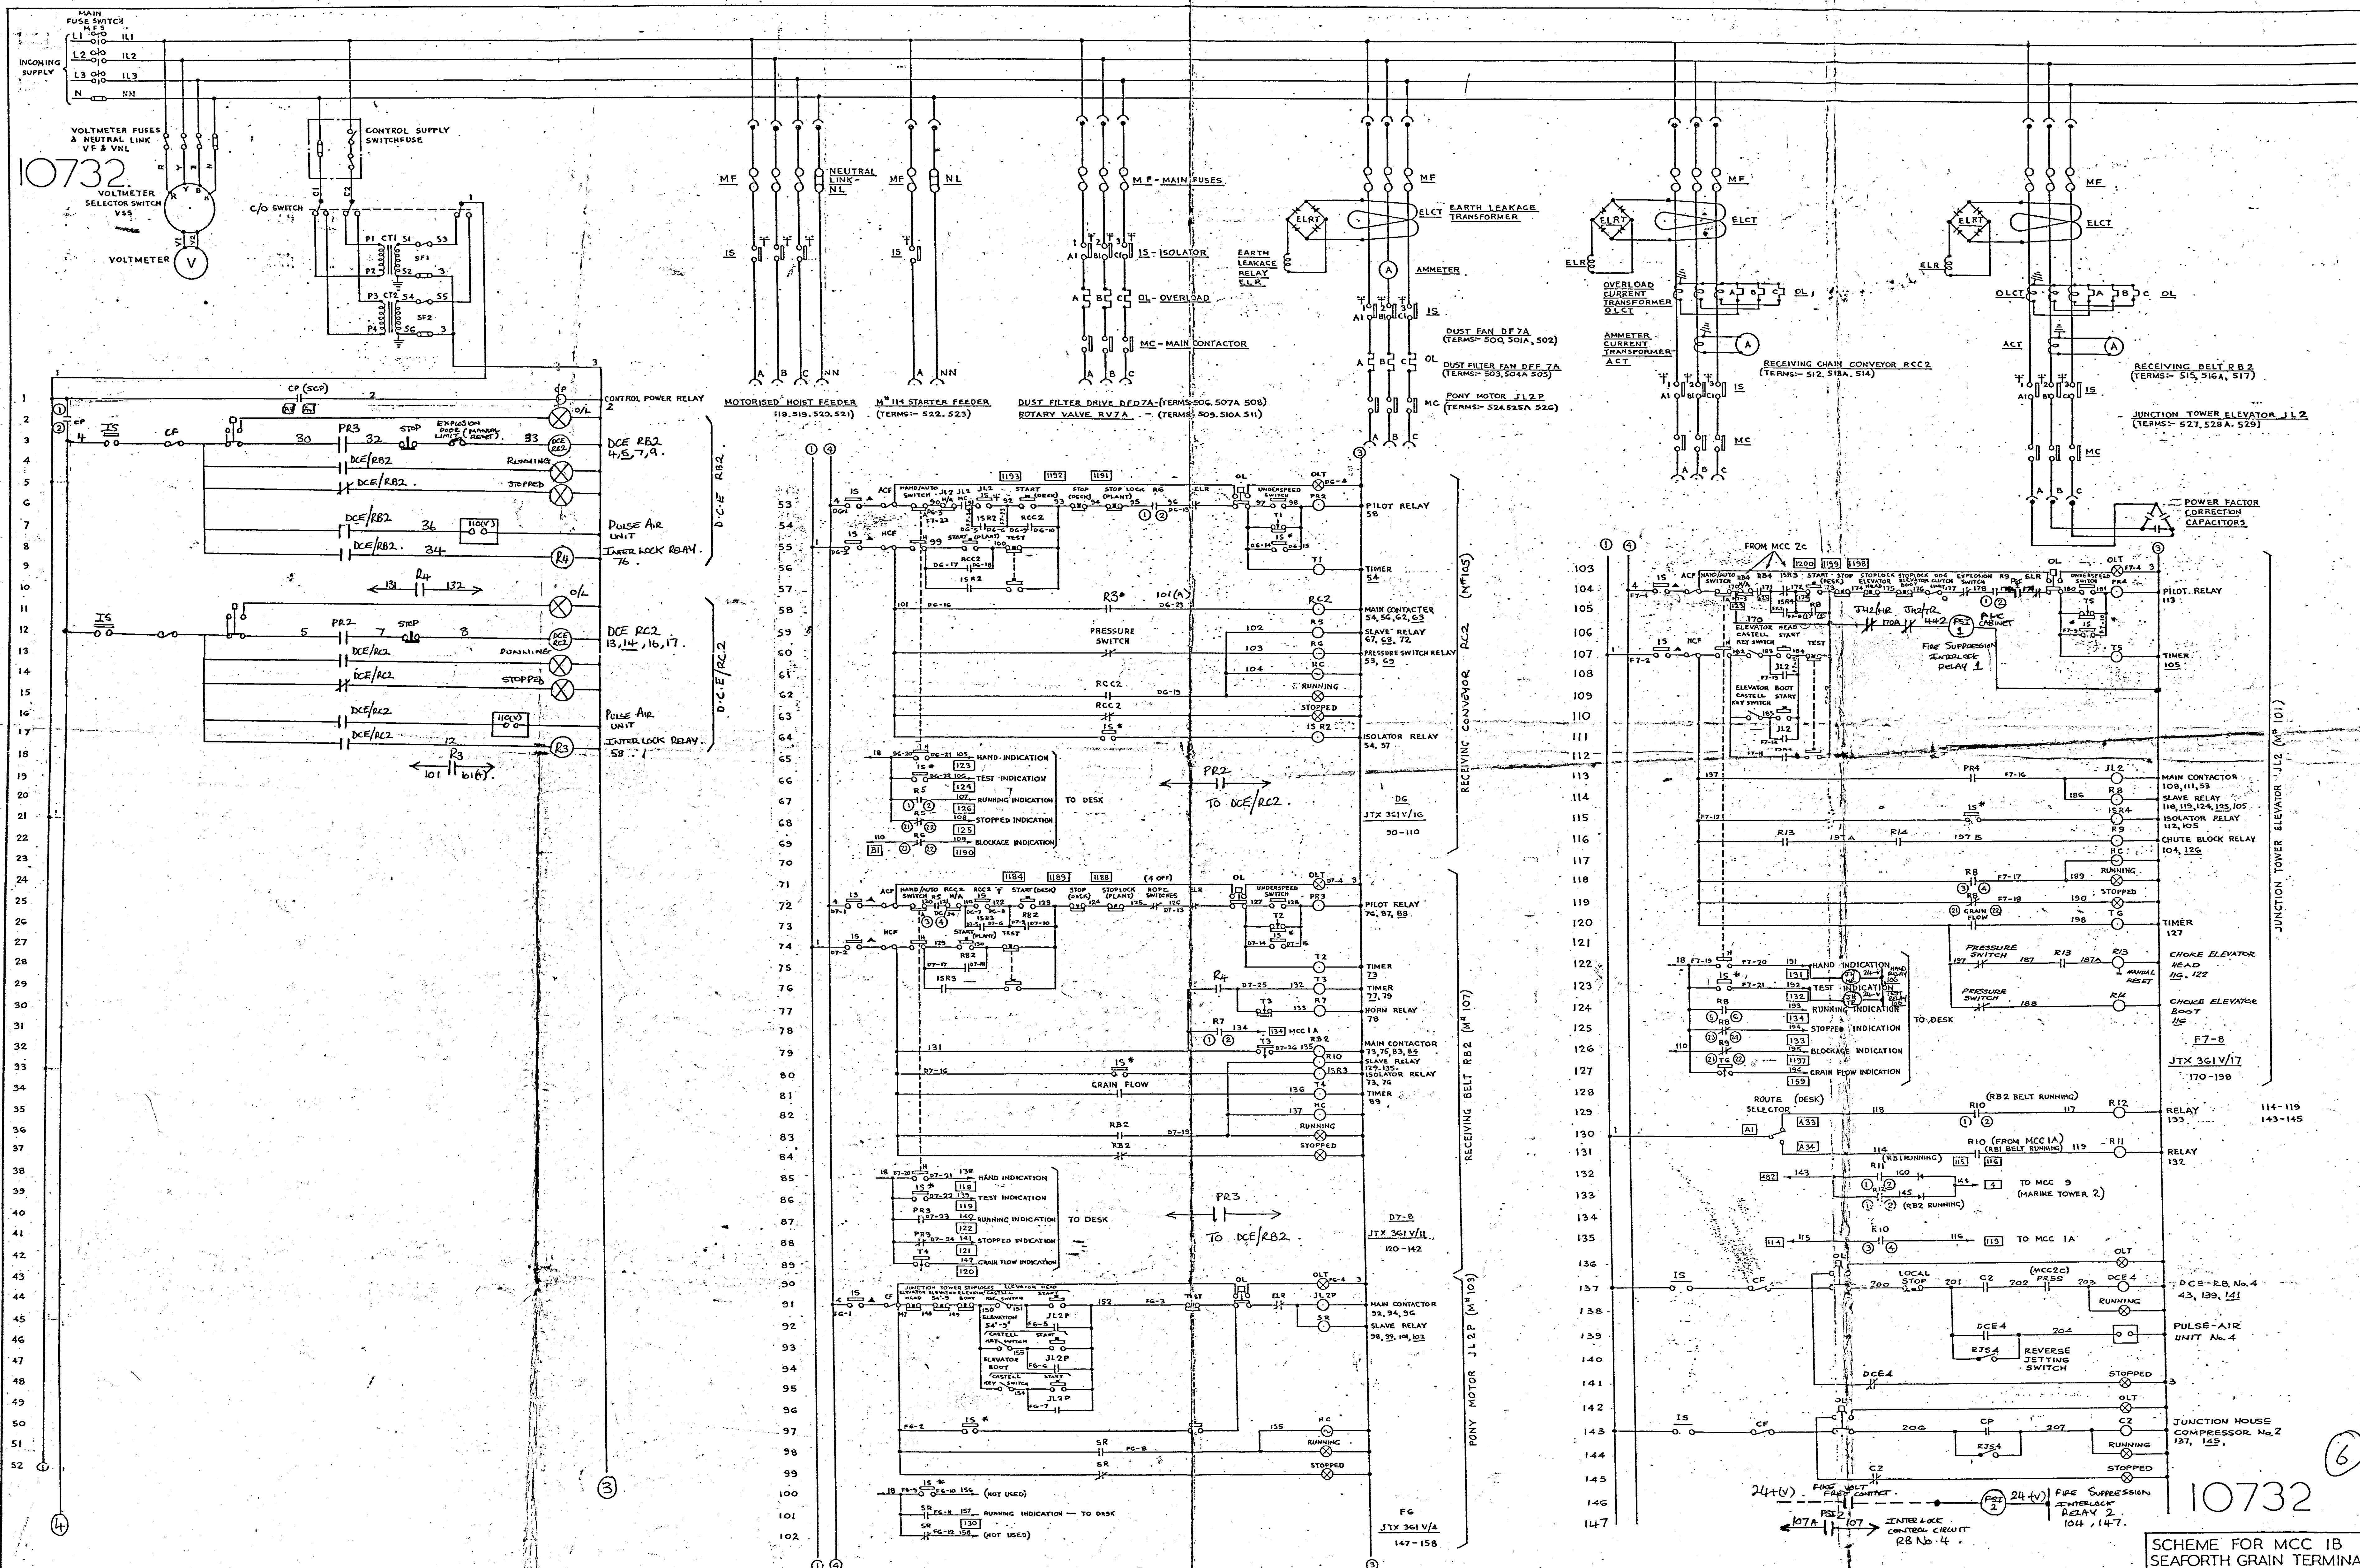

DEWHURST & PARTNER LTD.
MELBOURNE WORKS HOUNSLOW

SCHEME FOR MCCIB - SEAFORTH GRAIN TERMINAL

REVISION: 8; CONTACT R110/2 ADDED ON LINE 43.	REVISION: 7 RELAYS R11 & R12 REVERSED ORIGIN: SITE	REVISION: 6 CONNECTIONS TO MCC 9B MODIFIED ORIGIN: CUST.	REVISION: 5 DESK TERMINALS ADDED ORIGIN: I.C.D. U/4/74	REVISION: 4 MODS TO RCC2, R82 AND J1.2. ORIGIN: E.J.S.P. U/4/74
--	---	--	--	---

REVISION: 12 WIRING MISC. ORIGIN: JMS DATE: 1-1-60 ADDED: REL. DTD: 6-0 REVISION: 3 ON RB2 SUSTAINING CORRECT WAS ON M.C.	REVISION: 11 MISC. MODS. TO CHUTE BLOCK REAR REL. DTD: 4-15-60 ADDED: REL. DTD: 6-0 REVISION: 2 BLOCKAGE INDICATION REWR. MODIFIED MINOR MODS. MCB TERMINALS ORIGIN: ELS.R	REVISION: 10 NEW COMPRESSOR REL. DTD: 4-15-60 PUT FOR DIRM REL. DTD: 4-15-60 COMPRESSOR HITTER.	REVISION: 9 NEW DUST PLAN (M.C.) COMPRESSOR M/J REL. DTD: 4-15-60 M.C. 3-14-60 DATE: 5-13-60 EP DRAWN BY THOMAS DATE 10/2/71 CHECKED APPROVED BY DATE	RIGHT OF DUBHUIST & PARTNER LTD. AND MUST BE COPIED OR USED FOR MANUFACTURING PURPOSES KEY DIAG. NO EXT. DIAG. NO STX 361 AB REL. DIAG. NO JTX 361 AB PANEL LAYOUT NO MTA 361 AB
--	---	---	--	---

THE DESIGN AND MANUFACTURING
INFORMATION CONTAINED IN
THIS DRAWING IS THE EXCLUSIVE
RIGHT OF DEWHURST & PARTNER
LTD. AND MUST NOT BE COPIED
OR USED FOR MANUFACTURING
PURPOSES

SCHEME FOR MCC IB
SEAFORTH GRAIN TERMINAL

DTX 361 AB

DTX 361 AB