
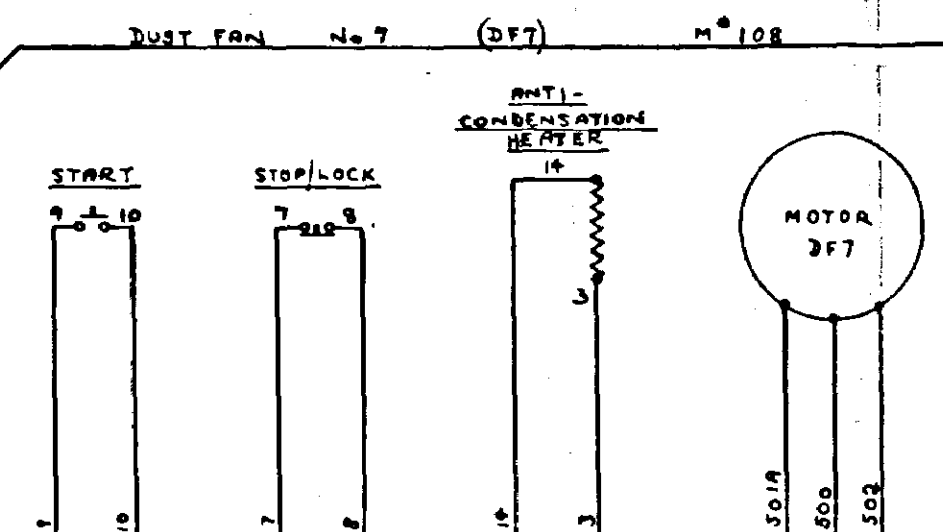
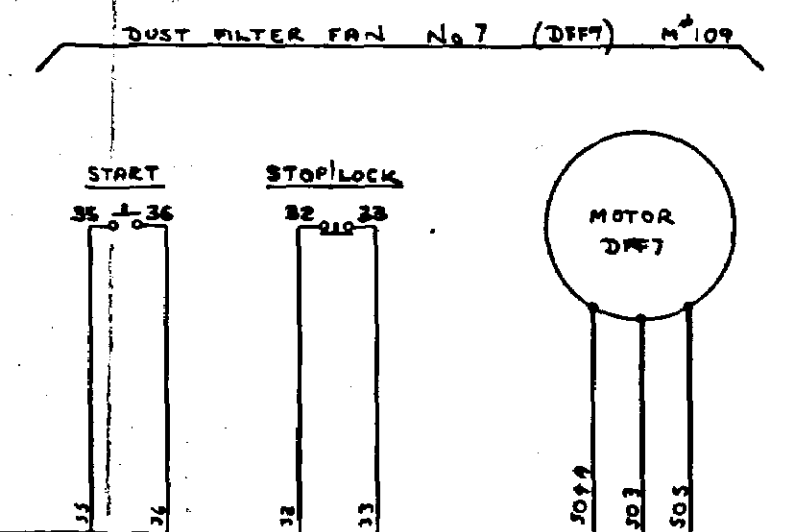
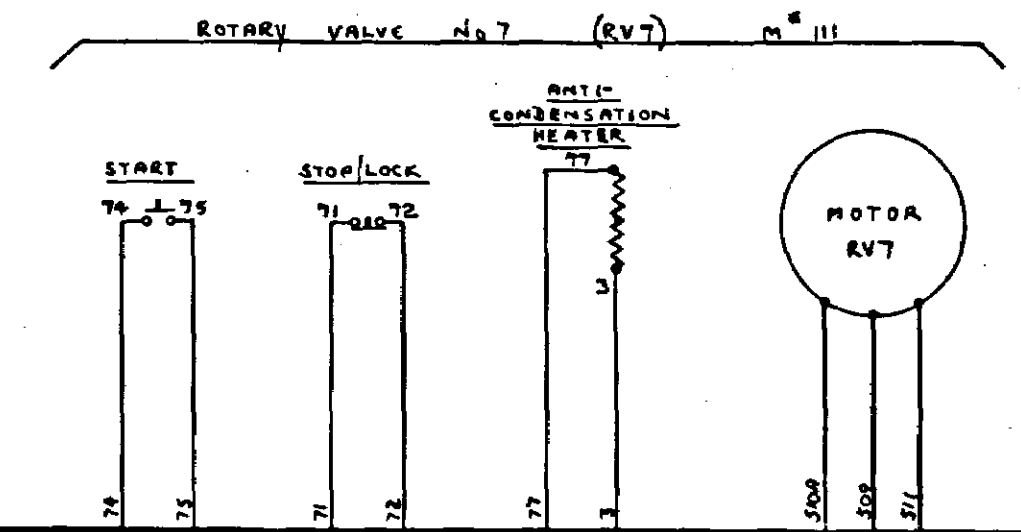
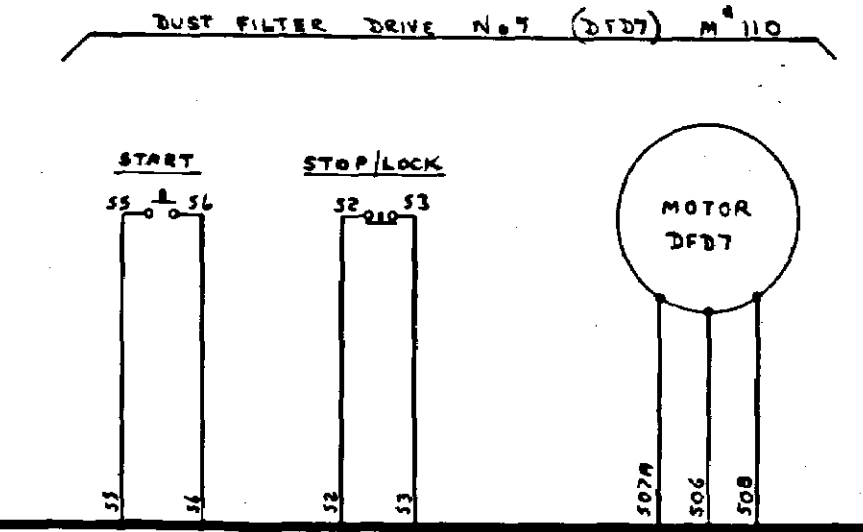
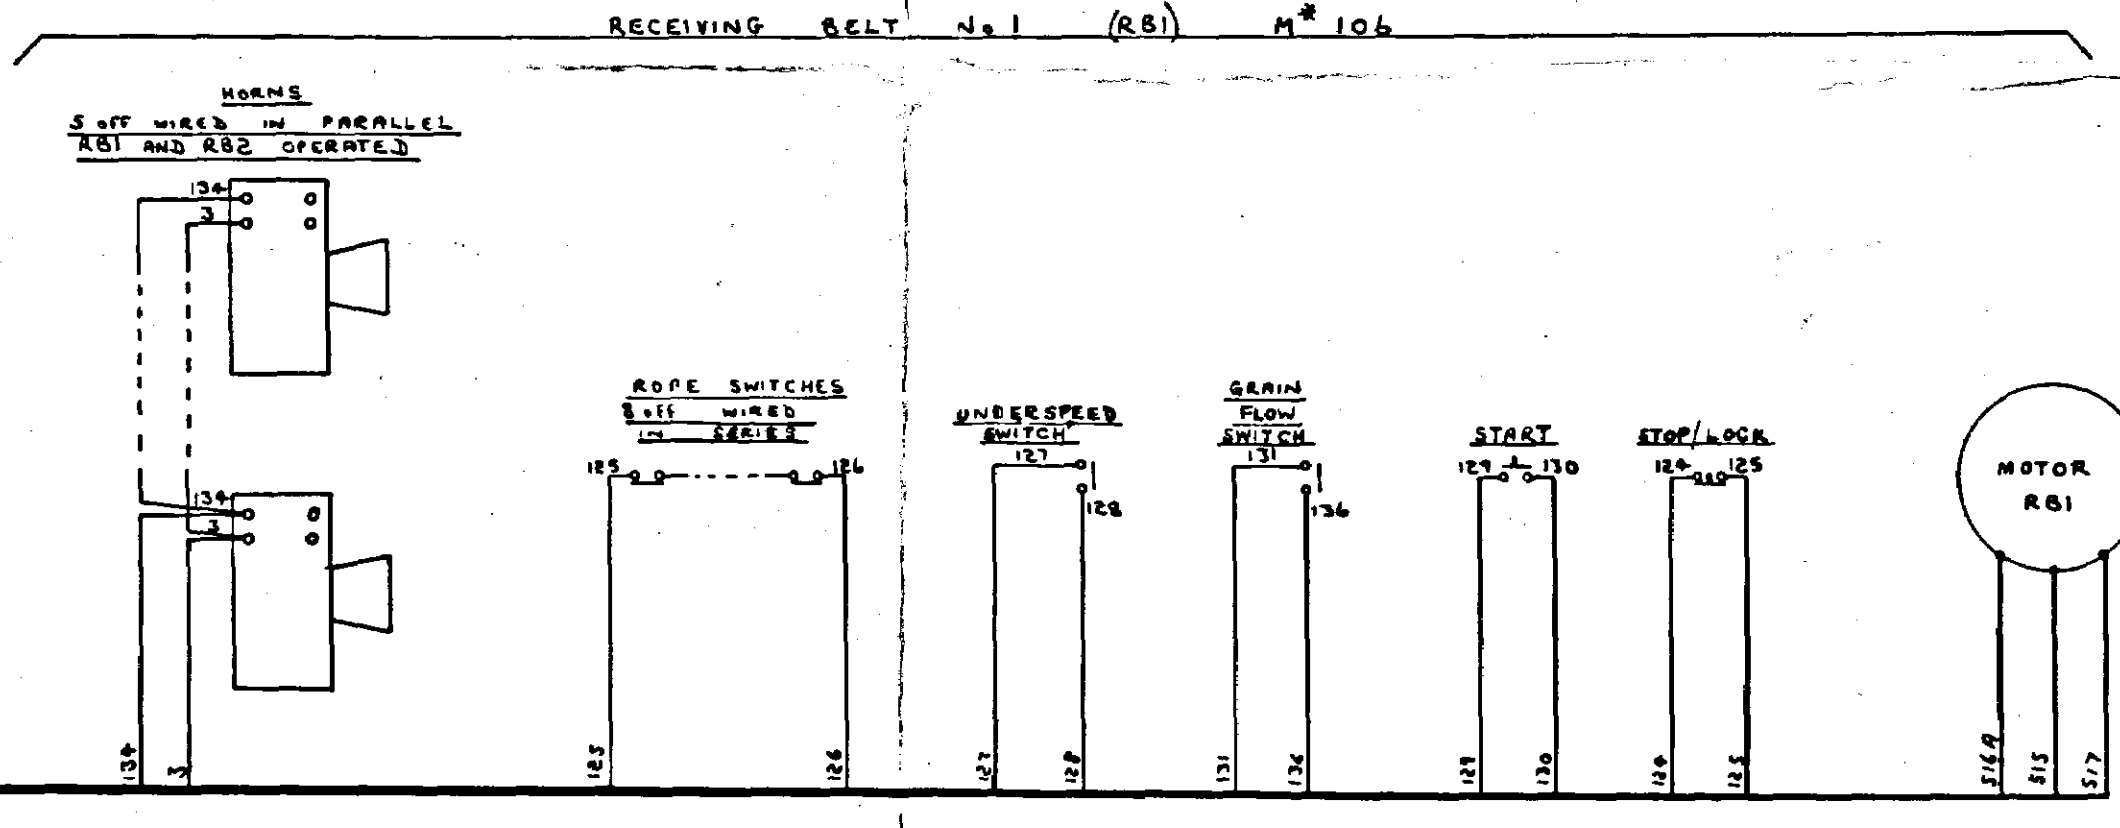
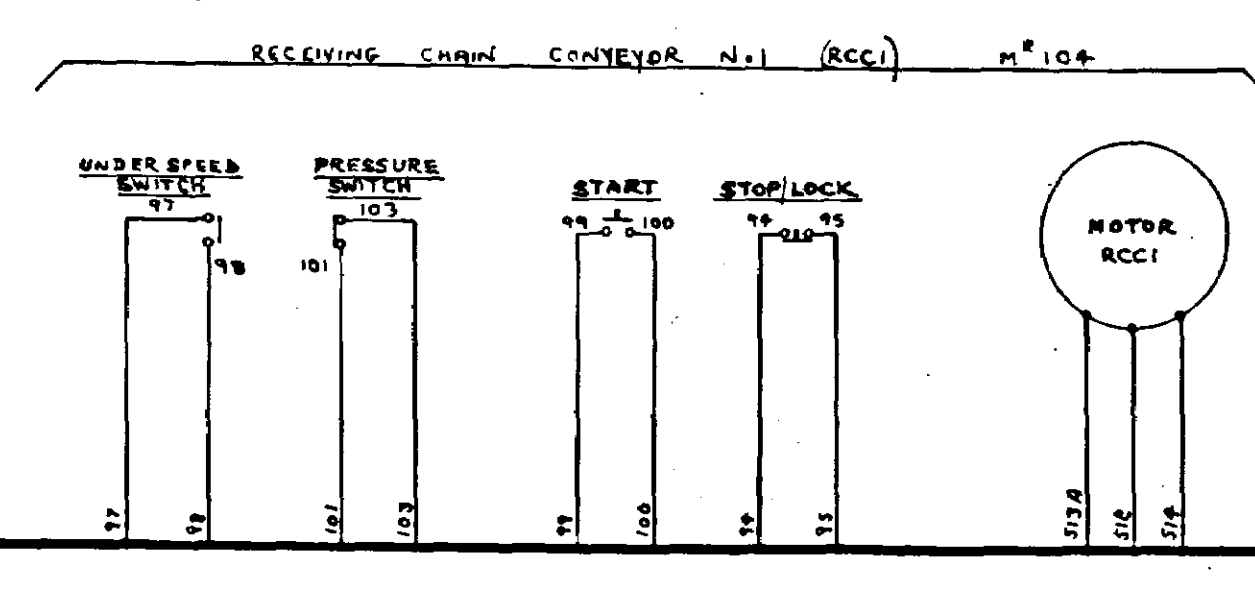
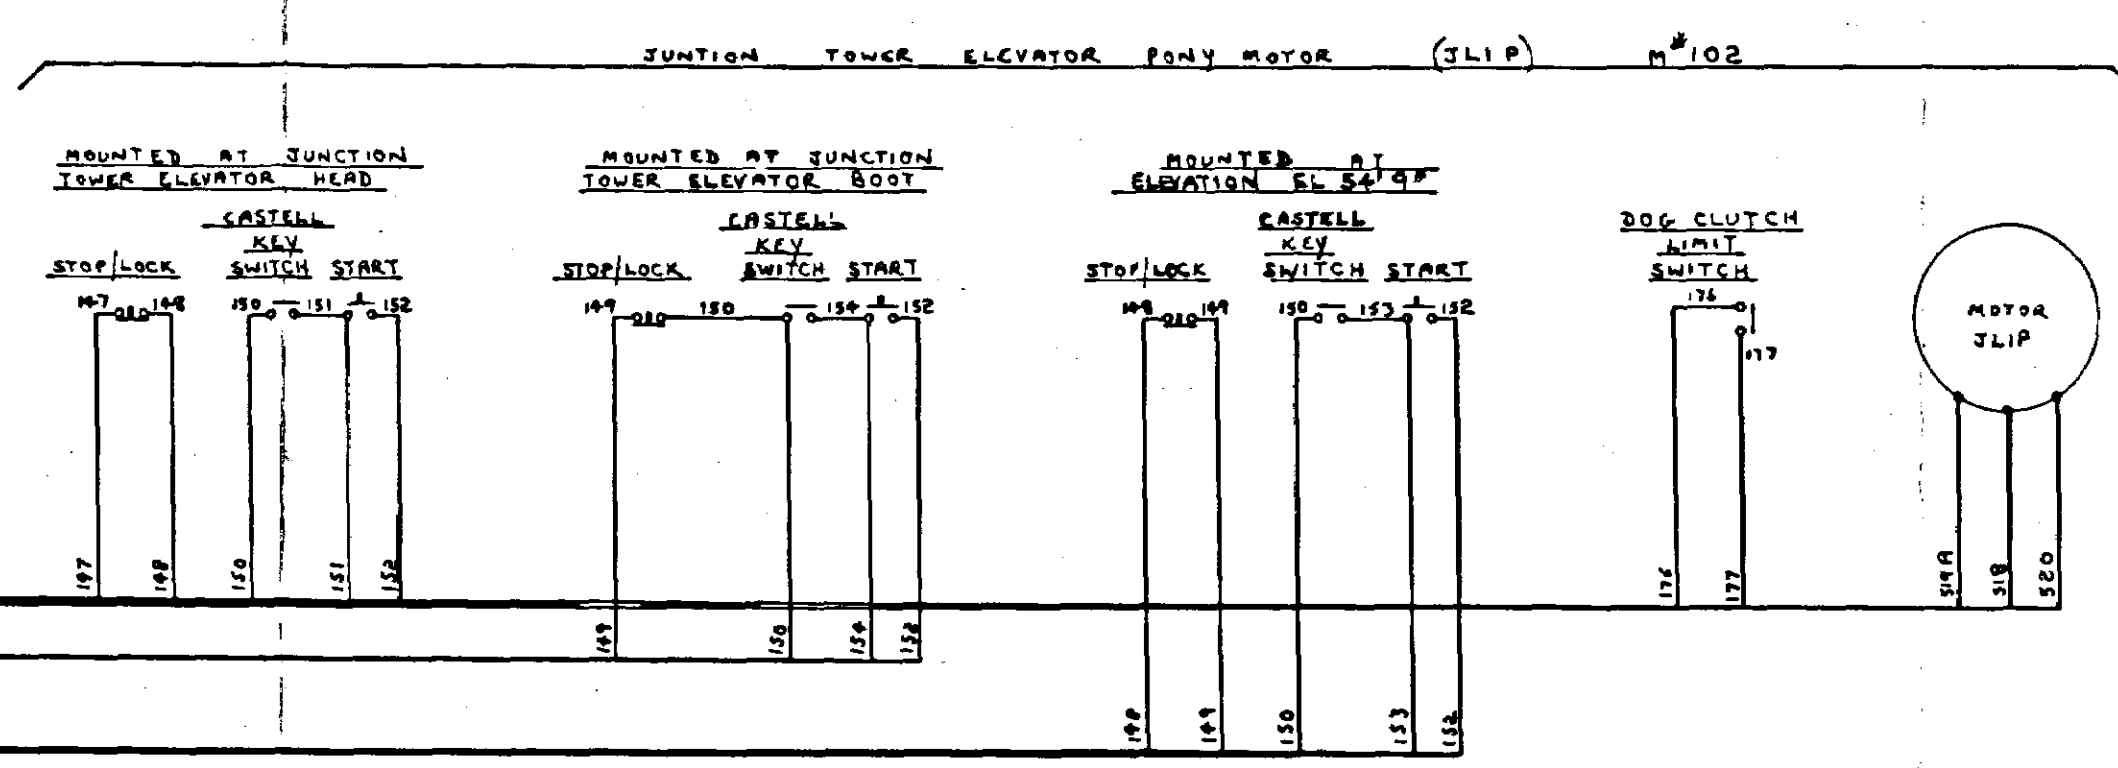
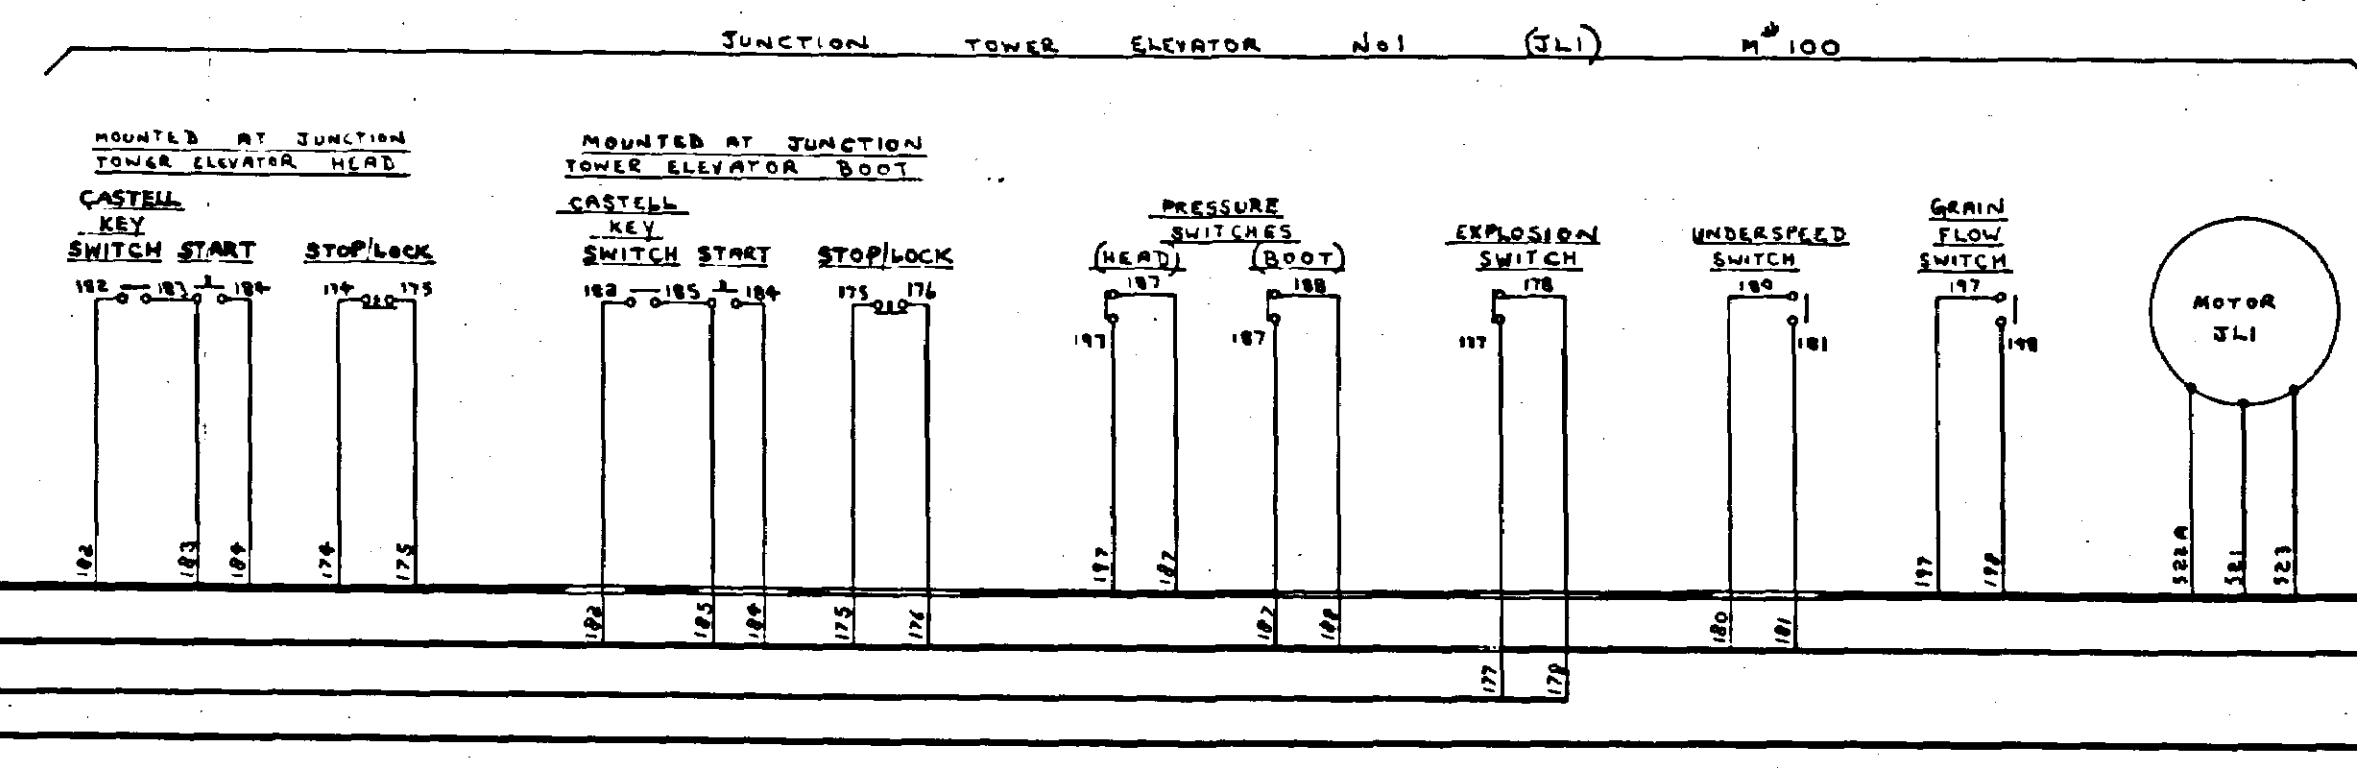


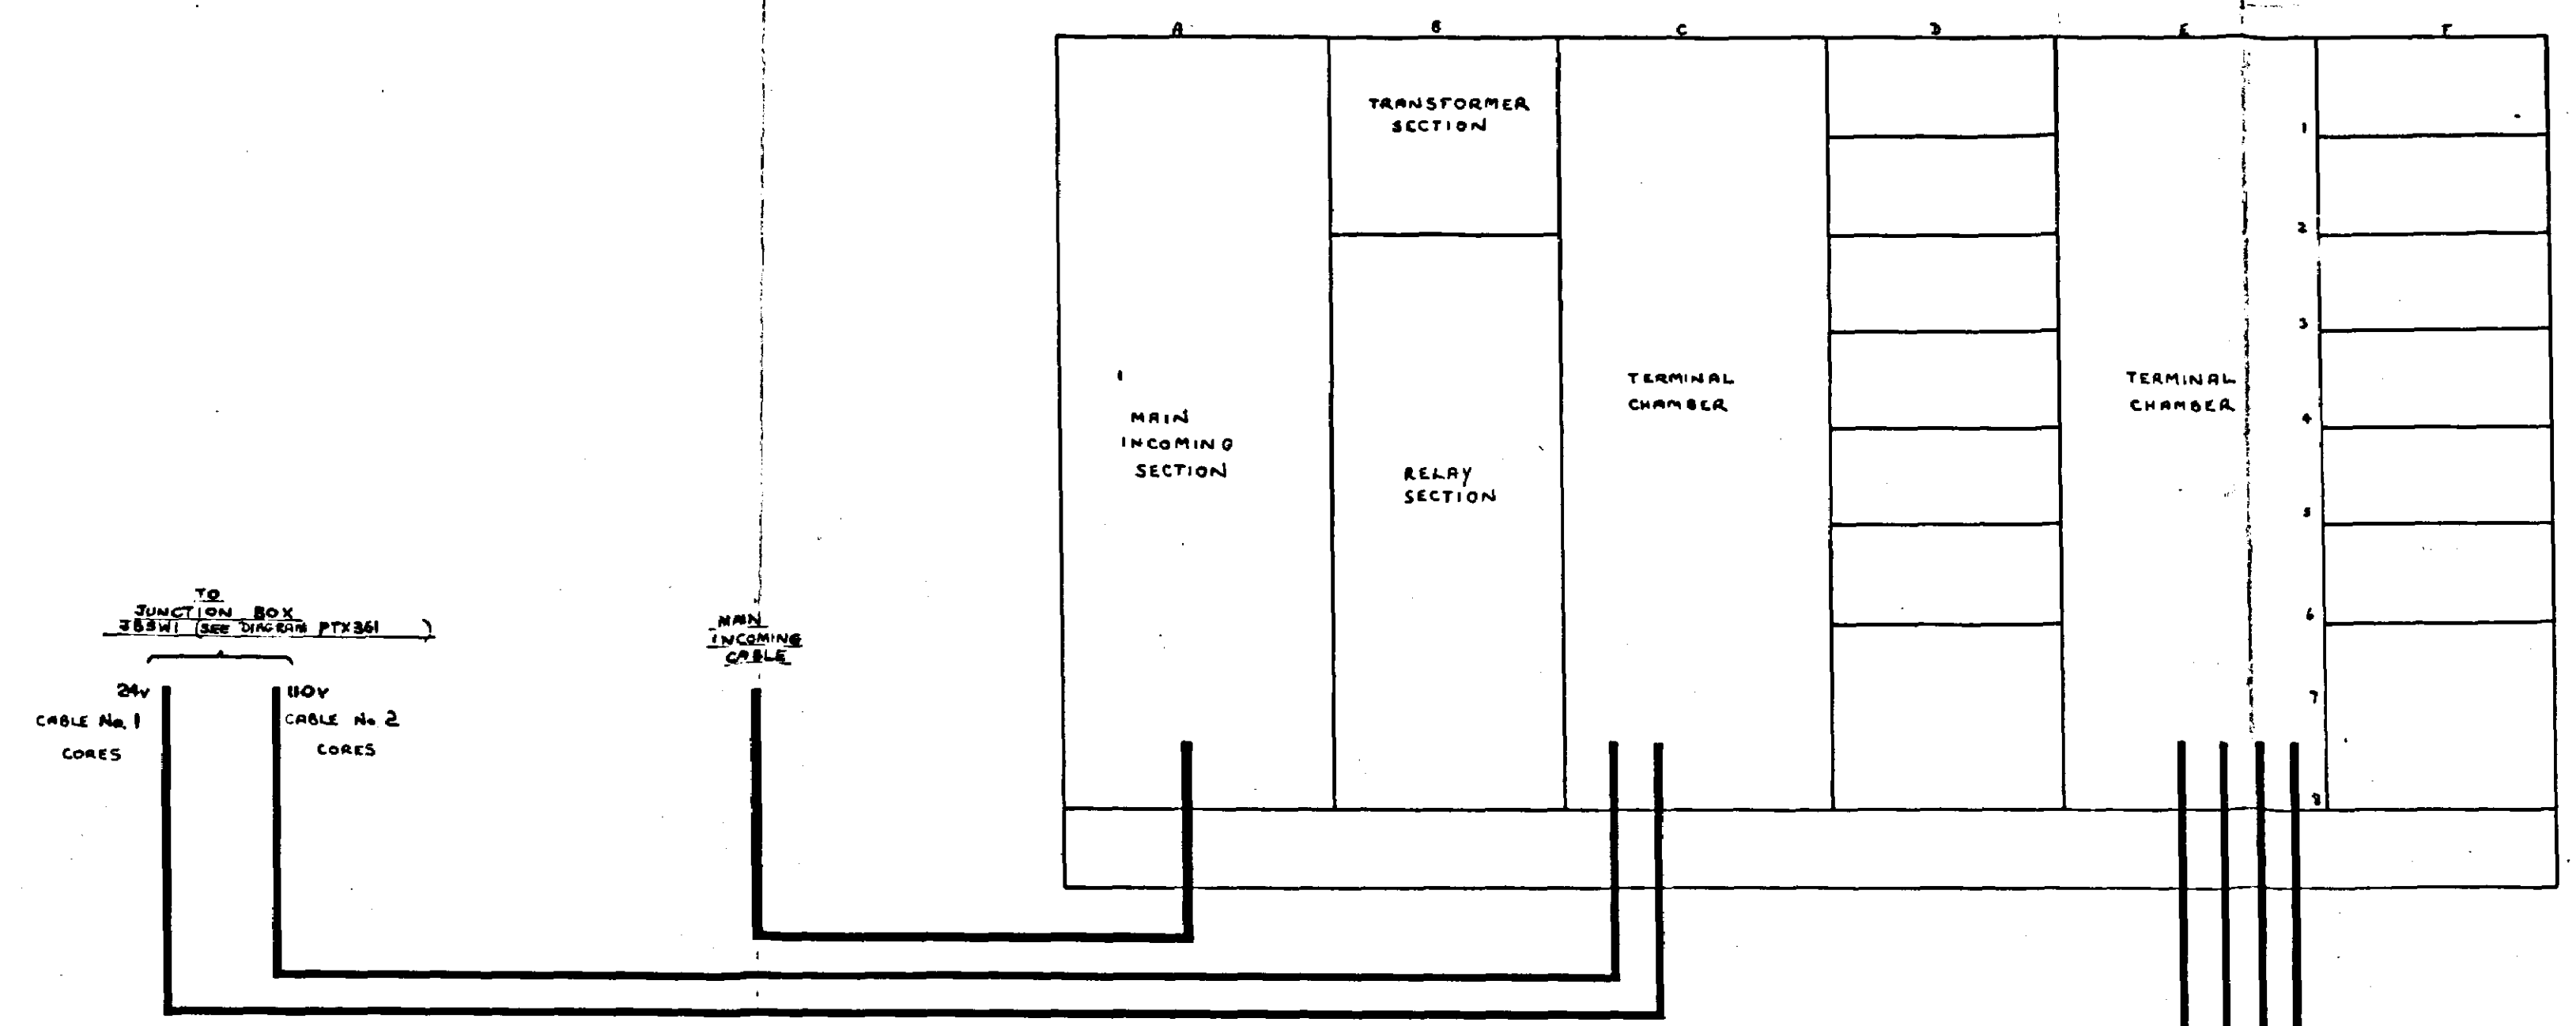

NUMBERS ADJACENT TO LOOMS
INDICATE TERMINAL DESIGNATION
ONLY - NOT WIRE NUMBERS

DEWHURST & PARTNER LTD.
MELBOURNE WORKS HOUNSLOW

TITLE
EXTERNAL WIRING DIAGRAM FOR MCCA - SEAFORTH GRAIN TERMINAL

REVISION: REVISION: REVISION: REVISION: REVISION:
ORIGIN: ORIGIN: ORIGIN: ORIGIN: ORIGIN:

DRAWN BY: 1-2-71
CHECKED BY:
APPROVED BY:
DATE:

Superseded: Issue 11 Revision 10.
EXTERNAL WIRING DIAGRAM FOR MCCA - SEAFORTH GRAIN TERMINAL

THE DESIGN AND MANUFACTURING INFORMATION CONTAINED IN THIS DRAWING IS THE EXCLUSIVE RIGHT OF DEWHURST & PARTNER LTD. AND MUST NOT BE COPIED OR USED FOR MANUFACTURING PURPOSES	ISSUE 1	STX361AA
		STX361AA

11169