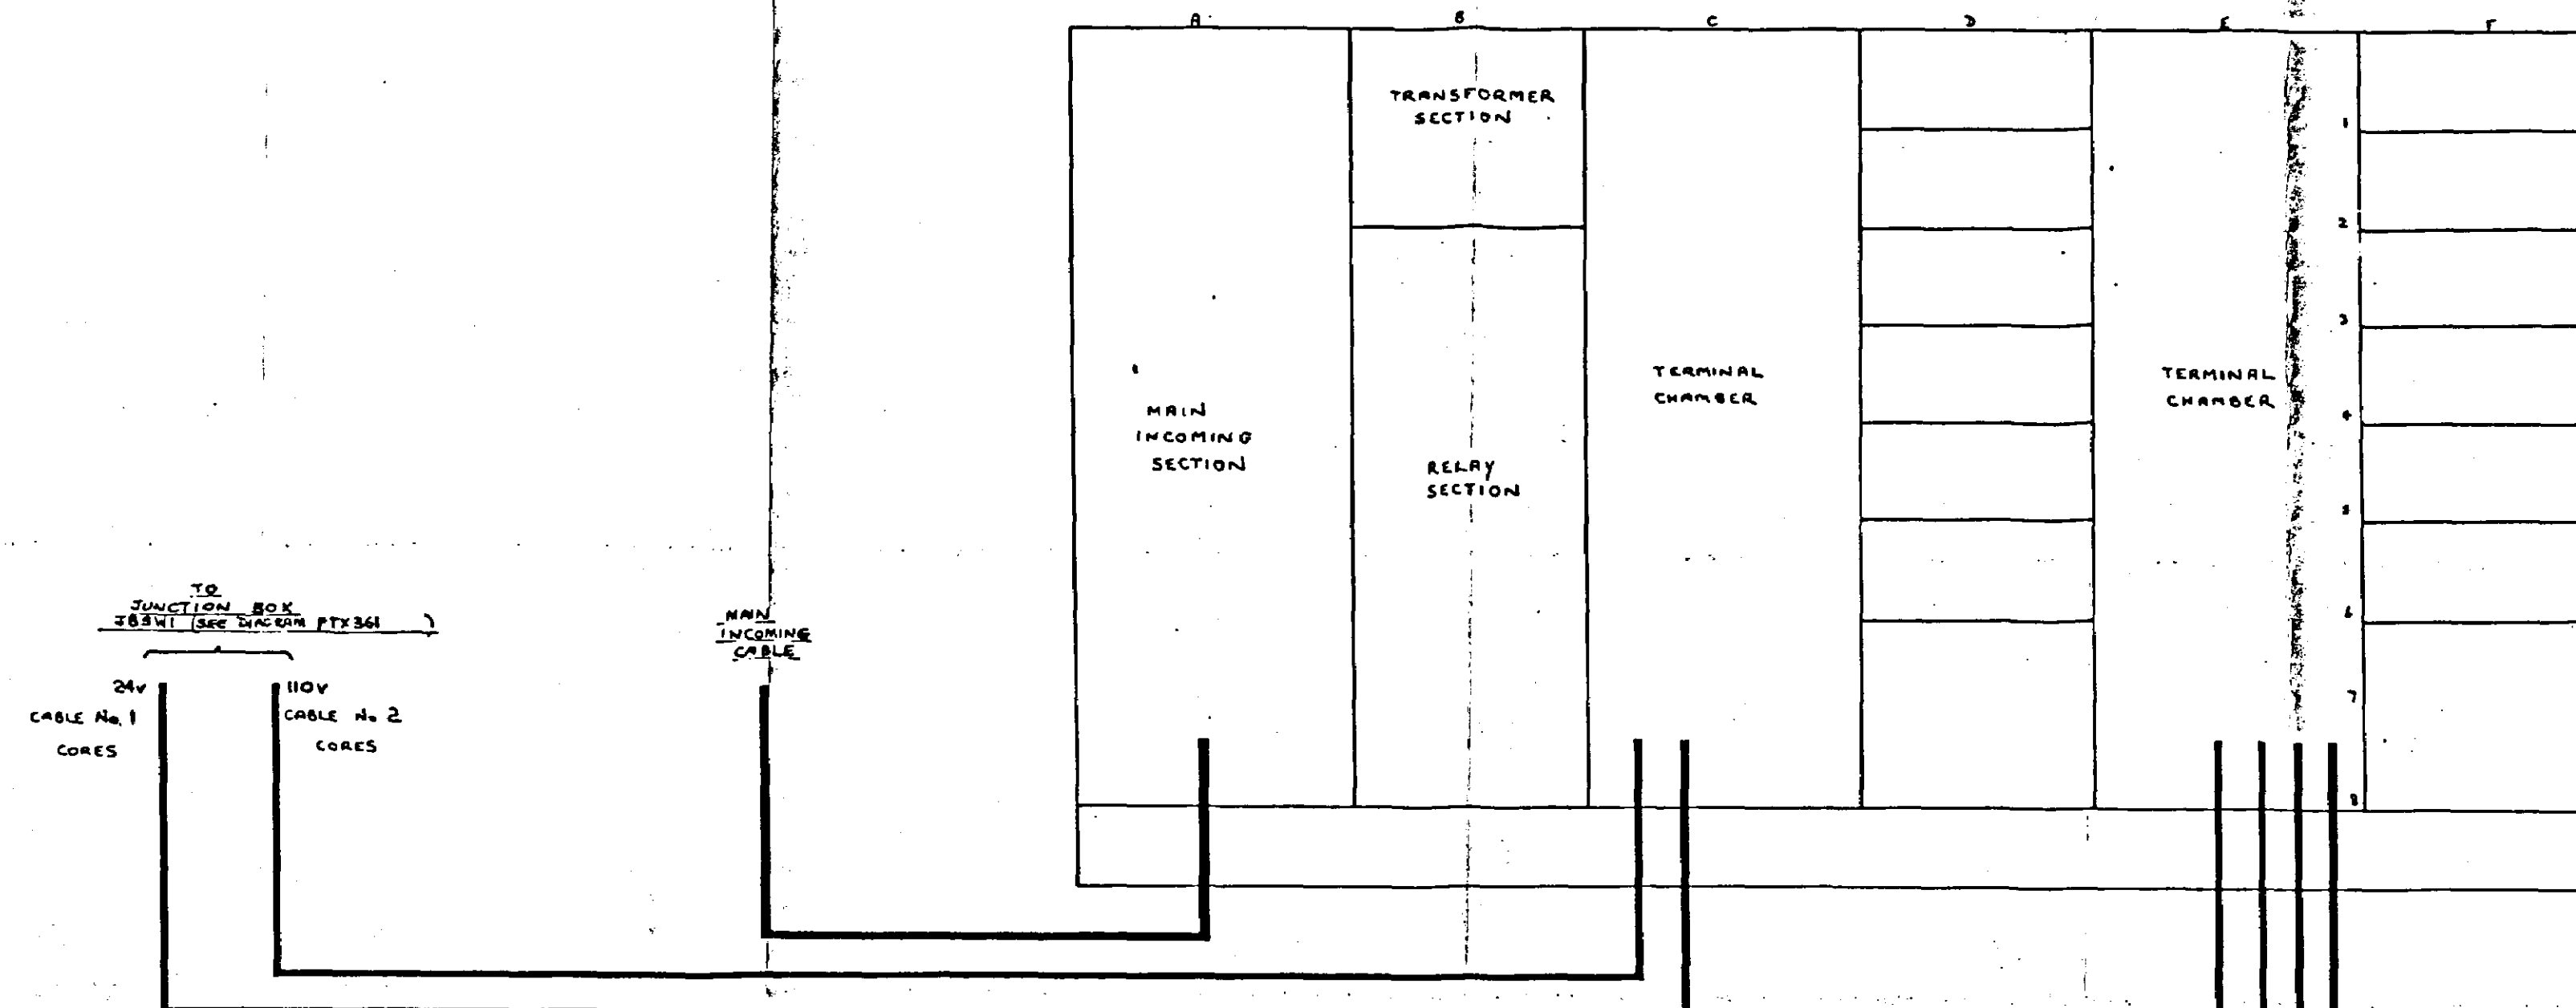


NUMBERS ADJACENT TO LOOMS INDICATE TERMINAL DESIGNATION ONLY - NOT WIRE NUMBERS

DEWHURST & PARTNER LTD.
MELBOURNE WORKS HOUNSLOW

TITLE
EXTERNAL WIRING DIAGRAM FOR MCCIA - SEAFORTH GRAIN TERMINAL

REVISION: / / SGD
ORIGIN: / / SGD
REVISION: / / SGD
ORIGIN: / / SGD
REVISION: / / SGD
ORIGIN: / / SGD
REVISION: / / SGD
ORIGIN: / / SGD

DRAWN BY
DATE
CHECKED BY
APPROVED BY
DATE

EXTERNAL WIRING DIAGRAM FOR MCCIA - SEAFORTH GRAIN TERMINAL

THE DESIGN AND MANUFACTURING INFORMATION CONTAINED IN THIS DRAWING IS THE EXCLUSIVE RIGHT OF DEWHURST & PARTNER LTD. AND MUST NOT BE COPIED OR USED FOR MANUFACTURING PURPOSES.

ISSUE 1

STX36IAA

STX36IAA

PANEL LAYOUT No. H736100

11169