


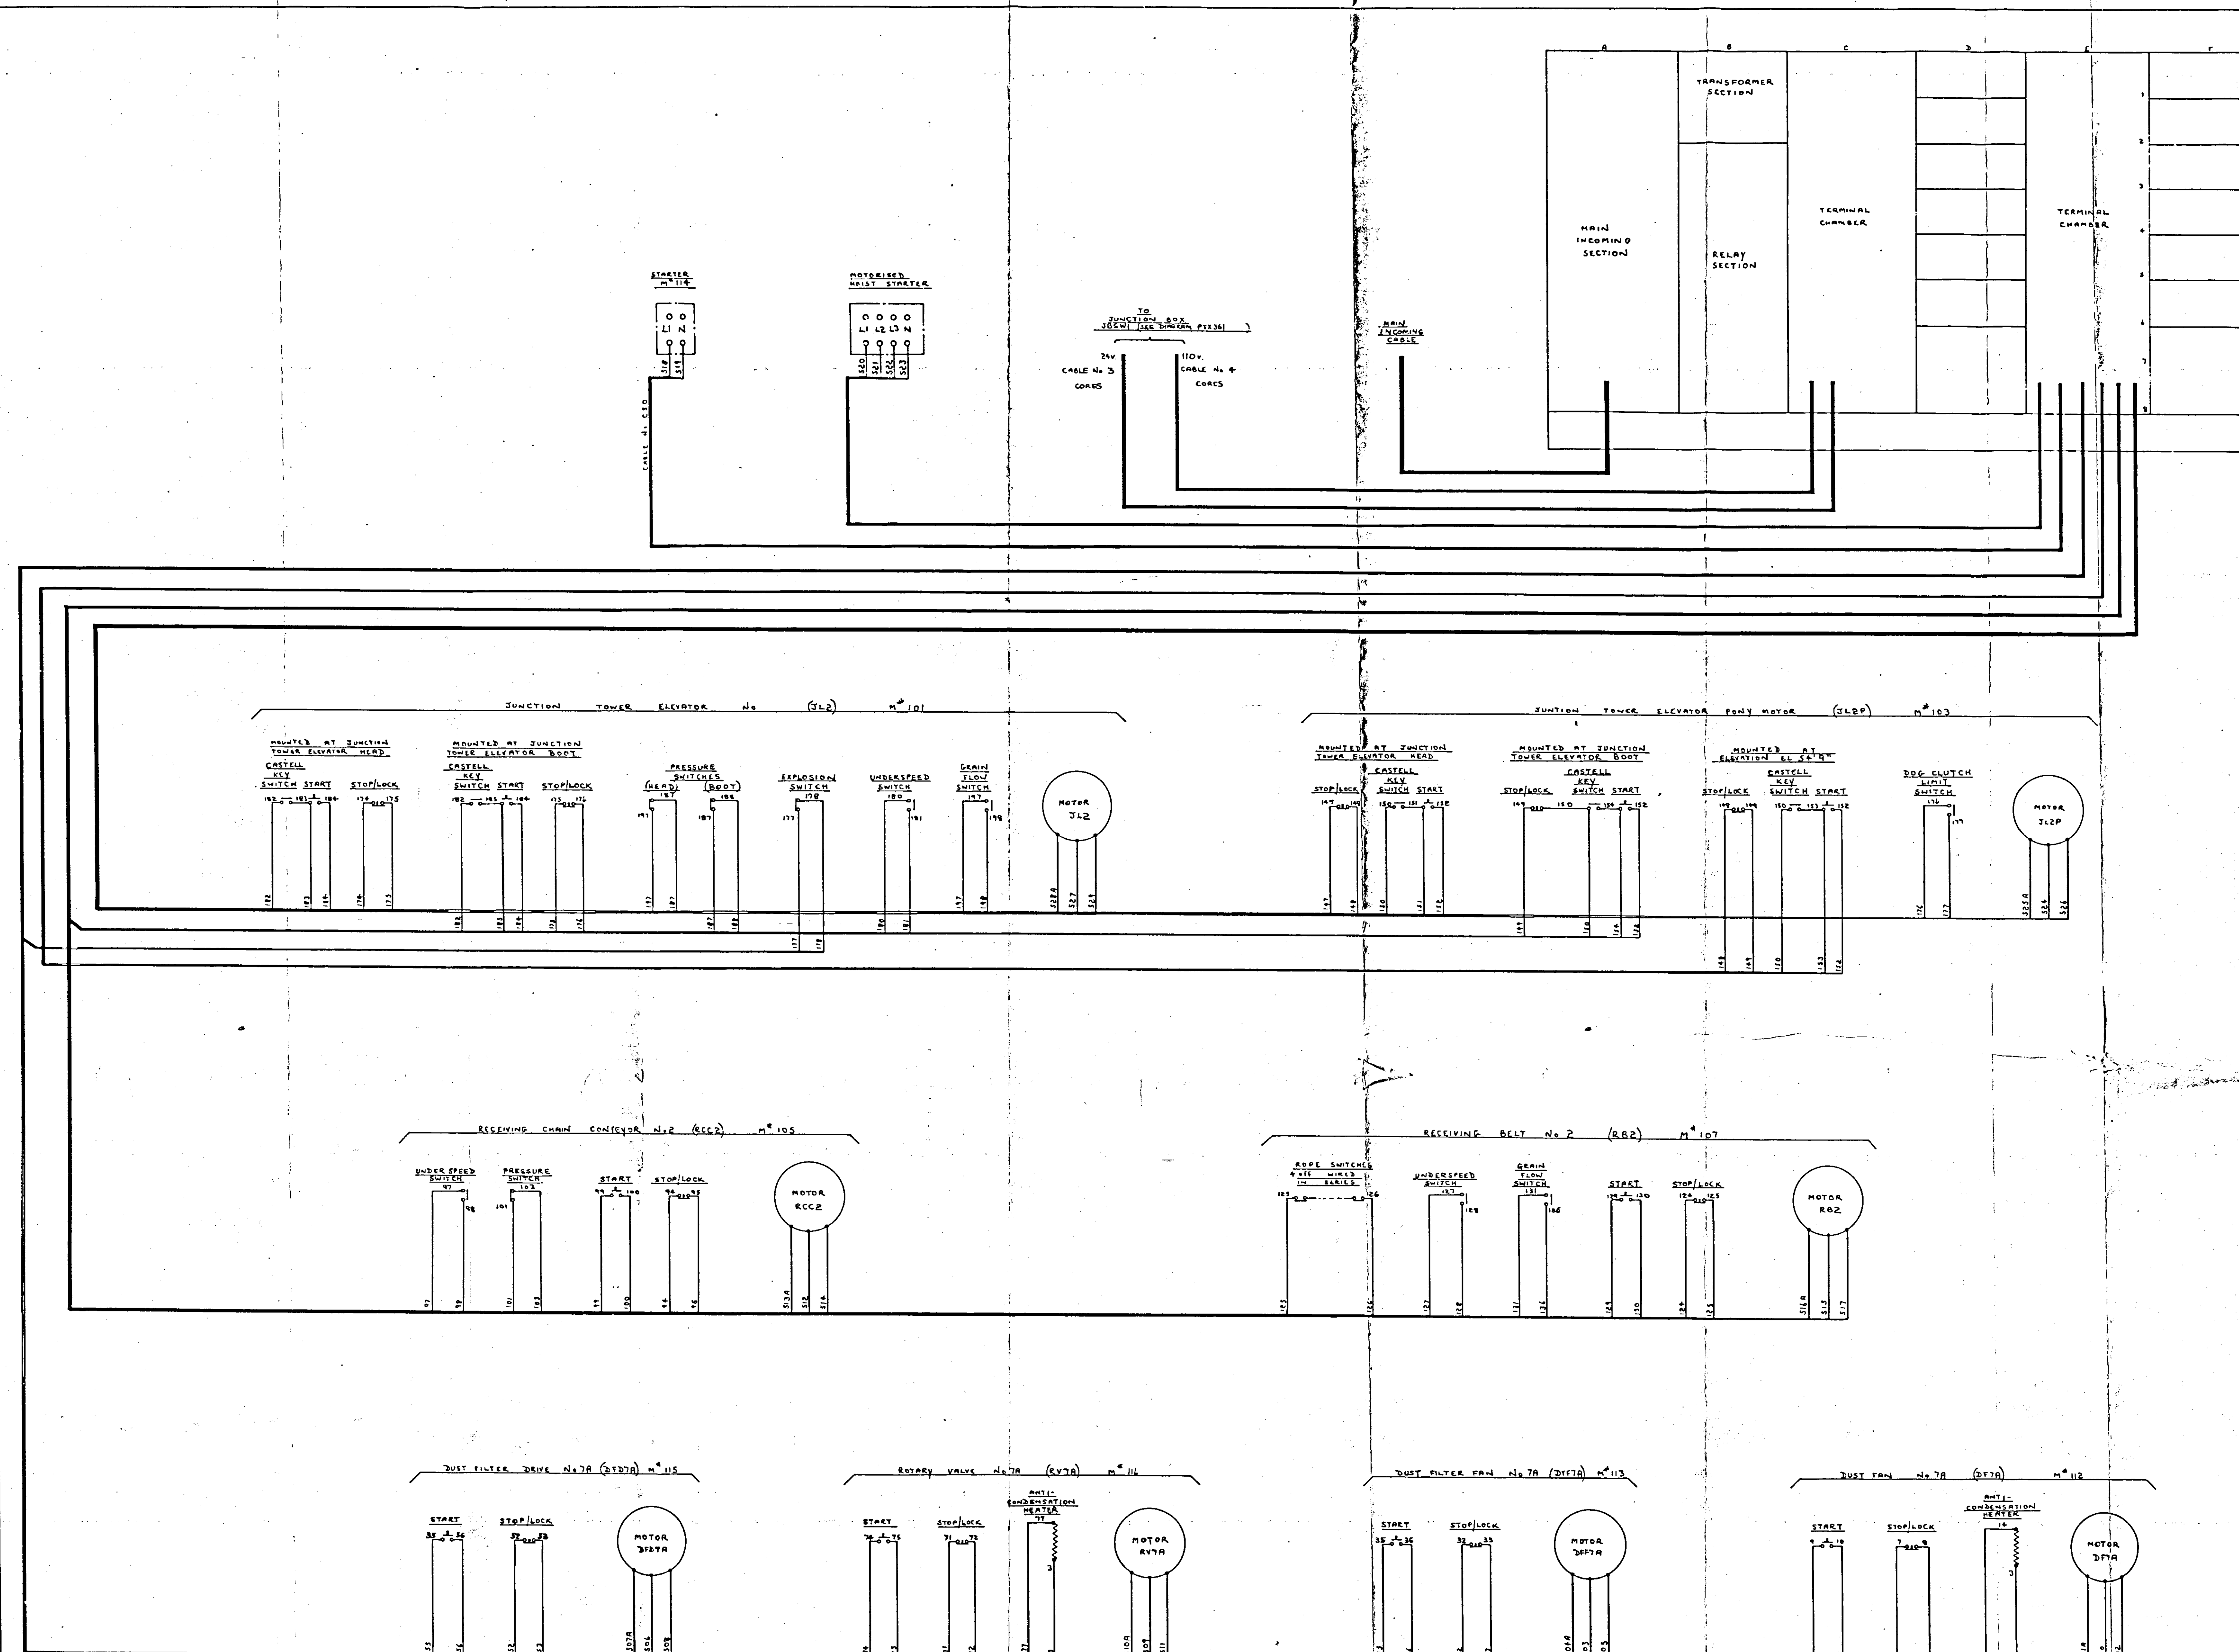

2

11170

DEWHURST & PARTNER LTD.
MELBOURNE WORKS HOUNSLOW

TITLE:
EXTERNAL WIRING DIAGRAM FOR MCCIB - SEAFORTH GRAIN TERMINAL

REVISION:	REVISION:	REVISION:	REVISION:	REVISION:
ORIGIN:	ORIGIN:	ORIGIN:	ORIGIN:	ORIGIN:
1 / 1 SGD	1 / 1 SGD	1 / 1 SGD	1 / 1 SGD	1 / 1 SGD

DRAWN BY
DATE
CHECKED BY
APPROVED BY
DATE

EXTERNAL WIRING DIAGRAM FOR MCCIB - SEAFORTH GRAIN TERMINAL

THE DESIGN AND MANUFACTURING INFORMATION CONTAINED IN THIS DRAWING IS THE EXCLUSIVE RIGHT OF DEWHURST & PARTNER LTD. AND MUST NOT BE COPIED OR USED FOR MANUFACTURING PURPOSES.	ISSUE
KEY DIAG. No.	STX361AB
EXT. DIAG. No.	
REL. DIAG. No.	
PANEL LAYOUT No.	STX361 AB