







10729

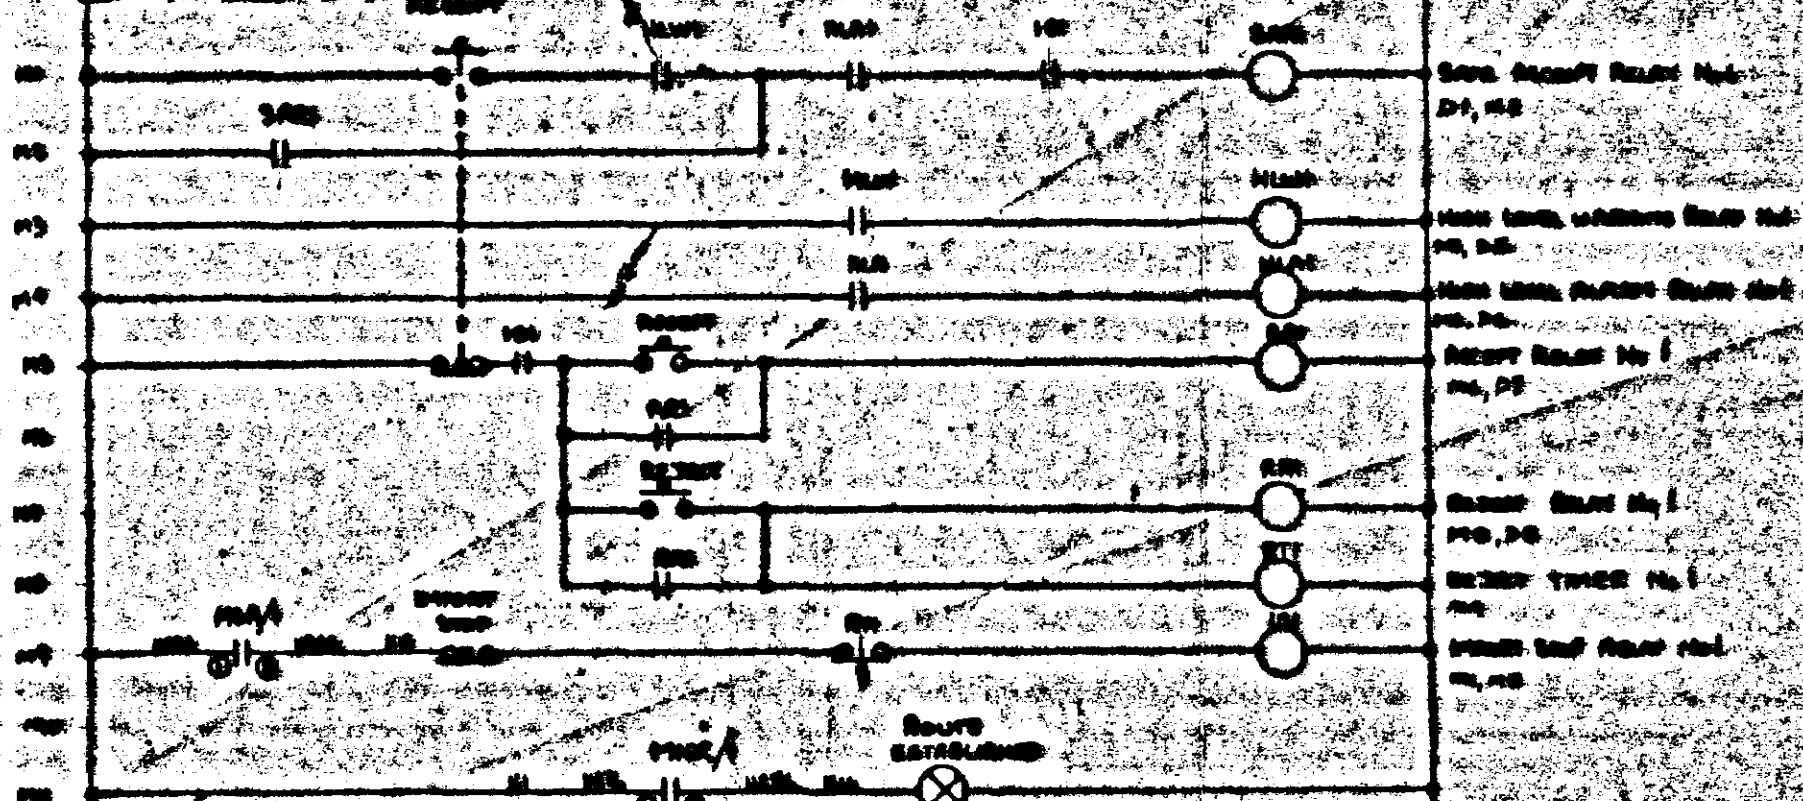

EQUIPMENT AT MILL 2 (ALLIED)

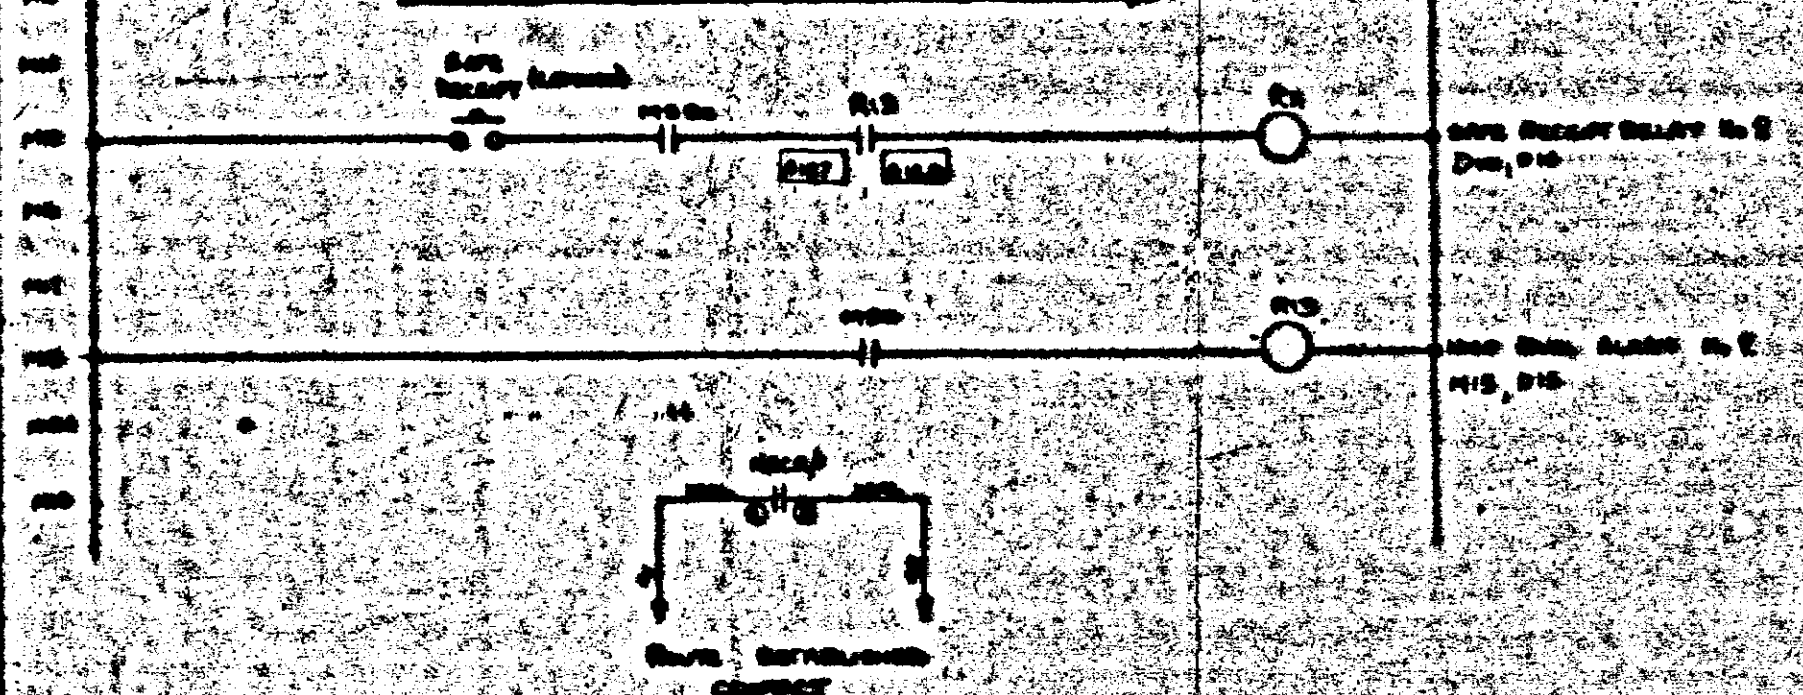

EQUIPMENT AT S.C.P.

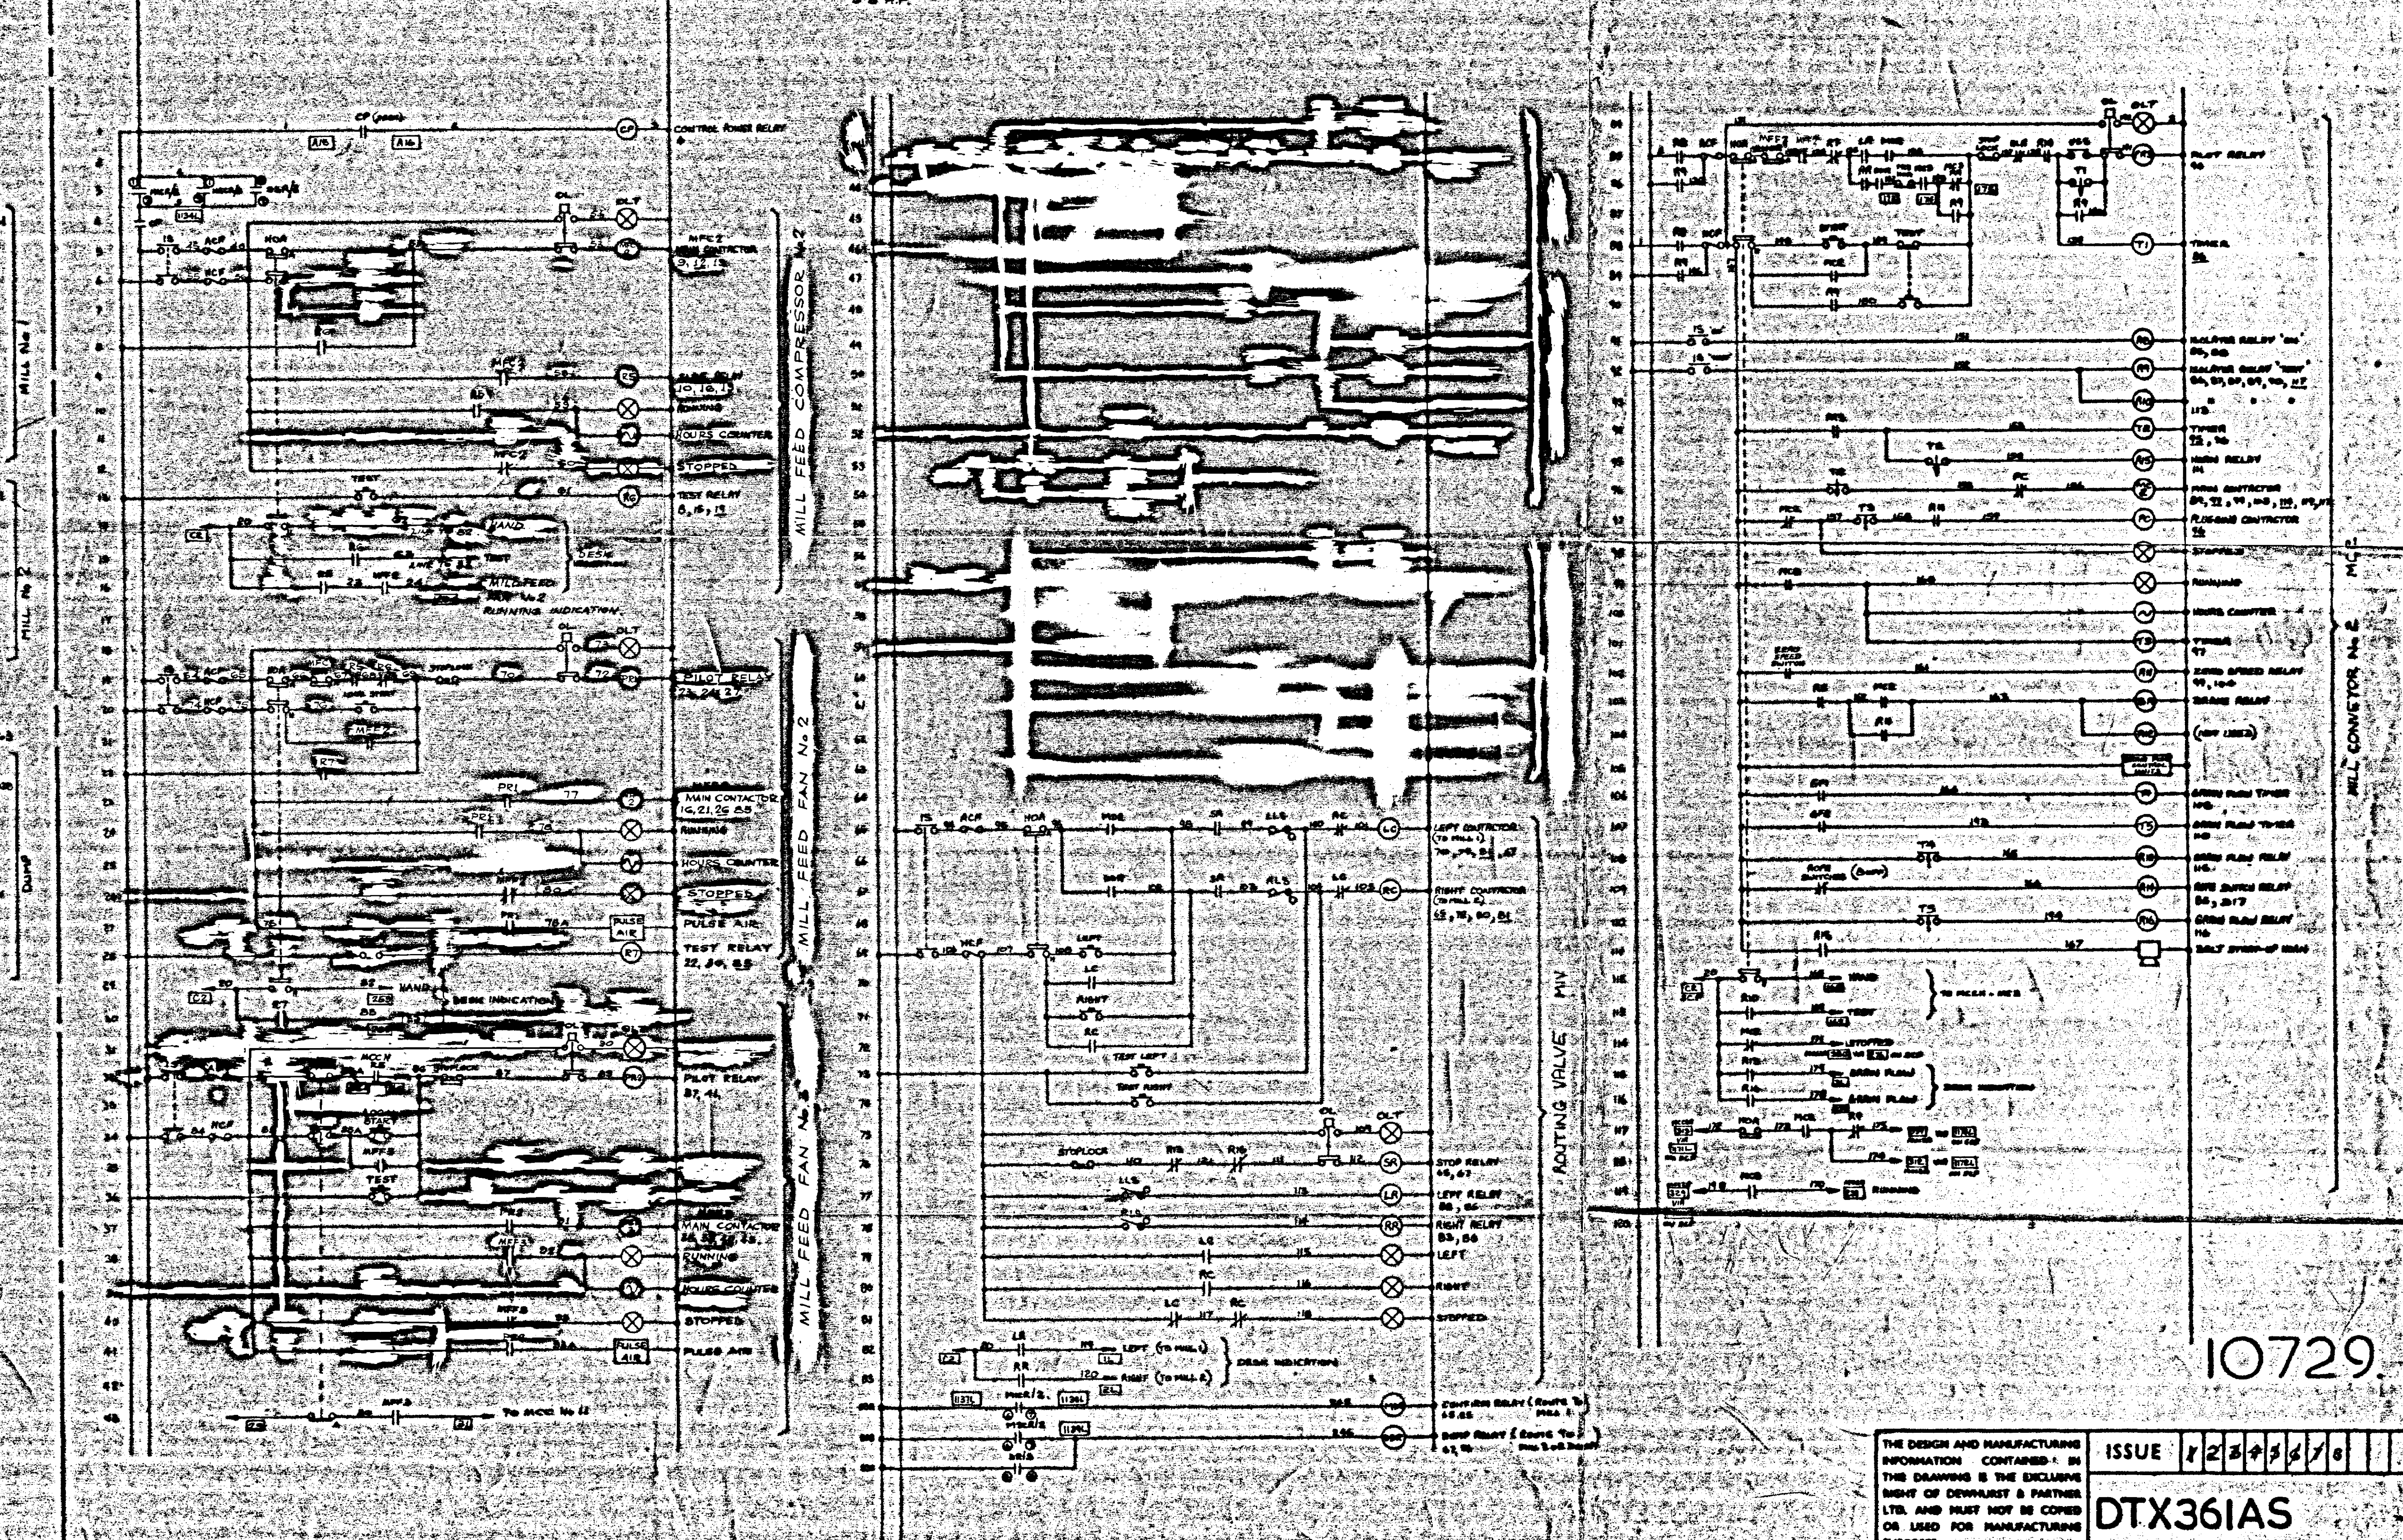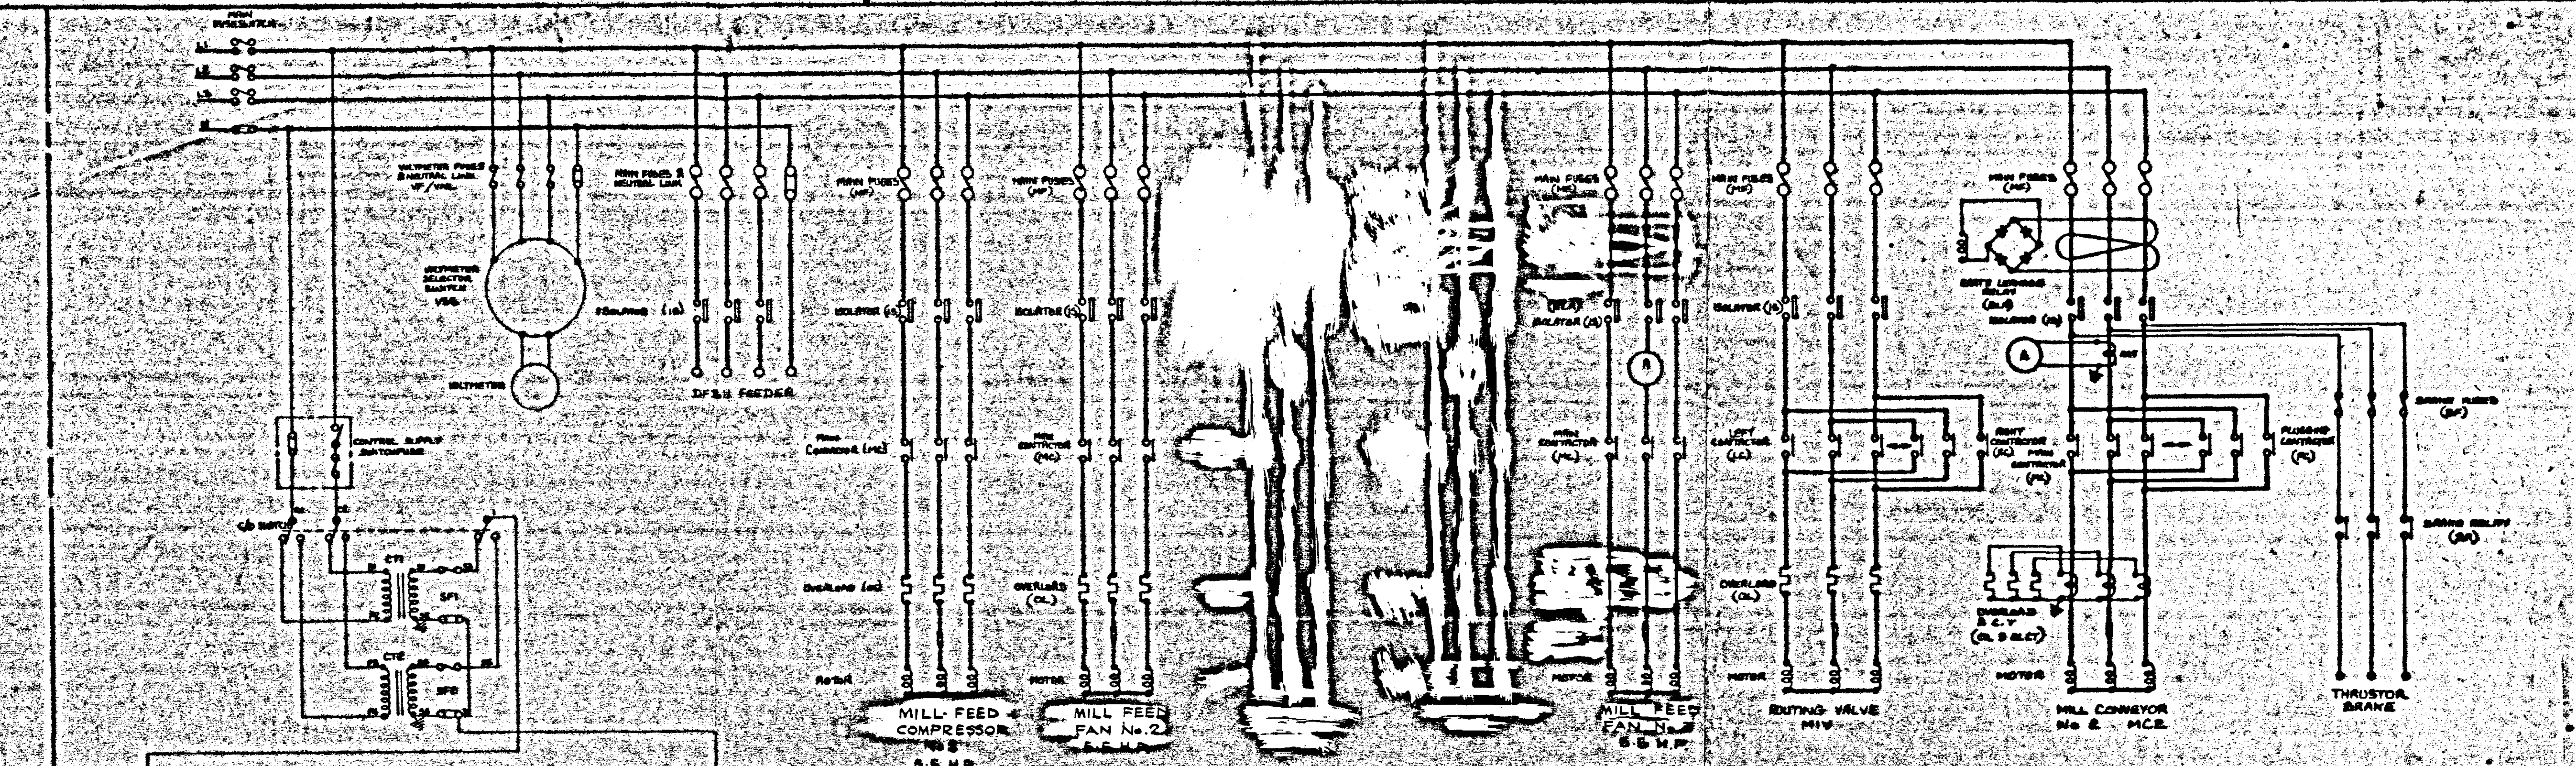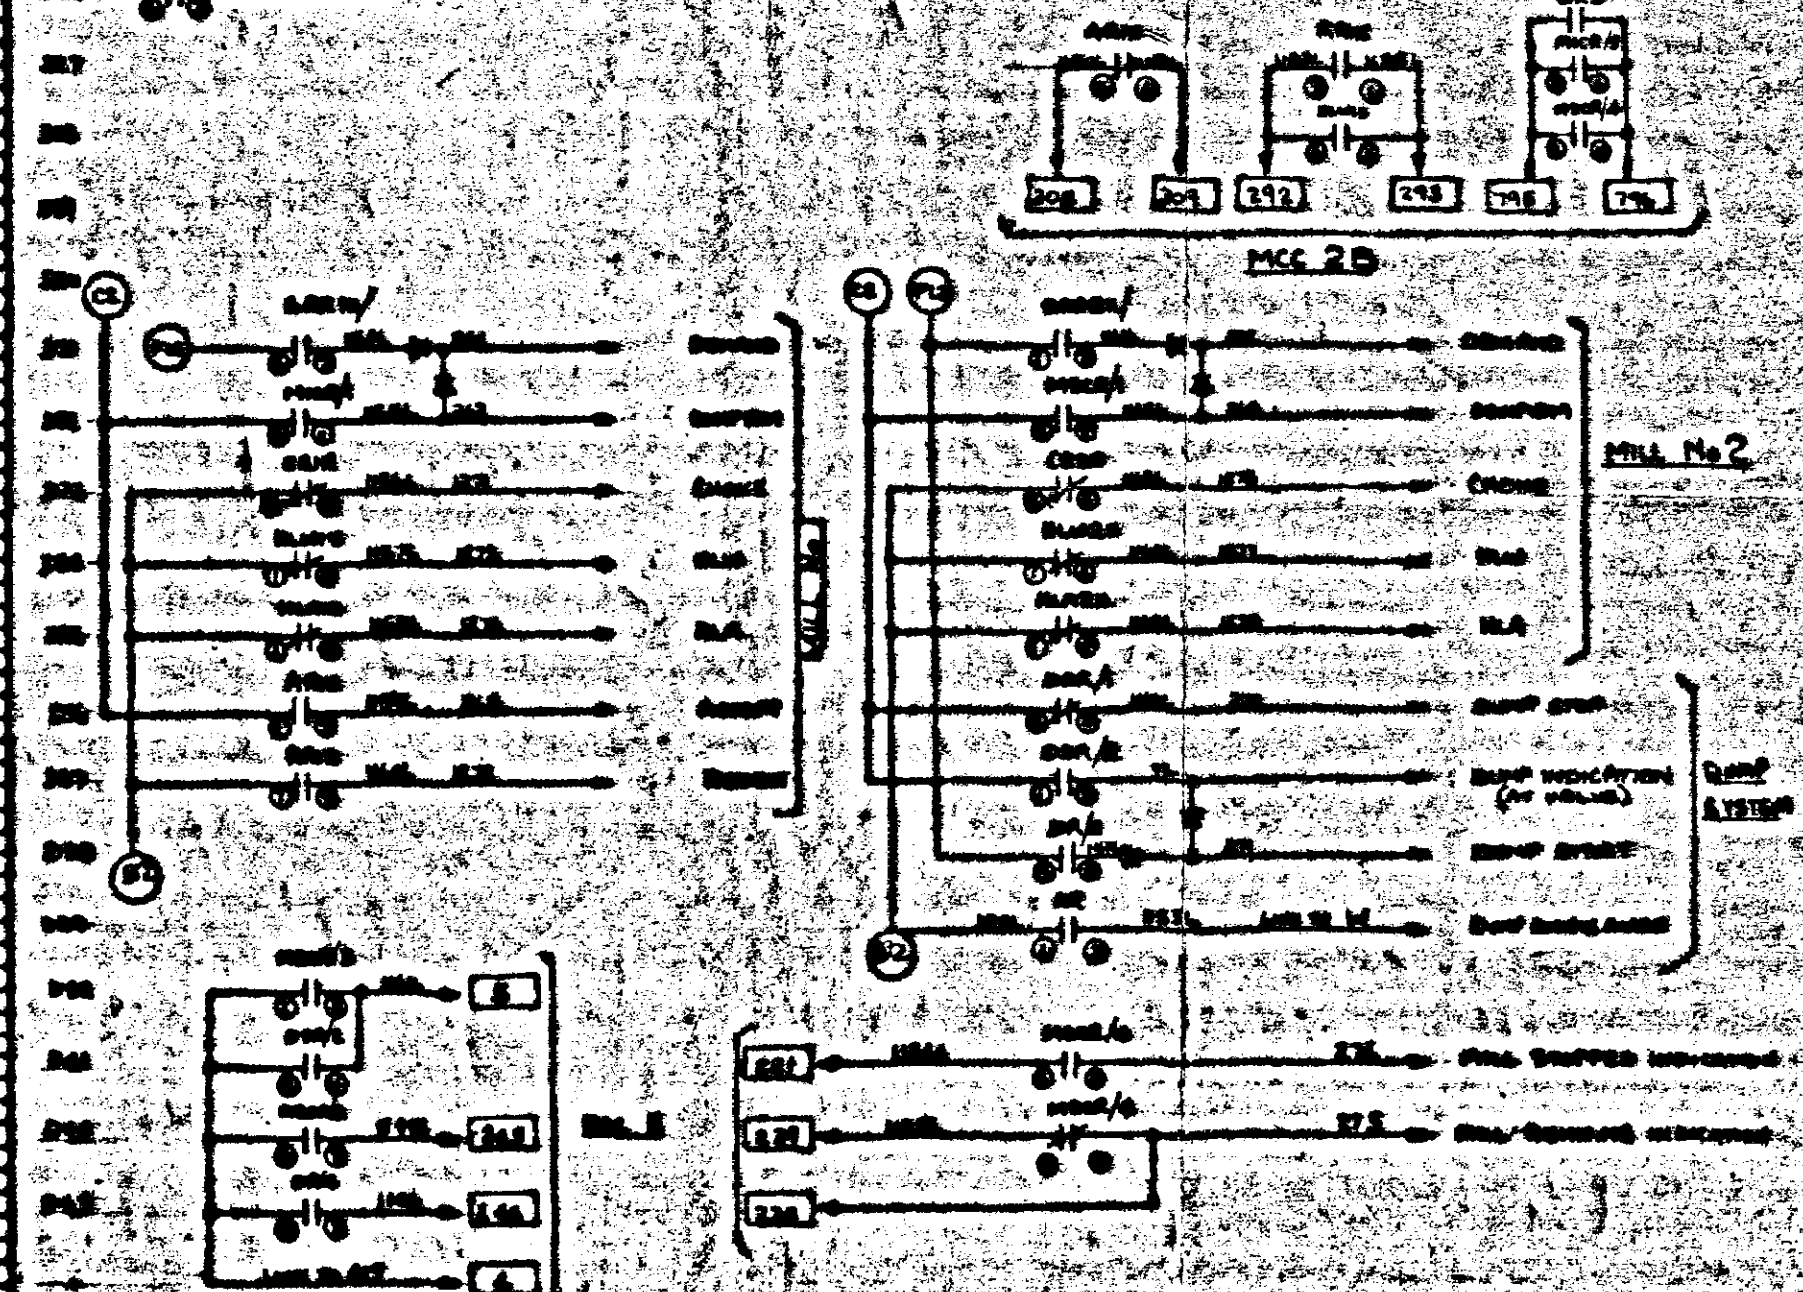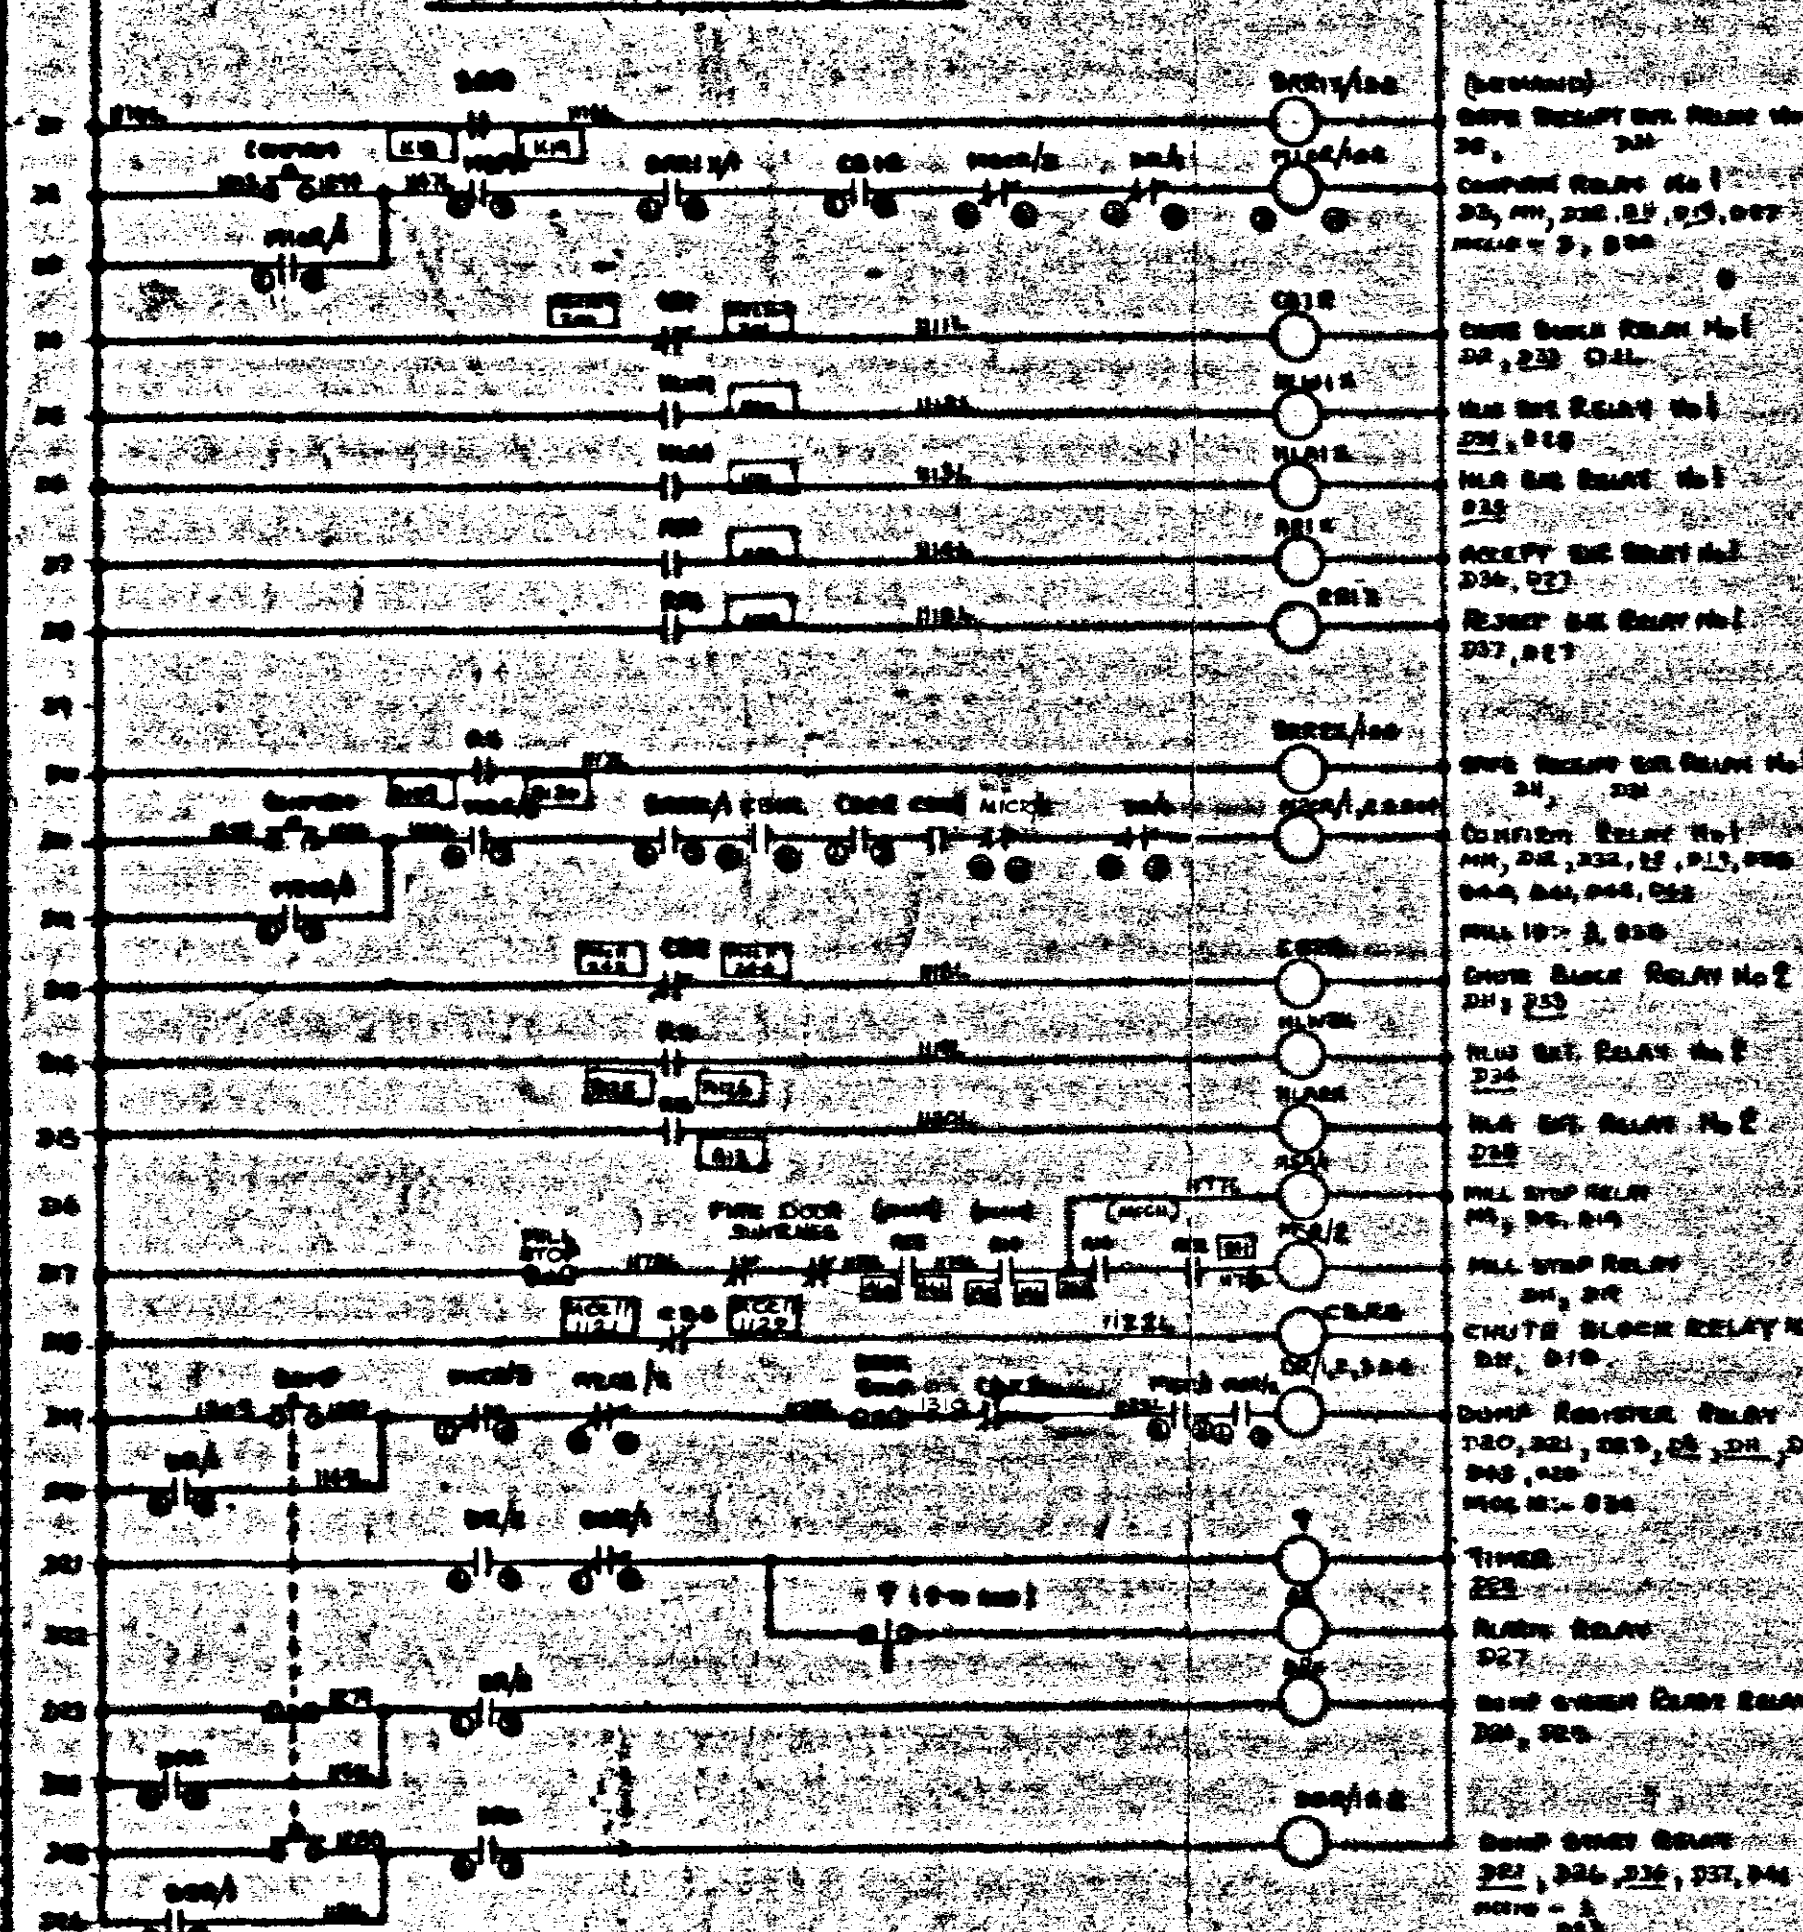

10729

DEWHURST & PARTNER LTD
MELBOURNE WORKS HOUNSLOW

SCHEME FOR MCCIQ - SEAFORTH GRAIN TERMINAL

[illegible]