


10730.

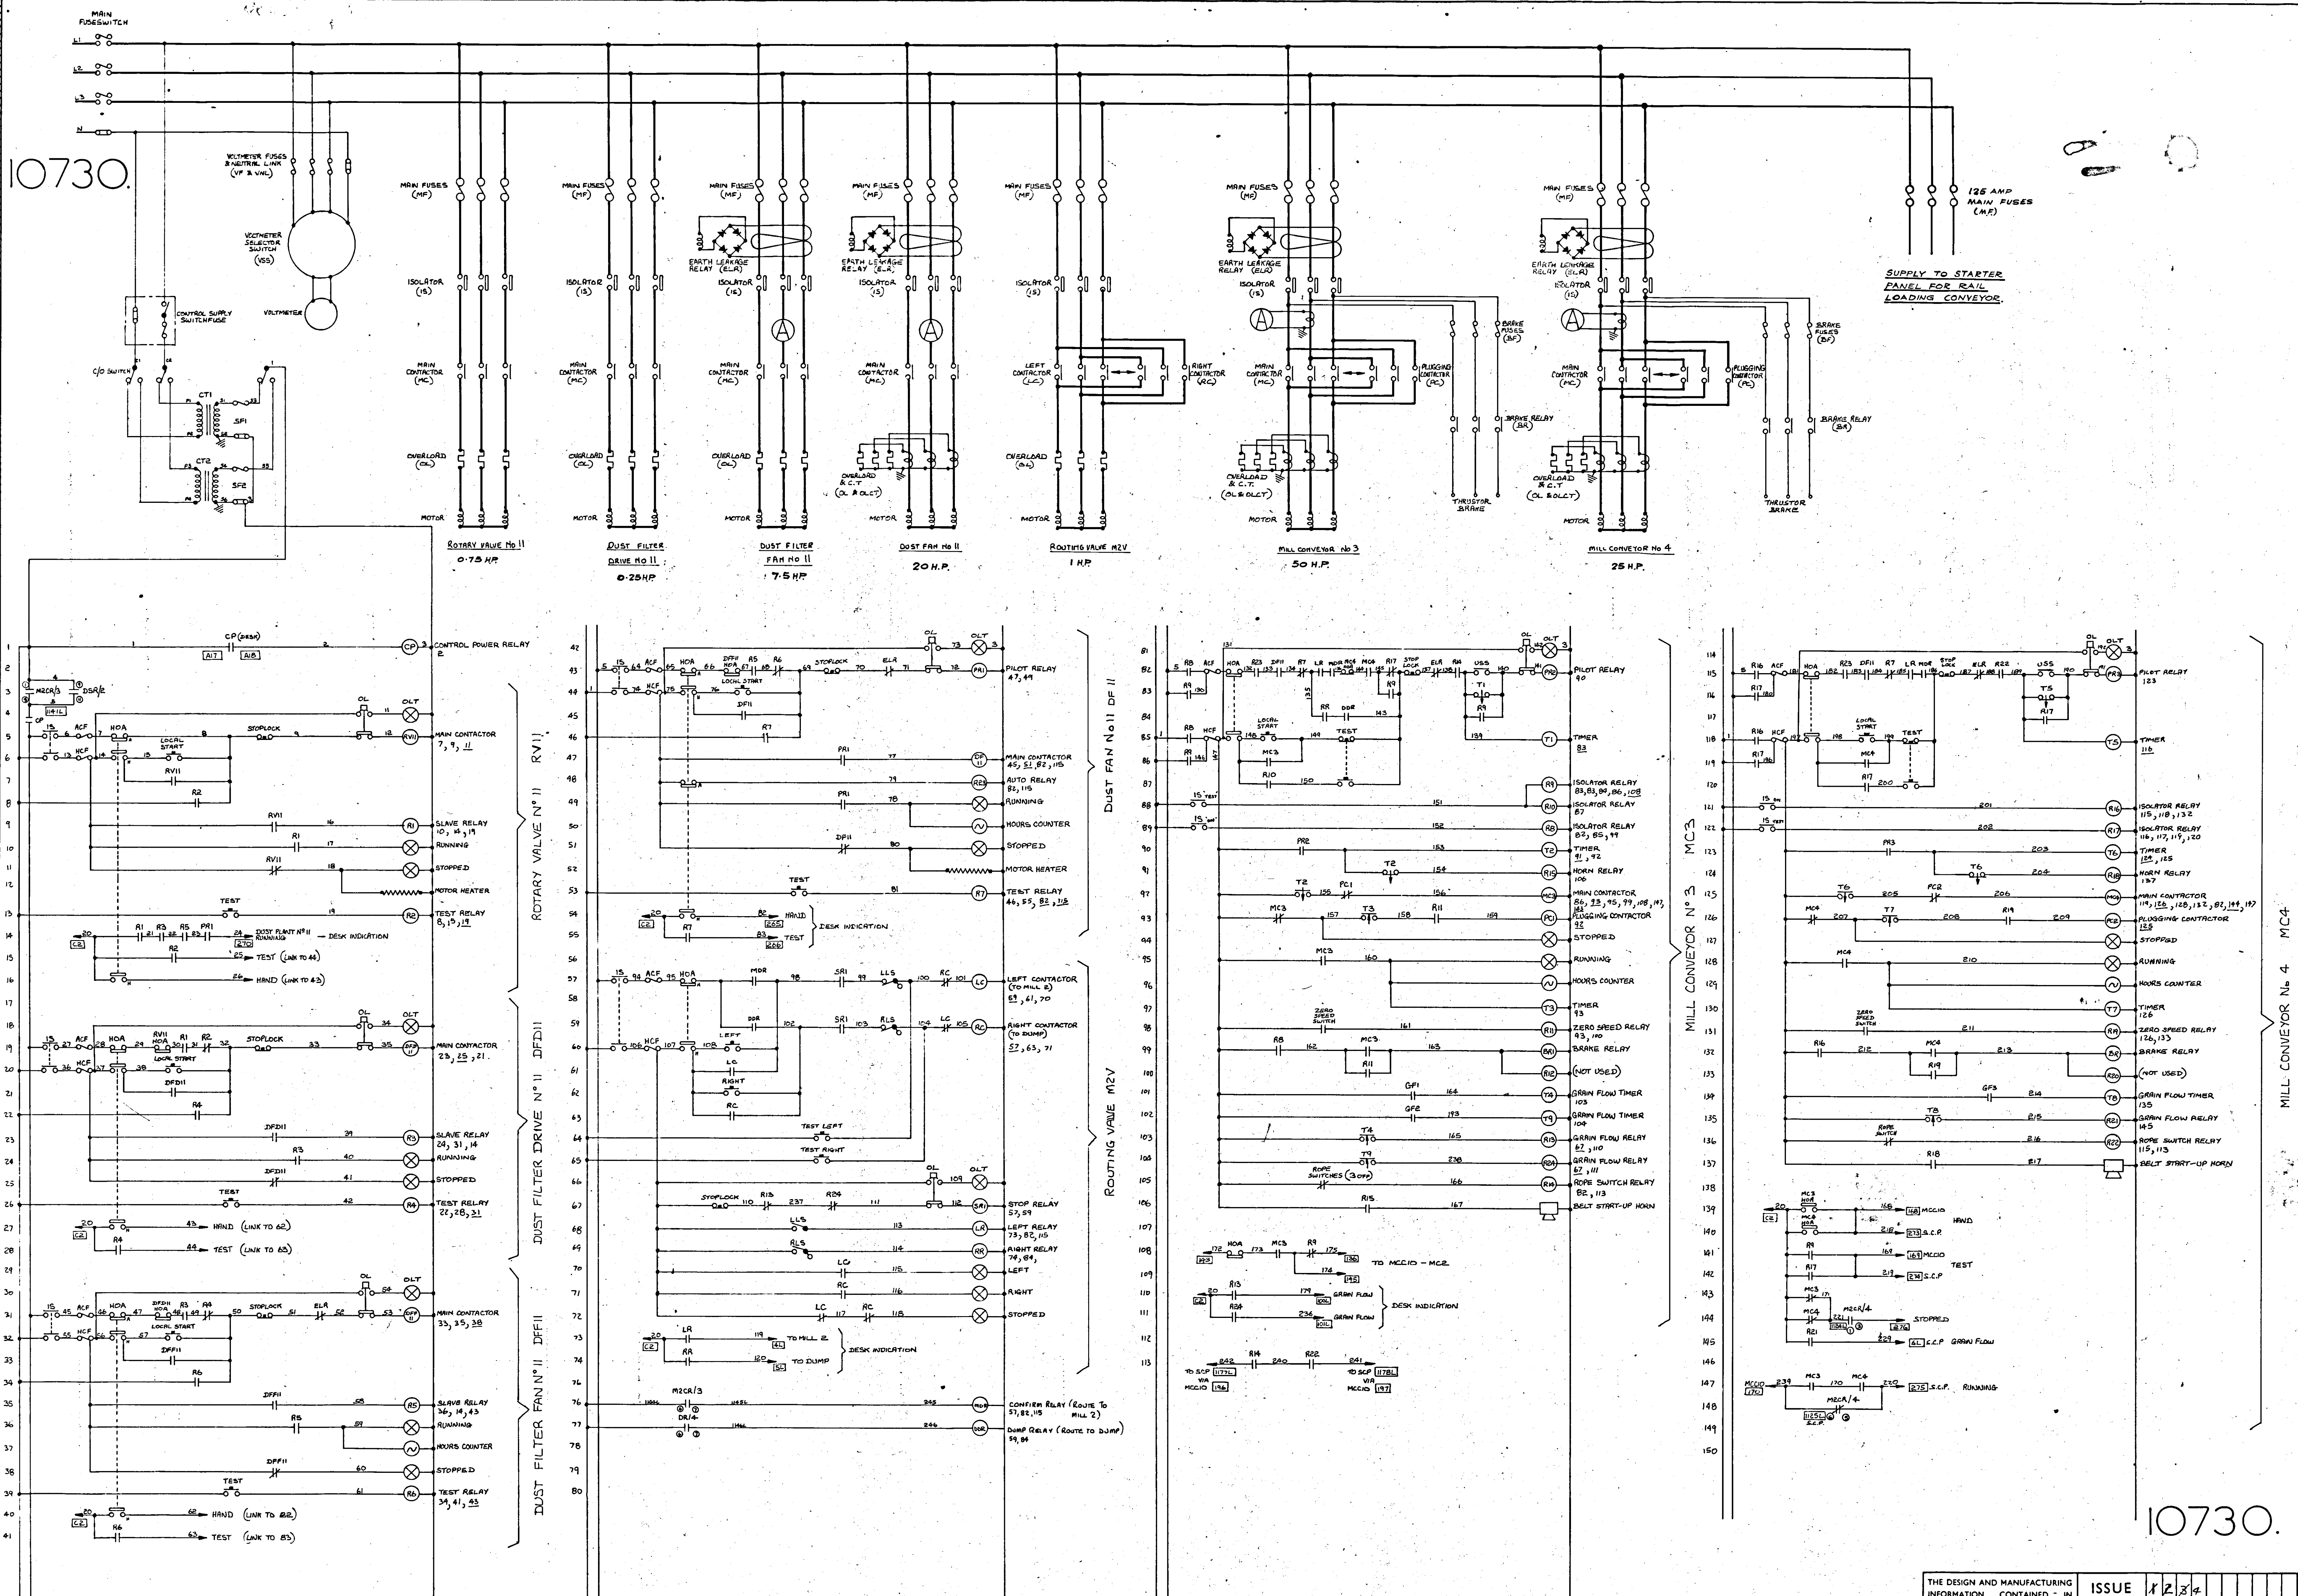

10730.

DEWHURST & PARTNER LTD.
MELBOURNE WORKS HOUNSLOW

TITLE: SCHEME FOR MCCII — SEAFORTH GRAIN TERMINAL

REVISION :	REVISION : 4 FUSES FOR RAIL LOADING CONV'R ADDED.	REVISION : 3 MRR & DDR ADDED.	REVISION : 2 CP CONTACT MOVED. DR4 CONTACT ON LINE 5 REMOVED. OVERLOAD TRIPPED FEED MODIFIED.	REVISION : 1 CONTACTS ADDED ON LINE 11A
ORIGIN : 1 / 1 SGD.	ORIGIN : 201105SGD. EP	ORIGIN : 10D 213 / 73SGD JS	ORIGIN : 10D 1413 / 73SGD JS	ORIGIN : 10D 111210 SGD BSC

DRAWN BY <i>BVL</i>	KEY DIAG. No.
DATE <i>16-10-72</i>	EXT. DIAG. No. <i>STX361AT</i>
CHECKED BY	REL. DIAG. No. <i>MTX361AT</i>
APPROVED BY	PANEL LAYOUT No. <i>HTX361AT</i>
DATE	

S N E R I O G	ISSUE	1	2	3	4							
	DTX361AT											
	DTX361AT											

G.A.F. 7231/70