
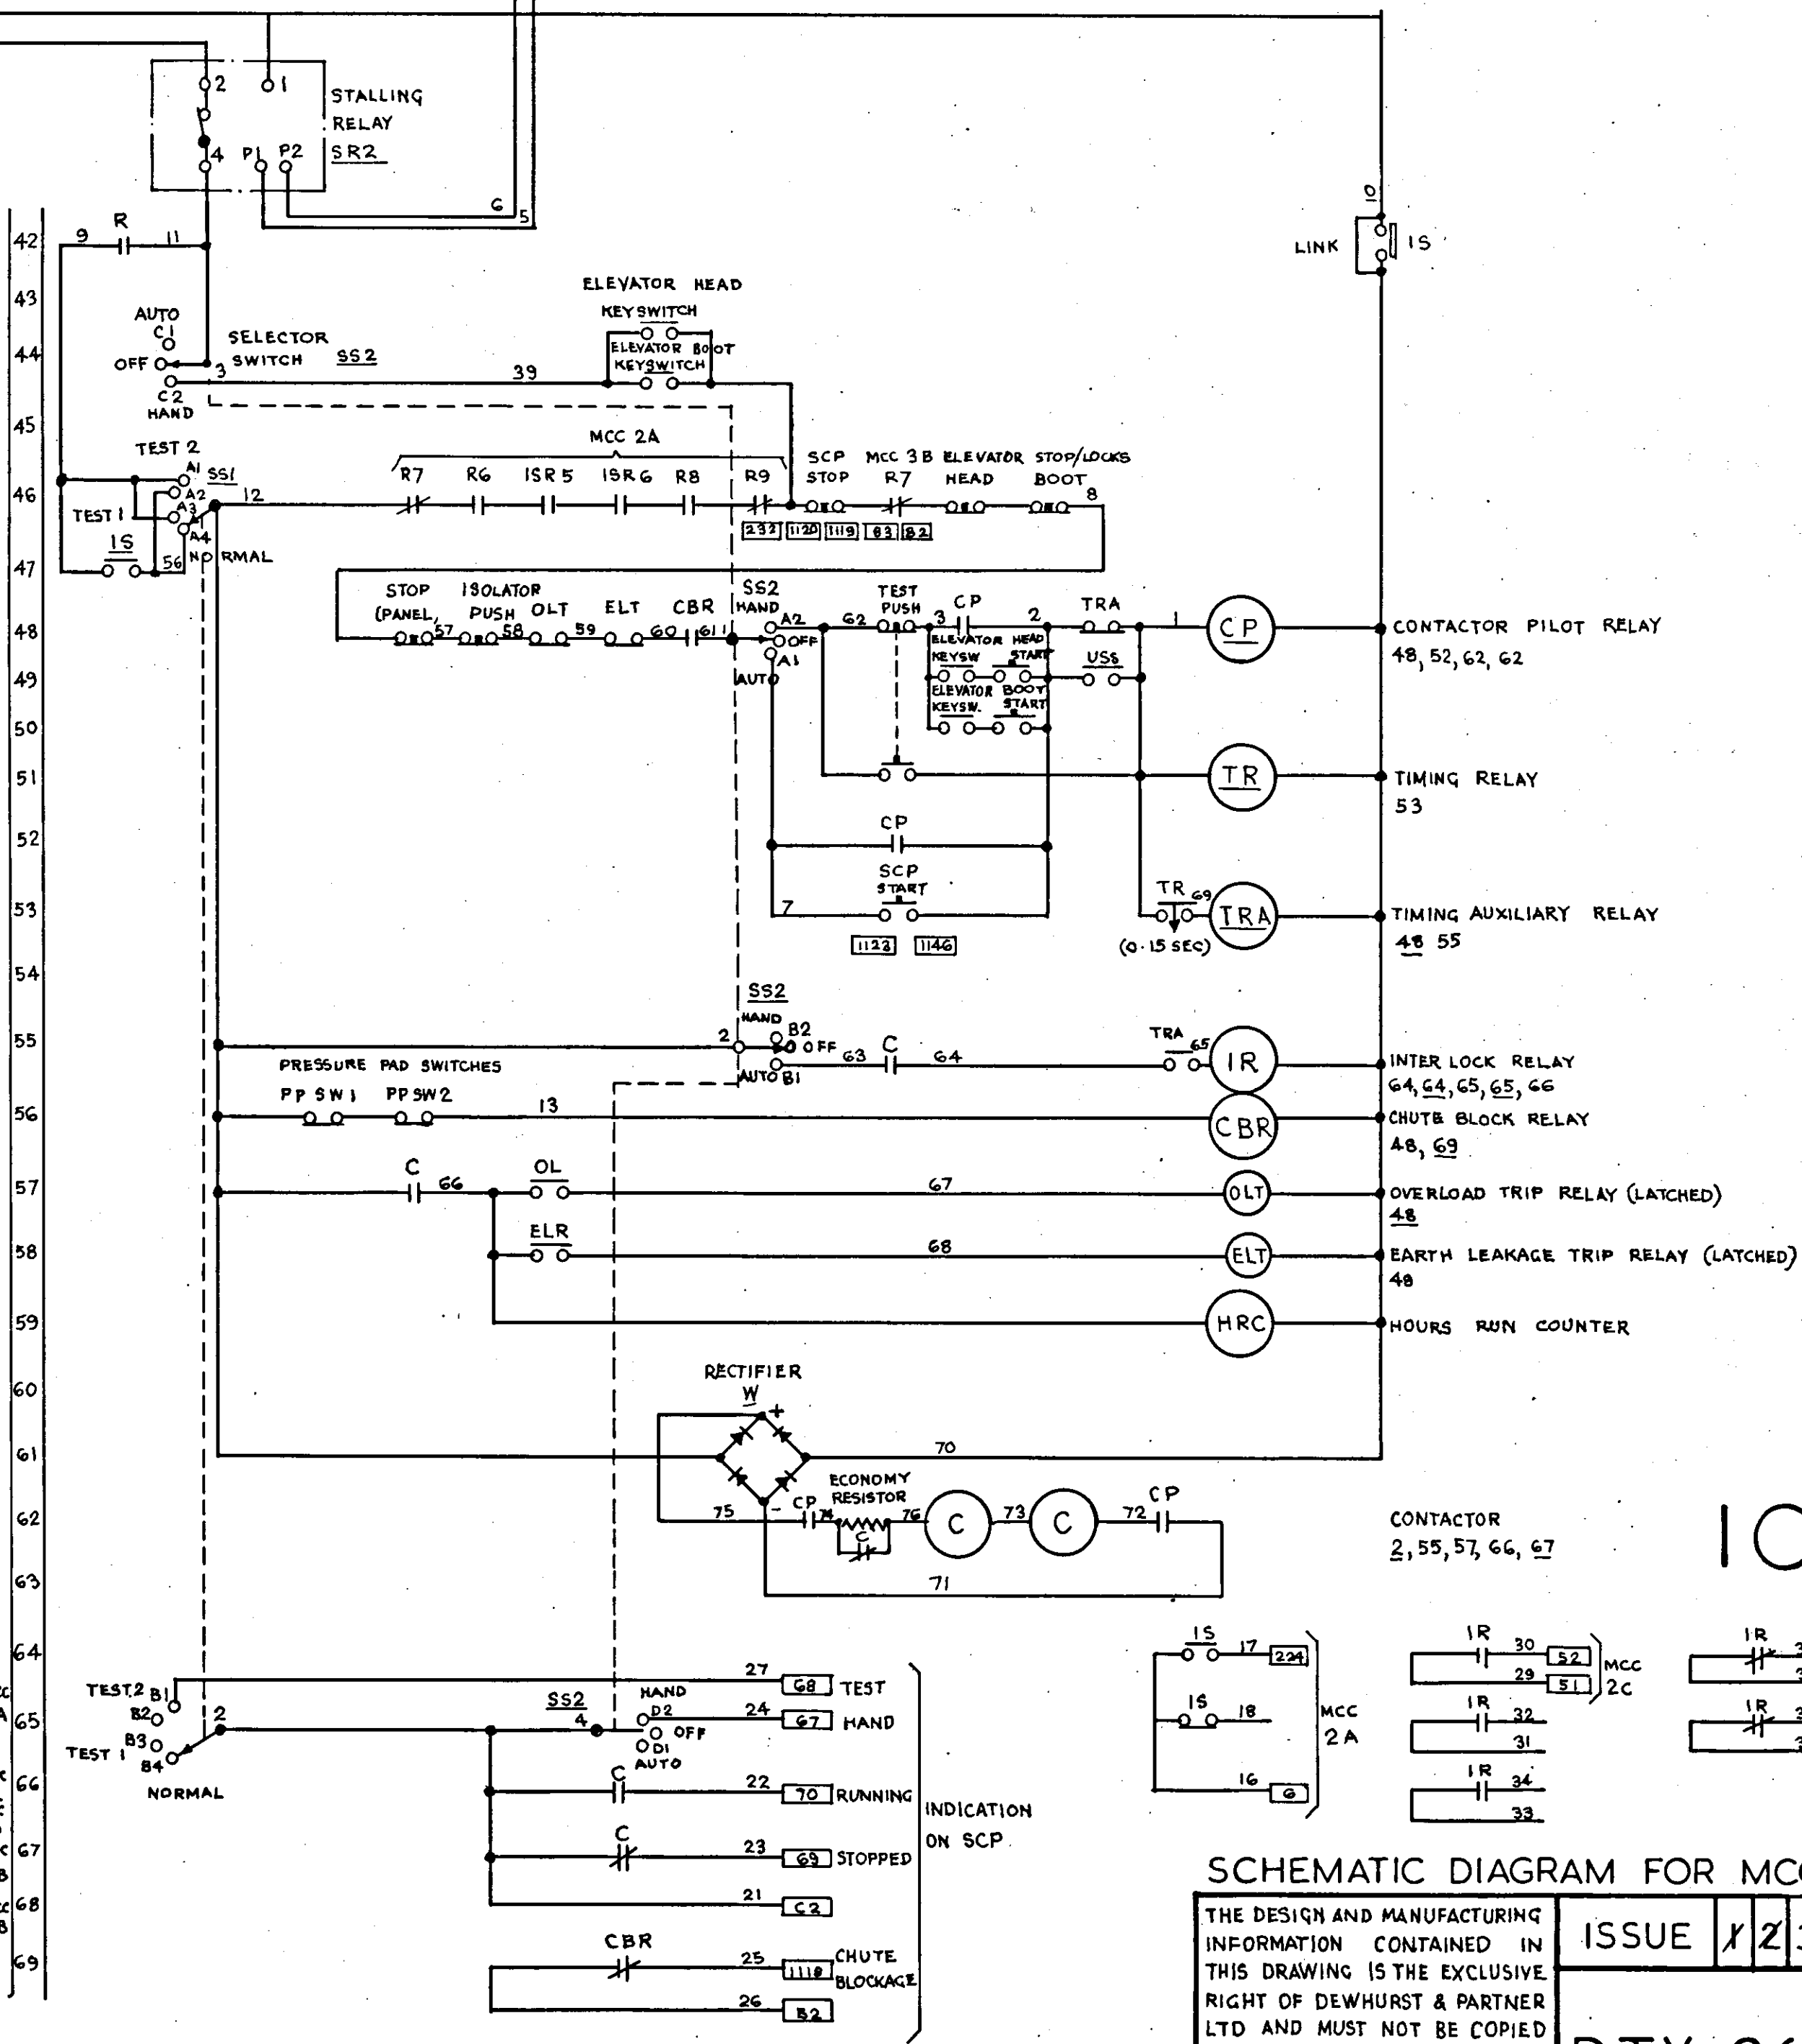


NOTE:
A TERMINAL REFERENCE SHOWN THUS MCC 4 B 3-21
REFERS TO TERMINAL 21 ON STAGE 3 OF MCC 4 B

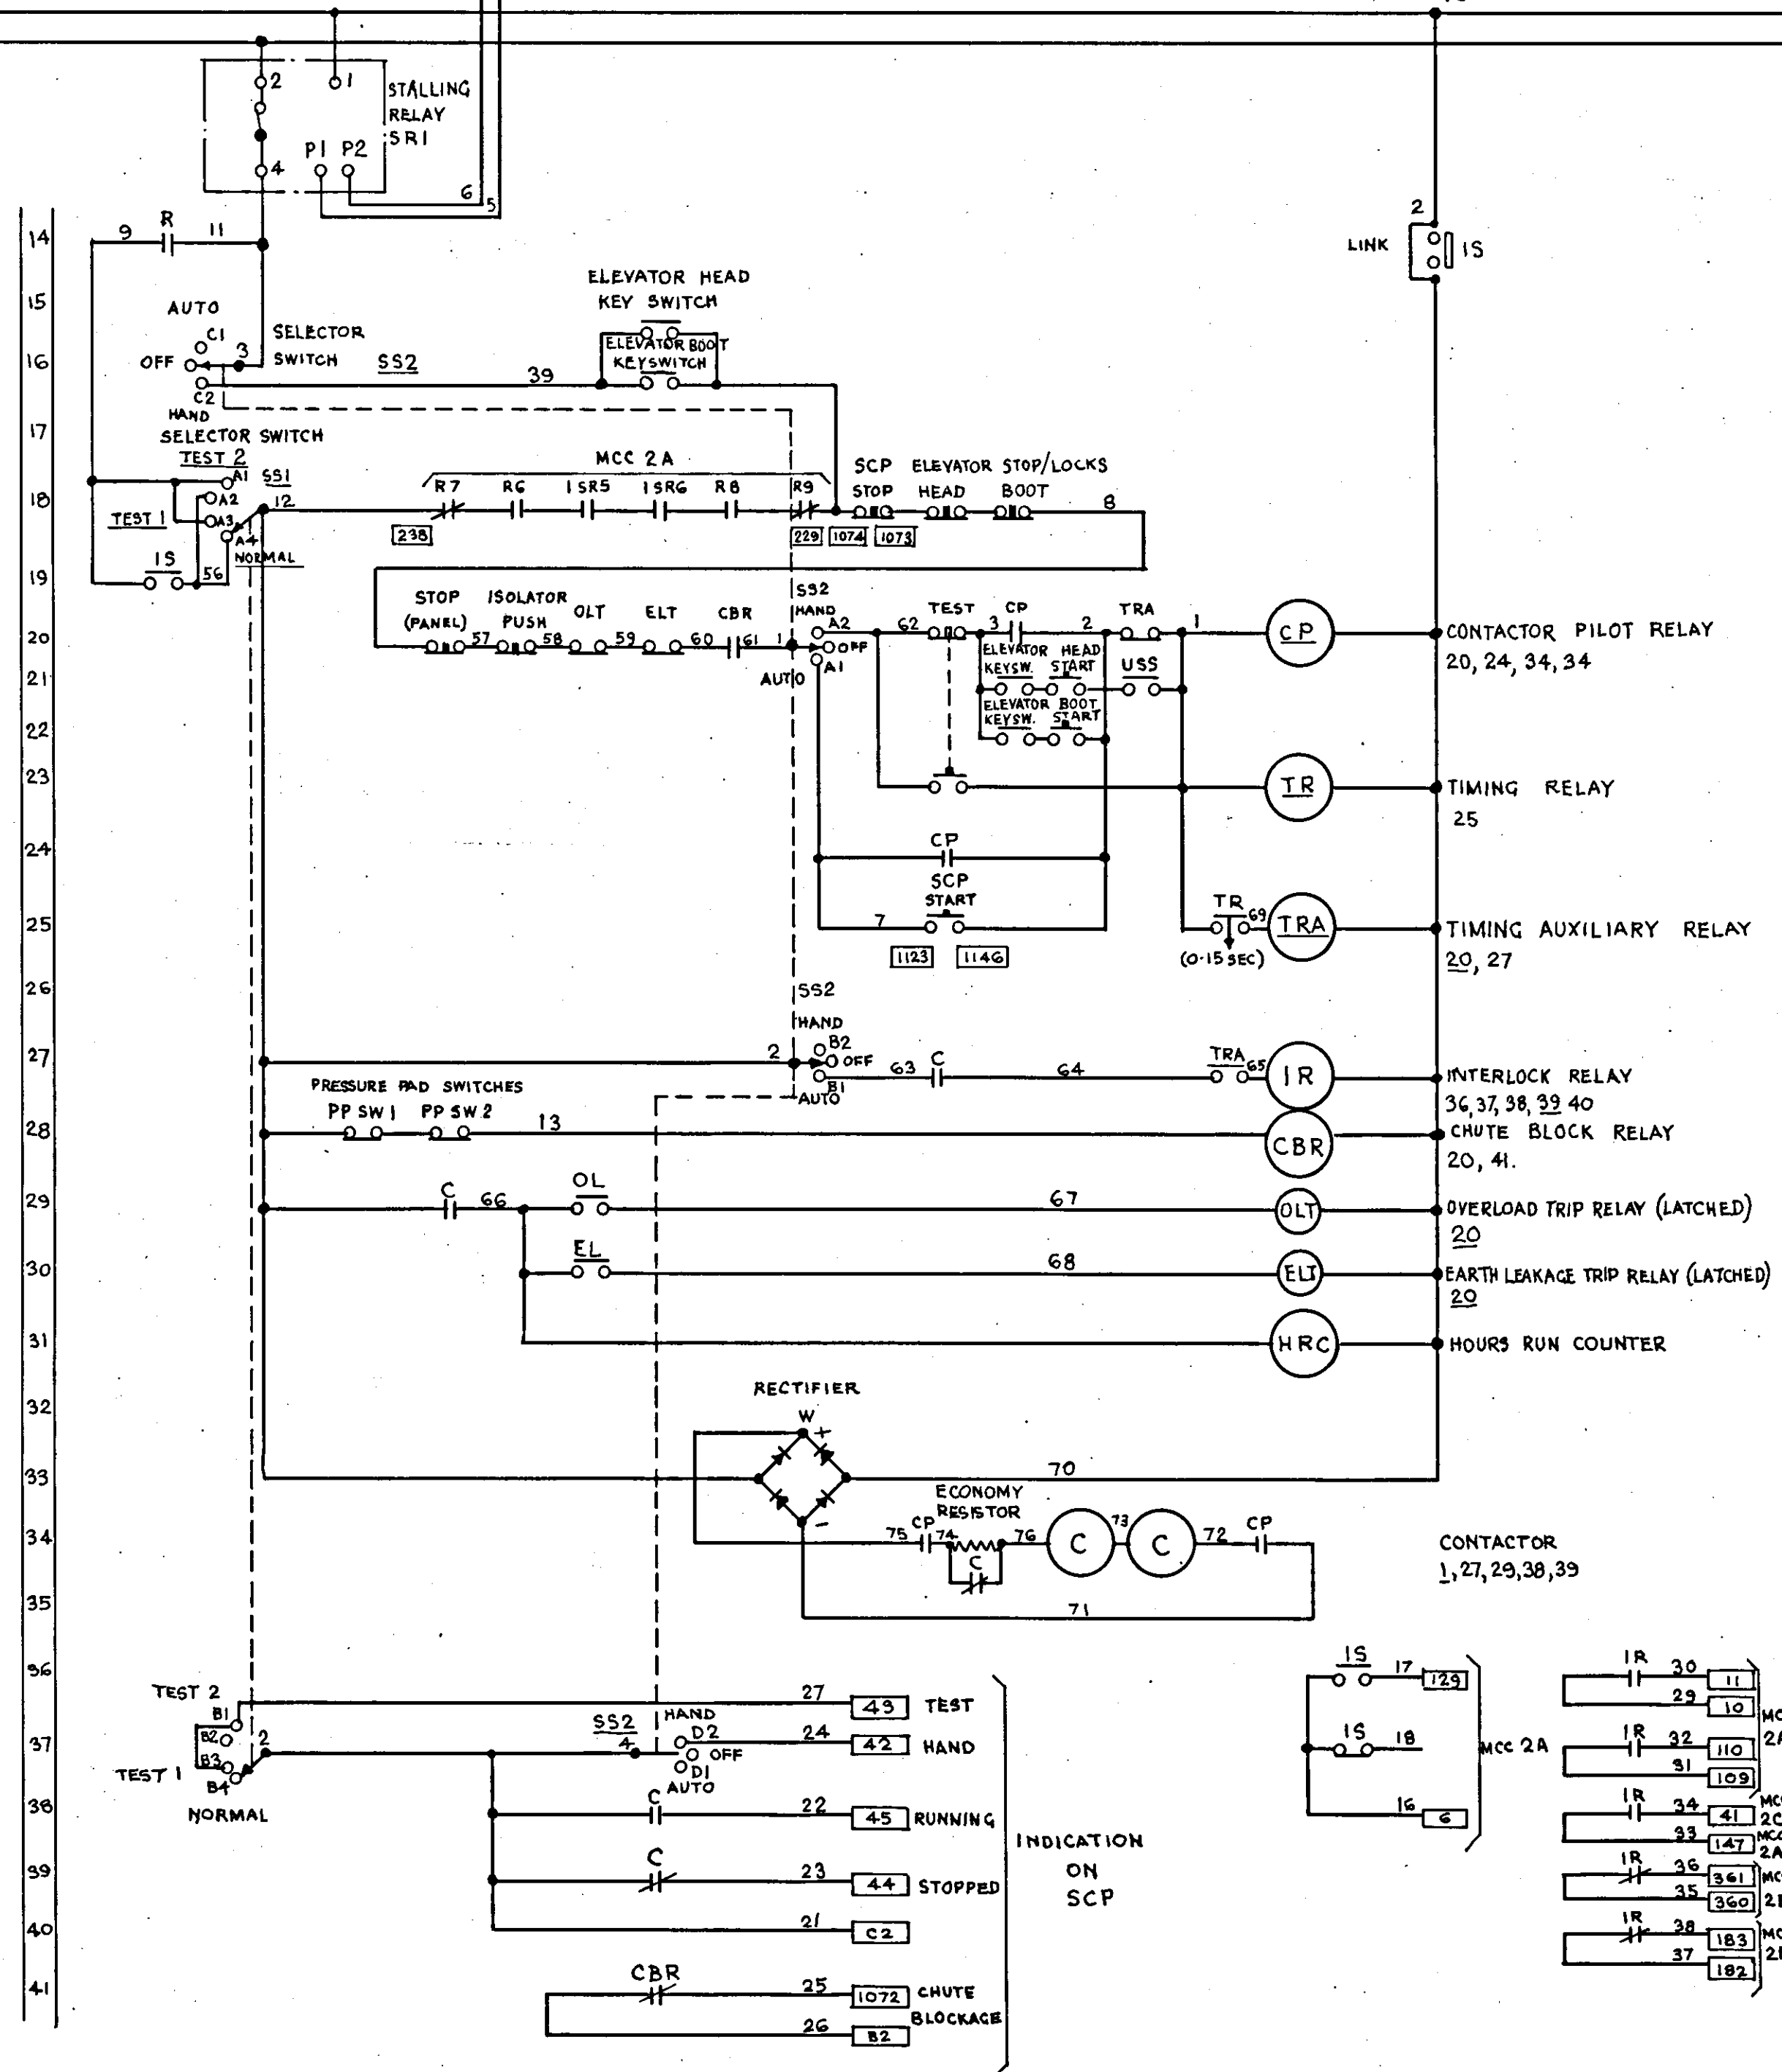

THE DESIGN AND MANUFACTURING INFORMATION CONTAINED IN THIS DRAWING IS THE EXCLUSIVE RIGHT OF DEWHURST & PARTNER LTD AND MUST NOT BE COPIED OR USED FOR MANUFACTURING PURPOSES.

ISSUE 1 2 3

DTX 361 AF/2

DTX 361 AF/2

c) DTX 361 AF/2