


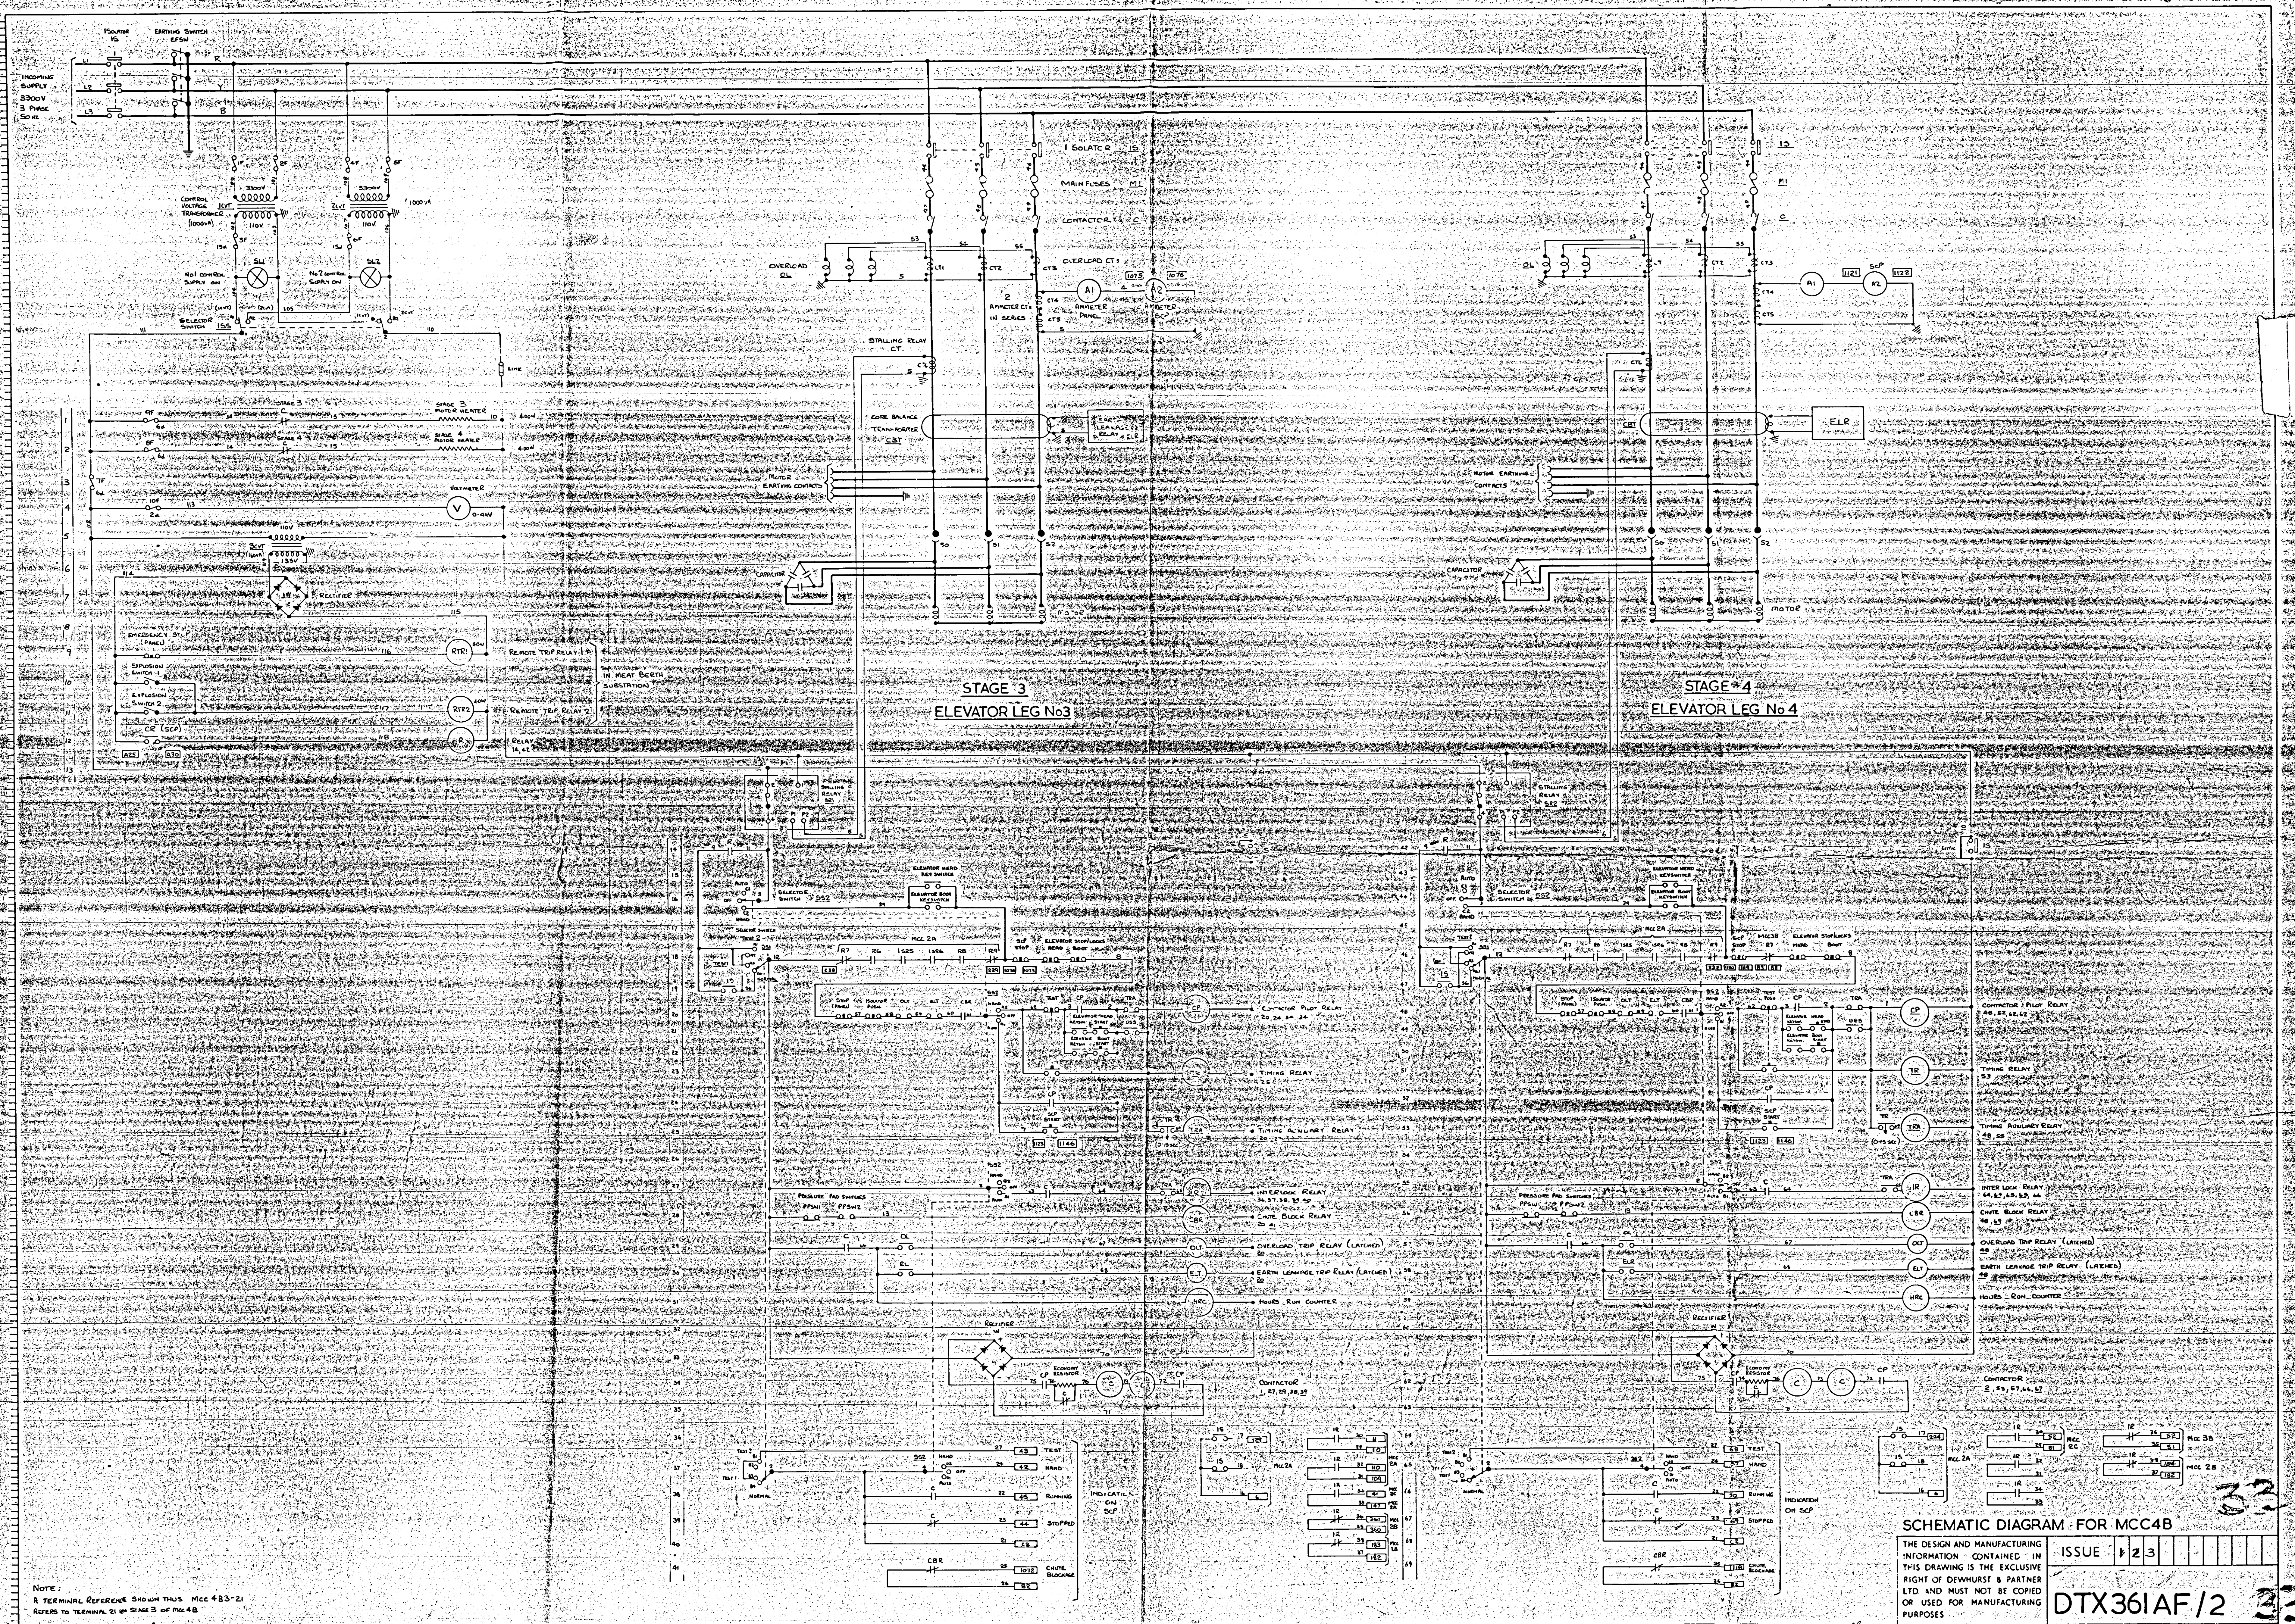

NOTE:
A TERMINAL REFERENCE SHOWN THIS MCC 4B3-21
REFERS TO TERMINAL 21 ON STAGE 3 OF MCC 4B

DEWHURST & PARTNER LTD.
MELBOURNE WORKS HOUNSLOW

SCHEMATIC DIAGRAM FOR MCC4B
(AS GEC SCHEME X319326)

REVISION:	REVISION:	REVISION:	REVISION:	REVISION:
ORIGIN: / / SGD.	ORIGIN: / / SGD.	ORIGIN: / / SGD.	ORIGIN: / / SGD.	ORIGIN: / / SGD.

DRAWN BY: [Signature]
DATE: 1/1/72
CHECKED BY: [Signature]
APPROVED BY: [Signature]
DATE: 1/1/72

KEY DIAG No. [Blank]
EXT. DIAG. No. [Blank]
REL. DIAG. No. [Blank]
PANEL LAYOUT No. [Blank]

DTX361AF/2
DTX361AF/2