




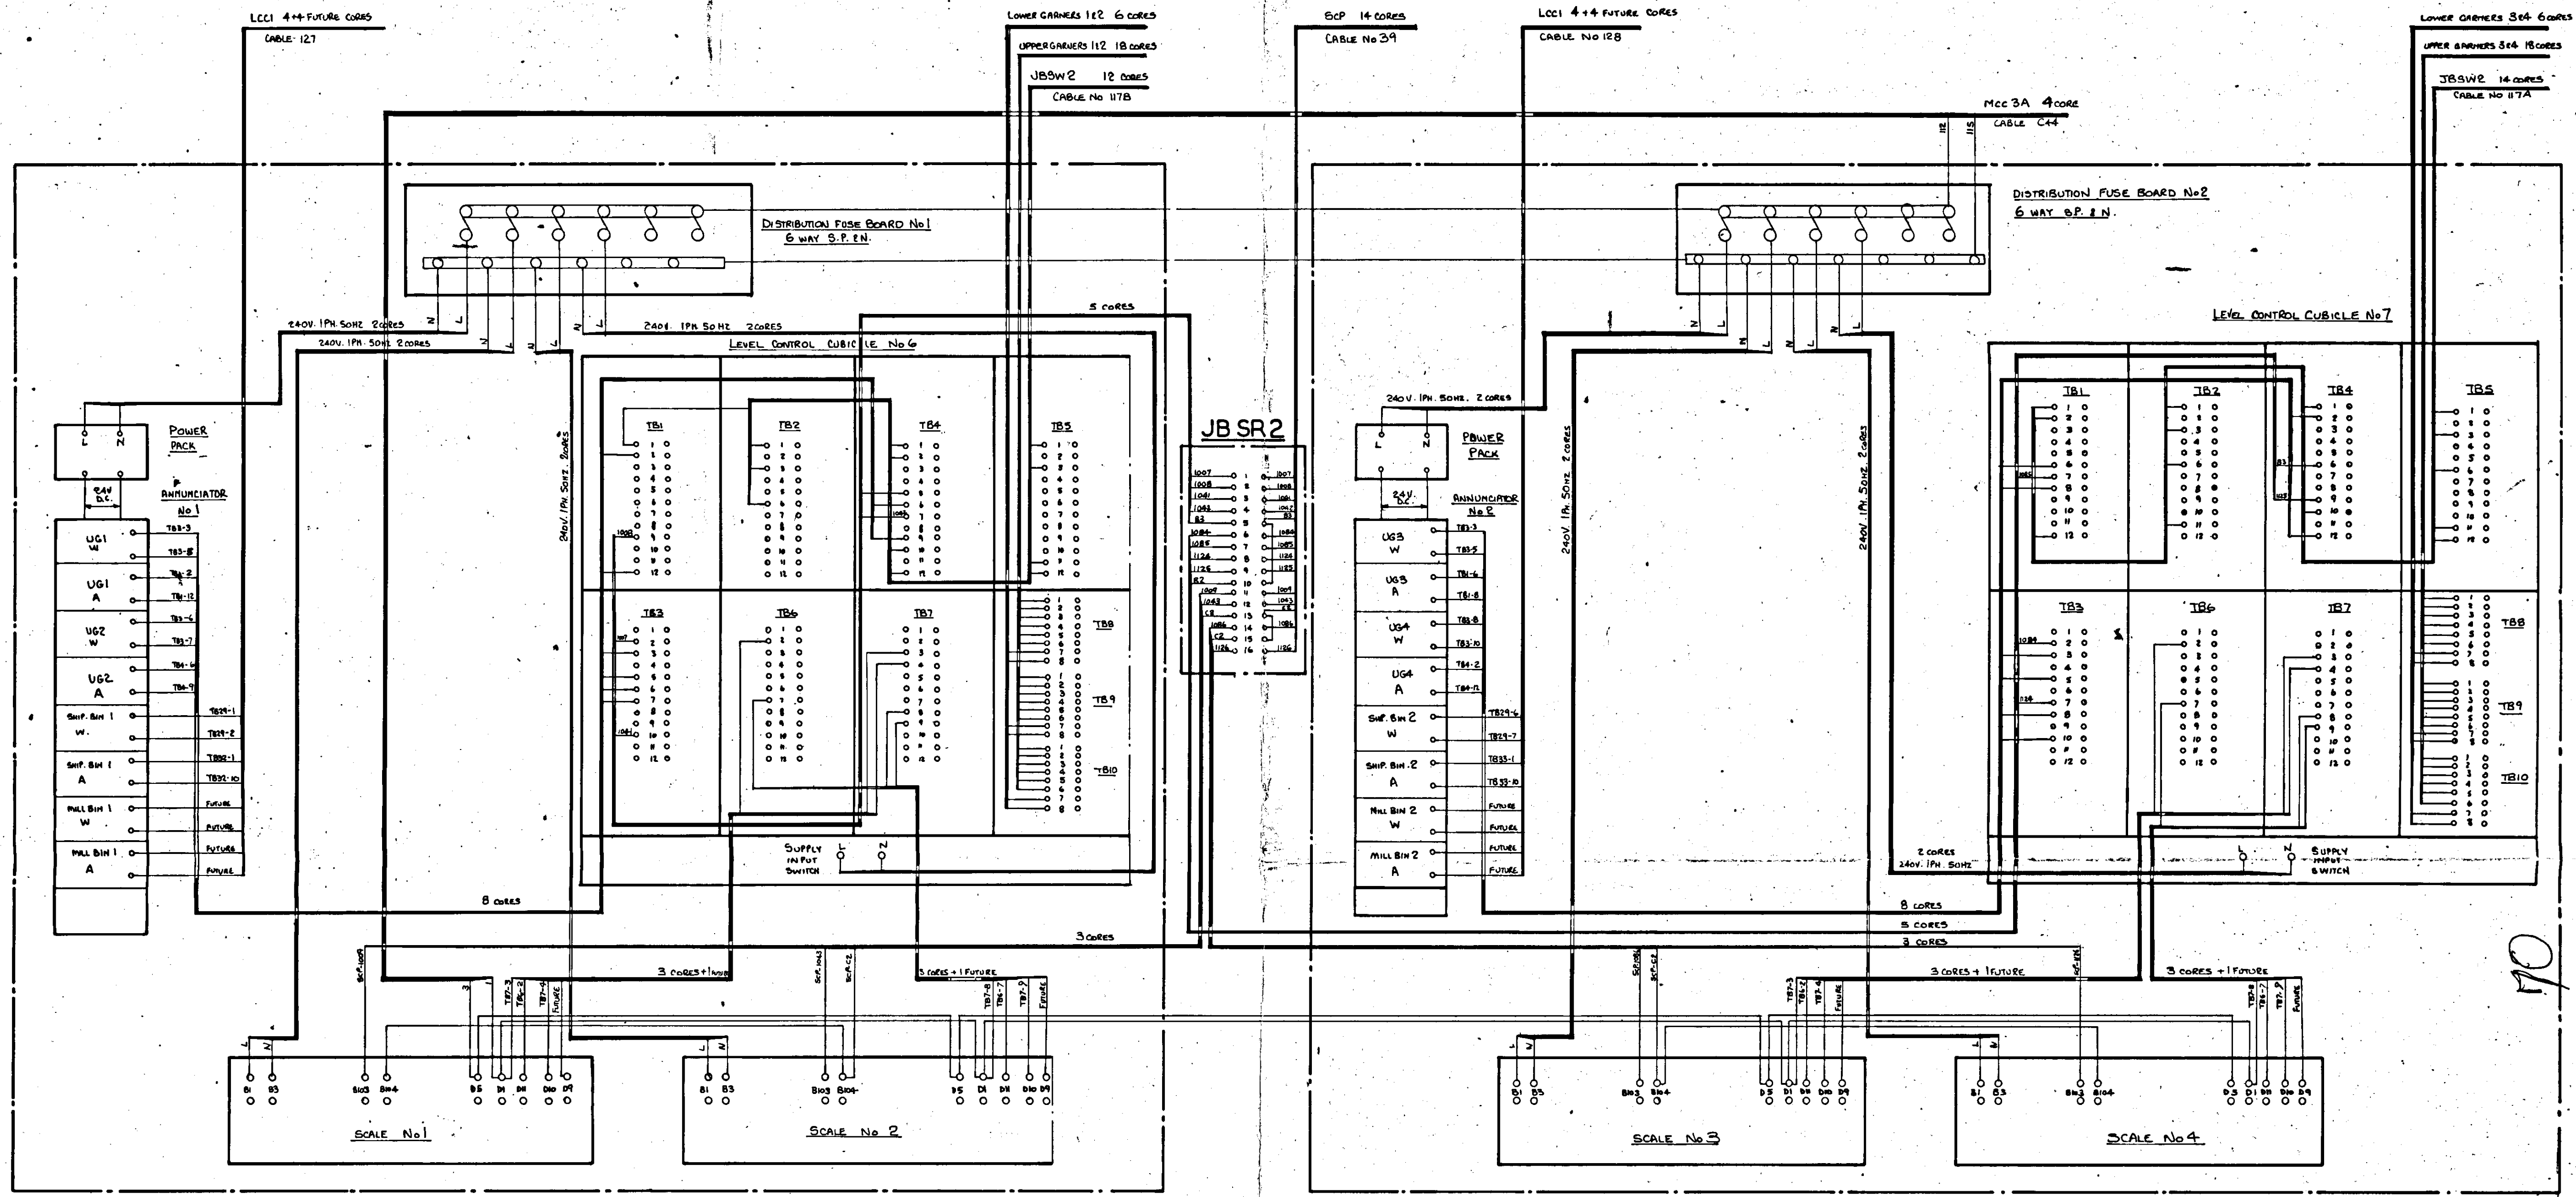

SCALE ROOM 1

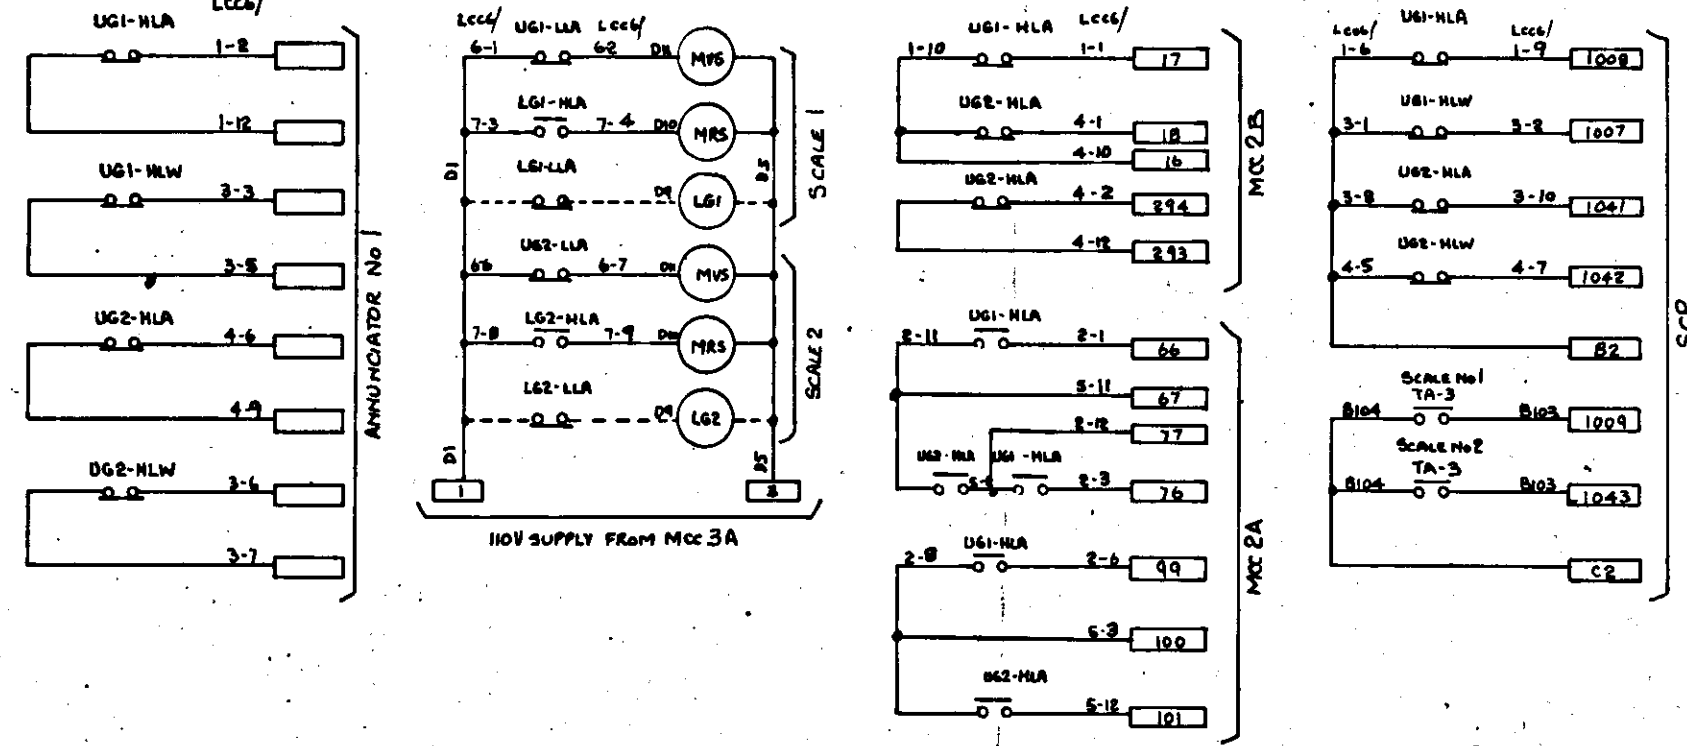

SCALE ROOM 2

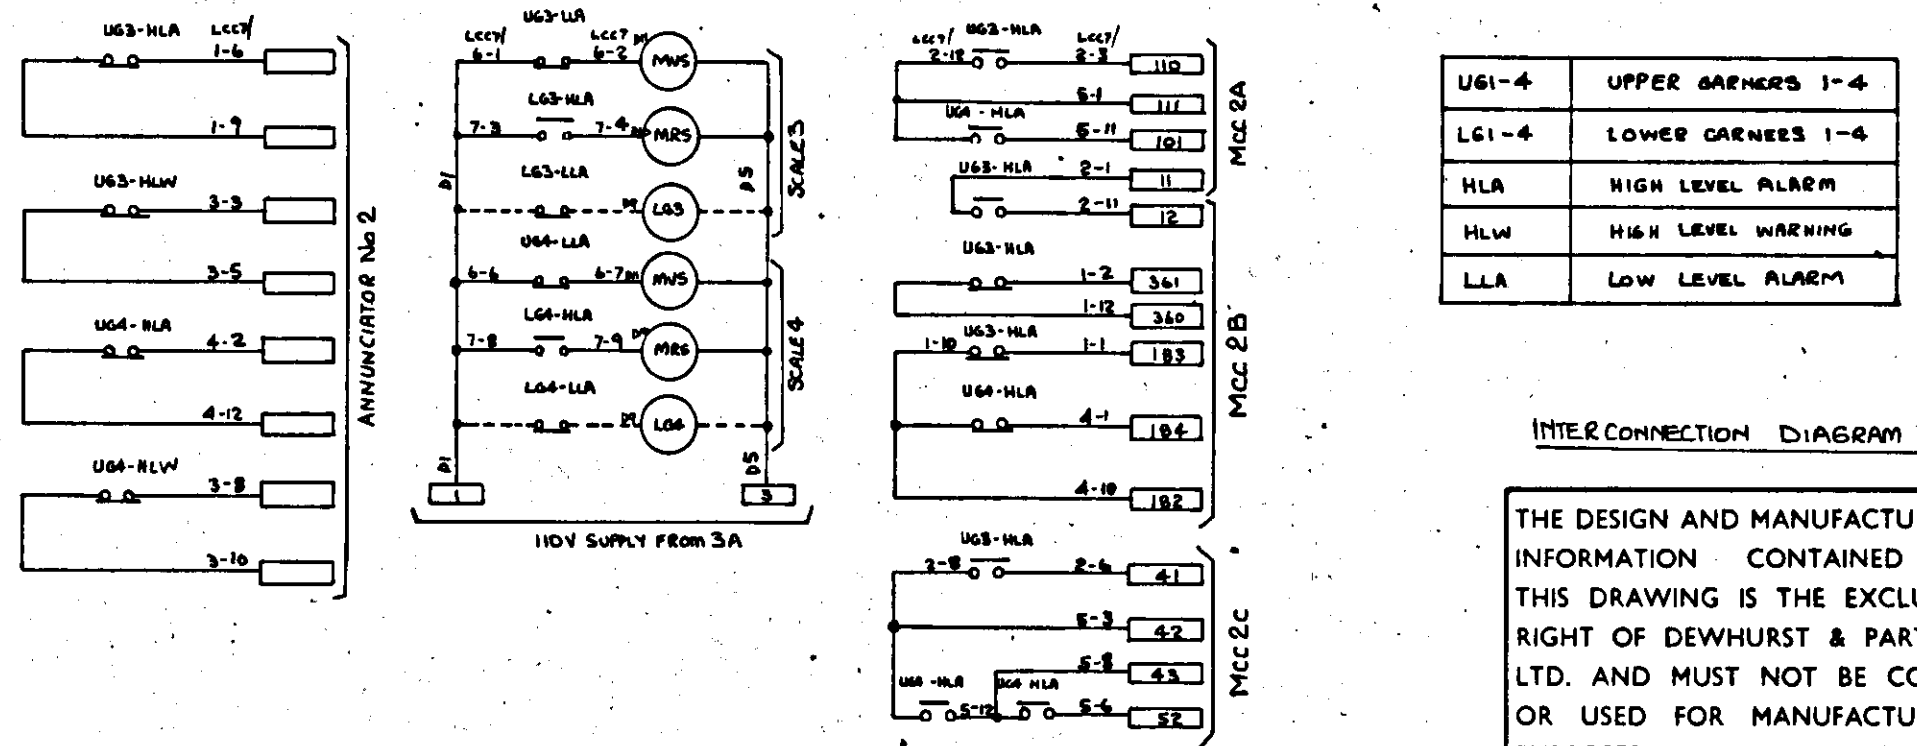

INTERCONNECTION DIAGRAM FOR SCALE ROOMS 1 & 2

THE DESIGN AND MANUFACTURING INFORMATION CONTAINED IN THIS DRAWING IS THE EXCLUSIVE RIGHT OF DEWHURST & PARTNER LTD. AND MUST NOT BE COPIED OR USED FOR MANUFACTURING PURPOSES.

ISSUE	1	2	3	4
RTX 361 AU				
RTX 361 AU				

DEWHURST & PARTNER LTD.
MELBOURNE WORKS HOUNSLOW

TITLE
INTERCONNECTION DIAGRAM FOR SCALE ROOMS 1 & 2

REVISION: 3 ALL CONNECTIONS REVERSED CONNECTIONS MODIFIED TO SUIT. ORIGIN: ICD. 9/4/73 SGD. JS.	REVISION: 2 SCALE TERMINALS ADDED. ORIGIN: ICD. 5/4/72 SGD. JS.	REVISION: 1 DETAILS OF INTERNAL CONNECTIONS ADDED. ORIGIN: ICD. 2/3/72 SGD. JS.	DRAWN BY DATE CHECKED BY APPROVED BY DATE
---	--	--	---

KEY DIAG. No.	EXT. DIAG. No.
REL. DIAG. No.	PANEL LAYOUT No.