



LORRY LOADING SCALE ROOM 1

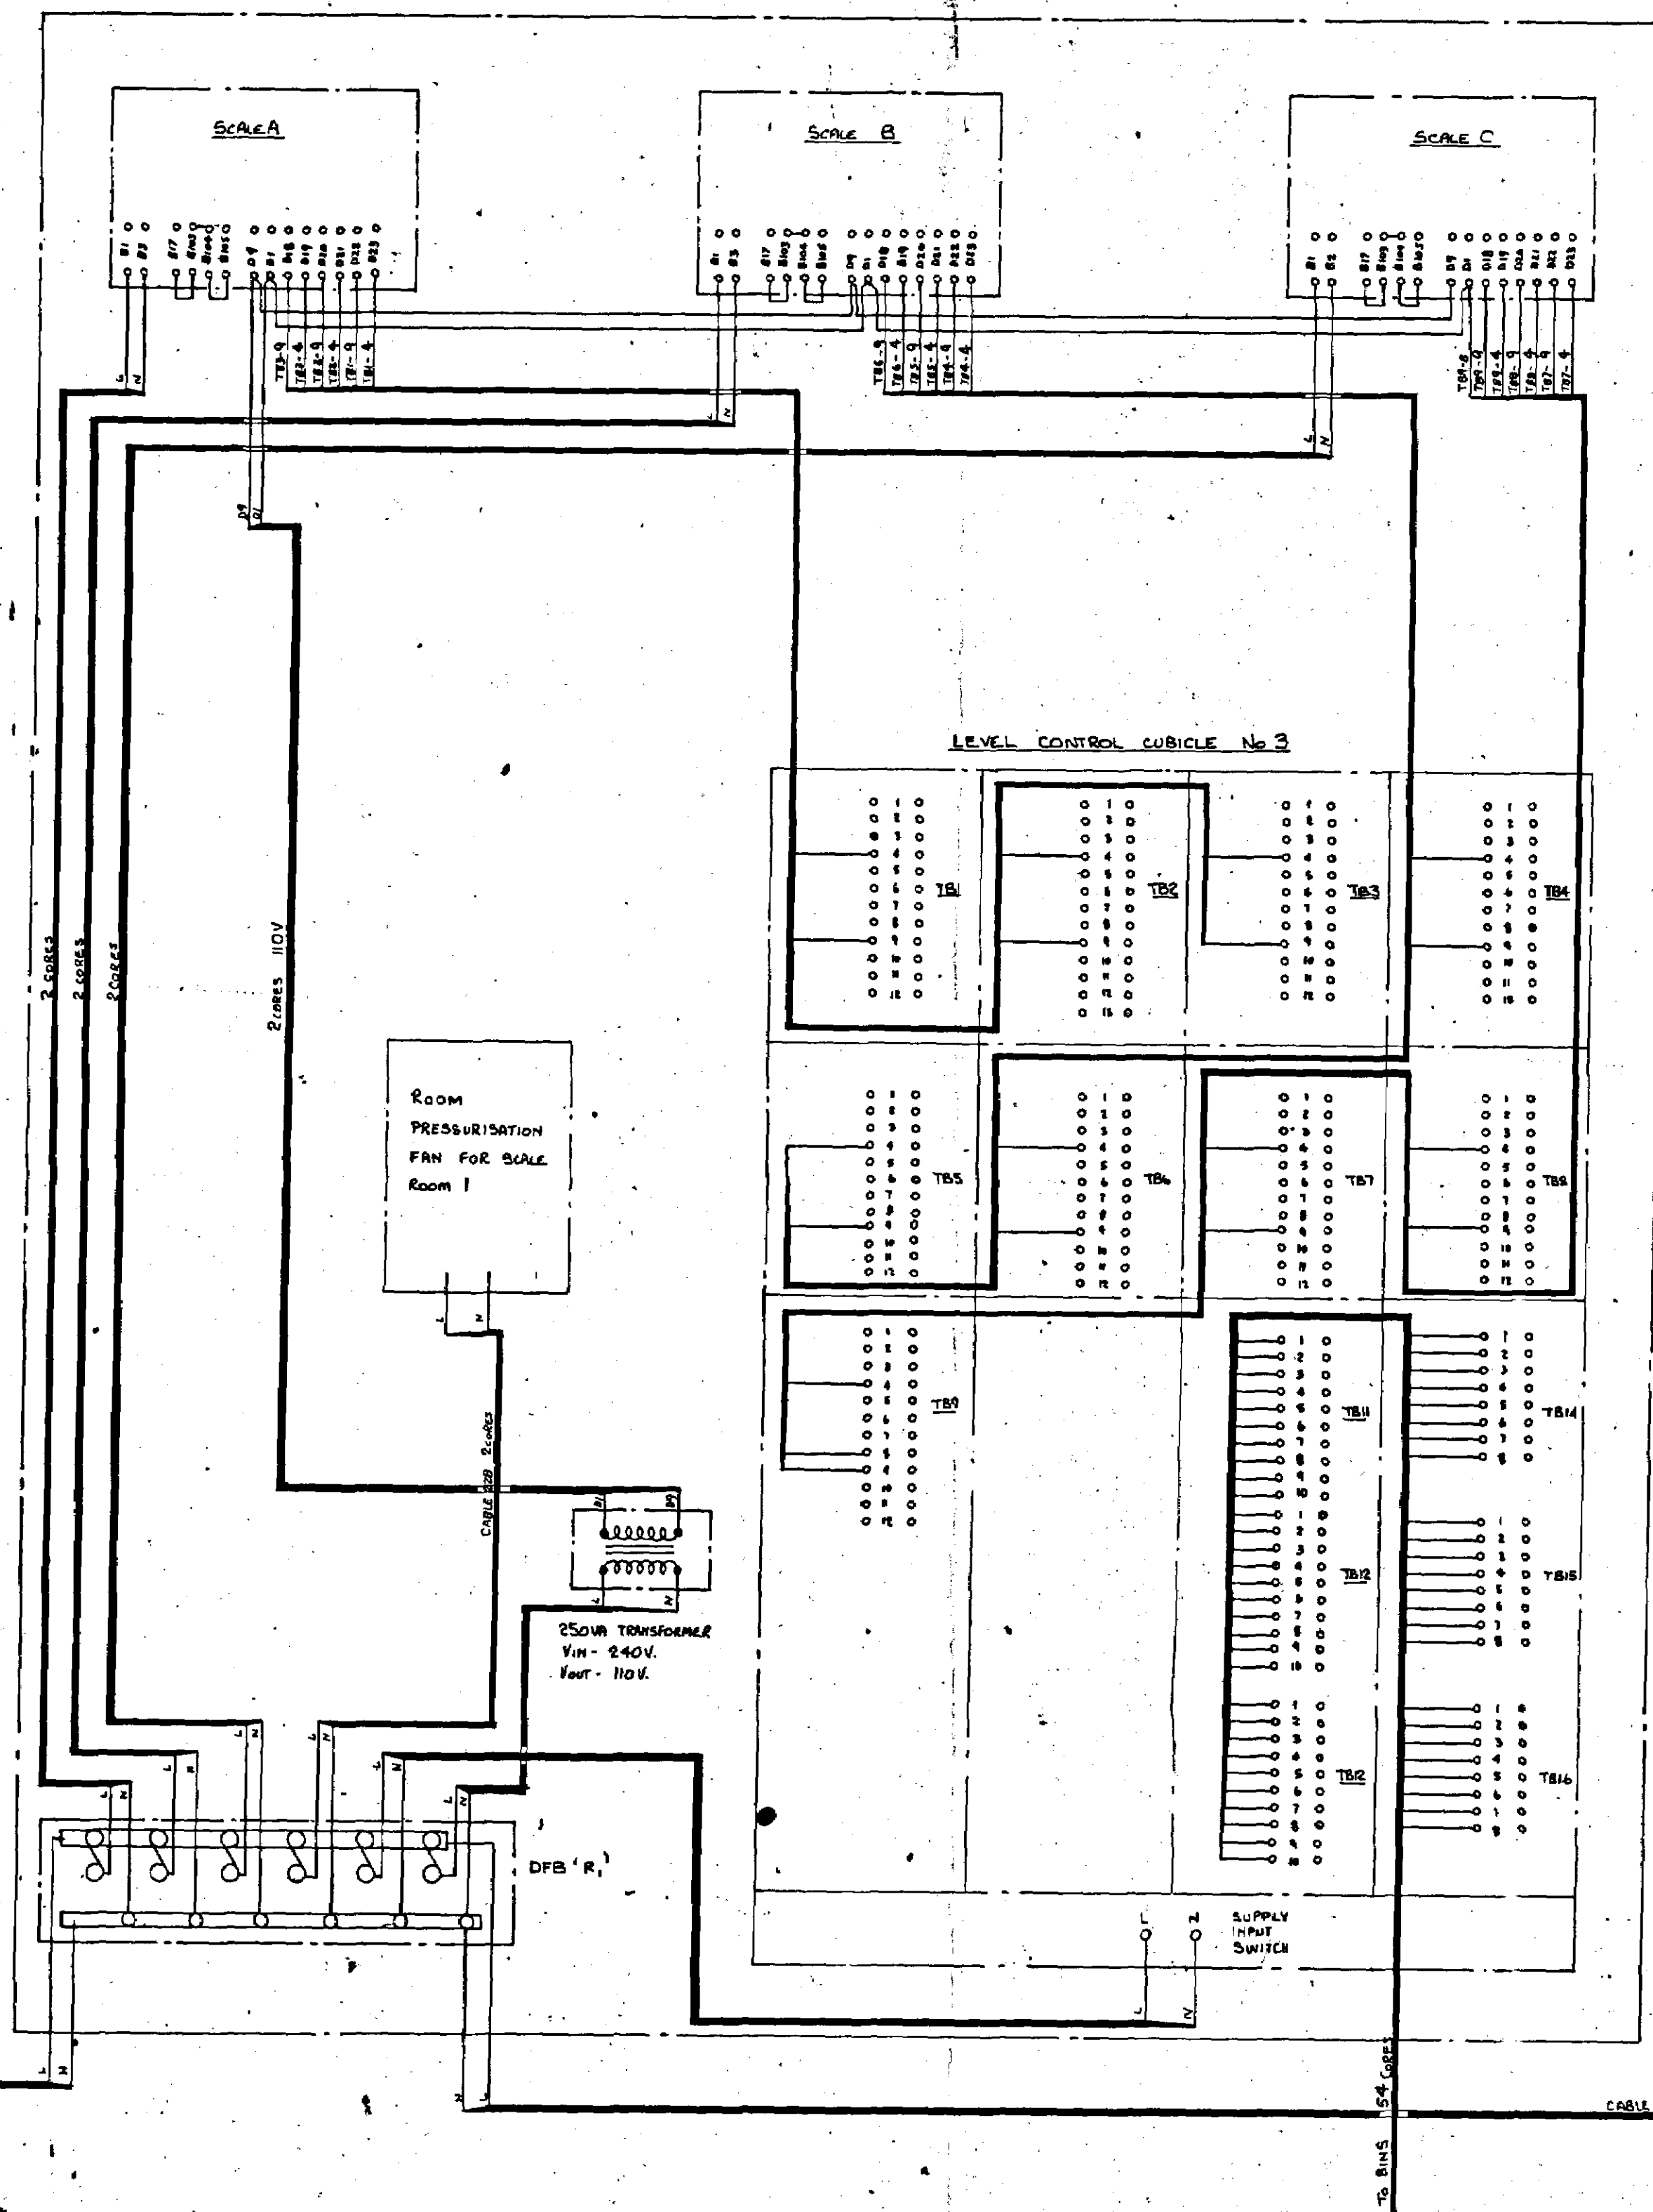

LORRY LOADING SCALE ROOM 2

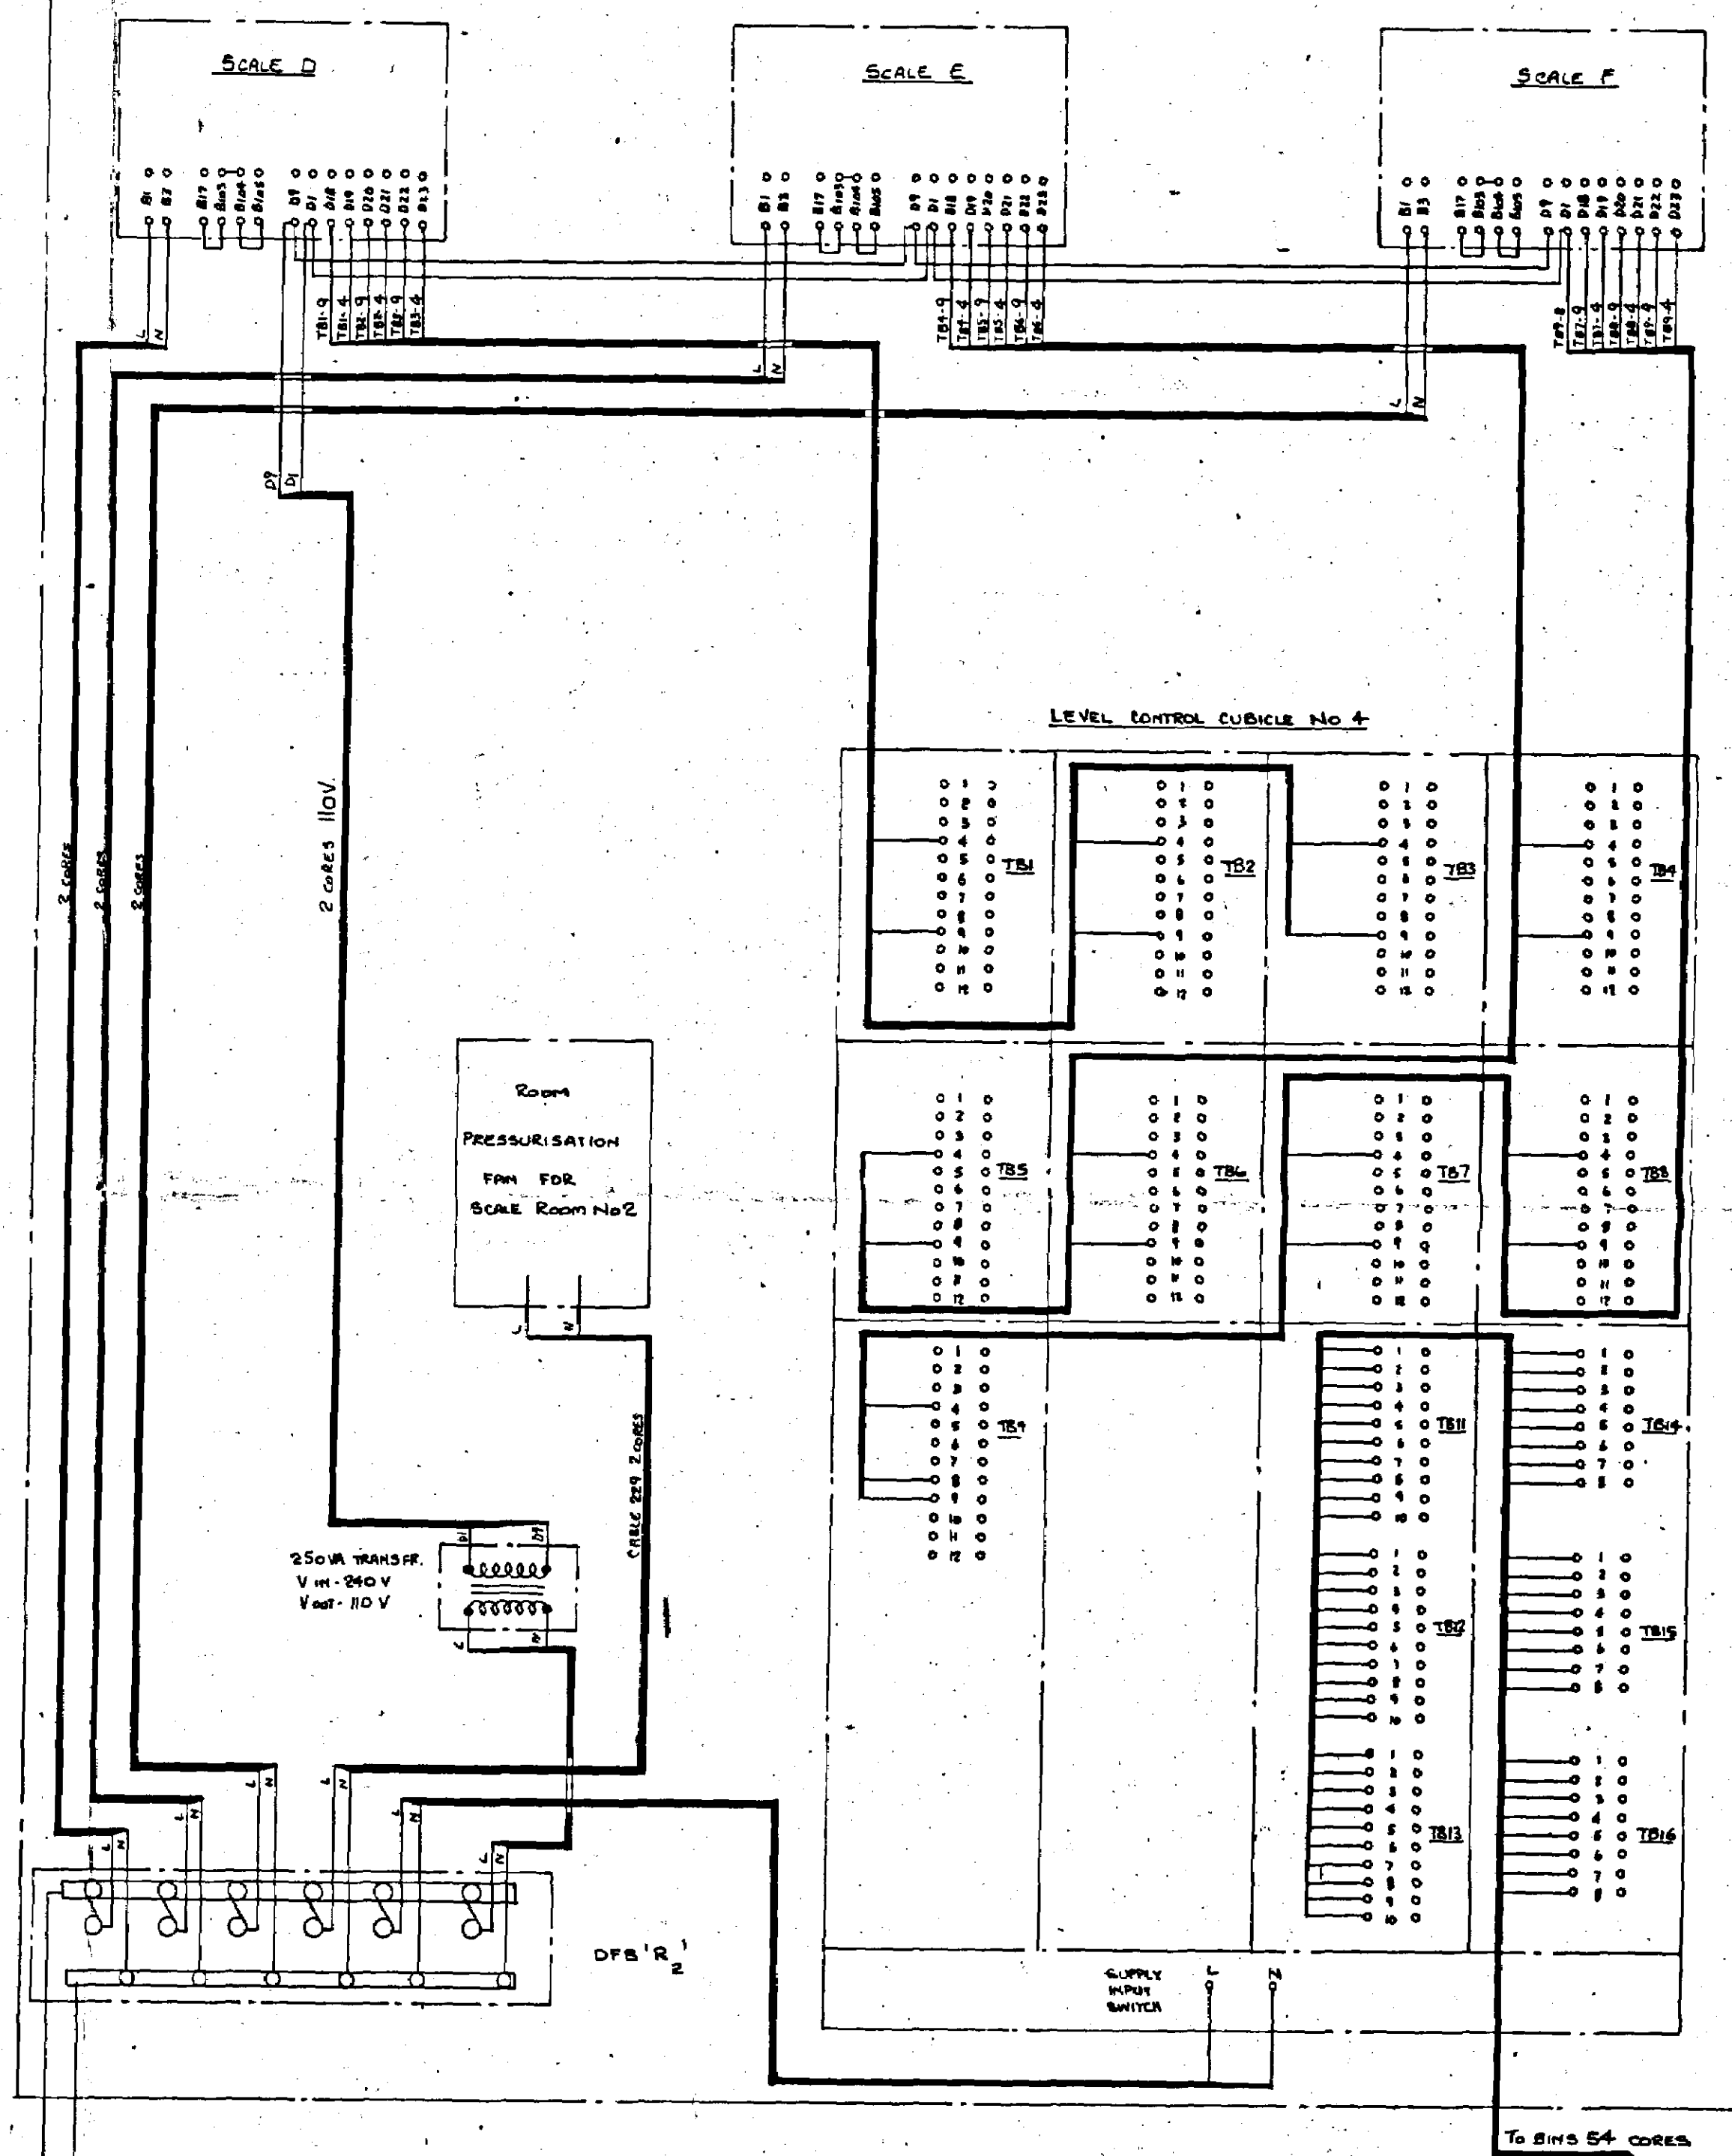

INTERCONNECTION DIAGRAM FOR LORRY LOADING SCALE ROOMS Nos 1 & 2

THE DESIGN AND MANUFACTURING INFORMATION CONTAINED IN THIS DRAWING IS THE EXCLUSIVE RIGHT OF DEWHURST & PARTNER LTD. AND MUST NOT BE COPIED OR USED FOR MANUFACTURING PURPOSES.

ISSUE	12
RTX 361 AV	
RTX 361 AV	

DEWHURST & PARTNER LTD.

MELBOURNE WORKS

HOUNSLOW

TITLE

INTERCONNECTION DIAGRAM FOR LORRY LOADING SCALE ROOMS Nos 1 & 2

REVISION

ORIGIN
/ / SGD.

REVISION

ORIGIN
/ / SGD.

REVISION: 1
WIRING MODS TO
LEVEL CONTROL
CUBICLES
ORIGIN: i.c.d.
11/7/73 SGD. JS.

DRAWN BY

DATE

CHECKED BY

APPROVED BY

DATE

KEY DIAG. No.

EXT. DIAG. No.

REL. DIAG. No.

PANEL LAYOUT No.