


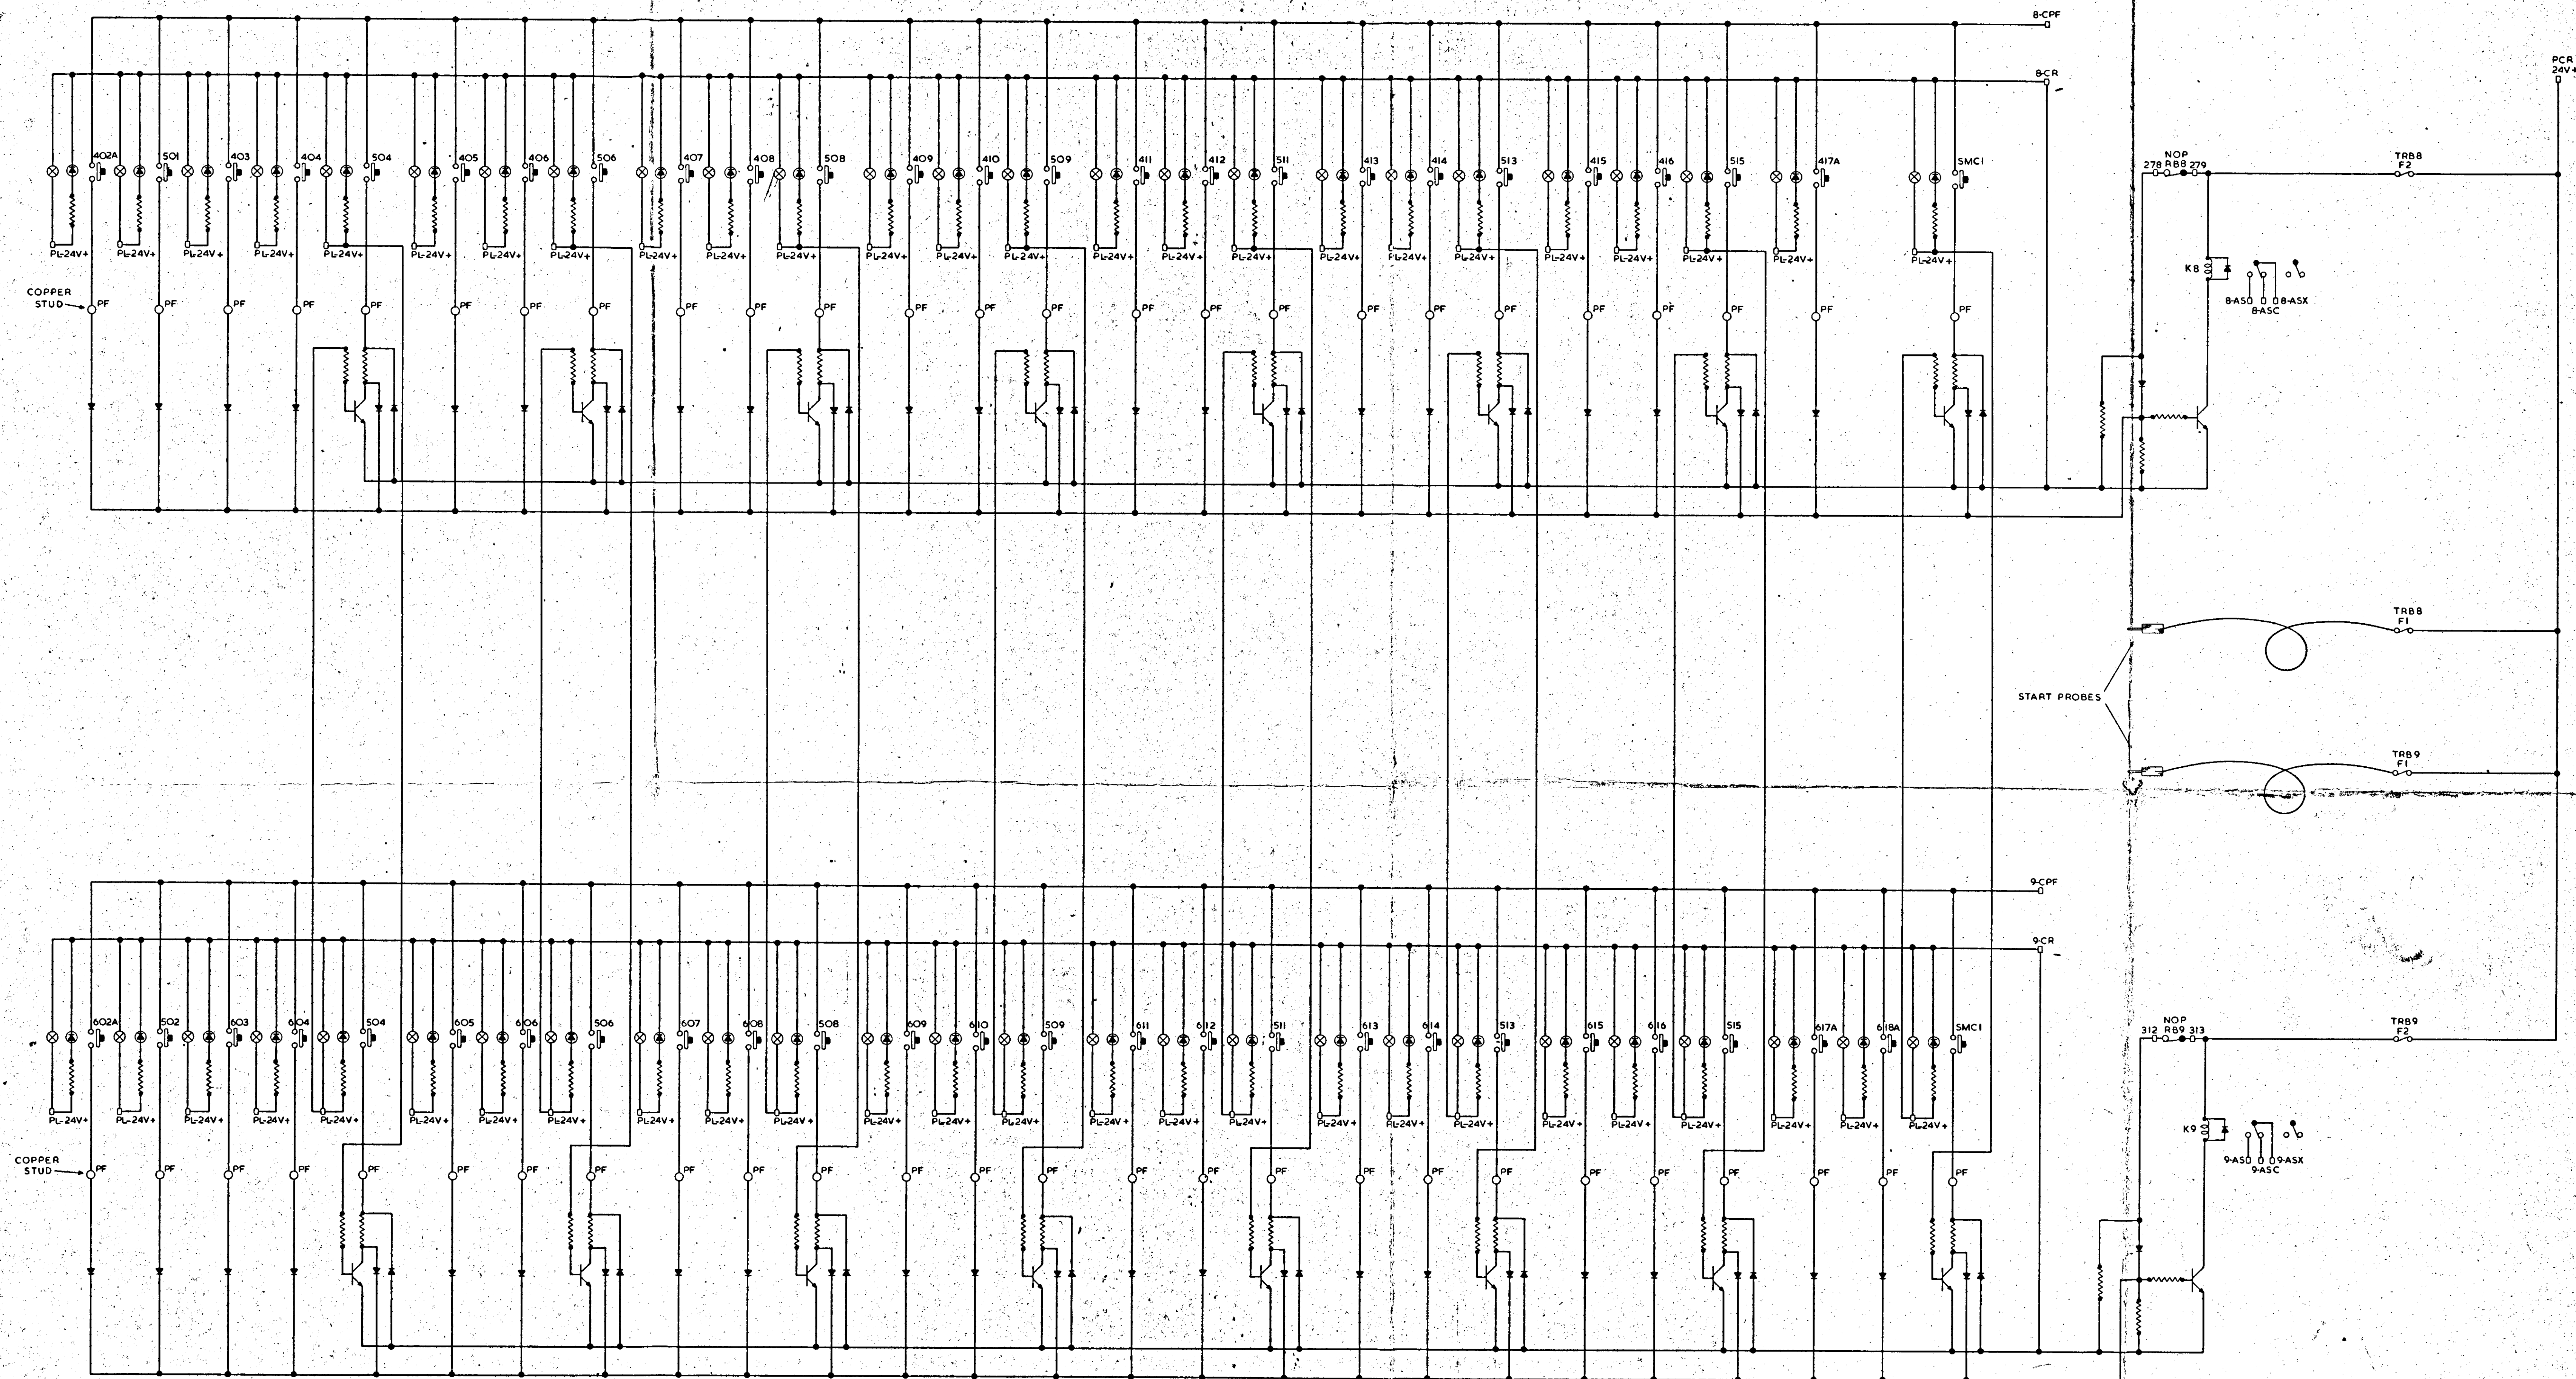

- ⊗ DENOTES SCP BIN INDICATION
- ⊙ DENOTES LED FOR ANTI-COINCIDENCE PANEL BIN INDICATION
- ⊕ DENOTES SCP BIN PUSHBUTTON

DEWHURST & PARTNER LTD.
MELBOURNE WORKS HOUNSLOW

TITLE: SCHEME FOR TRIPPER ANTI-COINCIDENCE PANEL SEAFORTH GRAIN TERMINAL

REVISION:	REVISION:	REVISION:	REVISION:	REVISION:
ORIGIN: / / SGD.	ORIGIN: / / SGD.	ORIGIN: / / SGD.	ORIGIN: / / SGD.	ORIGIN: / / SGD.

DRAWN BY: A.T.P.
DATE: 8.5.78
CHECKED BY:
APPROVED BY:
DATE:

THE DESIGN AND MANUFACTURING INFORMATION CONTAINED IN THIS DRAWING IS THE EXCLUSIVE RIGHT OF DEWHURST & PARTNER LTD. AND MUST NOT BE COPIED OR USED FOR MANUFACTURING PURPOSES.

KEY DIAG. No.
EXT. DIAG. No.
REL. DIAG. No.
PANEL LAYOUT No.

ISSUE	1	
-------	---	--	--	