


NOTE
'AT', 'APF', AND 'RSP' ONLY REQUIRED
ON MCC6B & MCC6E.

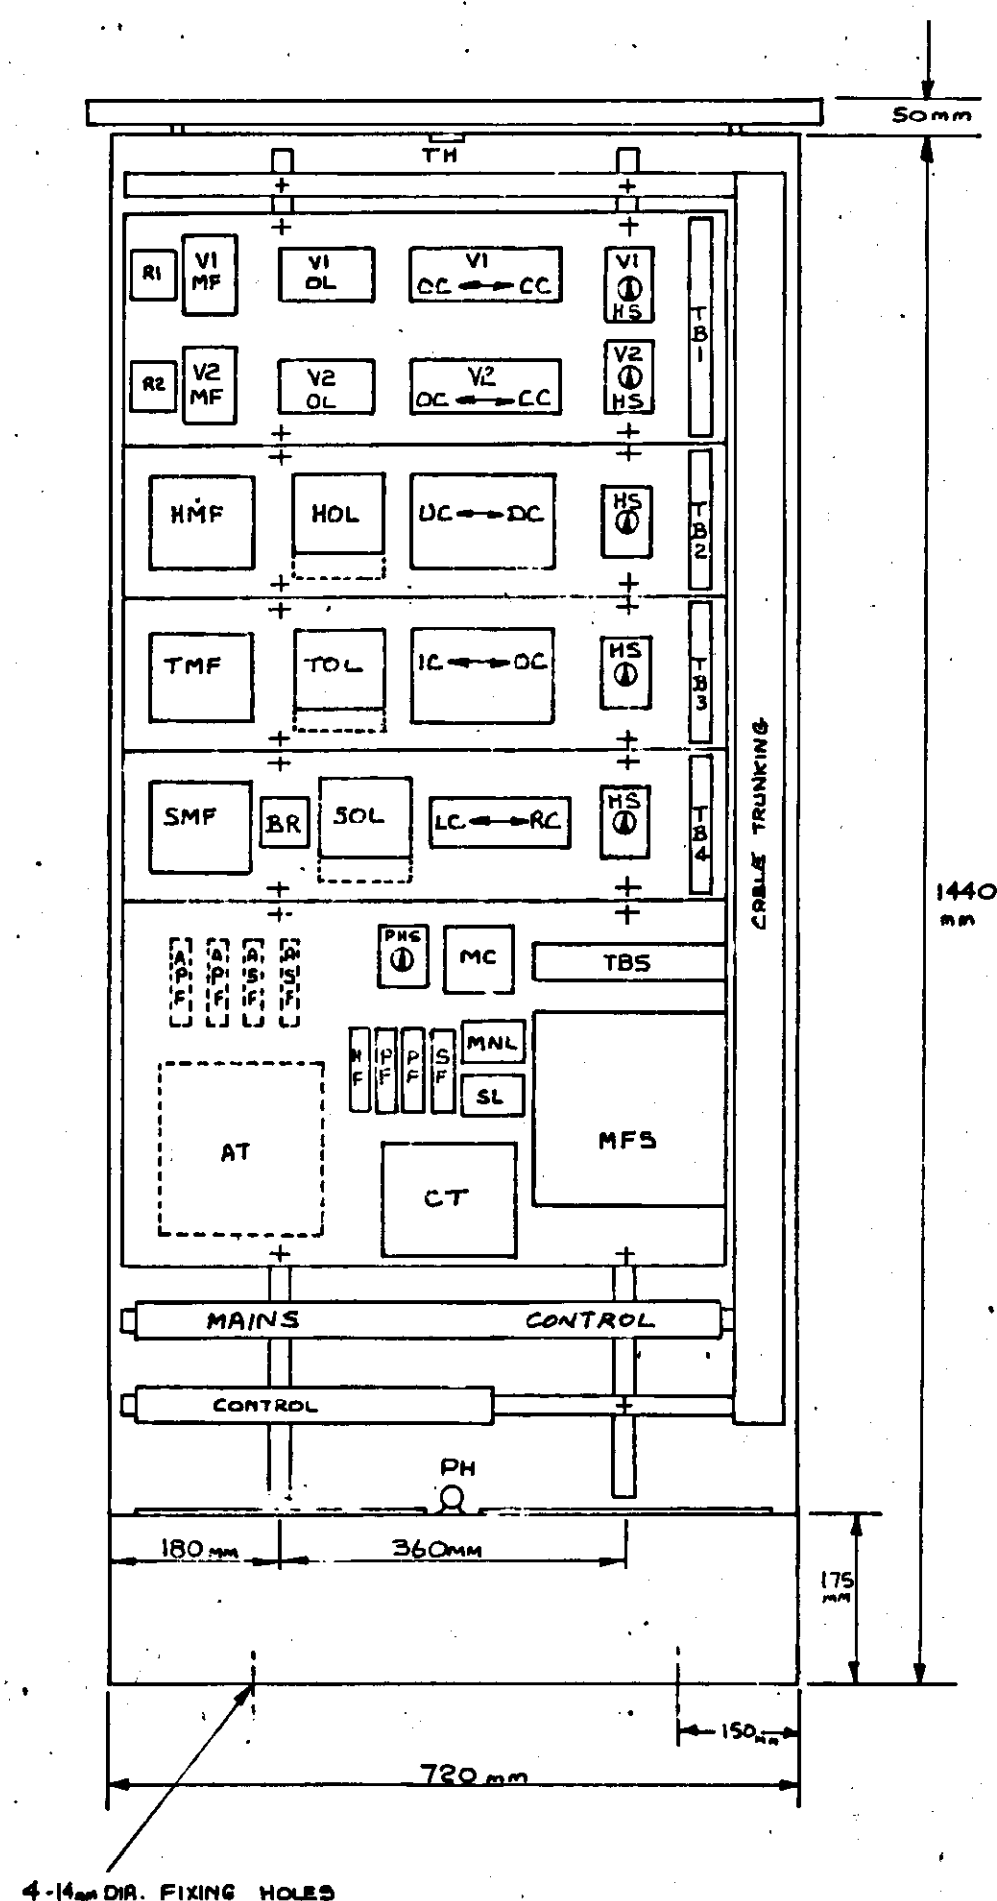

LAYOUT FOR BARGE LOADING/SHIPPING SPOUTS-PANELS MCC6A-6F — SEAFORTH GRAIN TERMINAL

DEWHURST & PARTNER LTD.

MELBOURNE WORKS

HOUNSLOW

REVISION: 2
MINOR MODS TO
INCOMING PANEL

ORIGIN: EISP
24/9/71 SGD. BSL

REVISION: 1
MNL. ADDED.

ORIGIN: EISP
7/6/71 SGD. JDL

DRAWN BY: BJC
DATE: 22-3-71
CHECKED BY:
APPROVED BY:
DATE:

REVISION: 4
AF ADDED.

ORIGIN: ICD.
9/2/72 JS.
REVISION: 3
R1 & R2 ADDED
TO SPOUT VALVE
PANEL.
ORIGIN: ICD.
16/12/71 JT.

LAYOUT FOR BARGE LOADING/SHIPPING SPOUTS - PANELS MCC6A-6F
SEAFORTH GRAIN TERMINAL

THE DESIGN AND MANUFACTURING
INFORMATION CONTAINED IN
THIS DRAWING IS THE EXCLUSIVE
RIGHT OF DEWHURST & PARTNER
LTD. AND MUST NOT BE COPIED
OR USED FOR MANUFACTURING
PURPOSES.

KEY DIAG. No. DTX36IAE
EXT. DIAG. No.
REL. DIAG. No.
PANEL LAYOUT No.

ISSUE 1 2 3 4 5

FTX36IAE

FTX36IAE

2 OFF 102 MM X 306 MM CUTOUTS
COVERED WITH SHT. STL GLANDPLATES

78mm
304mm
30mm

46

46