


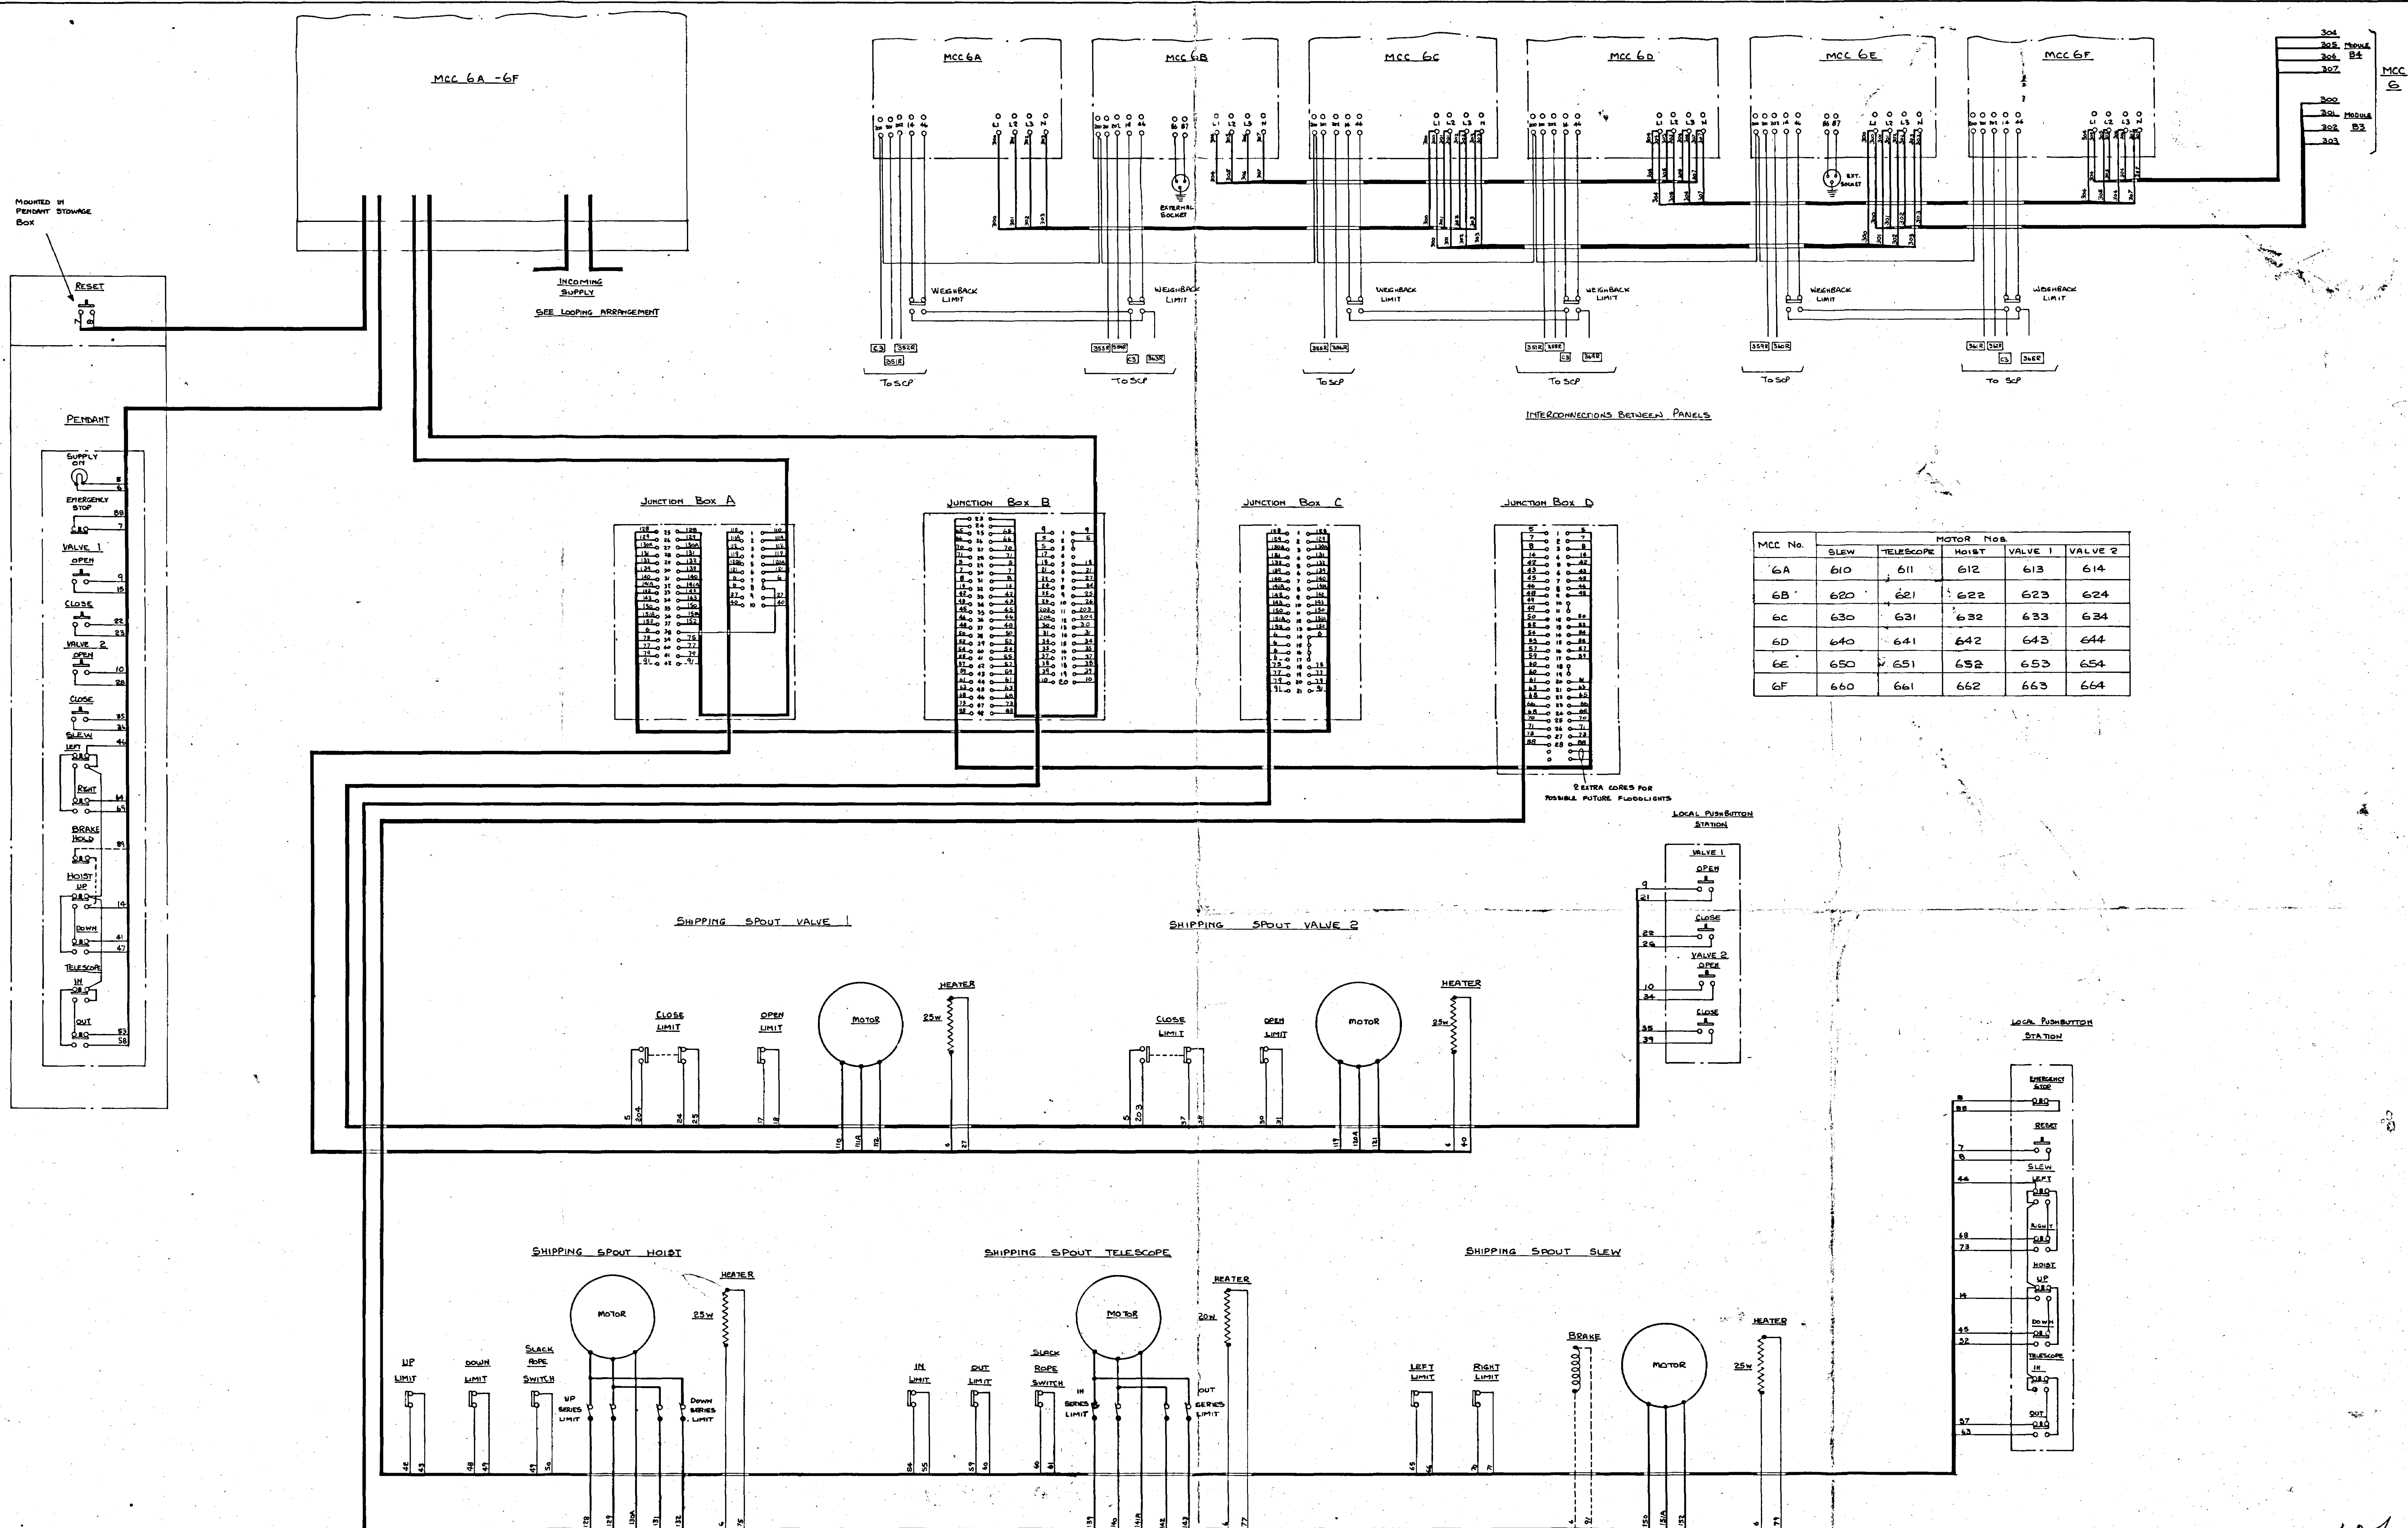

NUMBERS ADJACENT TO LOOMS  
INDICATE TERMINAL DESIGNATION  
ONLY - NOT WIRE NUMBERS

DEVHURST & PARTNER-LTD.  
MELBOURNE WORKS HOUNSLOW

TITLE: EXTERNAL WIRING DIAGRAM FOR BARGE LOADING/SHIPPING SPOUTS - MCC 6A-6F

REVISION: 6  
REVISION: 5  
REVISION: 4  
REVISION: 3  
REVISION: 2  
REVISION: 1  
DRAWN BY: J. Thomas  
DATE: 16/1/71  
CHECKED BY: J. Thomas  
APPROVED BY: J. Thomas  
DATE: 16/1/71

EXTERNAL WIRING DIAGRAM FOR BARGE LOADING/SHIPPING SPOUTS - MCC 6A-6F  
SEAFOORTH & RAIN TERMINAL  
THE DESIGN AND MANUFACTURING INFORMATION CONTAINED IN THIS DRAWING IS THE EXCLUSIVE RIGHT OF DEVHURST & PARTNER LTD. AND MUST NOT BE COPIED OR USED FOR MANUFACTURING PURPOSES.  
ISSUE 1 3 1 3 7  
STX 361 AE  
STX 361 AE

47