


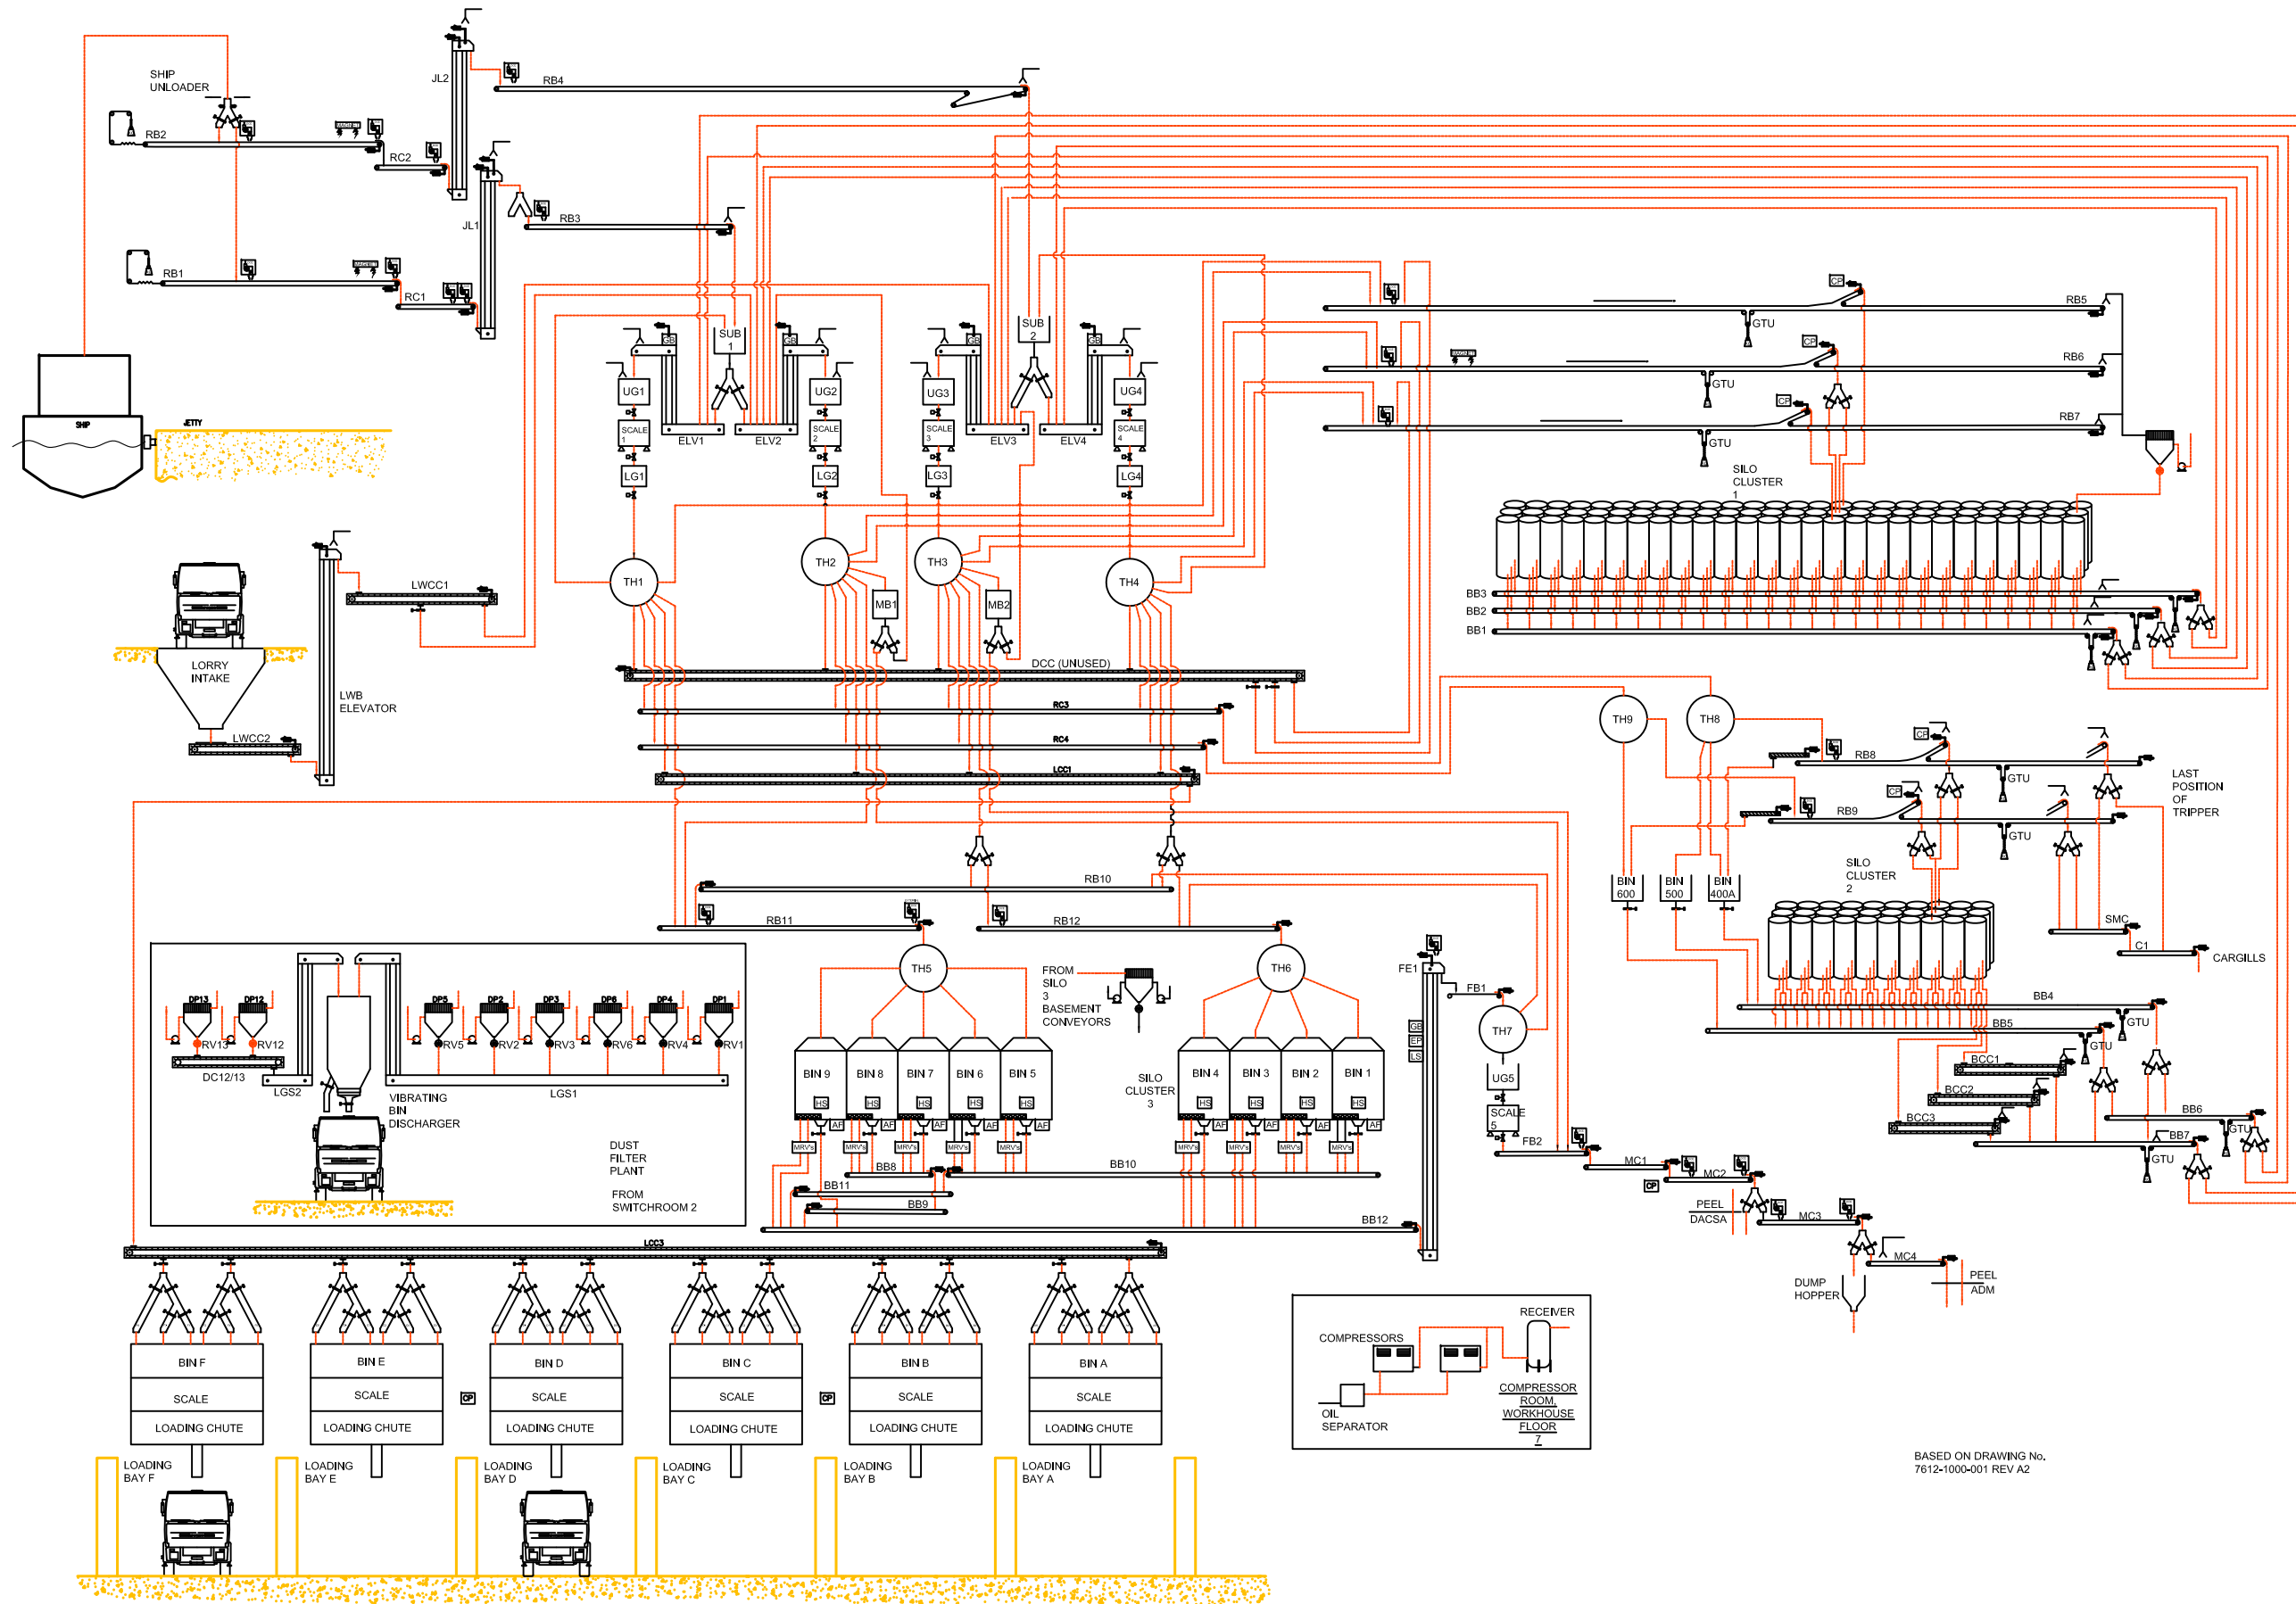

NOTES:

1. Legend

- Magnet
- Valve
- Dust Compaction Unit
- Motor
- Conveyor
- Process Connection
- Screw Conveyor
- Ventilation
- Gravity Tension Units
- Tripper
- Elevator
- CP Compressor
- HS Heat Sensor
- AF Aeration Fan
- GB Fike Gas Bottles
- MRV Manual Relief Valve
- EP Explosion Panel
- LS Limit Switch
- UG Upper Gamer
- LG Lower Gamer
- TH Turnhead
- MB Mill Bin

1
MOTORS ADDED
MOTORS REPOSITIONED
GTUs ADDED
DCES ADDED
RB8 & RB9 MODIFIED
SMC CONVEYOR ADDED
CONVEYORS REDRAWN
COLOURS ADDED FOR CLARITY
28-9-21

Revision	Description	Date
1	PEEL PORTS-MERSEY	
LIVERPOOL DOCKS GRAIN STORE FACILITY PROCESS SCHEMATIC		
PC Address	Drawn	Checked
	LF	LF
Scale : NTS @A1	Drawing No	Revision
	LFA/GS/PS/1	1